


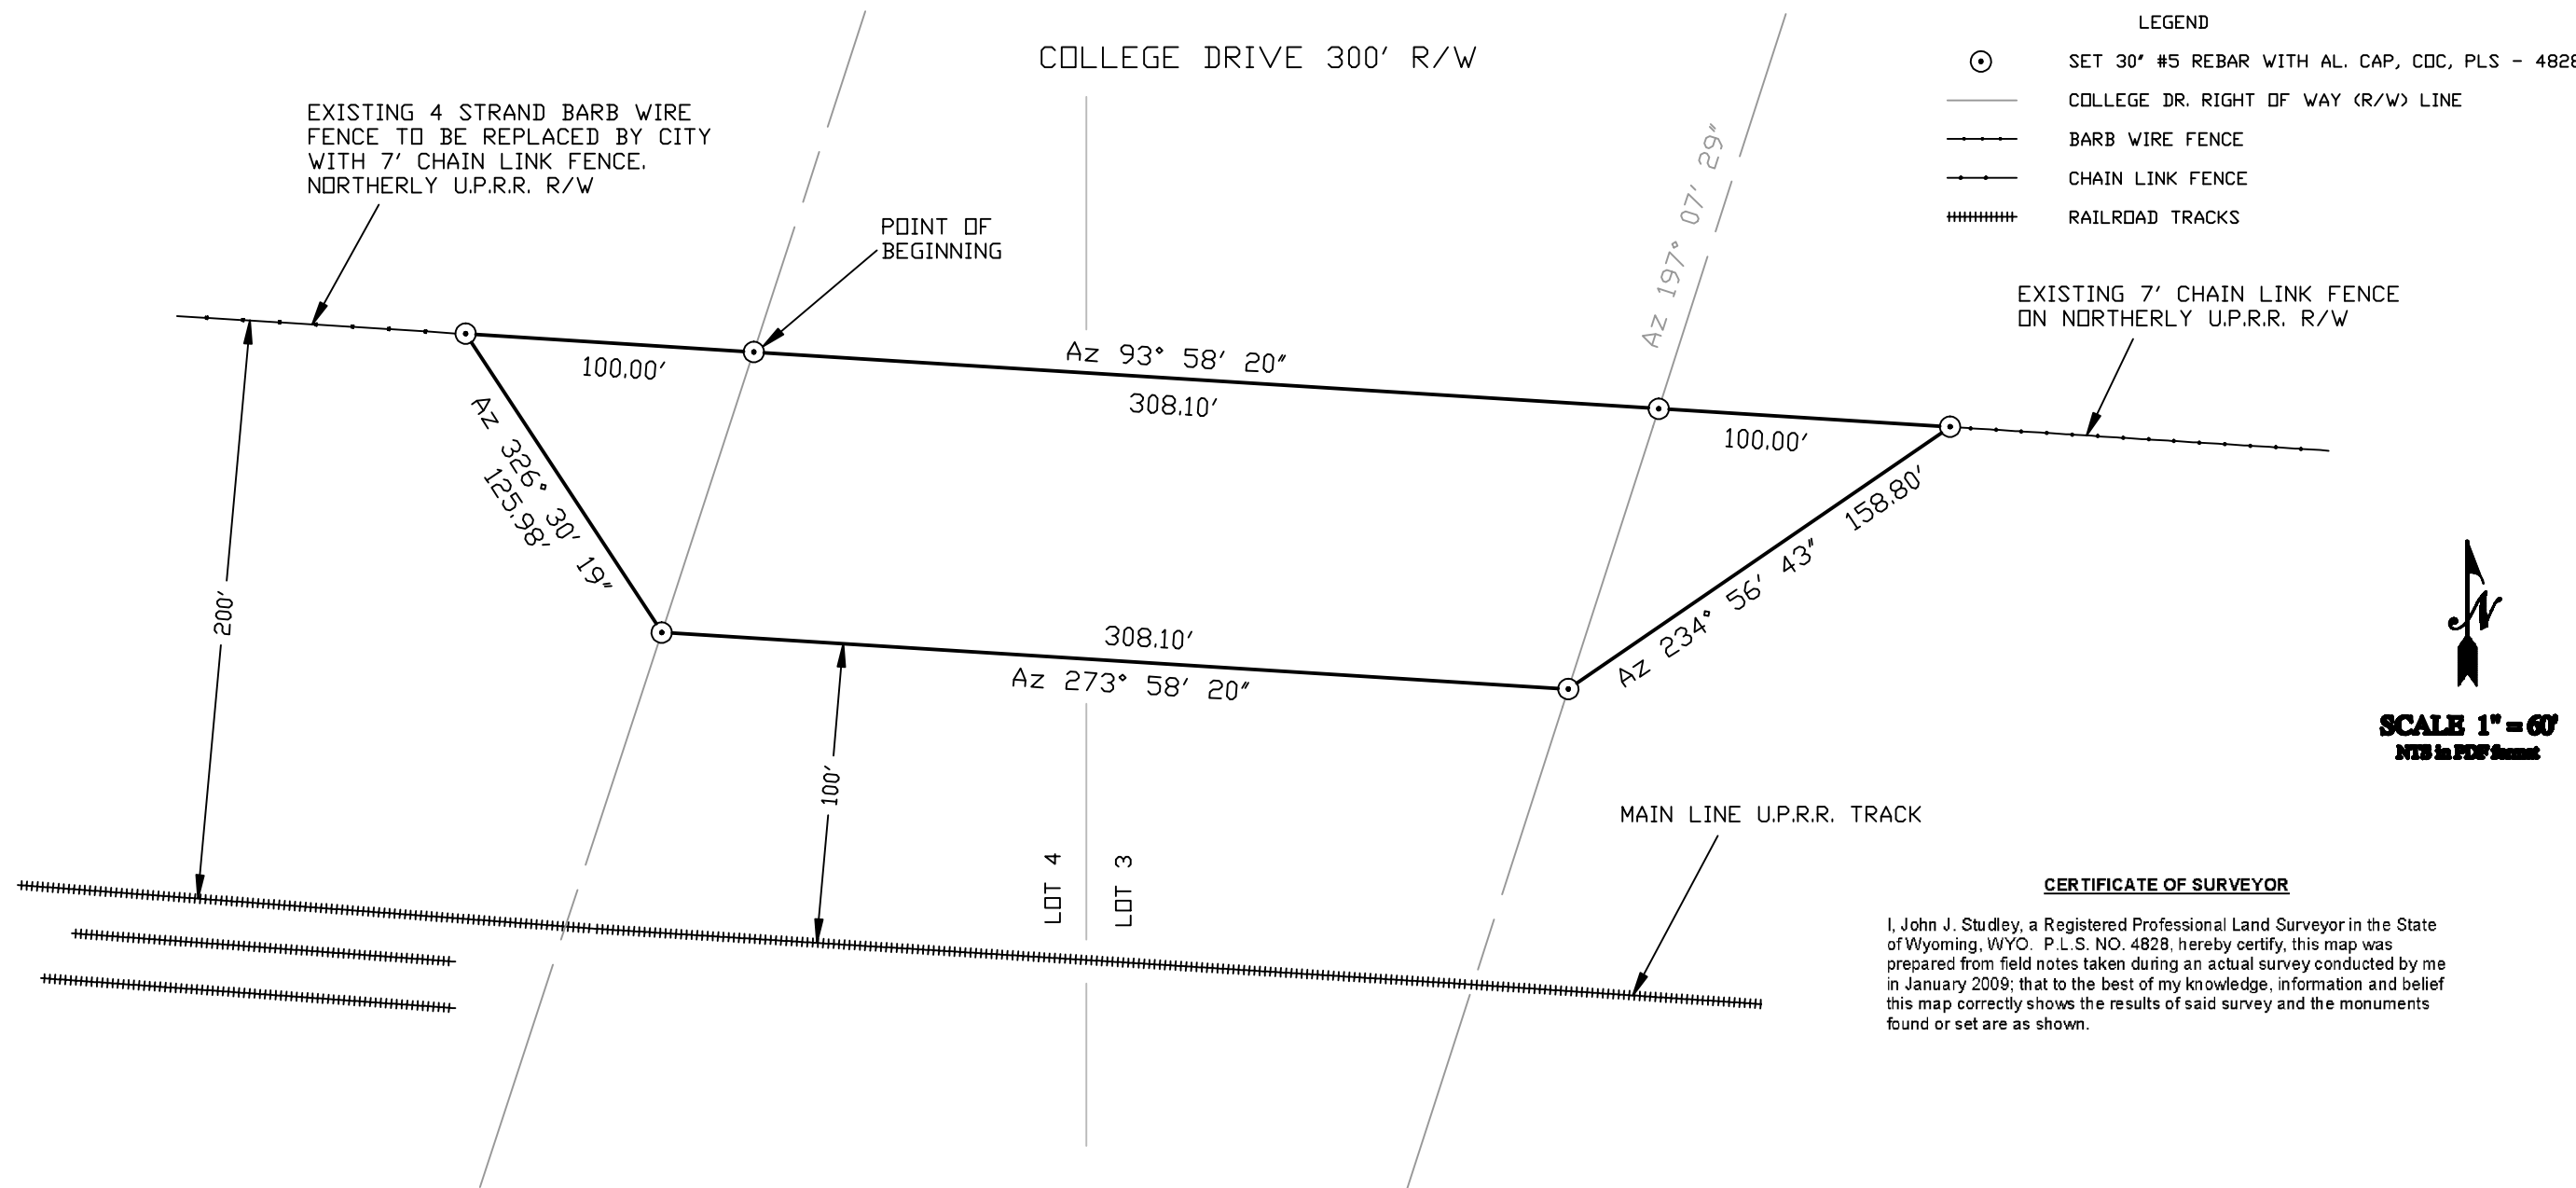

LEGAL DESCRIPTION - EASEMENT PARCEL

A portion of Lots 3 and 4, Section 3, Township 13 North, Range 66 West, 6th PM, Laramie County, Wyoming, being further described as follows:

Beginning at the point of intersection of the westerly right of way of College Drive and the northerly operating right of way of the Union Pacific Railroad, being located 200 feet northerly of the centerline of the existing tracks;
Thence on an Azimuth of 93° 58' 20" on and along the northerly operating right of way of the Union Pacific Railroad, and parallel with said centerline of the existing tracks, a distance of 308.10 feet to the point of intersection with the easterly right of way of College Drive;
Thence continuing on and along said northerly operating right of way of the Union Pacific Railroad, and parallel with said centerline of the existing tracks, a distance of 100.00 feet to a point;
Thence on an Azimuth of 234° 56' 43" a distance of 158.80 feet to a point of intersection with said easterly right of way of College Drive;
Thence on an Azimuth of 273° 58' 20" parallel to said centerline of the existing track and the northerly operating right of way of the Union Pacific Railroad, a distance of 308.10 feet to the point of intersection with said westerly right of way of College Drive;
Thence on an Azimuth of 326° 30' 19" a distance of 125.98 feet to a point of intersection with said northerly operating right of way of the Union Pacific Railroad;
Thence on an Azimuth of 93° 58' 20" on and along the northerly operating right of way of the Union Pacific Railroad, and parallel with said centerline of the existing tracks, a distance of 100.00 feet to the Point of Beginning.
Said parcel containing 40,807.38 square feet or 0.94 acre more or less.

MAP OF SURVEY
EASEMENT AGREEMENT BETWEEN
UNION PACIFIC RAILROAD AND
CITY OF CHEYENNE
SITUATE IN LOTS 3 AND 4 OF SECTION 3,
TOWNSHIP 13 NORTH, RANGE 66 WEST, 6TH PM,
LARAMIE COUNTY, WYOMING

PREPARED JANUARY 2009

DRAWN BY: MG
DATE: 2-7-09

JOB TITLE: UNION PACIFIC RAILROAD & CITY OF CHEYENNE
EASEMENT AGREEMENT
DRAWING NAME: MAP OF SURVEY

CITY OF CHEYENNE



DRAWING NO.