


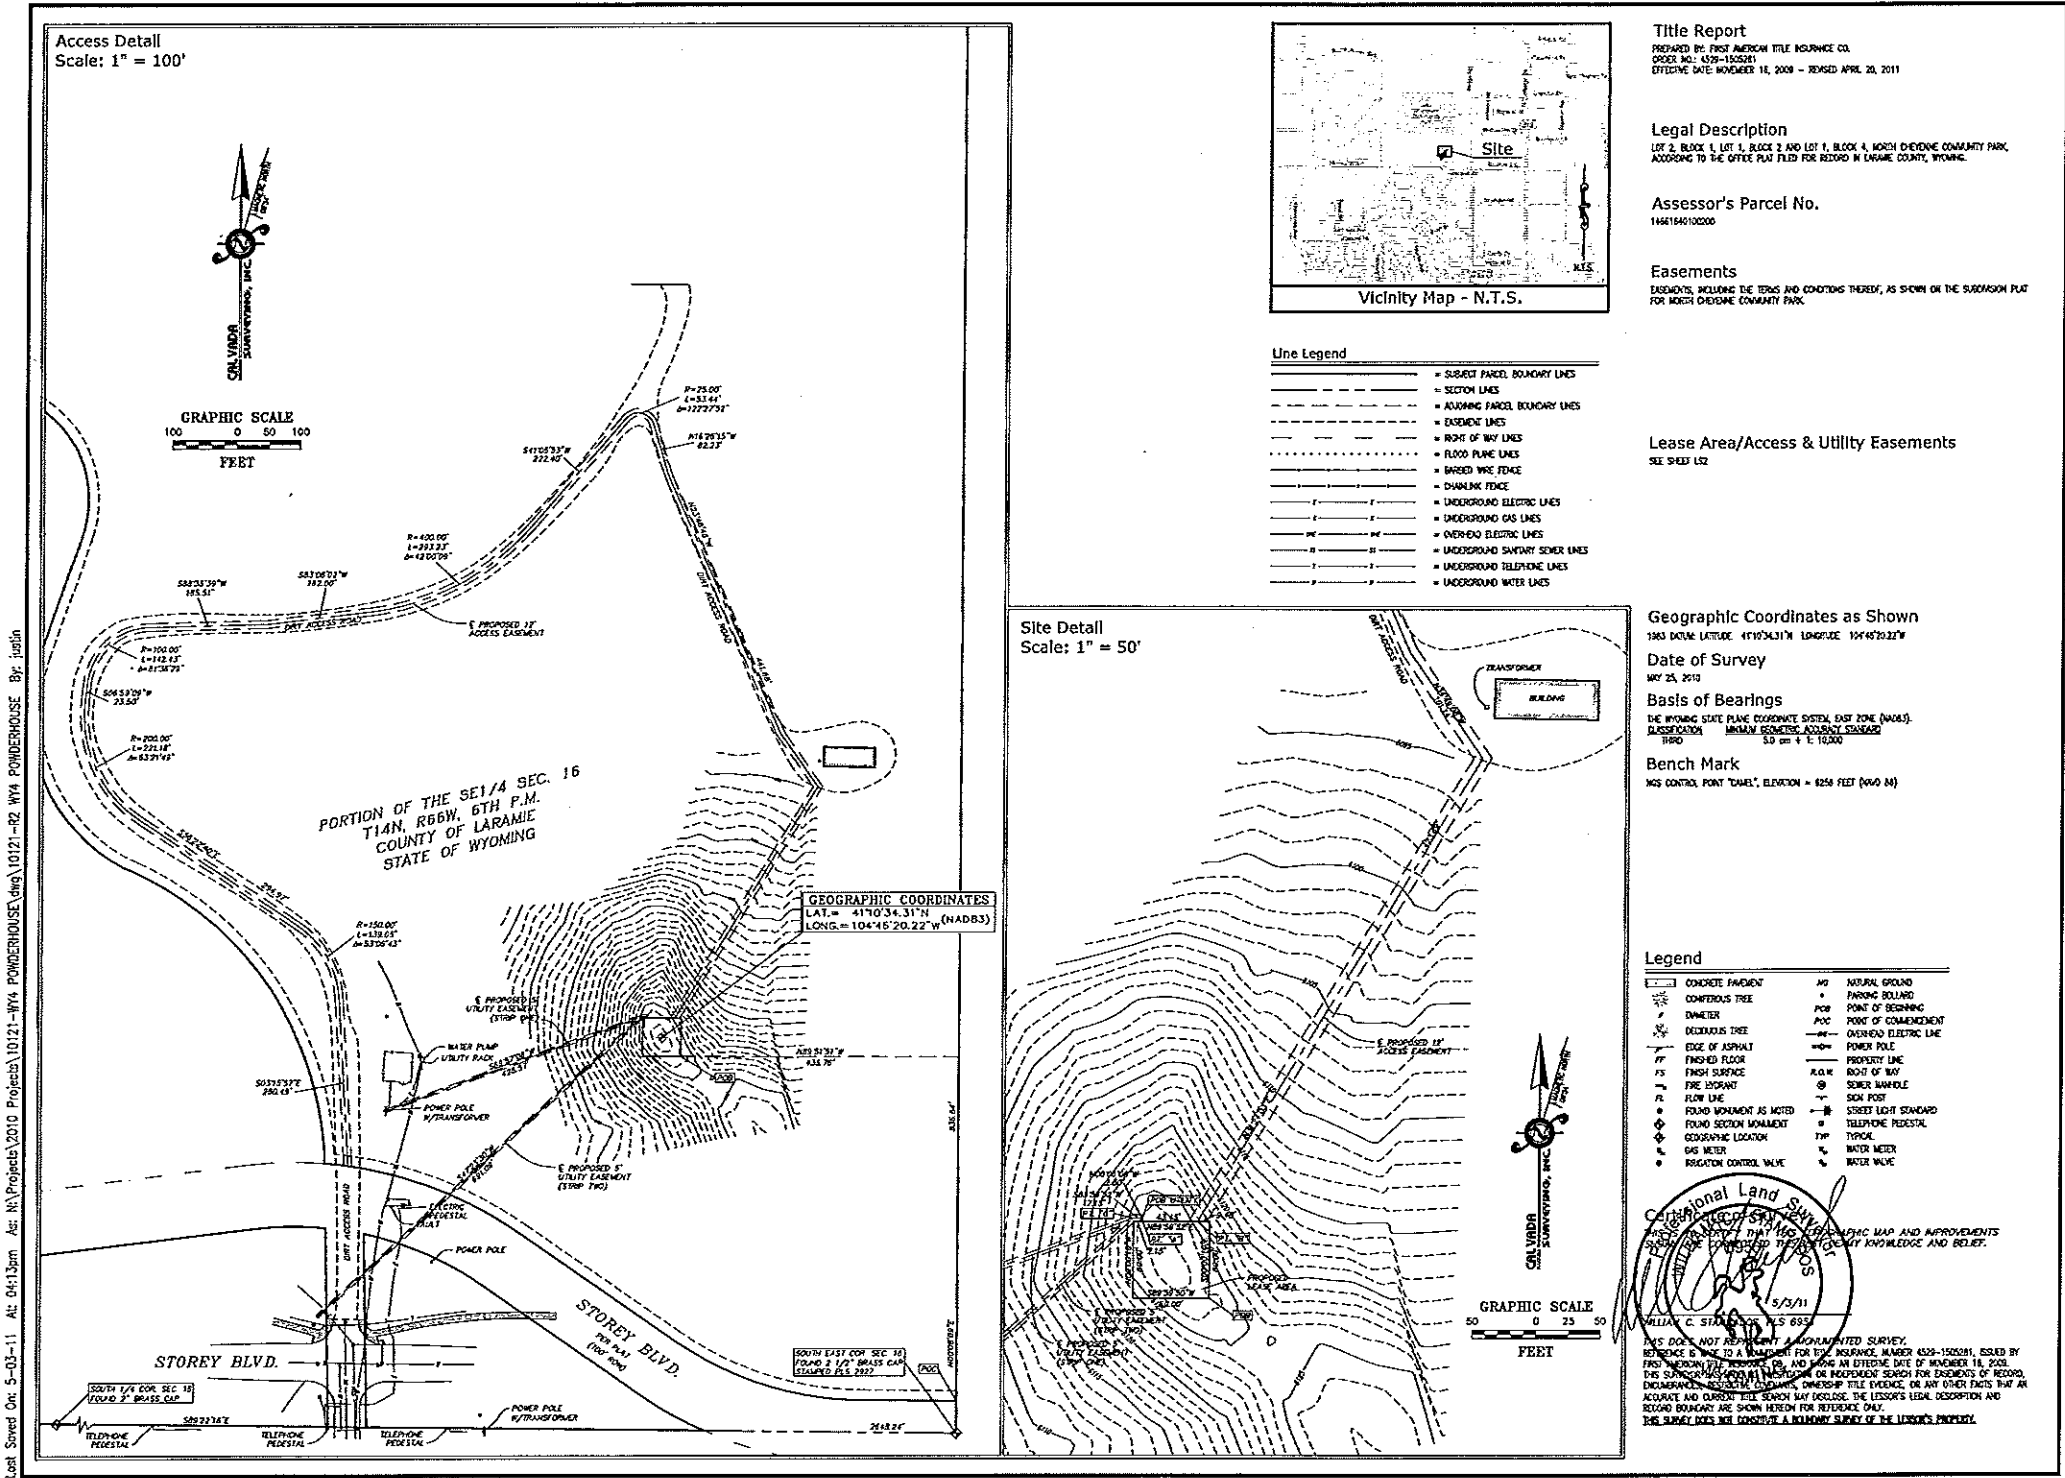

DEPT.	APPROVED	DATE
MAC		
SEC		
INT		
EX/IN		
OPS		
EV/OUT		

Assessor's Parcel No.
146164010000

Easements
EASEMENTS, INCLUDING THE TERMS AND CONDITIONS THEREOF, AS SHOWN ON THE SURVEY MAP FOR WY4 POWDERHOUSE ALT. 3.

Lease Area/Access & Utility Easements
SEE SHEET L22

Geographic Coordinates as Shown
1983 DATUM LATITUDE: 41°03'43.1"N LONGITUDE: 104°45'20.22"W

Date of Survey
MAY 25, 2010

Basis of Bearings
THE WYOMING STATE PLANE COORDINATE SYSTEM, EAST ZONE (NAD83).
CLASSIFICATION: MINIMUM GEOMETRIC ACCURACY STANDARD
THIRD
S.D. cm ± 1:10,000

Bench Mark
NCS CONTROL POINT "DAVE", ELEVATION = 8256 FEET (QVD M)

Legend

CONCRETE PAVEMENT	NO	NATURAL GROUND
CONIFEROUS TREE	+	PARKING BOLLARD
DWELLING	PCB	POINT OF BEGINNING
DECIDUOUS TREE	POC	POINT OF COMMENCEMENT
EDGE OF ASPHALT	POC	OVERHEAD ELECTRIC LINE
FINISHED FLOOR	POC	POWER POLE
FRESH SURFACE	POC	PROPERTY LINE
FIRE HYDRANT	POC	RIGHT OF WAY
FLOW LINE	POC	SEWER MANHOLE
FOUND MONUMENT AS NOTED	POC	SIGN POST
FOUND SECTION MONUMENT	POC	STREET LIGHT STANDARD
GEODETIC LOCATION	POC	TELEPHONE PEDESTAL
GAS METER	POC	TYPICAL
REGULATION CONTROL VALVE	POC	WATER METER
	POC	WATER VALVE

WY4 POWDERHOUSE
STOREY BLVD. & CANYON DR.
CHERAMIE, WY.
COUNTY OF LARAMIE
TOPOGRAPHIC SURVEY

LS1