
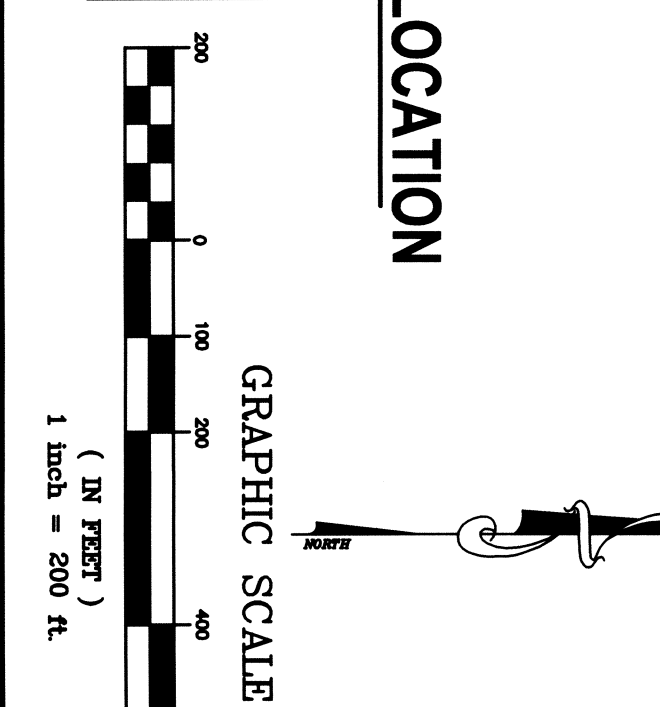
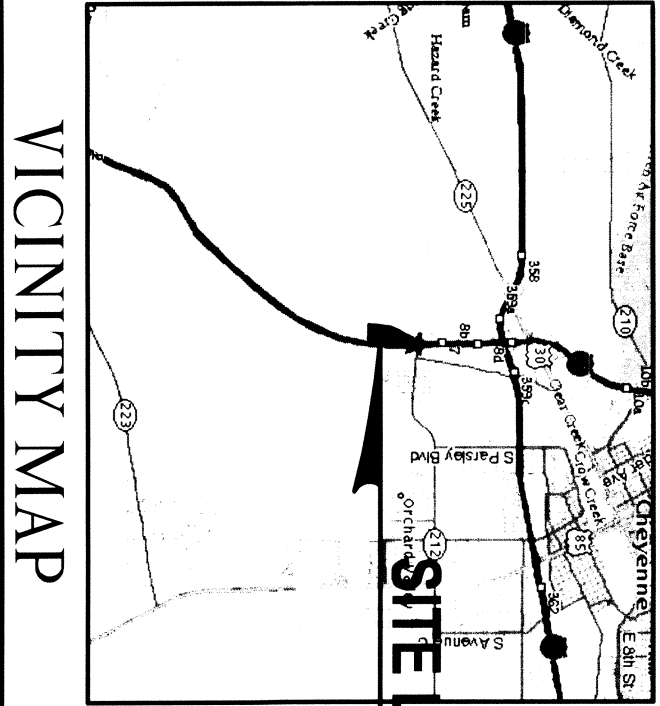


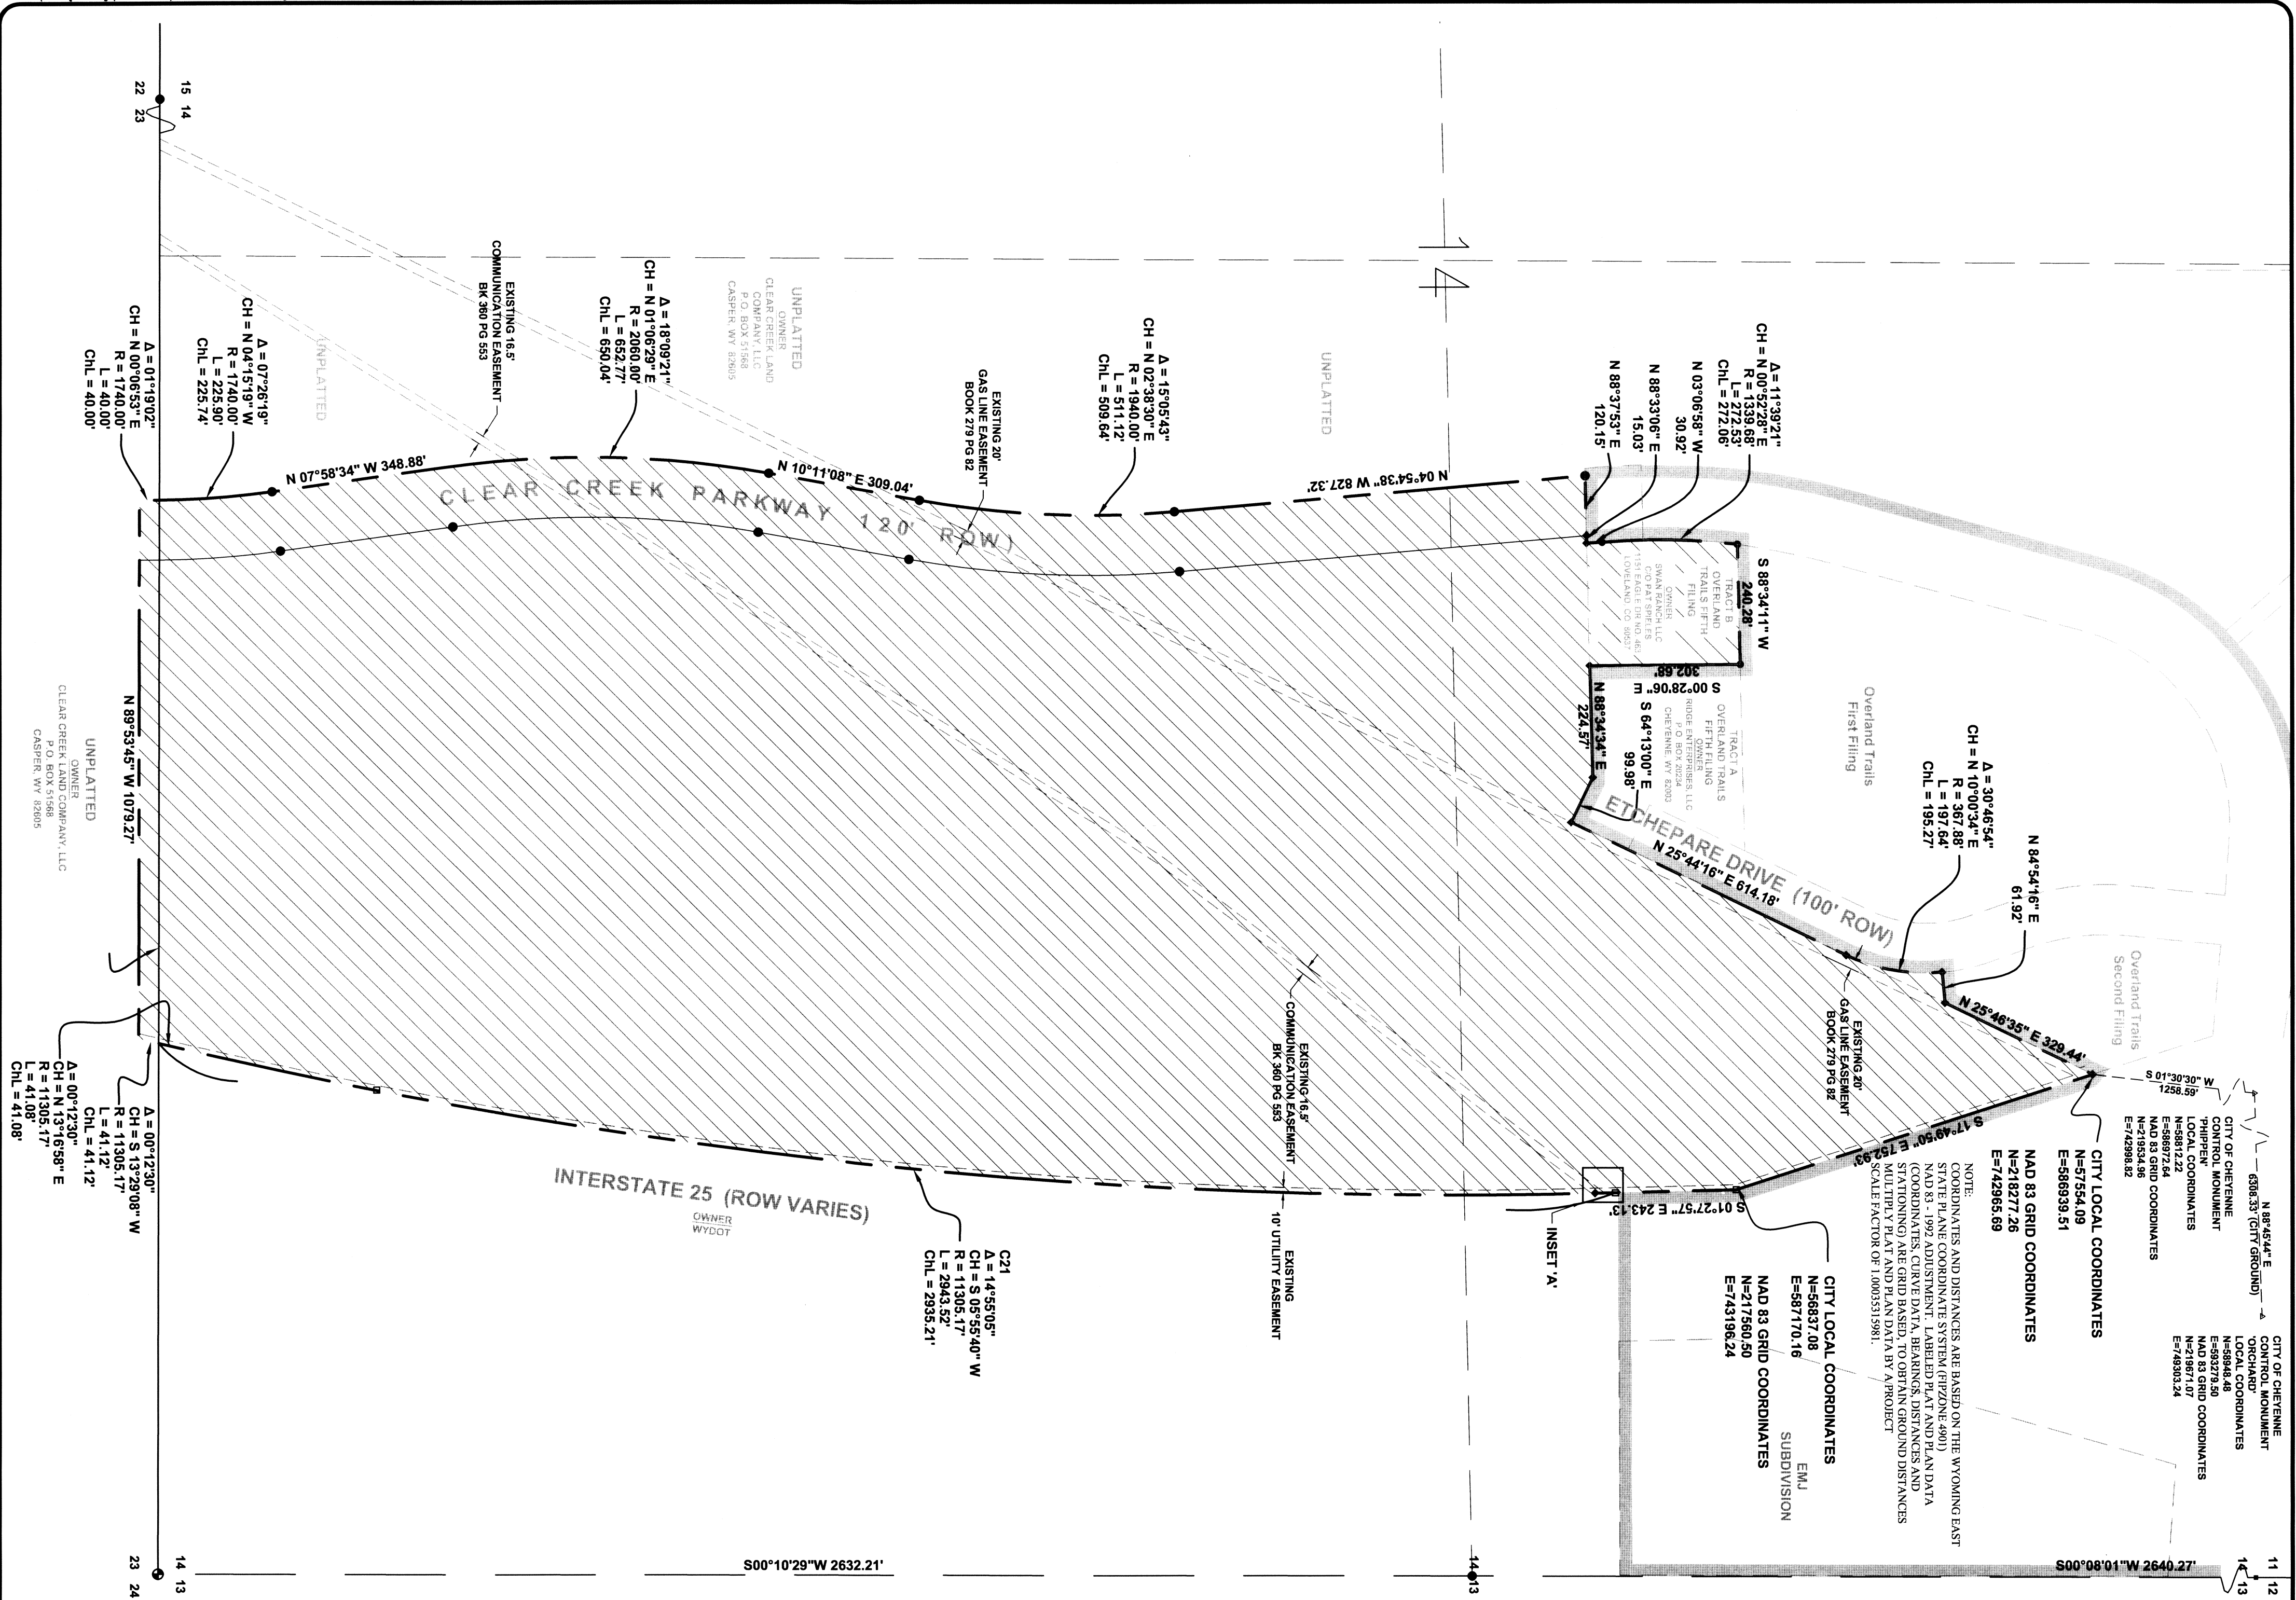

OVERLAND TRAILS BUSINESS PARK AND TRACT "B" OVERLAND TRAILS FIFTH FILING

BEING SITUATED IN PORTIONS OF SECTIONS 14, AND 23, TOWNSHIP 13 NORTH, RANGE 67 WEST OF THE SIXTH PRINCIPAL MERIDIAN, LARAMIE COUNTY, WYOMING.

PREPARED JUNE, 2011

CERTIFICATE OF SURVEYOR

I, S. DAWSON, A REGISTERED PROFESSIONAL LAND SURVEYOR IN THE STATE OF WYOMING, HEREBY STATE THAT THIS SURVEY WAS PREPARED FROM OFFICIAL PLATS AND DEEDS OF RECORD AND FROM NOTES OF A FIELD SURVEY CONDUCTED ON BEHALF OF A.V.P.C. BY ADAM DESCHER, PLUS 12045, CRAIG COMLEY, AND ME OR UNDER MY DIRECT SUPERVISION DURING THE PERIOD OF 2011, AND THAT THE MONUMENTS ARE SET OR FOUND AS SHOWN AND THAT THIS ANNEXATION MAP CORRECTLY REPRESENTS SAID SURVEY OF THE LAND DEPICTED HEREON TO THE BEST OF MY KNOWLEDGE.

LEGEND

- EXISTING CITY LIMITS
- PROPOSED CITY LIMITS

COMPUTATIONS:

- TOTAL ANNEXATION AREA - 99.3 AC
- DEDICATED STREET AREA - 153.9 AC
- CONTIGUOUS BOUNDARY - 32.3%

APPROVALS

APPROVED BY THE CITY COUNCIL OF THE CITY OF CHEYENNE THIS _____ DAY OF _____, 2011.

MAYOR _____

CITY CLERK _____

LINE TABLE

NUMBER	DIRECTION	DISTANCE
L1	N 07°57'52" W	134.31'
L2	N 04°57'52" W	214.56'
L3	N 04°55'01" W	77.12'
L4	N 85°05'24" E	51.95'
L5	N 25°46'52" E	22.88'
L6	S 64°13'00" E	9.98'
L7	S 64°13'00" E	9.98'
L8	N 23°46'52" E	22.88'
L9	N 90°00'00" E	105.01'
L10	S 05°36'28" W	32.02'
L11	S 05°36'28" W	39.52'

CURVE TABLE

NUMBER	DELTA ANGLE	RADIUS(ft)	ARC LENGTH(ft)	CHORD DIRECTION	CHORD LENGTH(ft)
C1	06°14'59"	1860.00	202.89	N 04°51'01" W	202.79
C2	03°20'33"	1940.00	113.17	N 06°18'07" W	113.16
C3	13°00'59"	1940.00	440.73	N 01°52'39" E	439.78
C4	08°10'42"	2080.00	284.04	N 06°06'03" E	283.80
C5	01°42'40"	1940.00	60.76	N 06°16'59" E	60.76
C6	08°56'28"	2080.00	269.58	S 01°22'32" E	269.41
C7	05°35'10"	342.00	33.34	S 01°32'39" W	33.33
C8	18°42'54"	350.00	114.32	S 16°25'25" W	113.82
C9	81°18'24"	342.00	485.32	N 35°14'13" W	445.51
C10	18°42'54"	270.00	88.19	N 16°25'25" E	87.80
C11	100°31'04"	262.00	459.64	S 44°38'04" E	402.93
C12	05°36'42"	11305.17	1107.26	S 01°28'10" W	1106.82
C13	01°41'24"	11305.17	333.48	S 05°07'13" W	333.46
C14	01°40'33"	11305.17	330.65	S 06°48'11" W	330.64
C15	02°15'09"	11305.17	444.46	N 08°46'02" E	444.43
C16	01°39'44"	11305.17	327.95	S 10°43'29" W	327.94
C17	05°11'08"	460.00	41.63	N 03°00'54" E	41.62
C18	01°37'23"	11305.17	320.24	S 12°22'02" W	320.23
C19	05°11'08"	540.00	48.87	S 03°00'54" W	48.86
C20	08°11'41"	11305.17	38.43	S 01°28'02" E	38.43

LEGAL DESCRIPTION

A PARCEL OF LAND SITUATE IN PORTIONS OF SECTIONS 14 & 23, TOWNSHIP 13 NORTH, RANGE 67 WEST OF THE SIXTH PRINCIPAL MERIDIAN, LARAMIE COUNTY, WYOMING, SAID PARCEL BEING AS DENOTED ON THE ANNEXATION MAP FOR OVERLAND TRAILS BUSINESS PARK AND TRACT "B" OVERLAND TRAILS FIFTH FILING, BEING MORE PARTICULARLY DESCRIBED BY METERS AND BOUNDS AS FOLLOWS:

THE POINT OF BEGINNING BEING A FOUND ALUMINUM CAP INSCRIBED W/P L.S. 2977, HEREIN AFTER REFERRED TO AS FAC 2977, MONUMENTING THE SOUTHEAST CORNER OF SAID SECTION 14;

THENCE N89°52'45"W ALONG THE SOUTH LINE OF SAID SECTION 14 FOR A DISTANCE OF 1062.53 FEET TO A SET ALUMINUM CAP INSCRIBED W/P L.S. 558, HEREIN AFTER REFERRED TO AS FAC 558, SAID POINT BEING THE TRUE POINT OF BEGINNING FOR THIS LEGAL DESCRIPTION; SAID POINT BEING THE BEGINNING POINT OF A CURVE TO THE RIGHT HAVING A RADIUS OF 11305.17 FEET AND A CENTRAL ANGLE OF 0° 12' 30" FROM WHICH THE RADIUS POINT BEARS N78°37'8"W, THENCE LEAVING THE SOUTH SECTION LINE OF SAID SECTION 14, RIGHT ALONG SAID CURVE FOR AN ARC LENGTH OF 41.12 FEET TO SAID CURVE HAVING A CHORD BEARING OF S19°29'8"W FOR 41.12 FEET TO SAID FAC 558 AND BEING IN COMMON WITH A POINT ON THE WESTERNLY ROW OF INTERSTATE 25; AND THE SOUTHERLY ROW OF WALLACK RD;

THENCE ALONG THE SOUTHERLY ROW OF FUTURE WALLACK ROAD SOUTHERLY ROW, N89°52'45"W FOR 1076.27 FEET TO SAID FAC 558 ON THE WEST BOUNDARY LINE OF CLEAR CREEK PARKWAY 120' ROW;

THENCE TO THE BEGINNING POINT OF A CURVE TO THE LEFT HAVING A RADIUS OF 1740.00 FEET AND A CENTRAL ANGLE OF 7°26'19" FROM WHICH THE RADIUS POINT BEARS N89°13'37"W;

THENCE TO THE BEGINNING POINT OF A CURVE TO THE LEFT HAVING A RADIUS OF 1740.00 FEET AND A CENTRAL ANGLE OF 1°18'27" FROM WHICH THE RADIUS POINT BEARS N89°13'37"W;

THENCE LEFT ALONG SAID CURVE FOR AN ARC LENGTH OF 40.00 FEET; SAID CURVE HAVING A CHORD BEARING OF N6°53'57" FOR 40.00 FEET TO A POINT ON THE SOUTH LINE OF SAID SECTION 14;

THENCE CONTINUING IN SAID SECTION 14 TO THE BEGINNING POINT OF A CURVE TO THE LEFT HAVING A RADIUS OF 1740.00 FEET AND A CENTRAL ANGLE OF 7°26'19" FROM WHICH THE RADIUS POINT BEARS N89°27'51"W, THENCE LEFT ALONG SAID CURVE FOR AN ARC LENGTH OF 225.90 FEET; SAID CURVE HAVING A CHORD BEARING OF N4°15'19"W FOR 225.74 FEET TO A FOUND ALUMINUM CAP INSCRIBED W/P L.S. 10838, HEREIN AFTER REFERRED TO AS FAC 10838;

THENCE N78°37'8"W FOR 348.88 FEET TO A FAC 10838;

THENCE TO THE BEGINNING POINT OF A CURVE TO THE RIGHT HAVING A RADIUS OF 2880.00 FEET AND A CENTRAL ANGLE OF 18°9'21" FROM WHICH THE RADIUS POINT BEARS N82°1'46"E;

THENCE N82°1'46"E FOR 390.00 FEET TO A FAC 10838; SAID CURVE HAVING A CHORD BEARING OF N7°15'54" FOR 390.00 FEET TO A FAC 10838;

THENCE TO THE BEGINNING POINT OF A CURVE TO THE LEFT HAVING A RADIUS OF 1940.00 FEET AND A CENTRAL ANGLE OF 15°5'43" FROM WHICH THE RADIUS POINT BEARS N78°48'39"W;

THENCE LEFT ALONG SAID CURVE FOR AN ARC LENGTH OF 511.12 FEET; SAID CURVE HAVING A CHORD BEARING OF N2°38'30"E FOR 509.64 FEET TO A FAC 10838;

THENCE N4°54'38"W FOR 827.32 FEET TO A FAC 10838, SAID POINT IS IN COMMON WITH THE SOUTHERLY BOUNDARY OF OVERLAND TRAILS 5TH FILING AND FALLS 15' EASTERLY OF THE WESTERNLY BOUNDARY OF CLEAR CREEK PARKWAY, A 150' ROW;

THENCE LEAVING THE SAID WEST BOUNDARY LINE OF CLEAR CREEK PARKWAY;

THENCE ALONG THE BOUNDARY OF OVERLAND TRAILS 5TH FILING FOR THE FOLLOWING 2 COURSES:

THENCE N88°37'50"E FOR 120.15 FEET TO A FAC 10838;

THENCE N88°37'50"E FOR 120.15 FEET TO A FAC 10838, ON THE EASTERLY BOUNDARY OF CLEAR CREEK PARKWAY 150' ROW;

THENCE CONTINUING ALONG SAID EASTERLY ROW, INTERSECTING FOR 30.00 FEET TO A FAC 3891;

THENCE CONTINUING ALONG SAID EASTERLY ROW, INTERSECTING FOR 30.00 FEET TO A FAC 3891;

THENCE CONTINUING ALONG SAID EASTERLY ROW TO THE BEGINNING POINT OF A CURVE TO THE RIGHT HAVING A RADIUS OF 1339.88 FEET AND A CENTRAL ANGLE OF 11°39'22" FROM WHICH THE RADIUS POINT BEARS N05°52'28"E, THENCE RIGHT ALONG SAID CURVE FOR AN ARC LENGTH OF 272.83 FEET; SAID CURVE HAVING A CHORD BEARING OF N07°52'28"E FOR 272.08 FEET TO A FAC 250;

THENCE N88°34'11"E FOR 240.28 FEET TO A FAC 3891, SAID POINT BEING IN COMMON WITH THE NORTH LINE OF TRACT "B" OVERLAND TRAILS 5TH FILING AND THE SOUTH LINE OF LOT 1, BLOCK 1, OVERLAND TRAILS 1ST FILING;

THENCE ALONG THE SOUTH LINE OF TRACT "A" OVERLAND TRAILS 5TH FILING, S00°28'06"E FOR 302.88 FEET TO A FAC 2500;

THENCE ALONG THE SOUTHERLY BOUNDARY OF OVERLAND TRAILS 5TH FILING, S84°13'04"E FOR 89.88 FEET AND IN COMMON WITH THE WESTERNLY ROW OF ETCHEPARE DRIVE;

THENCE NORTHERLY ALONG THE EASTERLY ROW OF ETCHEPARE DRIVE, N65°14°16'5" FOR 614.18 FEET TO A FAC 2500; OF 30°48'54" FROM WHICH THE RADIUS POINT BEARS N62°35'59"W;

THENCE N62°35'59"W FOR 30.00 FEET TO A FAC 2500; OF 30°48'54" FROM WHICH THE RADIUS POINT BEARS N62°35'59"W;

THENCE LEFT ALONG SAID CURVE FOR AN ARC LENGTH OF 157.64 FEET; SAID CURVE HAVING A CHORD BEARING OF N10°0'34"E FOR 157.27 FEET TO A POINT ON THE BOUNDARY OF OVERLAND TRAILS 2ND FILING, MONUMENTED BY A FAC 2590;

THENCE LEAVING THE SAID BOUNDARY OF OVERLAND TRAILS 1ST FILING AND THE EASTERLY ROW OF ETCHEPARE DRIVE, ALONG THE BOUNDARY OF OVERLAND TRAILS 2ND FILING FOR THE FOLLOWING 2 COURSES:

THENCE N84°54'18"E FOR 61.92 FEET TO A FAC 2590;

THENCE N25°46'52"E FOR 329.44 FEET TO A POINT ON THE WESTERNLY ROW OF INTERSTATE 25;

THENCE N25°46'52"E FOR 329.44 FEET TO A FAC 2590 TO A POINT ON THE WESTERNLY ROW OF WAY LINE OF INTERSTATE 25;

THENCE ALONG THE SAID WESTERNLY ROW OF WAY LINE OF INTERSTATE 25 FOR THE FOLLOWING 3 COURSES:

THENCE S17°49'50"E FOR 762.83 FEET TO A FOUND WYOMING DEPARTMENT OF TRANSPORTATION RIGHT-OF-WAY MONUMENT HEREIN AFTER REFERRED TO AS A FD RW, MONS;

THENCE S17°47'57"E FOR 245.13 FEET TO A FD RW, MONS;

THENCE TO THE BEGINNING POINT OF A CURVE TO THE RIGHT HAVING A RADIUS OF 11363.11 FEET AND A CENTRAL ANGLE OF 14°55'8" FROM WHICH THE RADIUS POINT BEARS S88°28'8"W;

THENCE RIGHT ALONG SAID CURVE FOR AN ARC LENGTH OF 2963.24 FEET; SAID CURVE HAVING A CHORD BEARING OF S5°58'40"W FOR 2593.24 FEET TO THE TRUE POINT OF BEGINNING.

ANNEXATION MAP FOR

OVERLAND TRAILS BUSINESS PARK AND TRACT "B" OVERLAND TRAILS FIFTH FILING

PROJECT:	ANNEXATION MAP FOR OVERLAND TRAILS BUSINESS PARK, AND TRACT B OVERLAND TRAILS FIFTH FILING
DRAWING TITLE:	ANNEXATION MAP
PREPARED FOR:	GRANITE PEAK DEVELOPMENT 1300 VENTURE WAY CASPER WY. 82609
DATE:	JUNE 2011
DRAWN BY:	
DESIGNED BY:	
CHECKED BY:	
JOB NO.:	2-3215
DRAWING NO.:	1 OF 1

PHONE 607.7.637.6017
1103 OLD TOWN LANE, SUITE 101
CARTERSVILLE, WY 82609
AV@AVP.C.COM

engineering
surveying
P.C.