

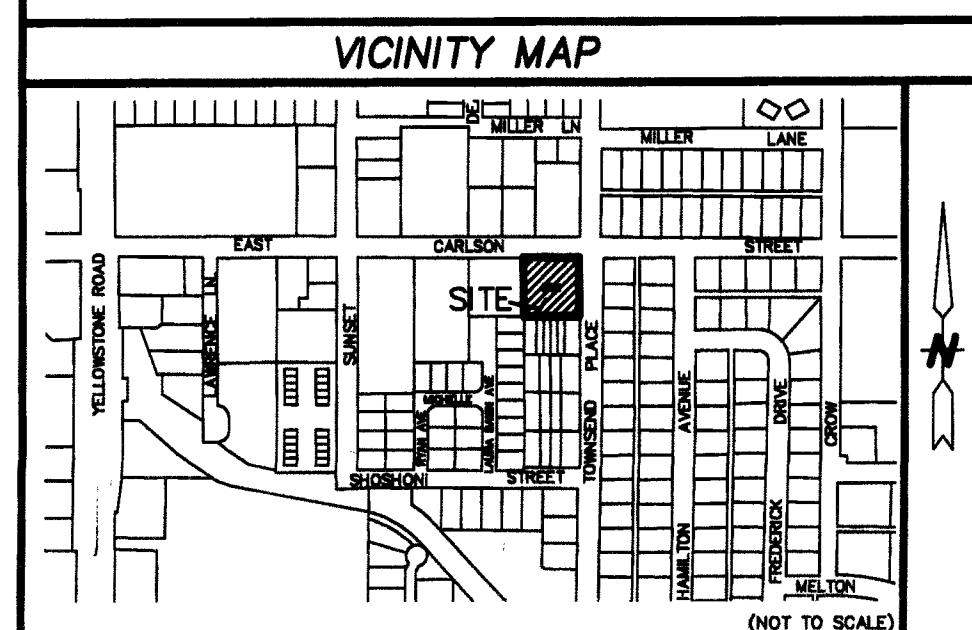


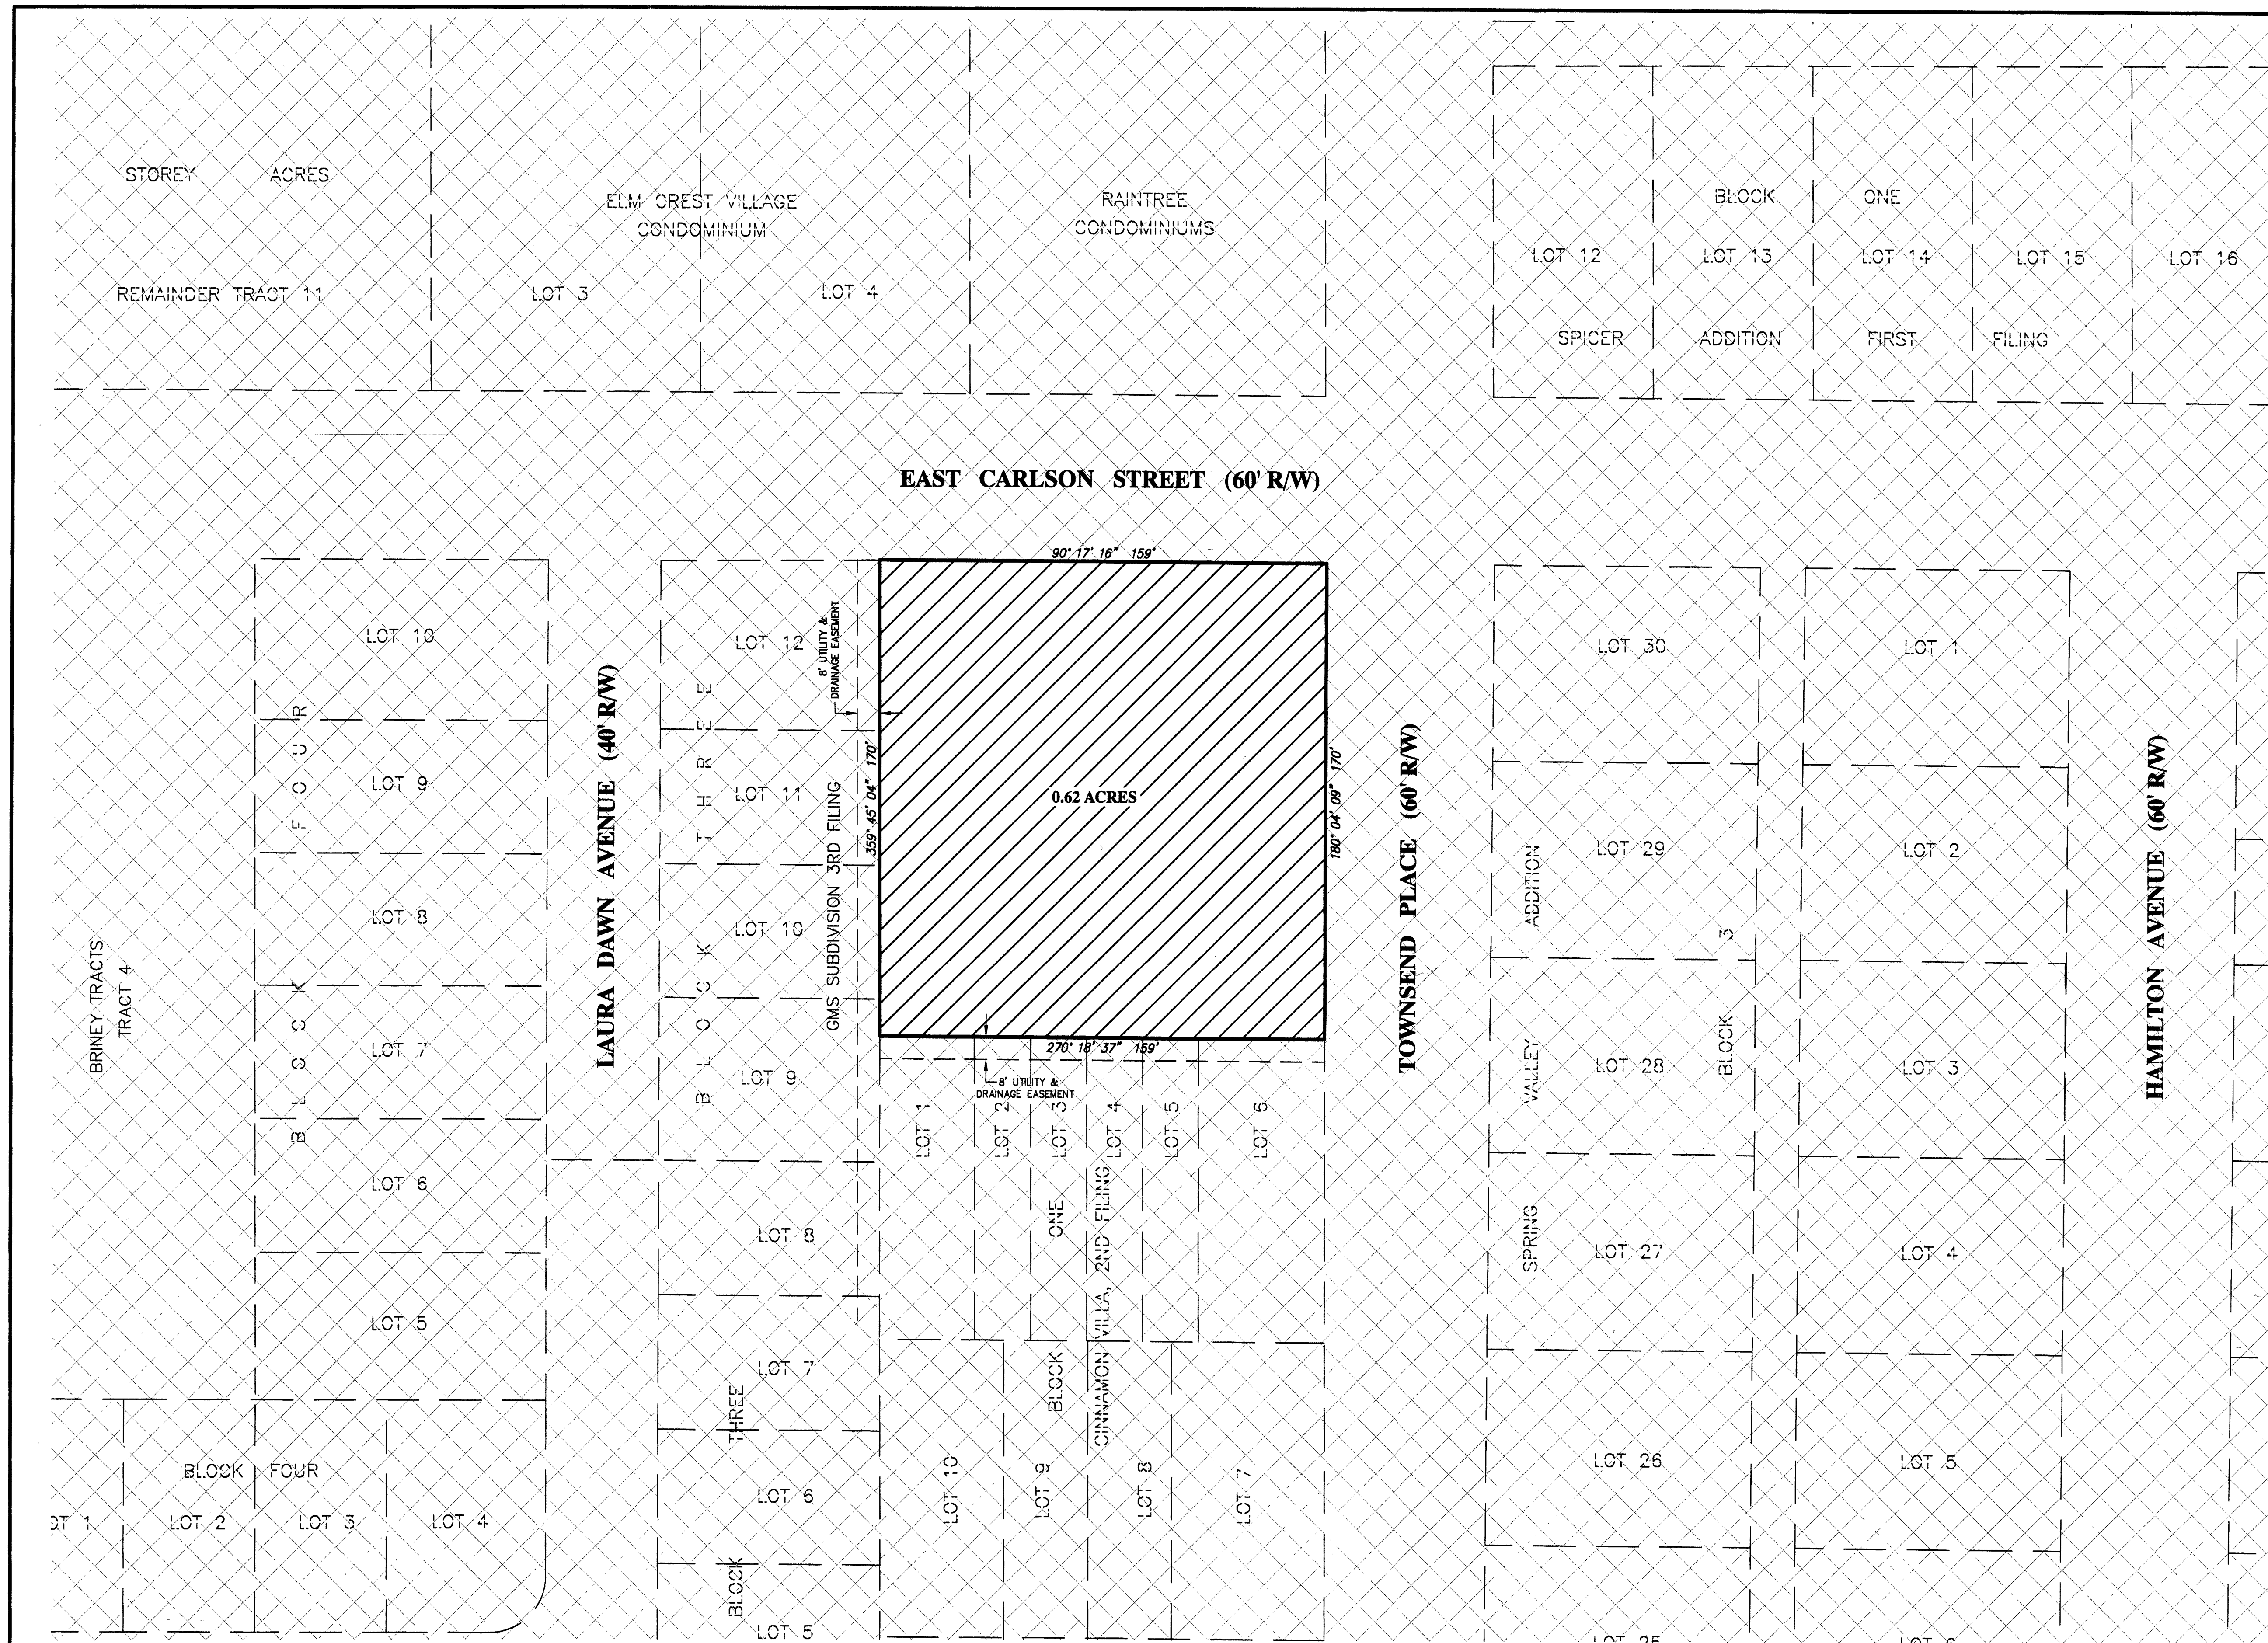


**LAND DESCRIPTION**  
THE NORTH 170 FEET OF TRACT 6, BRINEY TRACTS,  
BEING A SUBDIVISION OF THE NORTH HALF OF LOT 2,  
SECTION 19, TOWNSHIP 14 NORTH, RANGE 88 WEST  
OF THE 6TH P.M., LARAMIE COUNTY, WYOMING

**ANNEXATION AREA**  
TOTAL 27,068 SQ.FT. (0.62 ACRES)

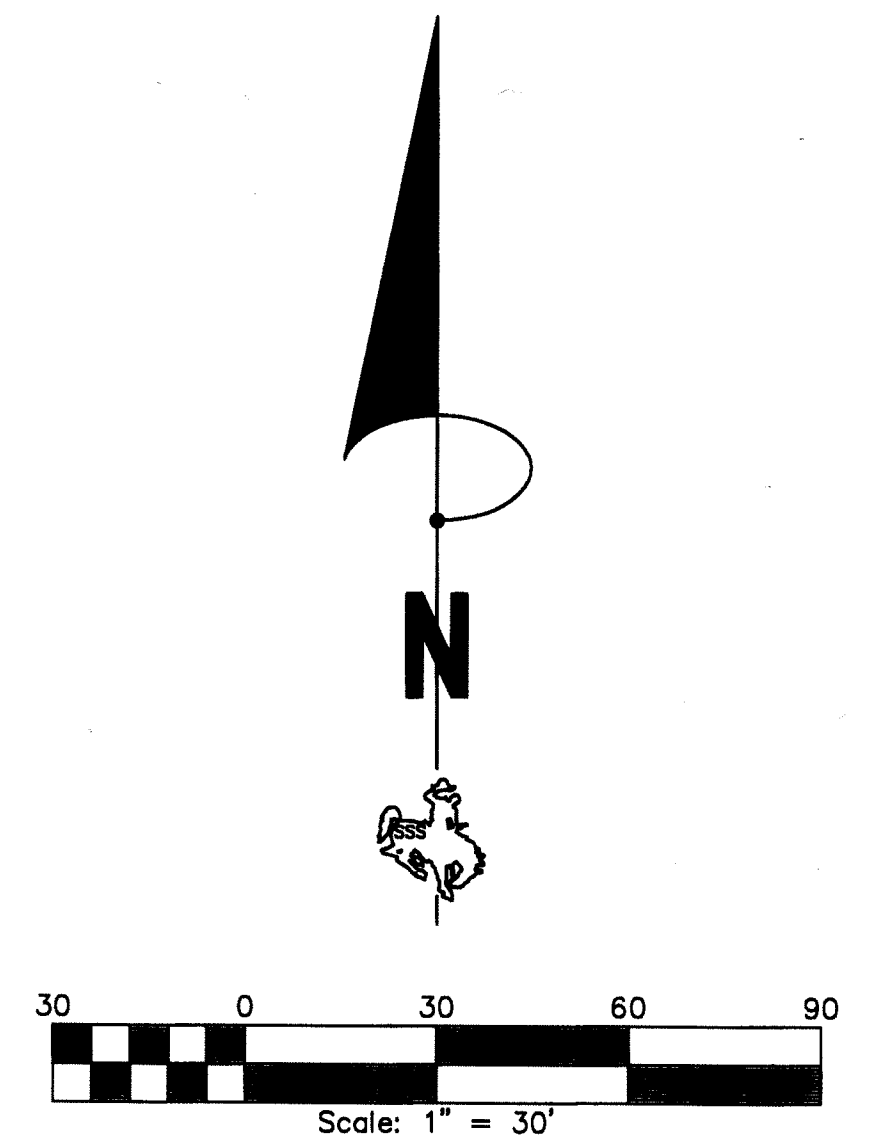

**LEGEND**  
EXISTING CITY LIMITS  
AREA TO BE ANNEXED

**APPROVALS**  
Approved by the City Council of the City of Cheyenne, Wyoming,  
this \_\_\_\_ day of \_\_\_\_\_, 2011.  
Mayor \_\_\_\_\_ ATTEST: \_\_\_\_\_  
City Clerk

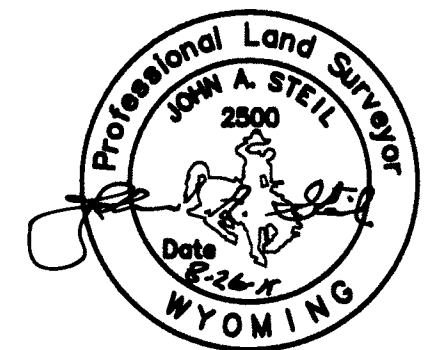

**CERTIFICATE OF SURVEYOR**

STATE OF WYOMING )  
COUNTY OF LARAMIE )  
I, John A. Stell, Registered Professional Land Surveyor in the State of Wyoming, do hereby state that this Annexation Map has been prepared by me or under my direct supervision, from official plats and documents of record and is correct to the best of my knowledge.

**ANNEXATION MAP  
FOR  
STANCEYK**

5618 TOWNSEND PLACE,  
THE NORTH 170 FEET OF  
TRACT 6, BRINEY TRACTS,  
LARAMIE COUNTY, WYOMING.

PREPARED AUGUST, 2011



**STEEL SURVEYING SERVICES, LLC**  
PROFESSIONAL LAND SURVEYORS

1102 WEST 19th STREET P.O. BOX 2073  
PH(307)634-7273 CHEYENNE, WY. 82003