

STATE OF WYOMING)
) SS
COUNTY OF LARAMIE)

PETITION FOR ANNEXATION

TO: **THE HONORABLE MAYOR, RICHARD L. KAYSEN**
 AND MEMBERS OF THE CITY COUNCIL, CITY OF CHEYENNE, WYOMING

KNOW ALL:

THAT United Western Corporation, a Wyoming Corporation, owner in fee simple of the following described tracts of land:

Parcel 1

Township 14 North, Range 66 West of the 6th P.M., Laramie County, Wyoming.

Section 20: A portion of the E1/2 E1/2 , being more particularly described as follows:

Beginning at the E1/4 corner of said Section 20; thence 179° 55' 22", a distance of 177.16 feet; thence 269° 55' 41", a distance of 304.32 feet to a point on the east boundary of the Converse Avenue right-of-way; thence northwesterly along said Converse Avenue boundary line along a curve concave to the northeast, having a radius of 746.32 feet and a central angle of 20° 47' 29" (chord azimuth of 349° 38' 18", chord distance of 269.34 feet); thence 359° 41' 16", a distance of 572.83 feet; thence 89° 58' 31", a distance of 352.39 feet; thence 179° 43' 03", a distance of 660.39 feet to the point of beginning.

Containing 291,063sf (6.68 acres) more or less.

Parcel 2

Township 14 North, Range 66 West of the 6th P.M., Laramie County, Wyoming.

Section 21: A portion of the SW1/4 SW1/4 NW1/4, being more particularly described as follows:

Beginning at the W1/4 corner of said Section 21; thence 359° 43' 03" for a distance of 188.01 feet, to a point on the west boundary of a 40 foot Board of Public Utilities Easement (recorded in Book 766 Page 555 at the Laramie County Office of Records); thence 90° 13' 49", a distance of 40.00 feet to a point on the east boundary of said easement; thence, 359° 43' 03" along said east boundary line, a distance of 120.00 feet; thence 90° 13' 49", a distance of 262.90 feet to a point on the west boundary of Ogden Road right-of-way; thence 171° 54' 47" along said Ogden Road boundary line, a distance of 136.50 feet; thence southeasterly along said Ogden Road boundary line along a curve concave to the southwest, having a radius of 1195.50 feet and a central angle of 08° 19' 02" (chord azimuth of 176° 04' 18", chord distance of 173.39 feet); thence 270° 13' 49" a distance of 332.46 feet to the point of beginning.

Containing 94,220sf (2.16 acres) more or less.

Laramie, County, Wyoming; which is currently zoned A-1 under the rules and regulations of the Bord of Laramie County Commissioners; and the undersigned petitioner(s) hereby respectfully request that said described land be annexed to the City of Cheyenne, and be made a part thereof; and an accurate annexation map prepared by Jeff Jones, Preofessional Land Surveyor registered in the State of Wyoming, No. 5910, accompanys this petition.

DATED THIS 5th DAY OF December, 2012


RESPECTFULLY SUBMITTED,


United Western Corporation, a Wyoming Corporation



Frank M. Cole, President

ATTEST:

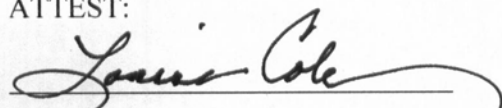

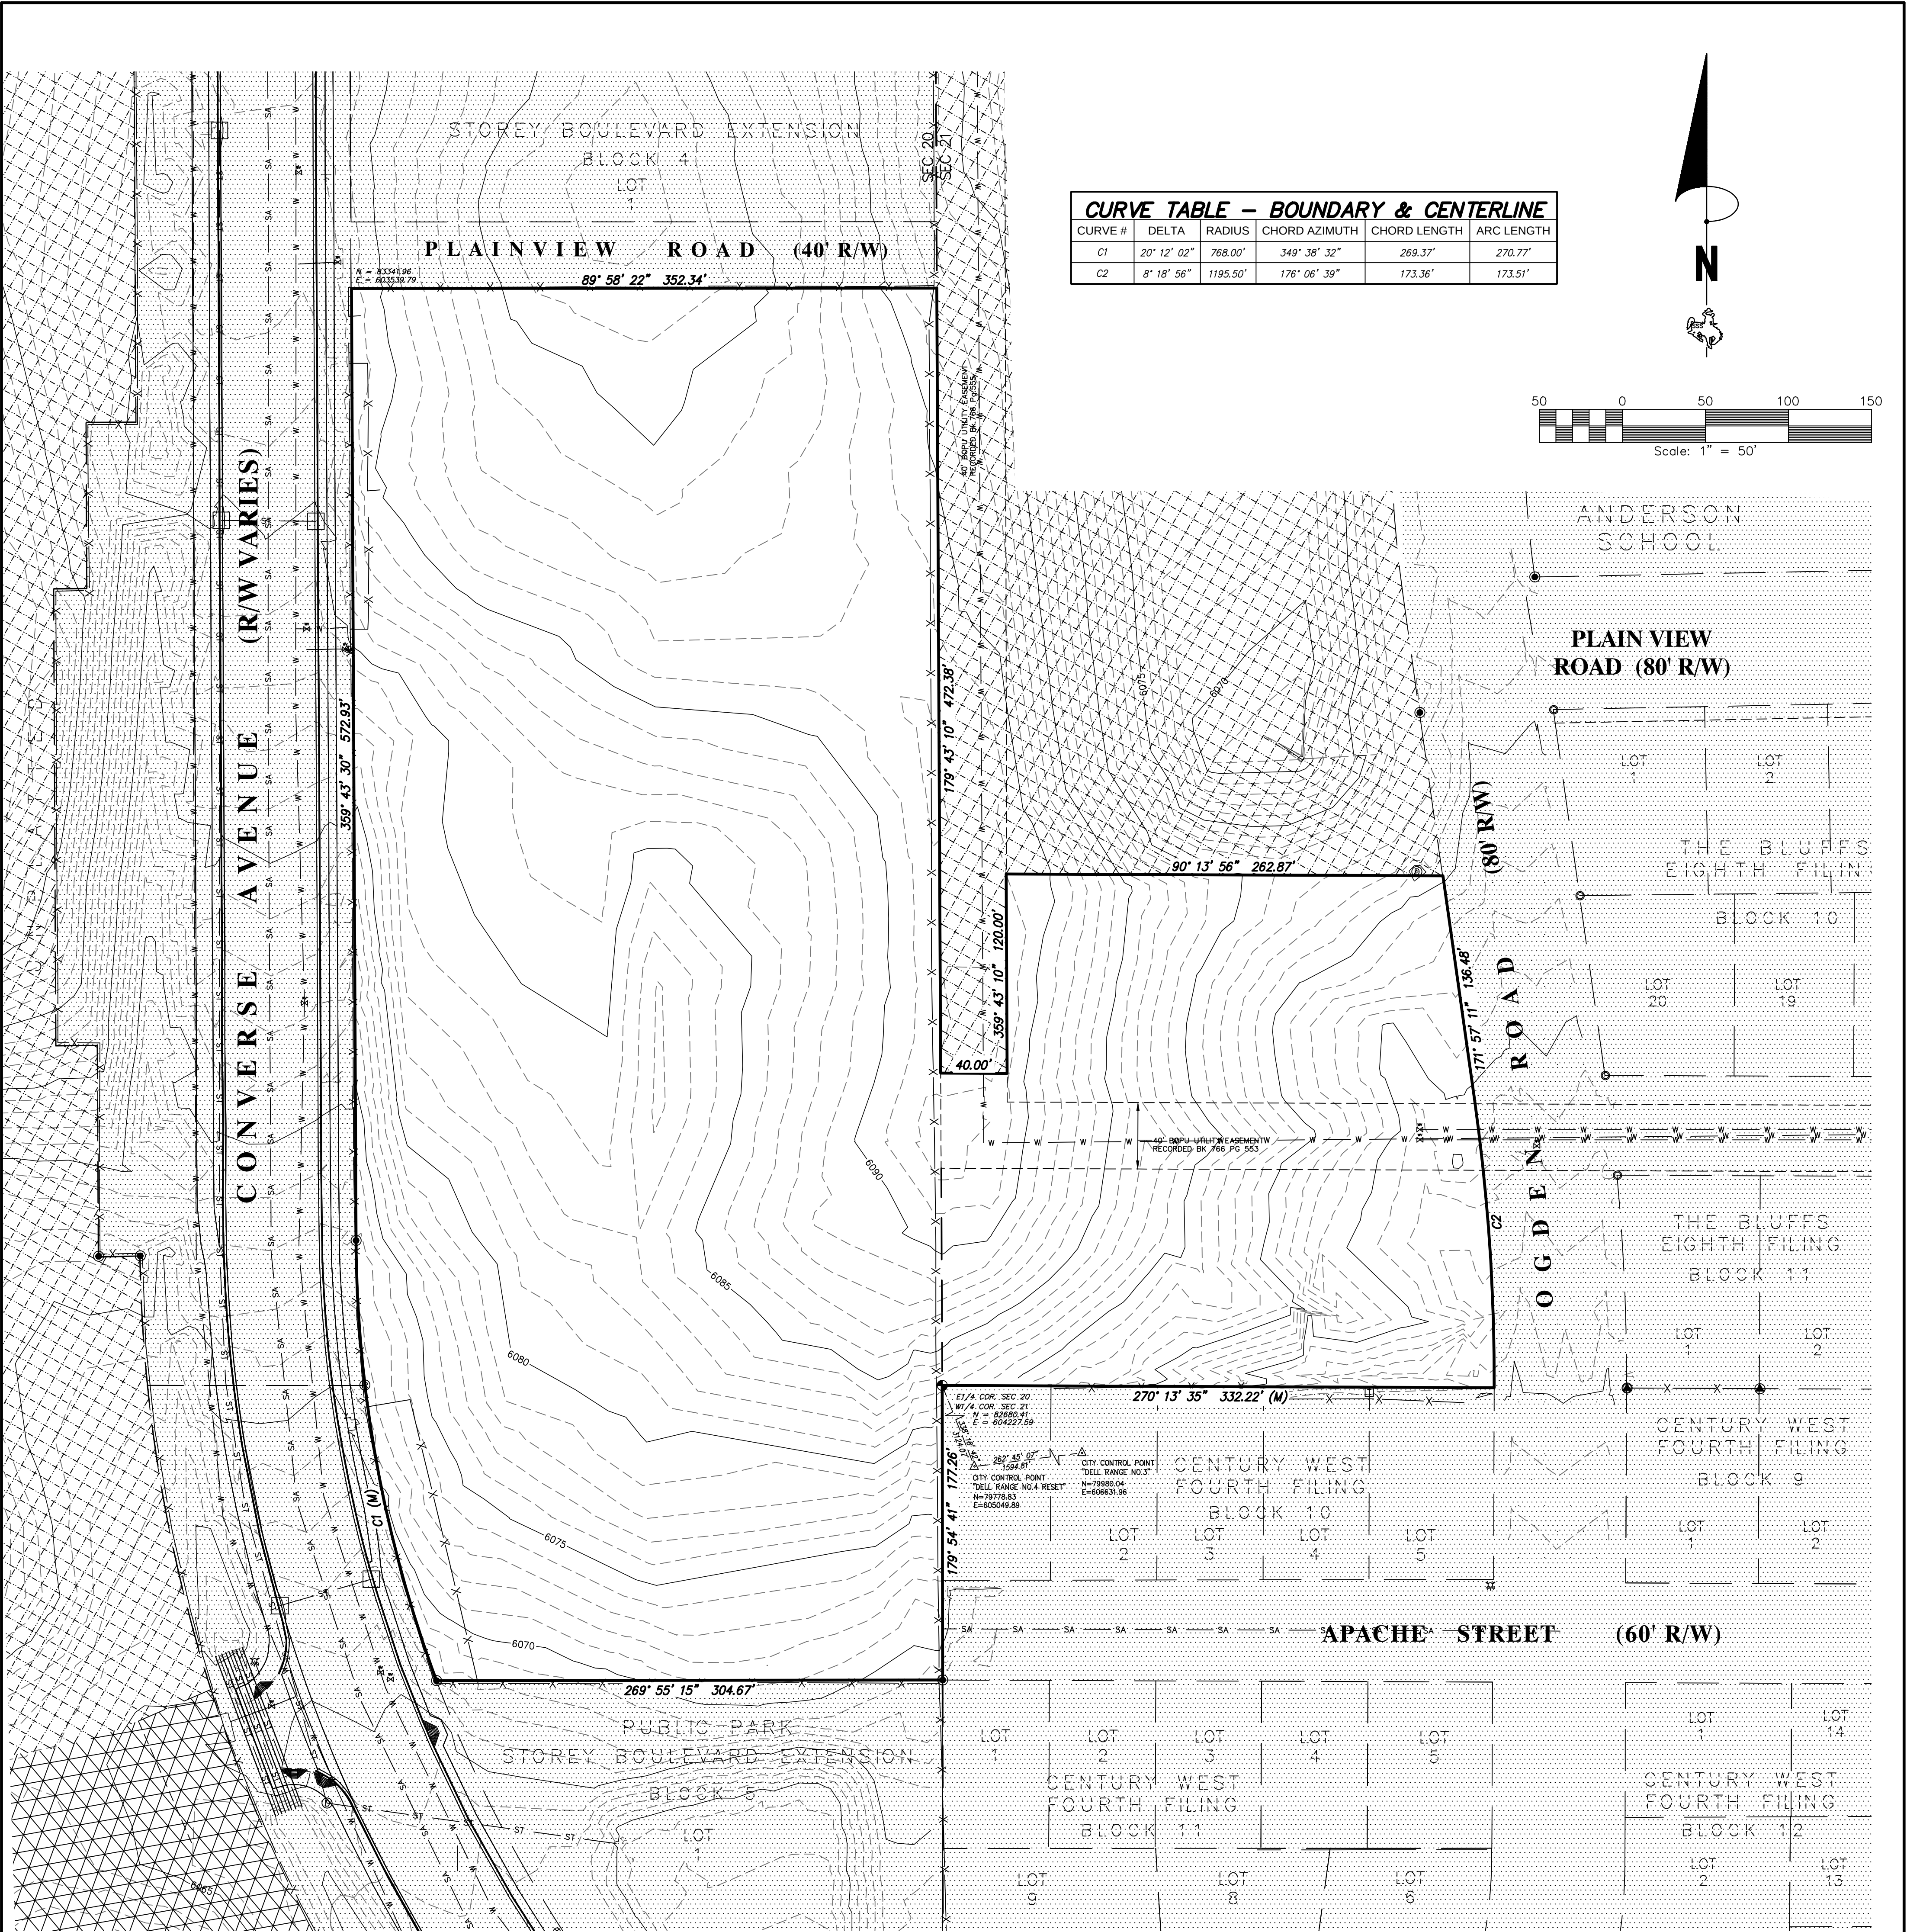

LAND DESCRIPTION

Parcel 1
Township 14 North, Range 66 West of the 6th P.M., Laramie County, Wyoming.

Section 20: A portion of the E1/2 E1/2 E1/2, being more particularly described as follows:

Beginning at the E1/4 corner of said Section 20; thence 179° 55' 22", a distance of 177.16 feet; thence 269° 55' 41", a distance of 304.32 feet to a point on the east boundary of the Converse Avenue right-of-way; thence northwesterly along said Converse Avenue boundary line along a curve concave to the northeast, having a radius of 746.32 feet and a central angle of 20° 47' 29" (chord azimuth of 349° 38' 18", chord distance of 269.34 feet); thence 359° 41' 16", a distance of 572.83 feet; thence 89° 58' 31", a distance of 352.39 feet; thence 179° 43' 03", a distance of 660.39 feet to the point of beginning.

Containing 291,063sf (6.68 acres) more or less.

Parcel 2
Township 14 North, Range 66 West of the 6th P.M., Laramie County, Wyoming.

Section 21: A portion of the SW1/4 SW1/4 NW1/4, being more particularly described as follows:

Beginning at the W1/4 corner of said Section 21; thence 359° 43' 03" for a distance of 188.01 feet, to a point on the west boundary of a 40 foot Board of Public Utilities Easement (recorded in Book 766 Page 555 at the Laramie County Office of Records); thence 90° 13' 49", a distance of 40.00 feet to a point on the east boundary of said easement; thence, 359° 43' 03" along said east boundary line, a distance of 120.00 feet; thence 90° 13' 49", a distance of 262.90 feet to a point on the west boundary of Ogden Road right-of-way; thence 171° 54' 47" along said Ogden Road boundary line, a distance of 136.50 feet; thence southeasterly along said Ogden Road boundary line along a curve concave to the southwest, having a radius of 1195.50 feet and a central angle of 08° 19' 02" (chord azimuth of 176° 04' 18", chord distance of 173.39 feet); thence 270° 13' 49" a distance of 332.46 feet to the point of beginning.

Containing 94,220sf (2.16 acres) more or less.

LEGEND

- FOUND 3/4" X 24" LONG REBAR WITH 1 1/2" ALUMINUM CAP STAMPED "P.L.S. 2927"
- SET 3/4" X 24" LONG REBAR WITH 1 1/2" ALUMINUM CAP STAMPED "SSS P.L.S. 5910"
- ⊙ FOUND 1/4 CORNER BRASS CAP STAMPED "L.S. 519"
- (M) DENOTES MEASURED DATA THIS SURVEY
- (P) DENOTES DATA PER PLATS OF RECORD
- △ CITY OF CHEYENNE CONTROL MONUMENTS
- AREA TO BE ANNEXED
- ▨ OTHER LANDS CURRENTLY IN ANNEXATION PROCESS
- ▧ OTHER LANDS CURRENTLY OUTSIDE OF THE CITY OF CHEYENNE CORPORATE LIMITS (COUNTY)
- ▩ LANDS CURRENTLY INCORPORATED WITHIN THE CITY OF CHEYENNE CORPORATE LIMITS

NOTES

- 1) BASIS OF AZIMUTH - CITY OF CHEYENNE DATUM REFERENCED FROM CITY CONTROL MONUMENTS "DELL RANGE NO.4 RESET" & "HUDSON".
- 2) NO PORTION OF THE SUBJECT PROPERTY FALLS WITHIN FEMA SPECIAL 100-YEAR FLOOD HAZARD AREA AS SHOWN ON F.I.R.M. PANEL # 56021C1091F; DATED JANUARY 17, 2007.
- 3) WATER AND SEWER TO BE PROVIDED BY CITY OF CHEYENNE BOPU.

APPROVALS

Approved by the Council of the City of Cheyenne, Wyoming this ____ day of ____ 2012.

Mayor _____ ATTEST: _____ City Clerk

FILING RECORD

CERTIFICATE OF SURVEYOR

I, Jeffrey B. Jones, Registered Professional Land Surveyor in the State of Wyoming, for and on behalf of Steil Surveying Services, LLC, hereby state, to the best of my knowledge, information and belief, that this map was prepared from field notes taken during an actual survey made by me or under my direct supervision; and that this map correctly shows the results of said survey and that the monuments found or set are as shown.

**ANNEXATION
MAP
FOR
THE BLUFFS
9TH FILING**

SITUATED IN THE E½ OF SECTION 20, AND THE SW¼NW¼ OF SECTION 21; T.14N., R.66W., 6TH P.M., LARAMIE COUNTY, WYOMING.

Prepared October, 2012



STEIL SURVEYING SERVICES, LLC
PROFESSIONAL LAND SURVEYORS

1102 W. 19th ST. CHEYENNE, WY. 82001 (307)634-7273
756 GILCHRIST ST. WHEATLAND, WY. 82201 (307)322-9789

