
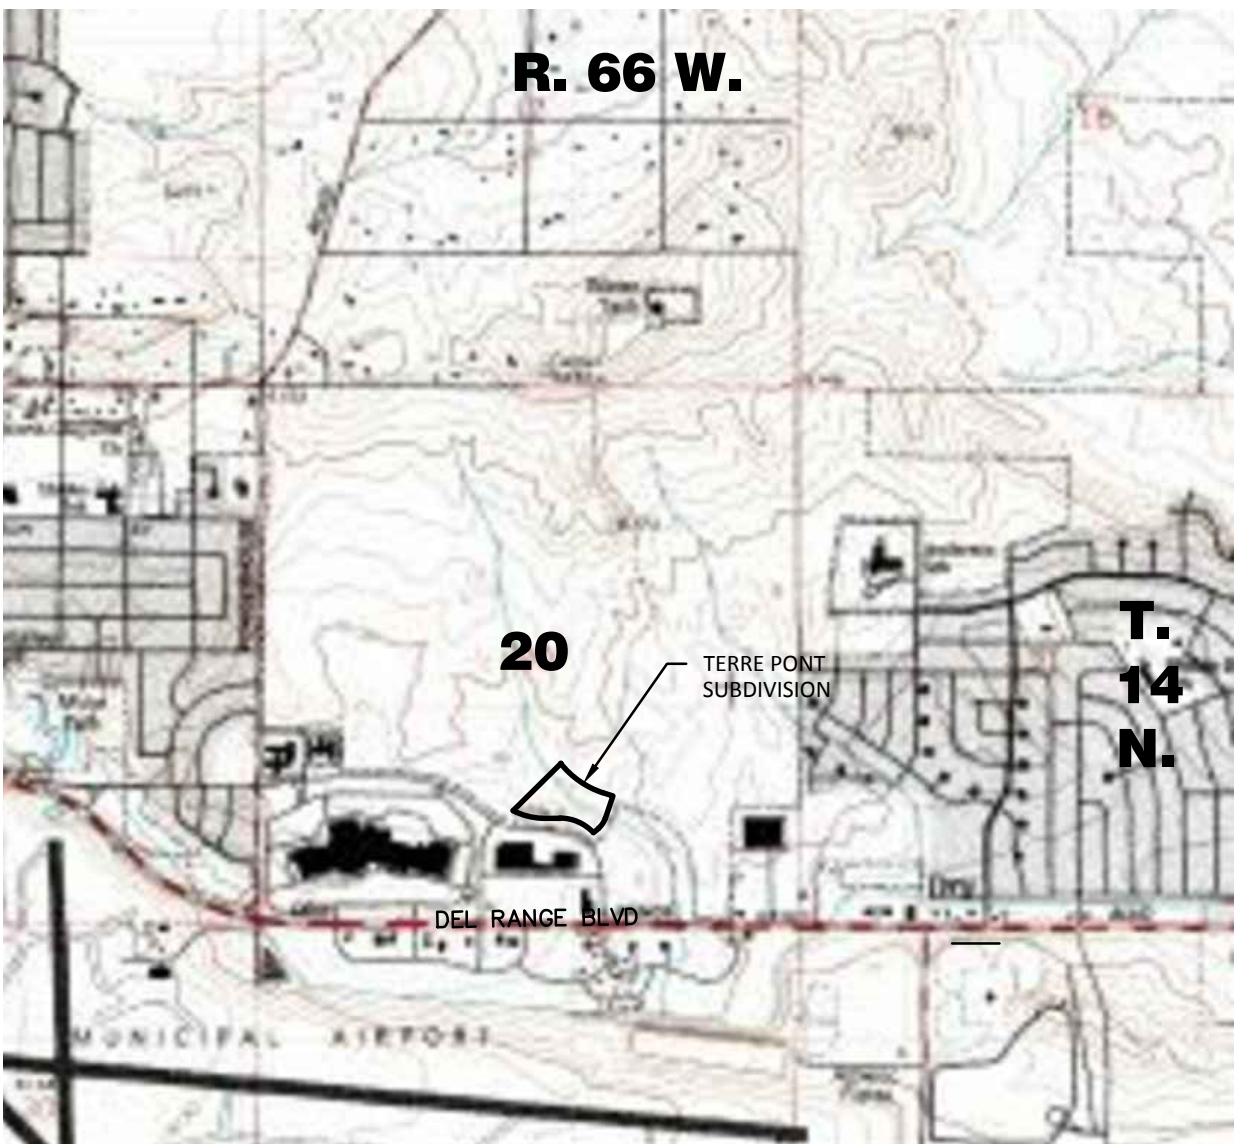


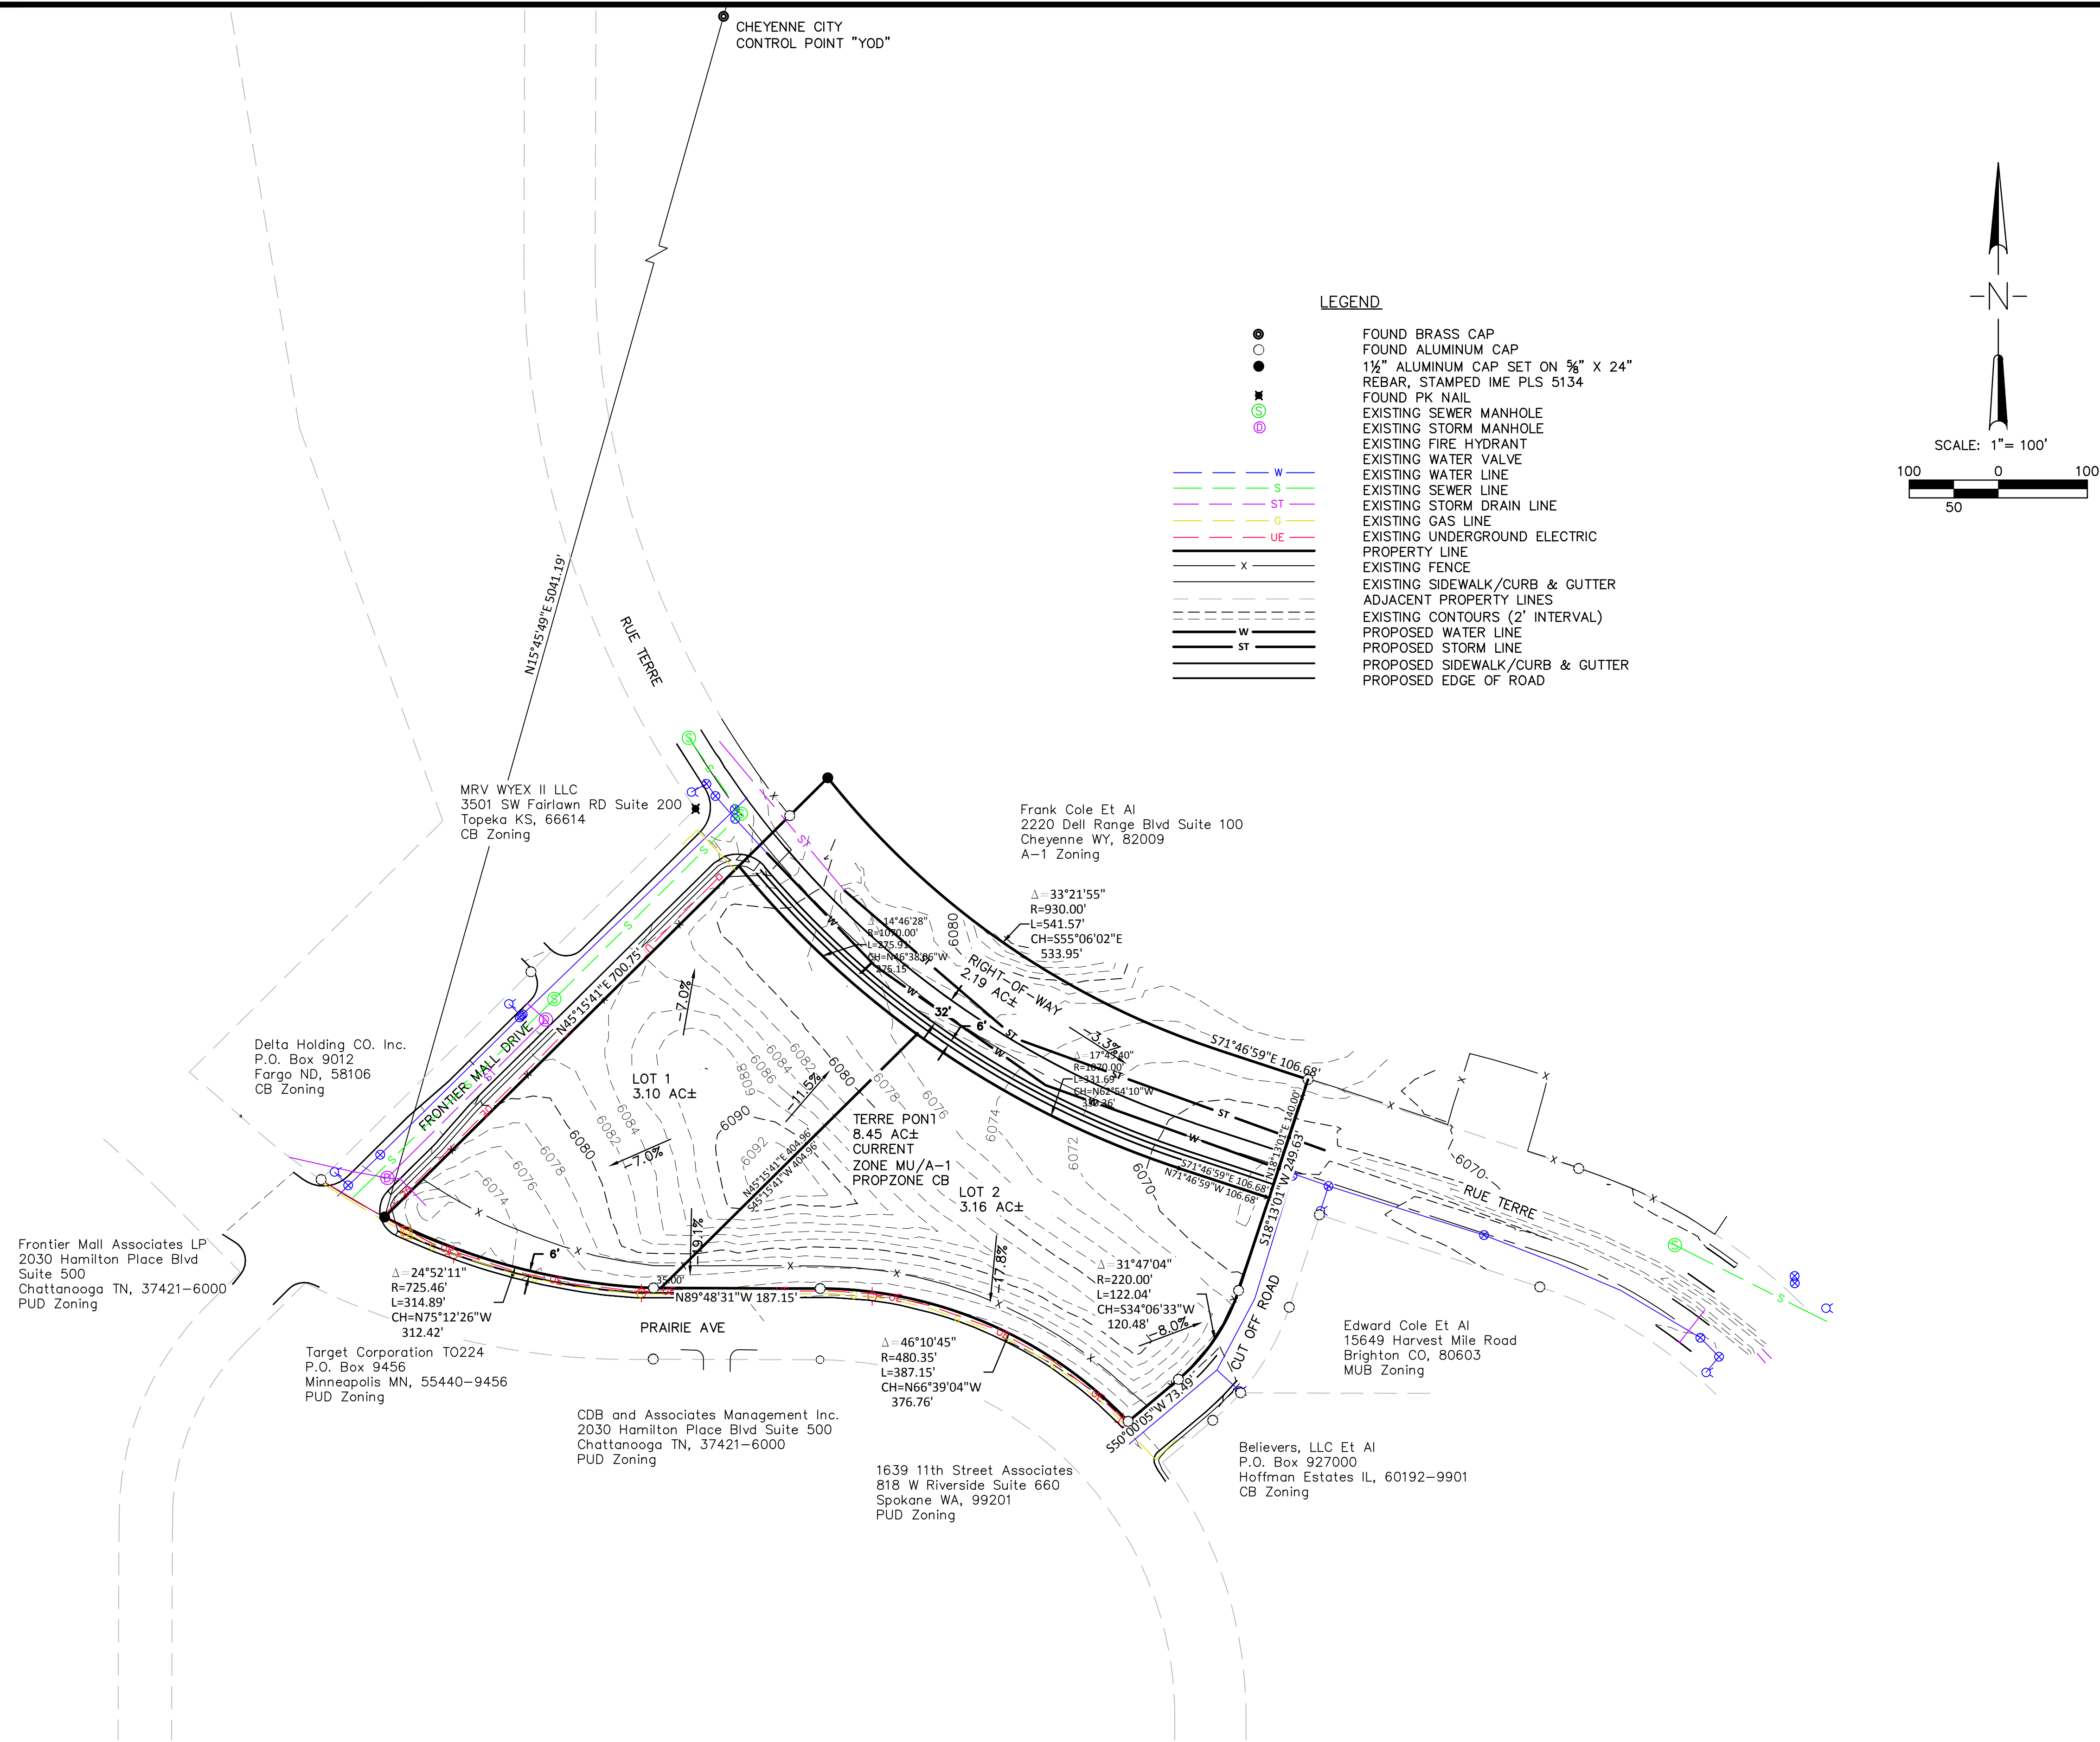

VICINITY MAP
1" = 2000'

- NOTE:
- LANDS WITHIN THIS PLAT AREA ARE NOT SUBJECT TO FLOODING ACCORDING TO THE AVERAGE FREQUENCY OF THE FIFTY-YEAR AND ONE HUNDRED-YEAR FLOOD PLANS.
 - OPEN SPACE TO MEET REQUIREMENTS OF UDC TABLE 4-15 WILL BE DETERMINED ON SITE PLAN.
 - NO RECORDED EASEMENTS OR RESTRICTIONS ASSOCIATED WITH THIS PARCEL.
 - THE UTILITY LOCATIONS SHOWN ARE AS MARKED BY THEIR OWNERS, FROM THE OWNERS RECORDS OR FROM FIELD EVIDENCE. THE SIZE AND LOCATION OF UNDERGROUND UTILITIES WAS NOT VERIFIED BY EXCAVATION. THE CONTRACTOR IS RESPONSIBLE FOR LOCATING AND PROTECTING UTILITIES DURING CONSTRUCTION.

SUBDIVIDERS:
TKO
P.O. Box 15
Aberdeen, South Dakota 57402
605-229-0030

PRELIMINARY PLAT OF TERRE PONT

LOCATED IN THE
S 1/2 SEC 20,
T. 14 N., R. 66 W., 6th P.M.
LARAMIE COUNTY, WYOMING

INBERG-MILLER ENGINEERS
124 EAST MAIN STREET
RIVERTON, WYOMING
DRAWN BY MDH
82501
DATE: 06/24/2013 BOOK 16446-HS
FILE: \\16446-HS PLAT.DWG