

LEGAL DESCRIPTION

THE FOLLOWING IS A LEGAL DESCRIPTION FOR A PARCEL OF LAND SITUATED IN A PORTION OF SECTIONS 14, 15, 22, 23 AND 27, TOWNSHIP 13 NORTH, RANGE 67 WEST OF THE SIXTH PRINCIPAL MERIDIAN, LARAMIE COUNTY WYOMING, AND BEING MORE PARTICULARLY DESCRIBED AS FOLLOWS:

BEGINNING AT THE ONE-QUARTER CORNER OF SECTIONS 14 AND 13 MONUMENTED BY A FOUND ALUMINUM CAP; THENCE S83°53'32"W A DISTANCE OF 2177.30 FEET TO A POINT ON THE WEST RIGHT OF WAY LINE OF CLEAR CREEK PARKWAY, SAID POINT ALSO BEING THE TRUE POINT OF BEGINNING;

THENCE ALONG SAID WESTERLY RIGHT OF WAY OF CLEAR CREEK PARKWAY THE FOLLOWING COURSES AND DISTANCES:

S04°54'36"E A DISTANCE OF 364.16 TO A POINT ON A CURVE CONCAVE WESTERLY;
SAID CURVE HAVING A RADIUS OF 1940.00 FEET, A DELTA ANGLE OF 15°05'39", WHOSE CHORD BEARS S02°38'15"W A DISTANCE OF 509.60 FEET; THENCE ALONG THE ARC OF SAID CURVE A DISTANCE OF 511.08 FEET TO A POINT;
THENCE S10°11'04"W A DISTANCE OF 309.02 FEET TO A POINT ON A CURVE CONCAVE EASTERLY;
SAID CURVE HAVING A RADIUS OF 2060.00 FEET, A DELTA ANGLE OF 18°09'17", WHOSE CHORD BEARS S01°06'26"W A DISTANCE OF 650.00 FEET; THENCE ALONG THE ARC OF SAID CURVE A DISTANCE OF 652.73 FEET TO A POINT;
THENCE S07°58'12"E A DISTANCE OF 348.93 FEET TO A POINT ON A CURVE CONCAVE WESTERLY;
SAID CURVE HAVING A RADIUS OF 1740.00 FEET, A DELTA ANGLE OF 38°48'19", WHOSE CHORD BEARS S11°25'57"W A DISTANCE OF 1156.07 FEET; THENCE ALONG THE ARC OF SAID CURVE A DISTANCE OF 1178.47 FEET TO A POINT;
THENCE S30°50'07"W A DISTANCE OF 1066.18 FEET TO A POINT ON A CURVE CONCAVE WESTERLY;
SAID CURVE HAVING A RADIUS OF 9940.00, A DELTA ANGLE OF 10°18'42", WHOSE CHORD BEARS S35°59'28"W A DISTANCE OF 1786.51 FEET; THENCE ALONG THE ARC OF SAID CURVE A DISTANCE OF 1788.92 FEET TO A POINT;
THENCE S41°08'49"W A DISTANCE OF 891.86 FEET TO A POINT ON A CURVE CONCAVE EASTERLY;
SAID CURVE HAVING A RADIUS OF 10060.00 FEET, A DELTA ANGLE OF 09°22'48", WHOSE CHORD BEARS S36°27'24"W A DISTANCE OF 1645.08 FEET; THENCE ALONG THE ARC OF SAID CURVE A DISTANCE OF 1646.92 FEET TO A POINT;
THENCE S 31°46'08"W A DISTANCE OF 223.67 FEET TO A POINT ON A CURVE CONCAVE WESTERLY;
SAID CURVE HAVING A RADIUS OF 2940.00 FEET, A DELTA ANGLE OF 21°43'09", WHOSE CHORD BEARS S42°37'35"W A DISTANCE OF 1107.81 FEET TO A POINT; THENCE ALONG THE ARC OF SAID CURVE A DISTANCE OF 1114.47 FEET TO A POINT;
THENCE S53°29'10"W A DISTANCE OF 528.24 FEET TO A POINT ON A CURVE CONCAVE EASTERLY;
SAID CURVE HAVING A RADIUS OF 3060.00 FEET, A DELTA ANGLE OF 20°35'45", WHOSE CHORD BEARS S43°11'18"W A DISTANCE OF 1094.04 FEET; THENCE ALONG THE ARC OF SAID CURVE A DISTANCE OF 1099.96 FEET TO A POINT;
THENCE S32°53'25"W A DISTANCE OF 767.24 FEET TO THE INTERSECTION OF THE SAID WESTERLY RIGHT OF WAY OF CLEAR CREEK PARKWAY AND THE NORTHERLY RIGHT OF WAY OF TUNDRA DRIVE;

THENCE ALONG SAID NORTHERLY RIGHT OF WAY OF TUNDRA DRIVE THE FOLLOWING COURSES AND DISTANCES;

THENCE N57°06'35"W A DISTANCE OF 276.06 FEET TO A POINT ON A CURVE CONCAVE NORTHERLY;
SAID CURVE HAVING A RADIUS OF 550.00 FEET, A DELTA ANGLE OF 17°47'11", WHOSE CHORD BEARS N48°12'59"W A DISTANCE OF 170.05 FEET; THENCE ALONG THE ARC OF SAID CURVE A DISTANCE OF 170.74 FEET TO A POINT;
THENCE N39°19'24"W A DISTANCE OF 355.59 FEET TO A POINT ON A CURVE CONCAVE SOUTHERLY;
SAID CURVE HAVING A RADIUS OF 350.00 FEET, A DELTA ANGLE OF 17°47'11", WHOSE CHORD BEARS N48°12'59"W A DISTANCE OF 108.22 FEET; THENCE ALONG THE ARC OF SAID CURVE A DISTANCE OF 108.65 FEET TO A POINT;
THENCE N57°06'35"W A DISTANCE OF 1741.36 FEET TO THE INTERSECTION OF SAID NORTHERLY RIGHT OF WAY OF TUNDRA DRIVE AND THE WESTERLY RIGHT OF WAY OF BERWICK DRIVE;


THENCE ALONG SAID WESTERLY RIGHT OF WAY OF BERWICK DRIVE THE FOLLOWING COURSES AND DISTANCES:

THENCE N34°38'33"E A DISTANCE OF 1727.74 FEET TO A POINT ON A CURVE CONCAVE WESTERLY;
SAID CURVE HAVING A RADIUS OF 525.08 FEET, A DELTA ANGLE OF 11°11'51", WHOSE CHORD BEARS N29°02'35"E A DISTANCE OF 102.46 FEET; THENCE ALONG THE ARC OF SAID CURVE A DISTANCE OF 102.62 FEET TO A POINT;
THENCE N23°21'11"E A DISTANCE OF 358.87 FEET TO A POINT ON A CURVE CONCAVE WESTERLY;
SAID CURVE HAVING A RADIUS OF 525.00 FEET, A DELTA ANGLE OF 19°14'06", WHOSE CHORD BEARS N13°44'08"E A DISTANCE OF 175.42 FEET; THENCE ALONG THE ARC OF SAID CURVE A DISTANCE OF 176.25 FEET TO A POINT;
THENCE N04°07'05"E A DISTANCE OF 200.00 FEET TO A POINT ON A CURVE CONCAVE EASTERLY;
SAID CURVE HAVING A RADIUS OF 625.00 FEET, A DELTA ANGLE OF 06°36'04", WHOSE CHORD BEARS N31°51'15"E A DISTANCE OF 71.97 FEET; THENCE ALONG THE ARC OF SAID CURVE A DISTANCE OF 72.01 FEET TO A POINT;
THENCE N10°43'09"E A DISTANCE OF 888.89 FEET TO A POINT ON A CURVE CONCAVE EASTERLY;
SAID CURVE HAVING A RADIUS OF 730.00 FEET, A DELTA ANGLE OF 42°16'13", WHOSE CHORD BEARS N31°51'15"E A DISTANCE OF 526.43 FEET; THENCE ALONG THE ARC OF SAID CURVE A DISTANCE OF 538.56 FEET TO A POINT;
THENCE N52°59'22"E A DISTANCE OF 646.39 FEET TO A POINT ON A CURVE CONCAVE WESTERLY;
SAID CURVE HAVING A RADIUS OF 600.00 FEET, A DELTA ANGLE OF 27°18'28", WHOSE CHORD BEARS N39°20'07"E A DISTANCE OF 283.27 FEET; THENCE ALONG THE ARC OF SAID CURVE A DISTANCE OF 285.97 FEET TO A POINT;
THENCE N25°40'53"E A DISTANCE OF 3406.27 FEET TO A POINT;
THENCE N26°07'40"E A DISTANCE OF 1277.69 FEET TO A POINT;
THENCE LEAVING SAID WESTERLY RIGHT OF WAY S64°19'09"E A DISTANCE OF 629.71 FEET TO A POINT ON A CURVE CONCAVE NORTHERLY;
SAID CURVE HAVING A RADIUS OF 600.00 FEET, A DELTA ANGLE OF 50°17'33", WHOSE CHORD BEARS S89°27'56"E A DISTANCE OF 509.92 FEET; THENCE ALONG THE ARC OF SAID CURVE A DISTANCE OF 526.66 FEET TO A POINT;
THENCE N65°23'18"E A DISTANCE OF 1376.10 FEET TO A POINT ON A CURVE CONCAVE SOUTHERLY;
SAID CURVE HAVING A RADIUS OF 570.00 FEET, A DELTA ANGLE OF 19°32'34", WHOSE CHORD BEARS N75°09'35"E A DISTANCE OF 193.48 FEET; THENCE ALONG THE ARC OF SAID CURVE A DISTANCE OF 194.42 FEET TO A POINT;
THENCE N84°55'52"E A DISTANCE OF 1057.24 FEET MORE OR LESS TO THE TRUE POINT OF BEGINNING;
SAID PARCEL OF LAND CONTAINS 882.79 ACRES MORE OR LESS.


- LEGEND
- EXISTING CITY LIMIT
 - PROPOSED CITY LIMIT
 - FOUND ALUMINUM CAP 10838
 - FOUND ALUMINUM CAP 12045
 - SET ALUMINUM CAP 12045

COMPUTATIONS:

- TOTAL ANNEXATION AREA - 882.79 AC
- DEDICATED STREET AREA - 22.24 AC.
- CONTIGUOUS BOUNDARY - 8.67%

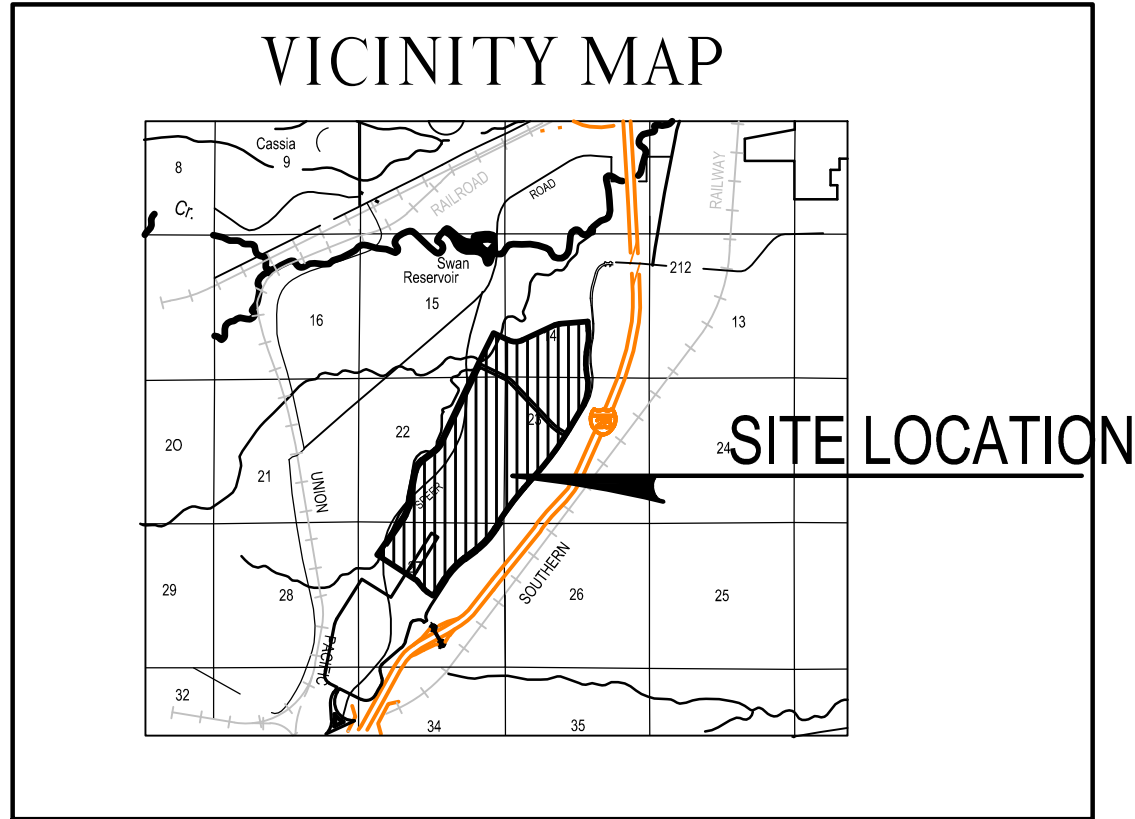

H:\Swan Ranch Planning\Annexation.dwg Apr 18, 2013 9:54am cphinson

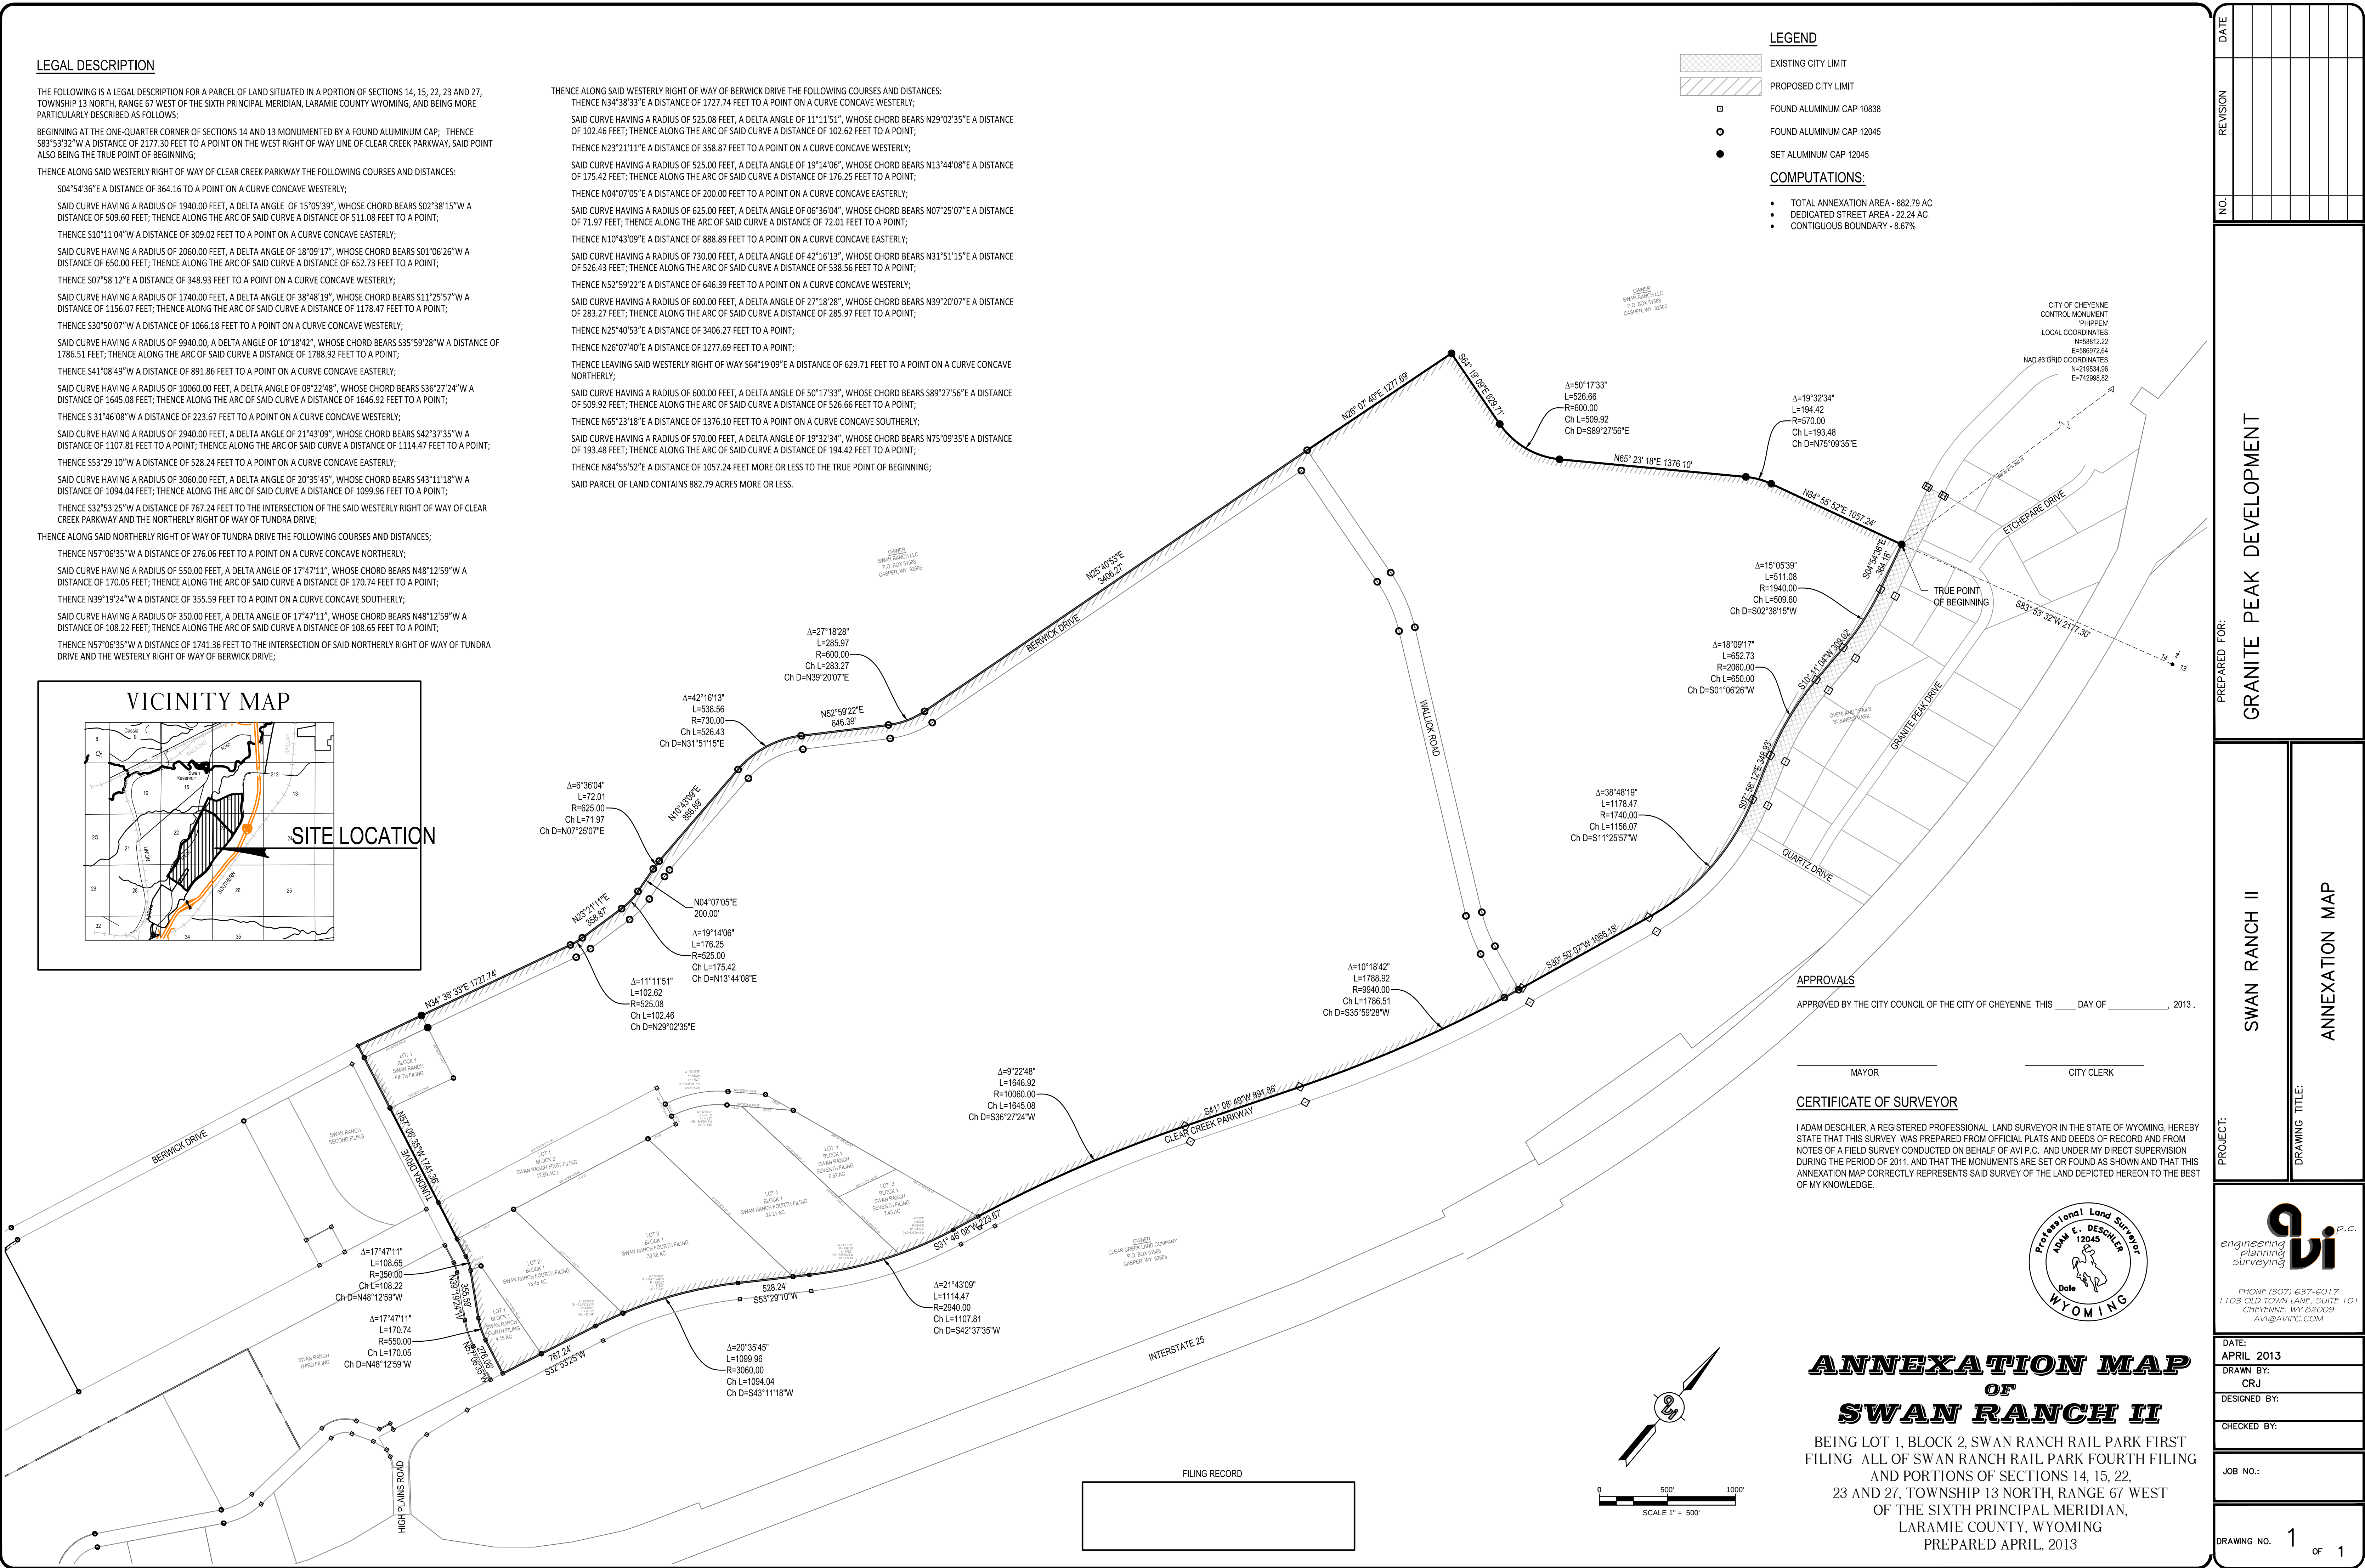


APPROVALS

APPROVED BY THE CITY COUNCIL OF THE CITY OF CHEYENNE THIS ____ DAY OF _____, 2013 .

MAYOR CITY CLERK

CERTIFICATE OF SURVEYOR

I ADAM DESCHLER, A REGISTERED PROFESSIONAL LAND SURVEYOR IN THE STATE OF WYOMING, HEREBY STATE THAT THIS SURVEY WAS PREPARED FROM OFFICIAL PLATS AND DEEDS OF RECORD AND FROM NOTES OF A FIELD SURVEY CONDUCTED ON BEHALF OF AVI P.C. AND UNDER MY DIRECT SUPERVISION DURING THE PERIOD OF 2011, AND THAT THE MONUMENTS ARE SET OR FOUND AS SHOWN AND THAT THIS ANNEXATION MAP CORRECTLY REPRESENTS SAID SURVEY OF THE LAND DEPICTED HEREON TO THE BEST OF MY KNOWLEDGE.

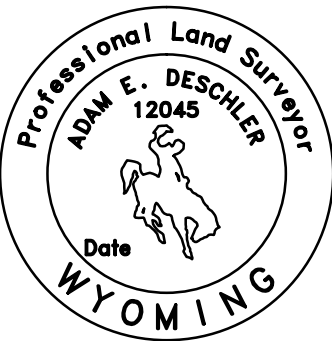

ANNEXATION MAP OF SWAN RANCH II

BEING LOT 1, BLOCK 2, SWAN RANCH RAIL PARK FIRST FILING ALL OF SWAN RANCH RAIL PARK FOURTH FILING AND PORTIONS OF SECTIONS 14, 15, 22, 23 AND 27, TOWNSHIP 13 NORTH, RANGE 67 WEST OF THE SIXTH PRINCIPAL MERIDIAN, LARAMIE COUNTY, WYOMING PREPARED APRIL, 2013

NO.	REVISION	DATE

PREPARED FOR: GRANITE PEAK DEVELOPMENT

PROJECT: SWAN RANCH II
DRAWING TITLE: ANNEXATION MAP

avi P.C.
engineering
planning
surveying
PHONE (307) 637-6017
1103 OLD TOWN LANE, SUITE 101
CHEYENNE, WY 82009
AVI@AVIPC.COM

DATE: APRIL 2013
DRAWN BY: CRJ
DESIGNED BY:
CHECKED BY:
JOB NO.:
DRAWING NO. 1 OF 1