


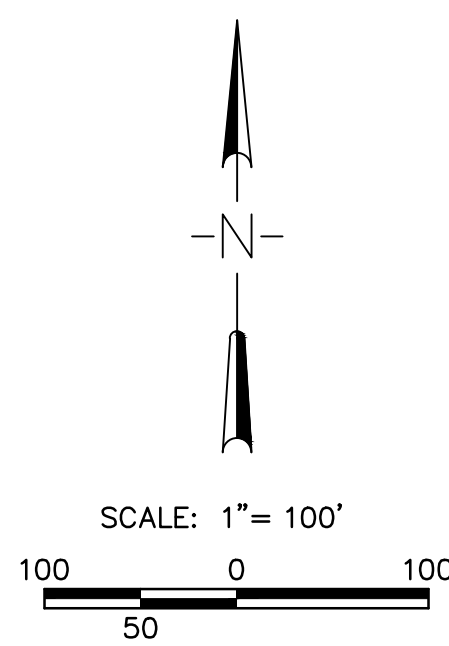

I, Randall S. Stelzner, do hereby certify that I am a Professional Land Surveyor of the State of Wyoming, that this plat is a true, correct and complete plat of the Terre Pout Subdivision to the City of Cheyenne, Wyoming, as laid out, platted, dedicated and shown hereon, that such plat was made from an accurate survey of said property by me or under my supervision and correctly shows the location and dimensions of the lot, and right-of-way of said subdivision as the same are staked upon the ground in compliance with the City of Cheyenne subdivision regulations governing the subdivision of land.

Approved by the Cheyenne Planning Commission
this _____ day of _____, 2013.

Development Director

Approved by the City Council of the City of Cheyenne Wyoming,
this _____ day of _____, 2013

Mayor

City Clerk

Know all men by these presents that, Edward George Cole, Casey Lee Cole, Christy Kay Cole, Kevin Louis Cole, Lester Lee Cole,
and Ann M. Cole having an equitable interest in all real property described as follows:

A parcel of land located in the South ½ Section 20, T.14N., R.66W., 6th P.M., City of Cheyenne, Laramie County, Wyoming, said parcel of land being more particularly described as follows:

BEGIN at the southeasterly corner of the Frontier North 2nd Filing, a subdivision map recorded as Reception Number 469124 and filed in P/C 9, Slot 20 in the office of the Laramie County Clerk and Records in Cheyenne, Wyoming, being a set rebar with 2 inch aluminum cap stamped IME, LS 5134; thence along said Point of Beginning, N45°15'41"E along the southeasterly line of said Frontier North 2nd Filing and its northerly extension, 700.76 feet (record azimuth 45°15'41") to a set rebar with 2 inch aluminum cap stamped IME, LS 5134; thence along an arc of a non-tangent curve concave to the northeast 541.57 feet, said curve having a radius of 930.00 feet and chord bearing S55°06'02"E, 533.95 feet to a set rebar with 2 inch aluminum cap stamped IME, LS 5134; thence S71°46'59"E, 106.68 feet to a found aluminum cap stamped LS 2500 at the northwest corner of Terri Fini, a subdivision map recorded as Reception Number 074530 and filed in P/C 6, Slot 41, in said Clerk's office; thence along the westerly line of said Terri Fini the following three courses: thence S18°13'10"N, 249.63 feet (record azimuth 198°12'21"), 249.63 feet to a found aluminum cap stamped LS 2500; thence along an arc of a curve concave to the northwest 122.04 feet, said curve having a radius of 220.0 feet and chord bearing S34°06'33"N, 120.49 feet (record length of 122.04 feet and radius of 220.00 feet) to a found aluminum cap stamped LS 2500; and, thence S50°00'05"W, 73.44 feet (record azimuth 229°59'25", 73.31 feet) to intersect the northerly right-of-way line of Prairie Avenue also being the northerly line of Frontier Square, 2nd Filing, a subdivision map recorded as Reception Number 782124 and filed in P/C 9, Slot 20 in the office of the Laramie County Clerk and Records in Cheyenne, Wyoming, being a set rebar with 2 inch aluminum cap stamped IME, LS 5134; thence along the northerly right-of-way line and said northerly line of Frontier Square, 2nd Filing, the following three courses: thence along an arc of a non-tangent curve concave to the southwest 387.18 feet, said curve having a radius of 480.23 feet and chord bearing of N66°39'32"W, 376.78 feet (record radius of 480.00 feet) to a found aluminum cap stamped LS 2500; thence N89°48'27"W, 187.15 feet (record azimuth 270°13'16", 187.18 feet) to a found aluminum cap stamped LS 2500; thence along an arc of a non-tangent curve concave to the northeast 314.89 feet, said curve having a radius of 725.46 feet and chord bearing N75°12'26"W, 312.42 feet, to the Point of Beginning of this parcel description, containing 368.132 square feet, or 8.45 acres of land, more or less, and subject to all easements, rights-of-way and restrictions of record.

Have caused the same to be surveyed, platted and known as the TERRE PONT SUBDIVISION, do hereby declare the subdivision of said lands as it appears on this plat, to be their free act and deed and in accordance with their desires, and do hereby dedicate to the public the streets and grant the easements for the purposes indicated hereon.

Edward George Cole

Casey Lee Cole

Christy Kay Cole now know as
Christy Marziano

Kevin Louis Cole

Lester Lee Cole

Ann M. Cole

STATE OF _____)
COUNTY OF _____) SS

The dedication instrument was acknowledged before me this ____day of _____, 2013
by Edward George Cole.

Notary Public, _____ County, _____
My commission Expires _____

STATE OF _____)
COUNTY OF _____) SS

The dedication instrument was acknowledged before me this ____day of _____, 2013
by Casey Lee Cole.

Notary Public, _____ County, _____
My commission Expires _____

STATE OF _____)
COUNTY OF _____) SS

The dedication instrument was acknowledged before me this ____day of _____, 2013 by Christy Kay Cole, now know as Christy Marziano.

Notary Public, _____ County, _____
My commission Expires _____

STATE OF _____) SS
COUNTY OF _____)

The dedication instrument was acknowledged before me this ____day of _____, 2013
by Kevin Louis Cole.

Notary Public, _____ County, _____
My commission Expires _____

STATE OF _____)
COUNTY OF _____) SS

The dedication instrument was acknowledged before me this ____day of _____, 2013
by Lester Lee Cole.

Notary Public, _____ County, _____
My commission Expires _____

STATE OF _____)
COUNTY OF _____) SS

The dedication instrument was acknowledged before me this ____day of _____, 2013
by Ann M. Cole.

Notary Public, _____ County, _____
My commission Expires _____

INBERG-MILLER ENGINEERS
124 EAST MAIN STREET
(307)856-8136 RIVERTON, WYOMING
DRAWN BY MDH

82501

DATE: 08/29/2013 16446-HS
16446-HS PLAT.DWG

**LOCATED IN THE
S¹/₂ SECTION 20,
T. 14 N., R. 66 W., 6th P.M.
CHEYENNE, LARAMIE COUNTY, WYOMING**