

# Fox Farm Road Corridor Plan

## Appendix A – Corridor Plan and Profile Sheets

- Fox Farm Road Corridor Plan 10/35 %



# FOX FARM ROAD CORRIDOR PLAN 10/35%

## INDEX OF SHEETS

| SHEET NO.   | DESCRIPTION                        |
|-------------|------------------------------------|
| 1           | TITLE SHEET                        |
| 2           | TYPICAL SECTIONS                   |
| ST01 - ST20 | PLAN & PROFILE FOX FARM RD.        |
| ST21        | PLAN & PROFILE WALTERSCHIED BLVD.  |
| ST22        | PLAN & PROFILE AVENUE C            |
| ST23        | PLAN COLLEGE DRIVE                 |
| ST24 - ST33 | PLAN & PROFILE BURLINGTON TRAIL    |
| XS01 - XS21 | CROSS SECTIONS FOX FARM RD.        |
| XS22 - XS23 | CROSS SECTIONS WALTERSCHIED BLVD.  |
| XS24 - XS25 | CROSS SECTIONS AVENUE C            |
| XS26 - XS37 | CROSS SECTIONS BURLINGTON TRAIL    |
| XS38 - XS47 | CROSS SECTIONS BURLINGTON SIDEWALK |

### SURVEY CONTROL:

|                   |                                   |
|-------------------|-----------------------------------|
| HORIZONTAL DATUM: | CITY OF CHEYENNE CONTROL (GROUND) |
| VERTICAL DATUM:   | NAVD 88                           |

#### CP COLLEGE

N:59732.36  
E:608926.74  
ELEV:6001.75

#### CP INTERSTATE

N:64971.63  
E:599701.15  
ELEV:6109.58

### ENGINEER:




1103 OLD TOWN LANE,  
SUITE 101  
CHEYENNE, WYOMING 82001  
307.637.6017  
FAX 307.632.9326  
WWW.AVIPC.COM

## LARAMIE COUNTY, WYOMING


**ENGINEER'S CERTIFICATE:** I HEREBY CERTIFY THAT THESE PLANS WERE PREPARED BY ME OR UNDER MY DIRECT SUPERVISION AND THAT I AM A DULY REGISTERED PROFESSIONAL ENGINEER IN THE STATE OF WYOMING.

**TOPOGRAPHIC SURVEY:** PORTIONS OF THE TOPOGRAPHIC SURVEY, PLANIMETRICS, AND UTILITY INFORMATION DEPICTING EXISTING CONDITIONS WERE PROVIDED BY DATAMAP DIGITAL SERVICES, INC. AVI, PC. IS NOT RESPONSIBLE FOR THE ACCURACY OR COMPLETENESS OF SURVEY DATA SUPPLIED BY OTHERS.

**BOUNDARY & PROPERTY INFORMATION:** BOUNDARY AND PROPERTY INFORMATION DEPICTED WAS PROVIDED BY THE CHEYENNE-LARAMIE COUNTY COOPERATIVE GIS DATA BASE AND IS FOR DISPLAY PURPOSES ONLY. AVI, PC IS NOT RESPONSIBLE FOR THE ACCURACY OR COMPLETENESS OF THE GIS RIGHTS-OF-WAY, PROPERTY LINES, OR OWNERSHIPS.

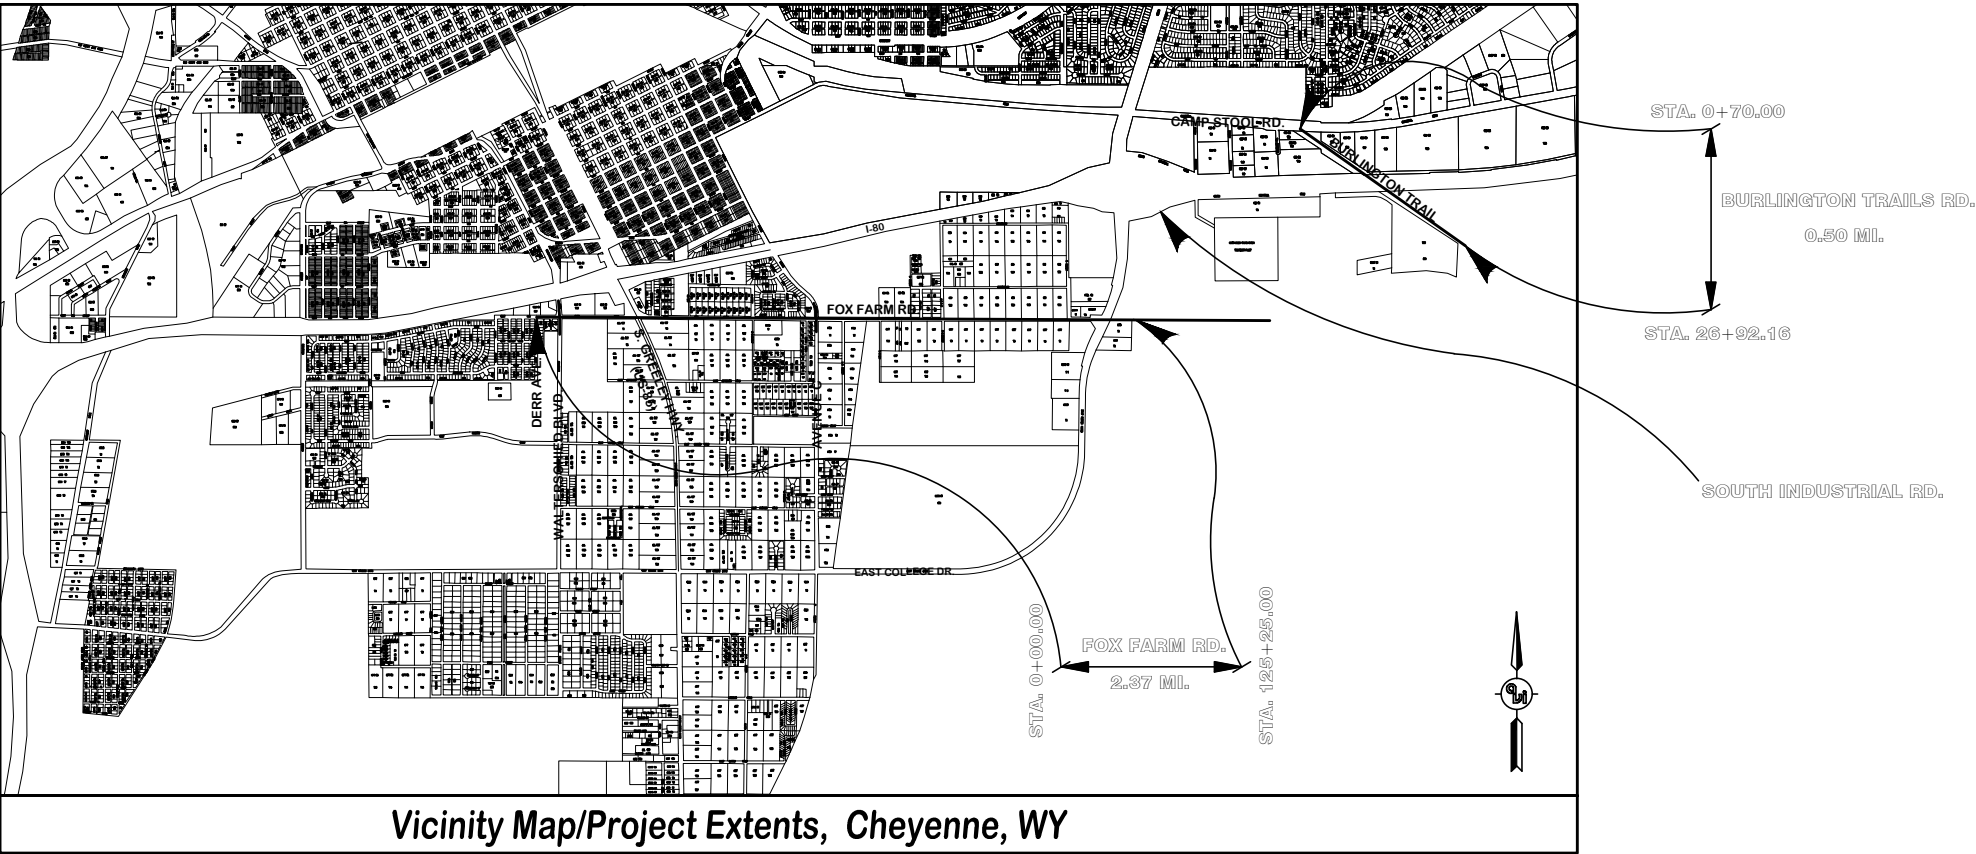

H:\3211\design\3211B FOX FARM STREET IMP.dwg Aug 30, 2013 4:07pm jwilson

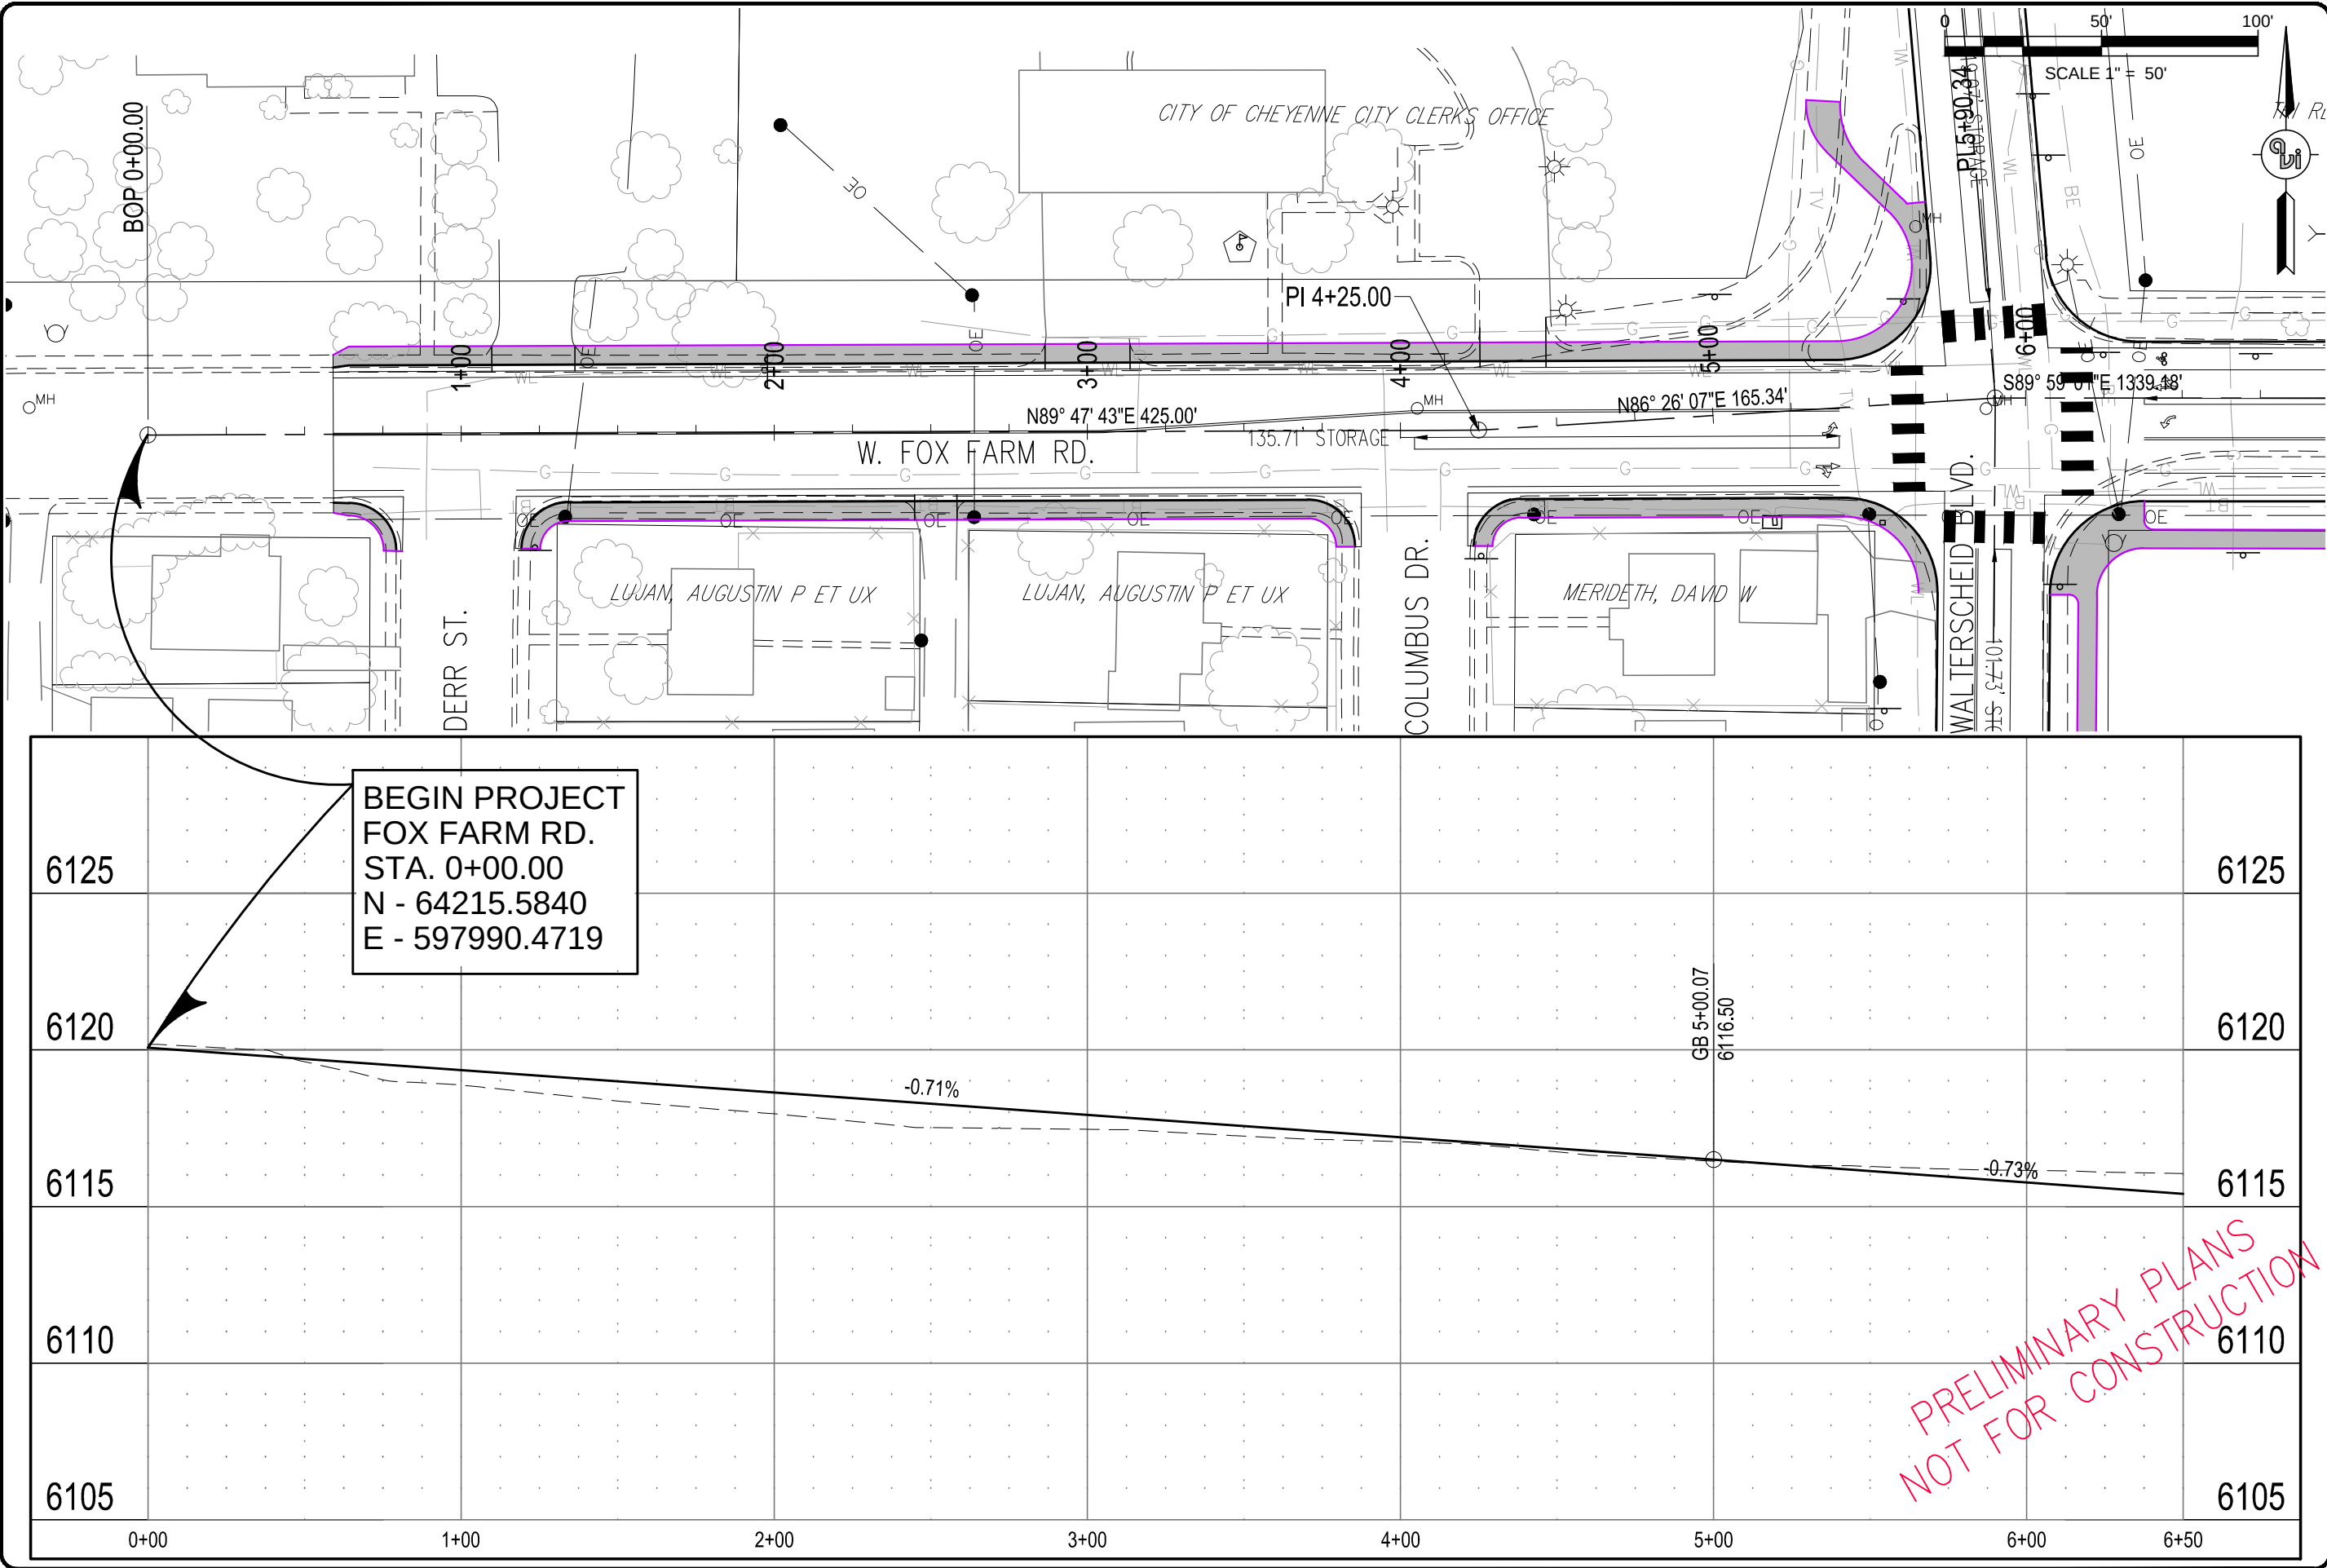

| DATE |          |
|------|----------|
| NO.  | REVISION |
|      |          |
|      |          |
|      |          |

PREPARED FOR:  
MPO  
2101 ONEIL AVE.  
RM 205  
CHEYENNE, WY. 82001

PROJECT:  
FOX FARM ROAD STREET  
IMPROVEMENTS

DRAWING TITLE:  
FOX FARM RD. PLAN AND PROFILE  
STA. 0+00 - 6+50



**avi** p.c.  
engineering  
planning  
surveying  
PHONE (307) 637-6017  
1103 OLD TOWN LANE, SUITE 101  
CHEYENNE, WY 82009  
AVI@AVIPC.COM

DATE:  
6-20-13  
DRAWN BY:  
SRL  
DESIGNED BY:  
TC  
CHECKED BY:  
TC

JOB NO.:  
2-3211-B

ST-01 83  
SHEET NO. OF

H:\3211\design\3211B FOX FARM STREET IMP.dwg Aug 30, 2013 4:08pm jwilson

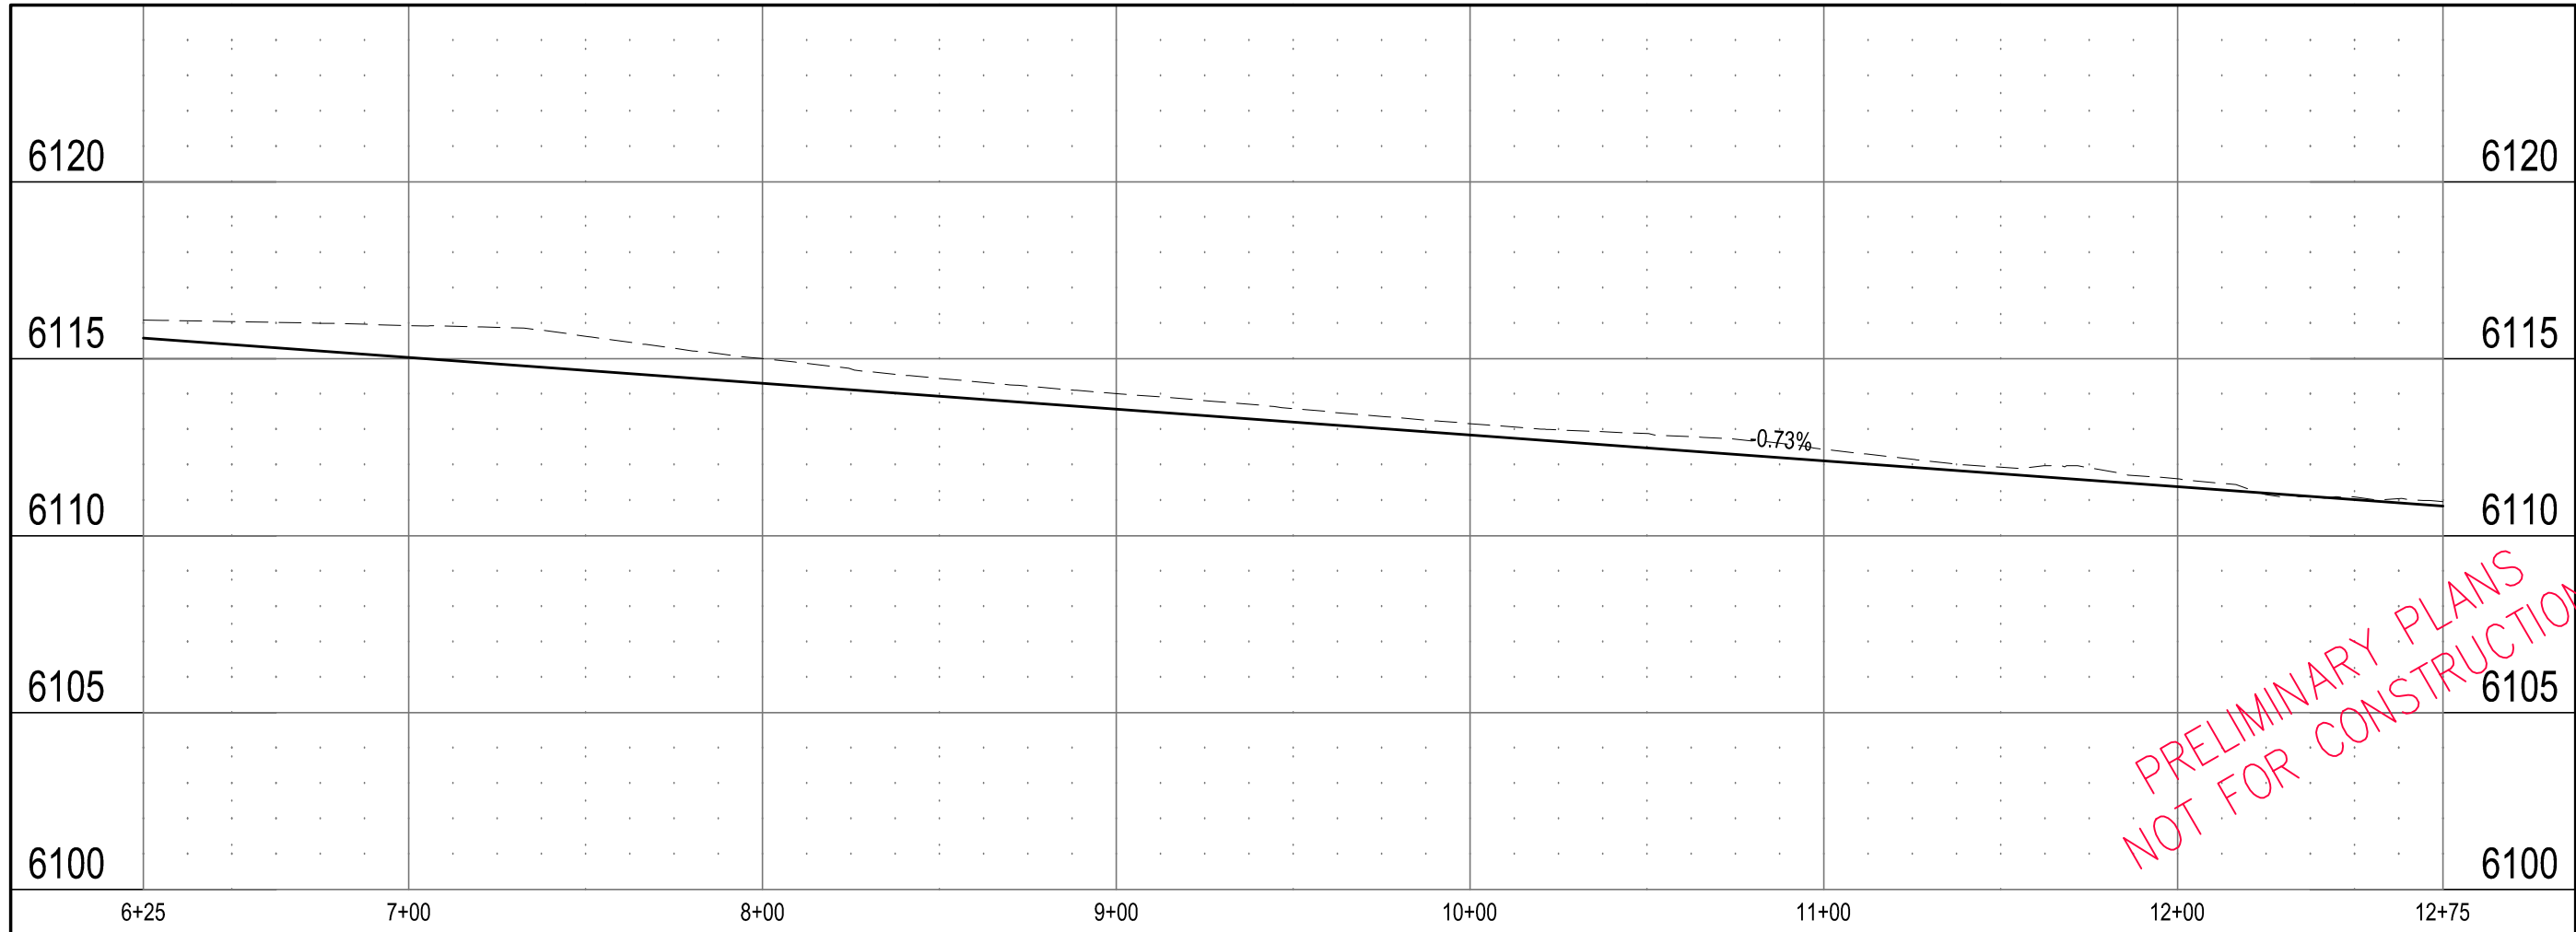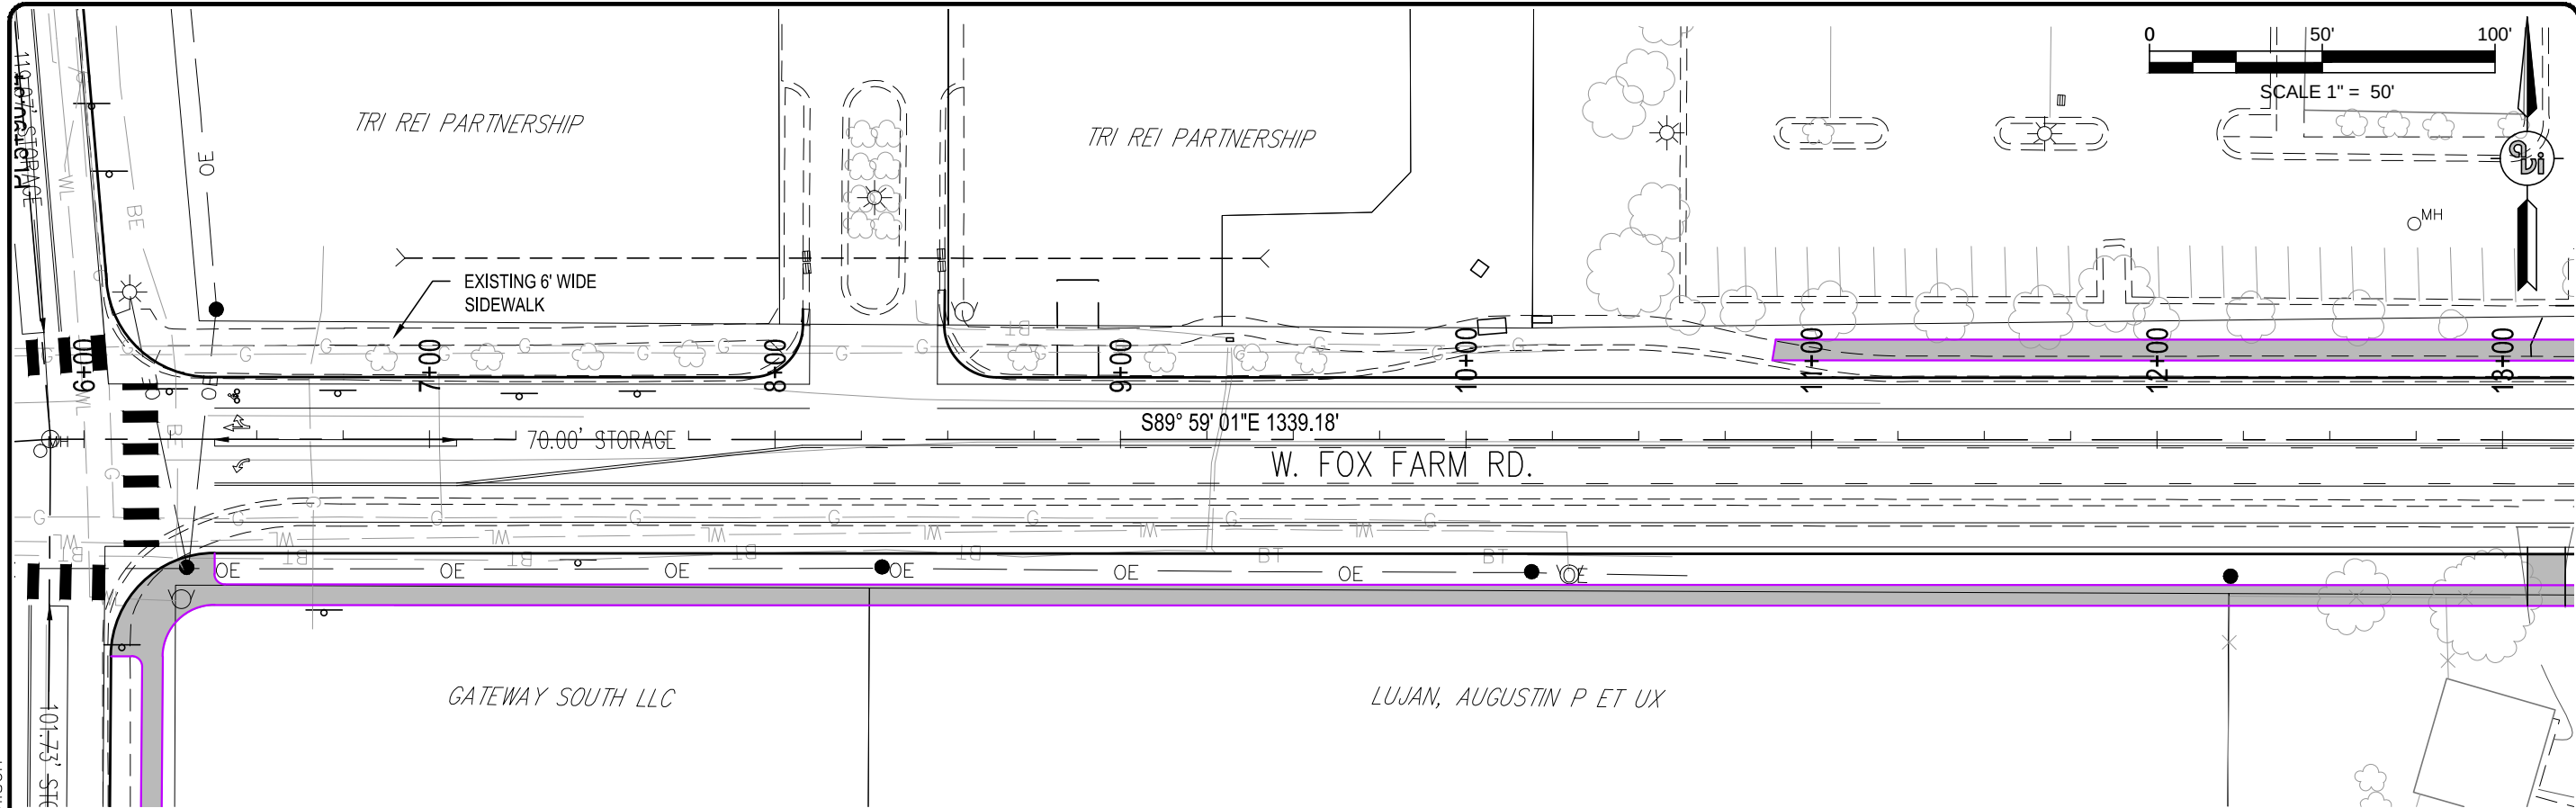

PRELIMINARY PLANS  
NOT FOR CONSTRUCTION

|          |  |
|----------|--|
| DATE     |  |
| REVISION |  |
| NO.      |  |

PREPARED FOR:  
MPO  
2101 ONEIL AVE.  
RM 205  
CHEYENNE, WY. 82001

PROJECT:  
FOX FARM ROAD STREET IMPROVEMENTS

DRAWING TITLE:  
FOX FARM RD. PLAN AND PROFILE  
STA. 6+25 - 12+75



**avi** p.c.  
engineering  
planning  
surveying  
PHONE (307) 637-6017  
1103 OLD TOWN LANE, SUITE 101  
CHEYENNE, WY 82009  
AVI@AVIPC.COM

DATE:  
6-20-13  
DRAWN BY:  
SRL  
DESIGNED BY:  
TC  
CHECKED BY:  
TC

JOB NO.:  
2-3211-B

ST-02 83  
SHEET NO. OF

H:\3211\design\3211B FOX FARM STREET IMP.dwg Aug 30, 2013 4:08pm jwilson

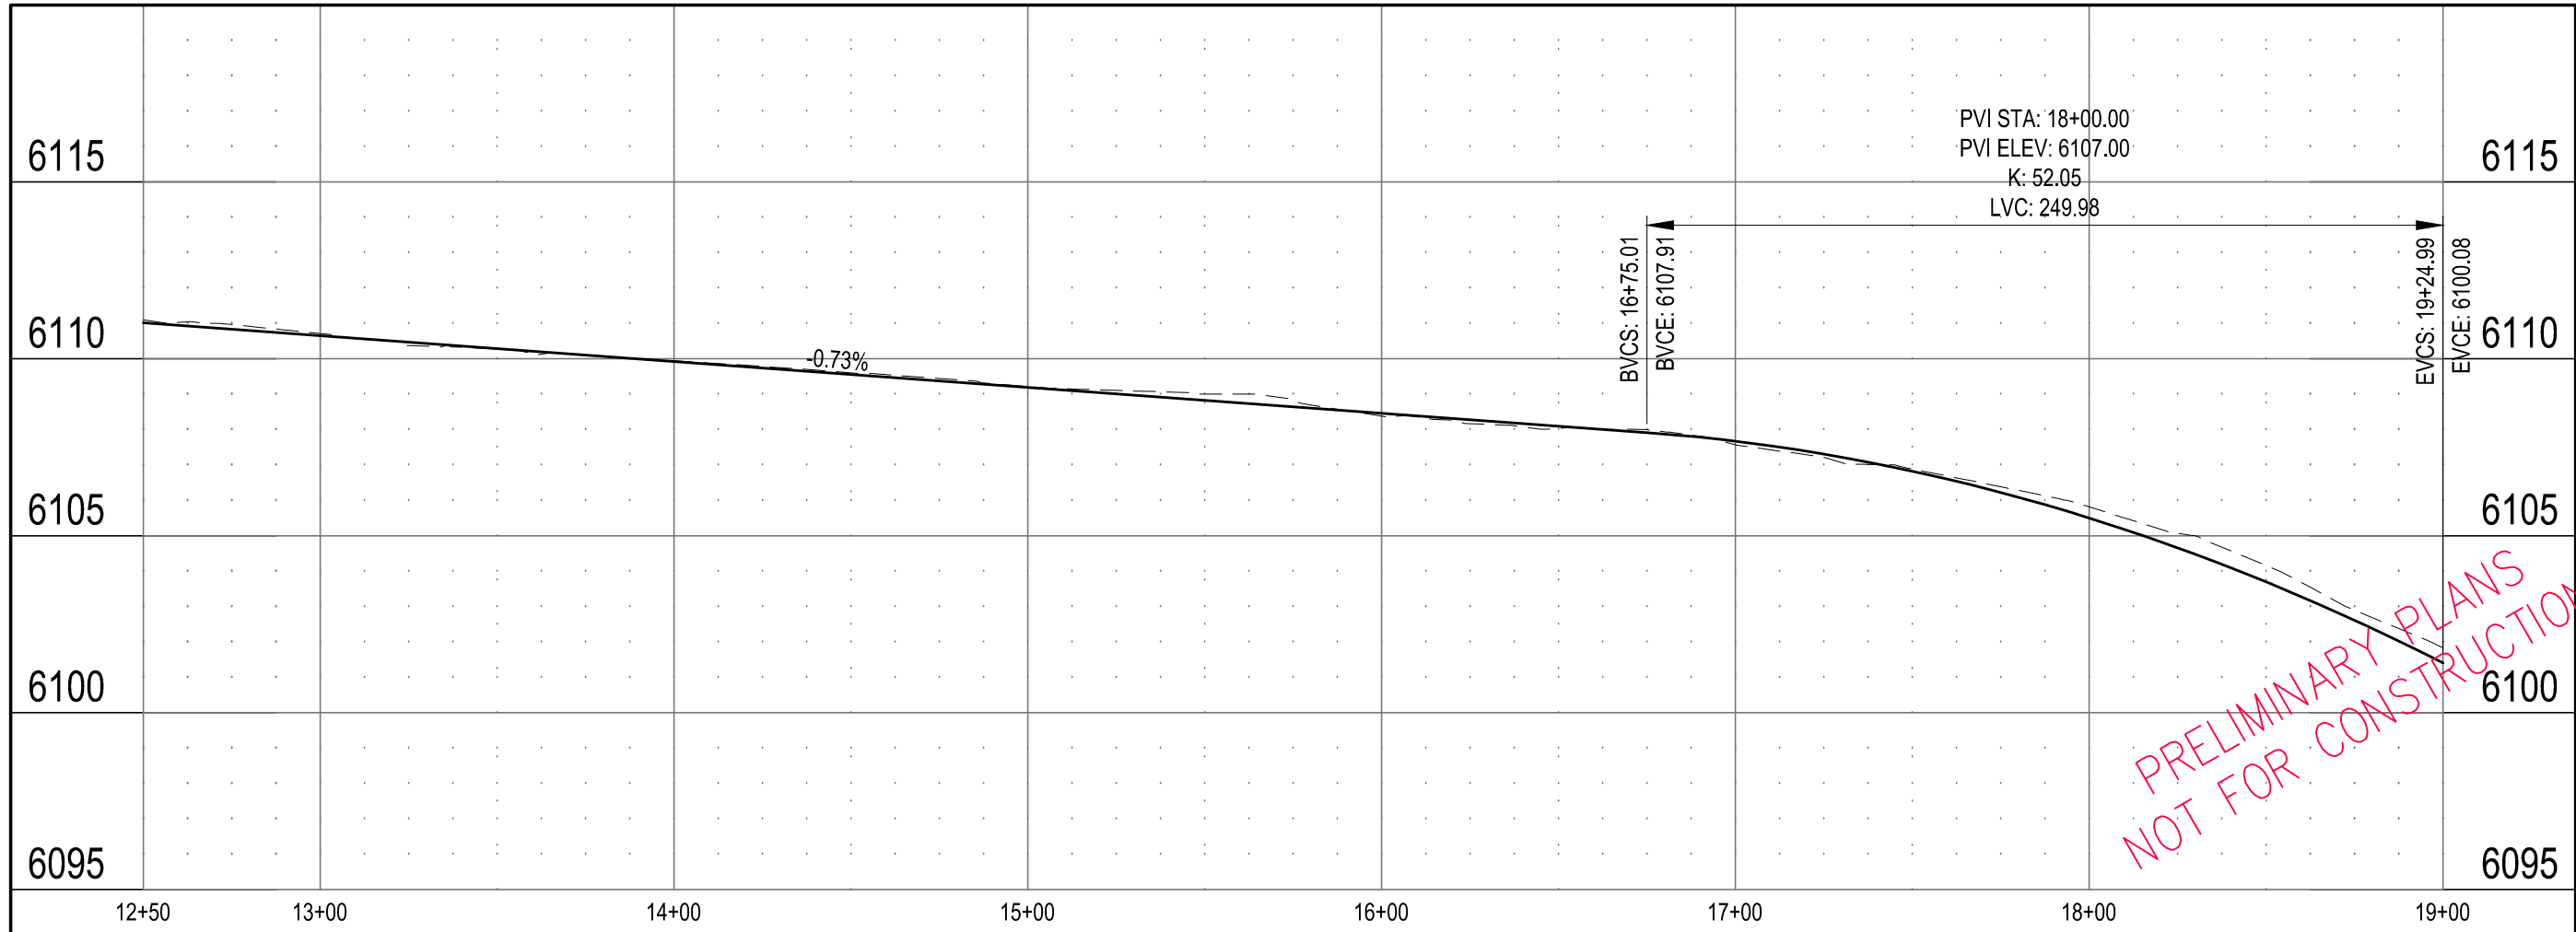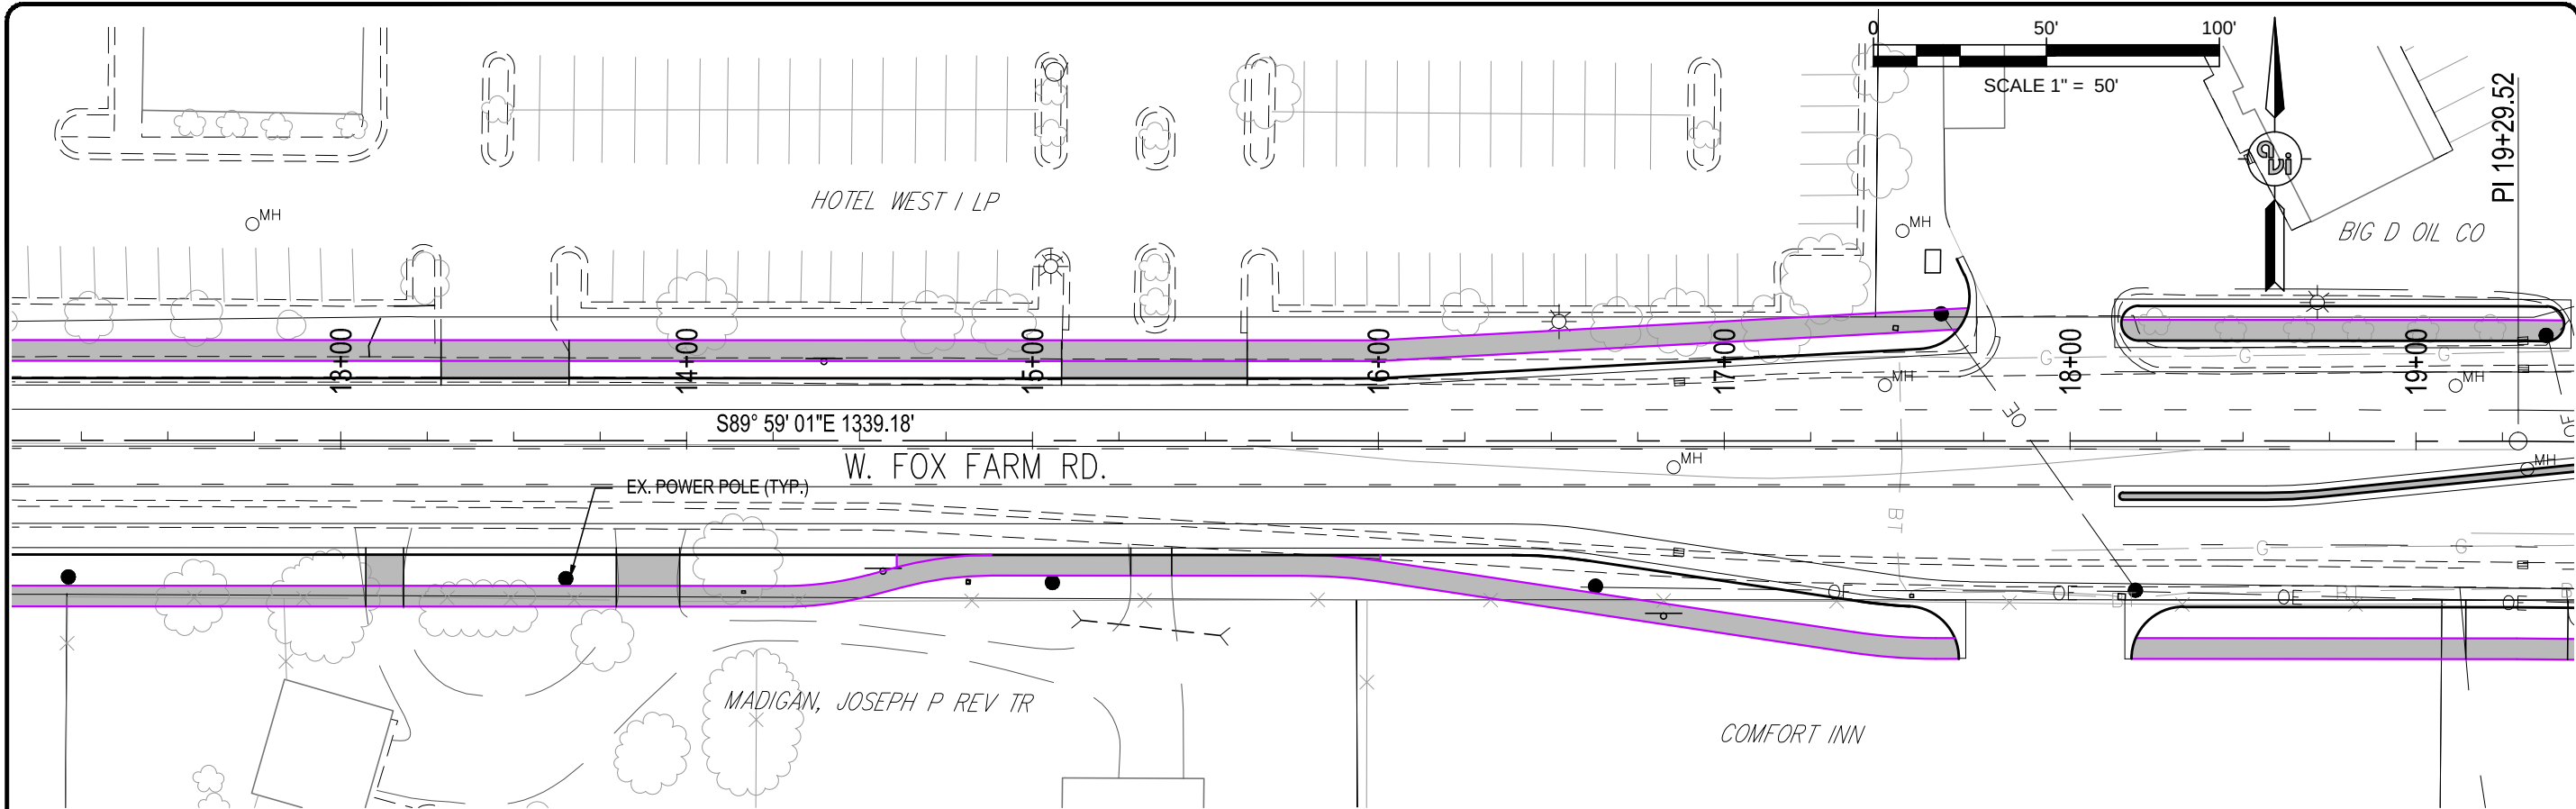

PRELIMINARY PLANS  
NOT FOR CONSTRUCTION

|          |  |
|----------|--|
| DATE     |  |
| REVISION |  |
| NO.      |  |

PROJECT: FOX FARM ROAD STREET IMPROVEMENTS

DRAWING TITLE: FOX FARM RD. PLAN AND PROFILE  
STA. 12+50 - 19+00



PREPARED FOR:  
MPO  
2101 ONEIL AVE.  
RM 205  
CHEYENNE, WY. 82001

AVI p.c.  
engineering  
planning  
surveying  
PHONE (307) 637-6017  
1103 OLD TOWN LANE, SUITE 101  
CHEYENNE, WY 82009  
AVI@AVIPC.COM

DATE: 6-20-13  
DRAWN BY: SRL  
DESIGNED BY: TC  
CHECKED BY: TC

JOB NO.: 2-3211-B

ST-03 83  
SHEET NO. OF

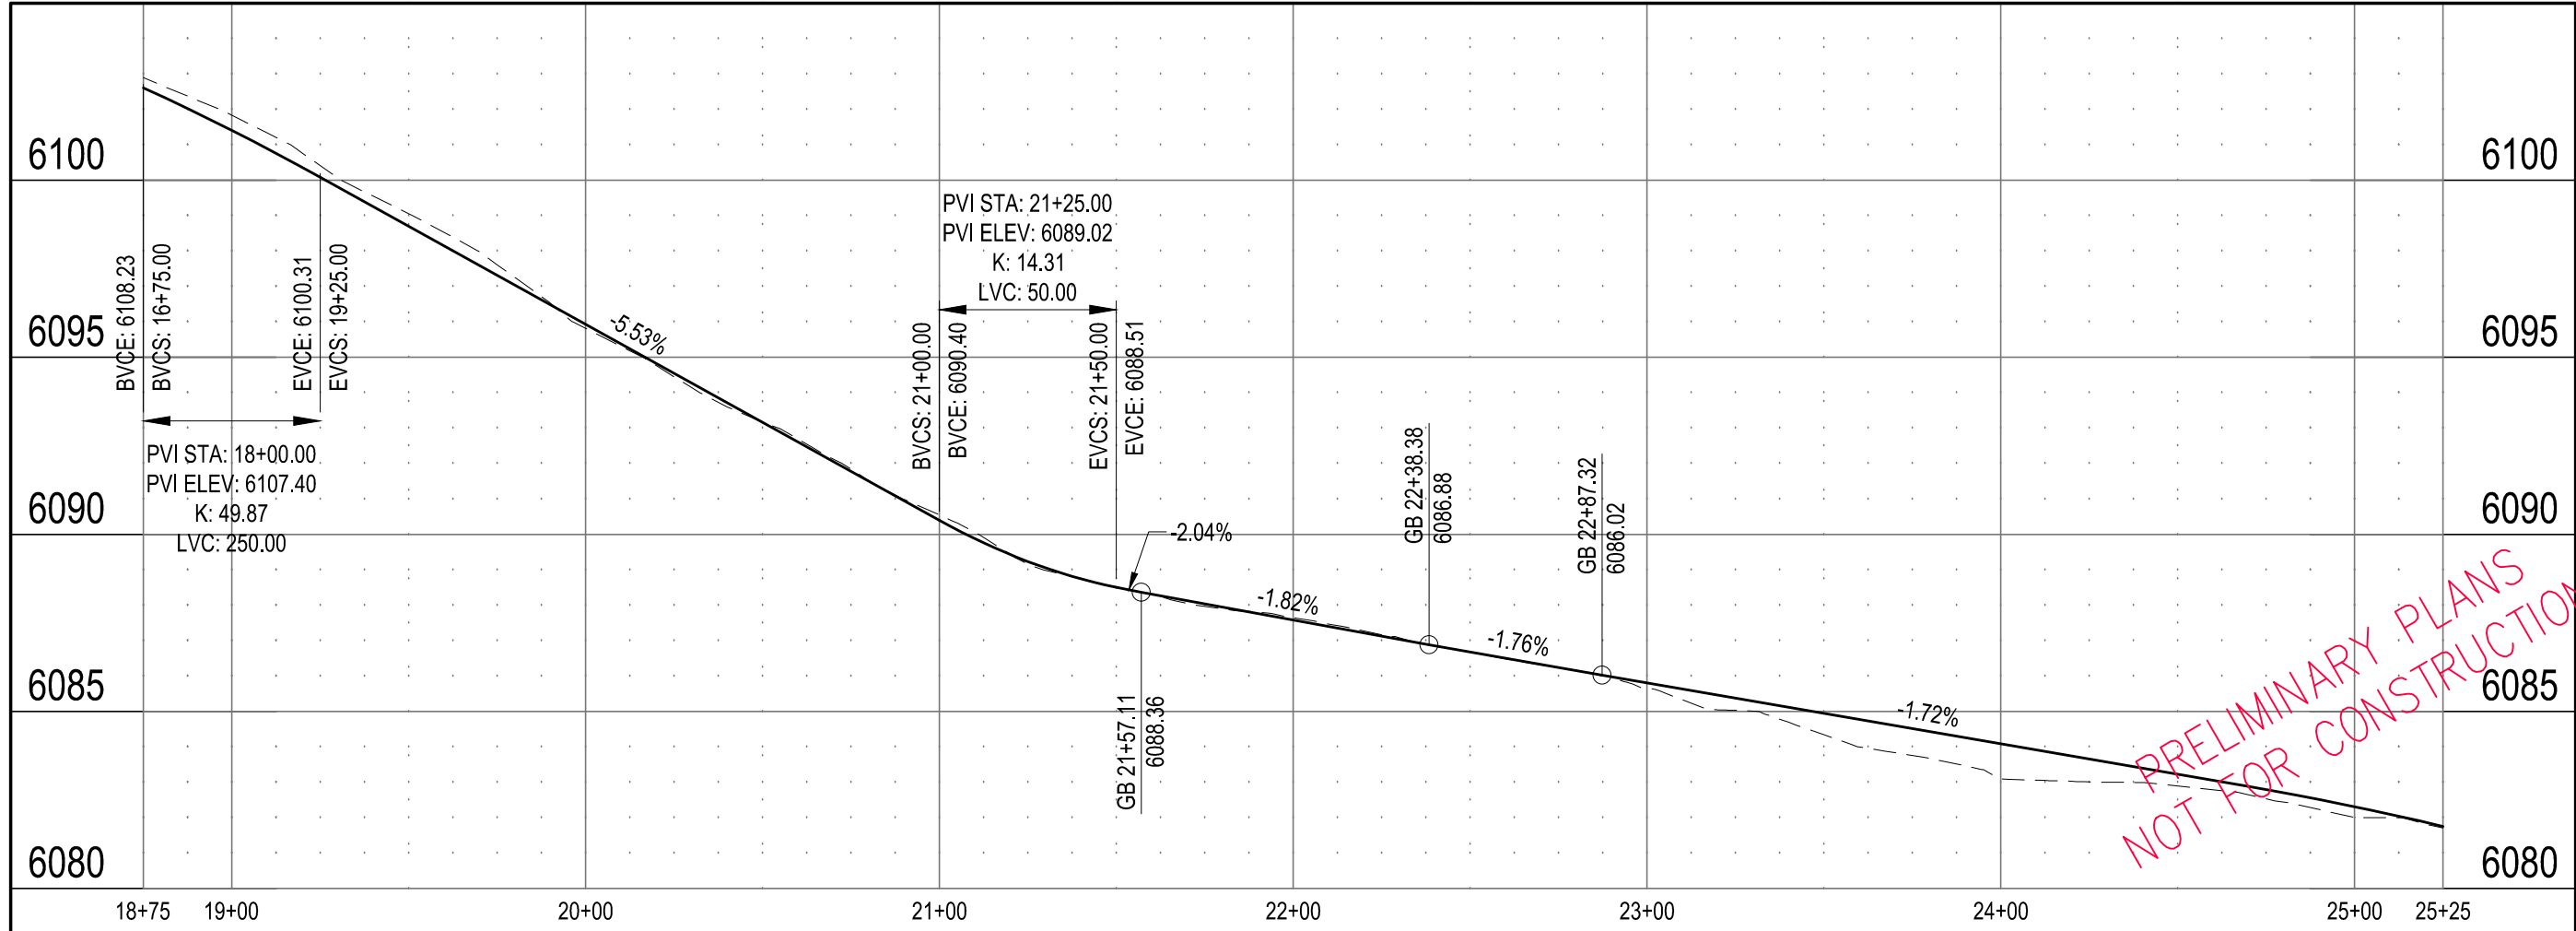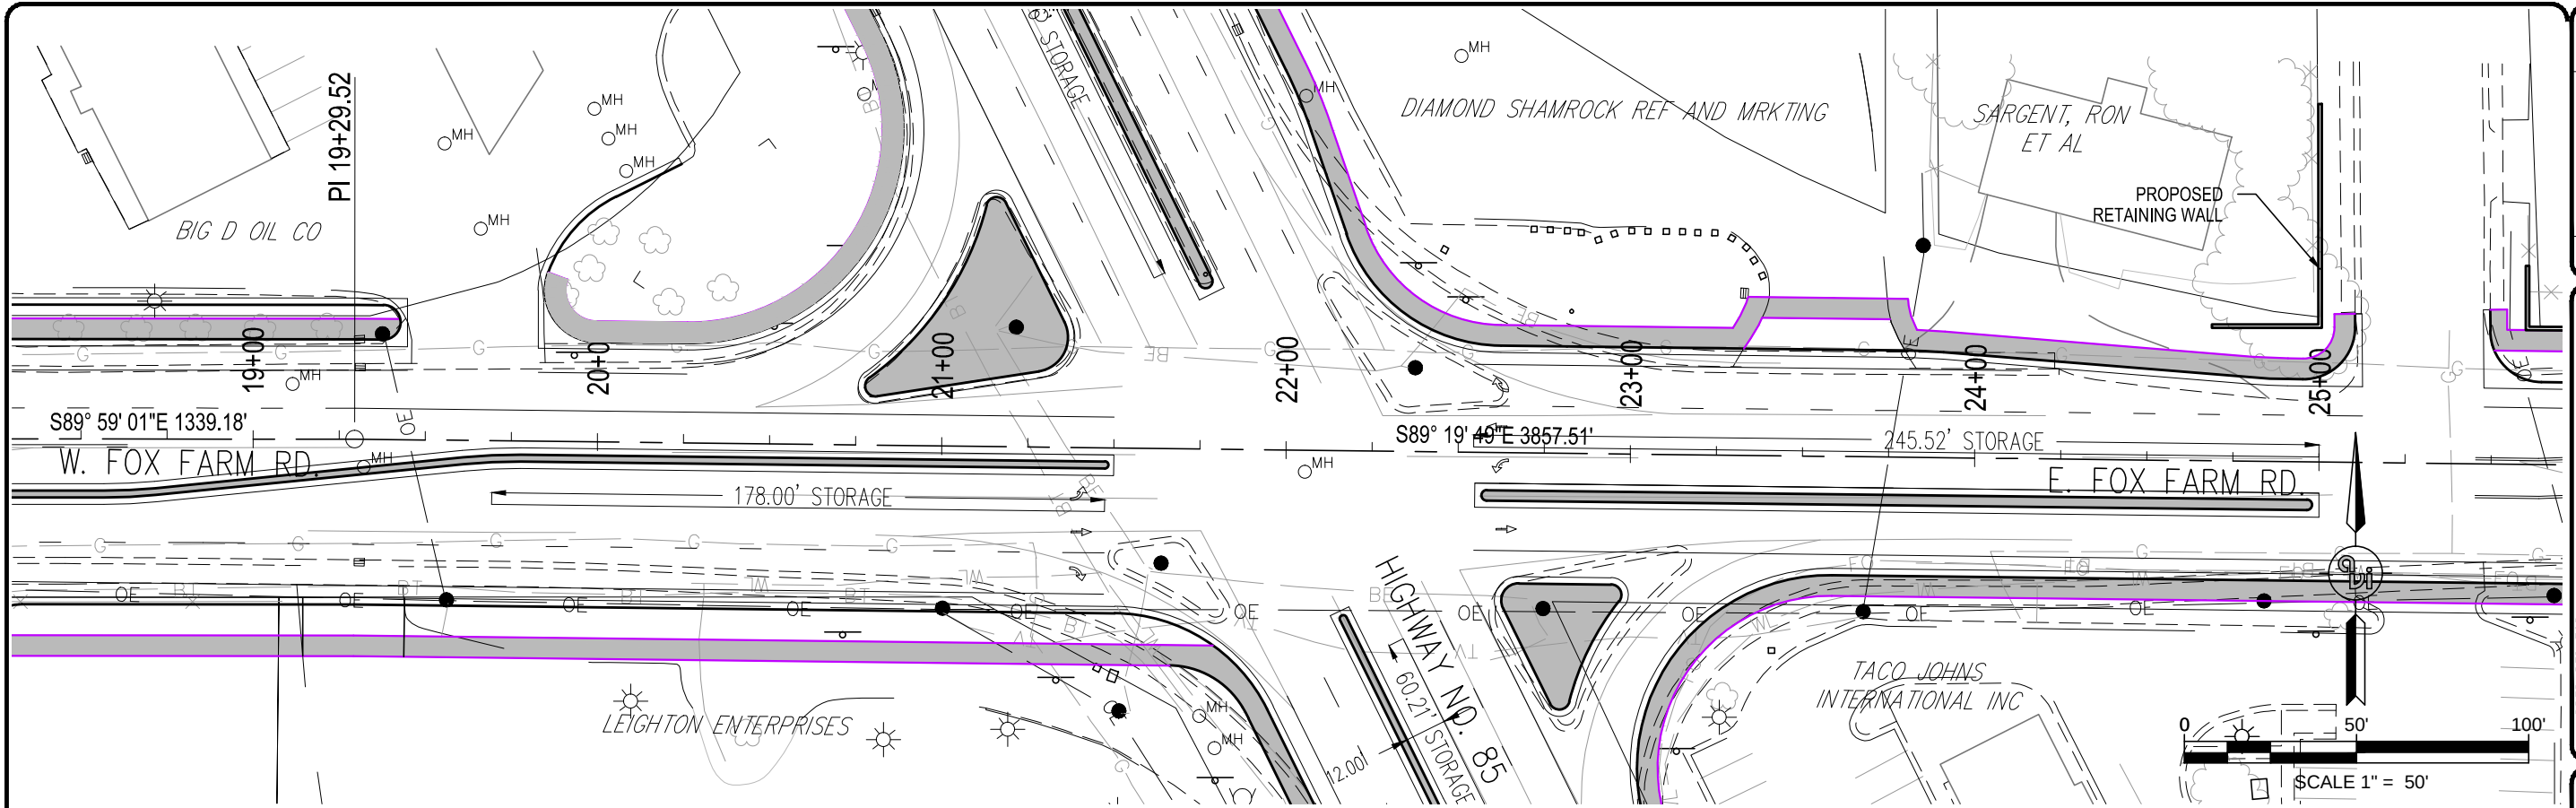

PRELIMINARY PLANS  
NOT FOR CONSTRUCTION

|          |  |
|----------|--|
| DATE     |  |
| REVISION |  |
| NO.      |  |

PREPARED FOR:  
MPO  
2101 ONEIL AVE.  
RM 205  
CHEYENNE, WY. 82001

PROJECT:  
FOX FARM ROAD STREET IMPROVEMENTS

DRAWING TITLE:  
FOX FARM RD. PLAN AND PROFILE  
STA. 18+75 - 25+25





**avi** p.c.  
engineering  
planning  
surveying  
PHONE (307) 637-6017  
1103 OLD TOWN LANE, SUITE 101  
CHEYENNE, WY 82009  
AVI@AVIIFC.COM

DATE:  
6-20-13  
DRAWN BY:  
SRL  
DESIGNED BY:  
TC  
CHECKED BY:  
TC

JOB NO.:  
2-3211-B

SHEET NO. 83 OF

H:\3211\design\3211B FOX FARM STREET IMP.dwg Aug 30, 2013 4:09pm jwilson

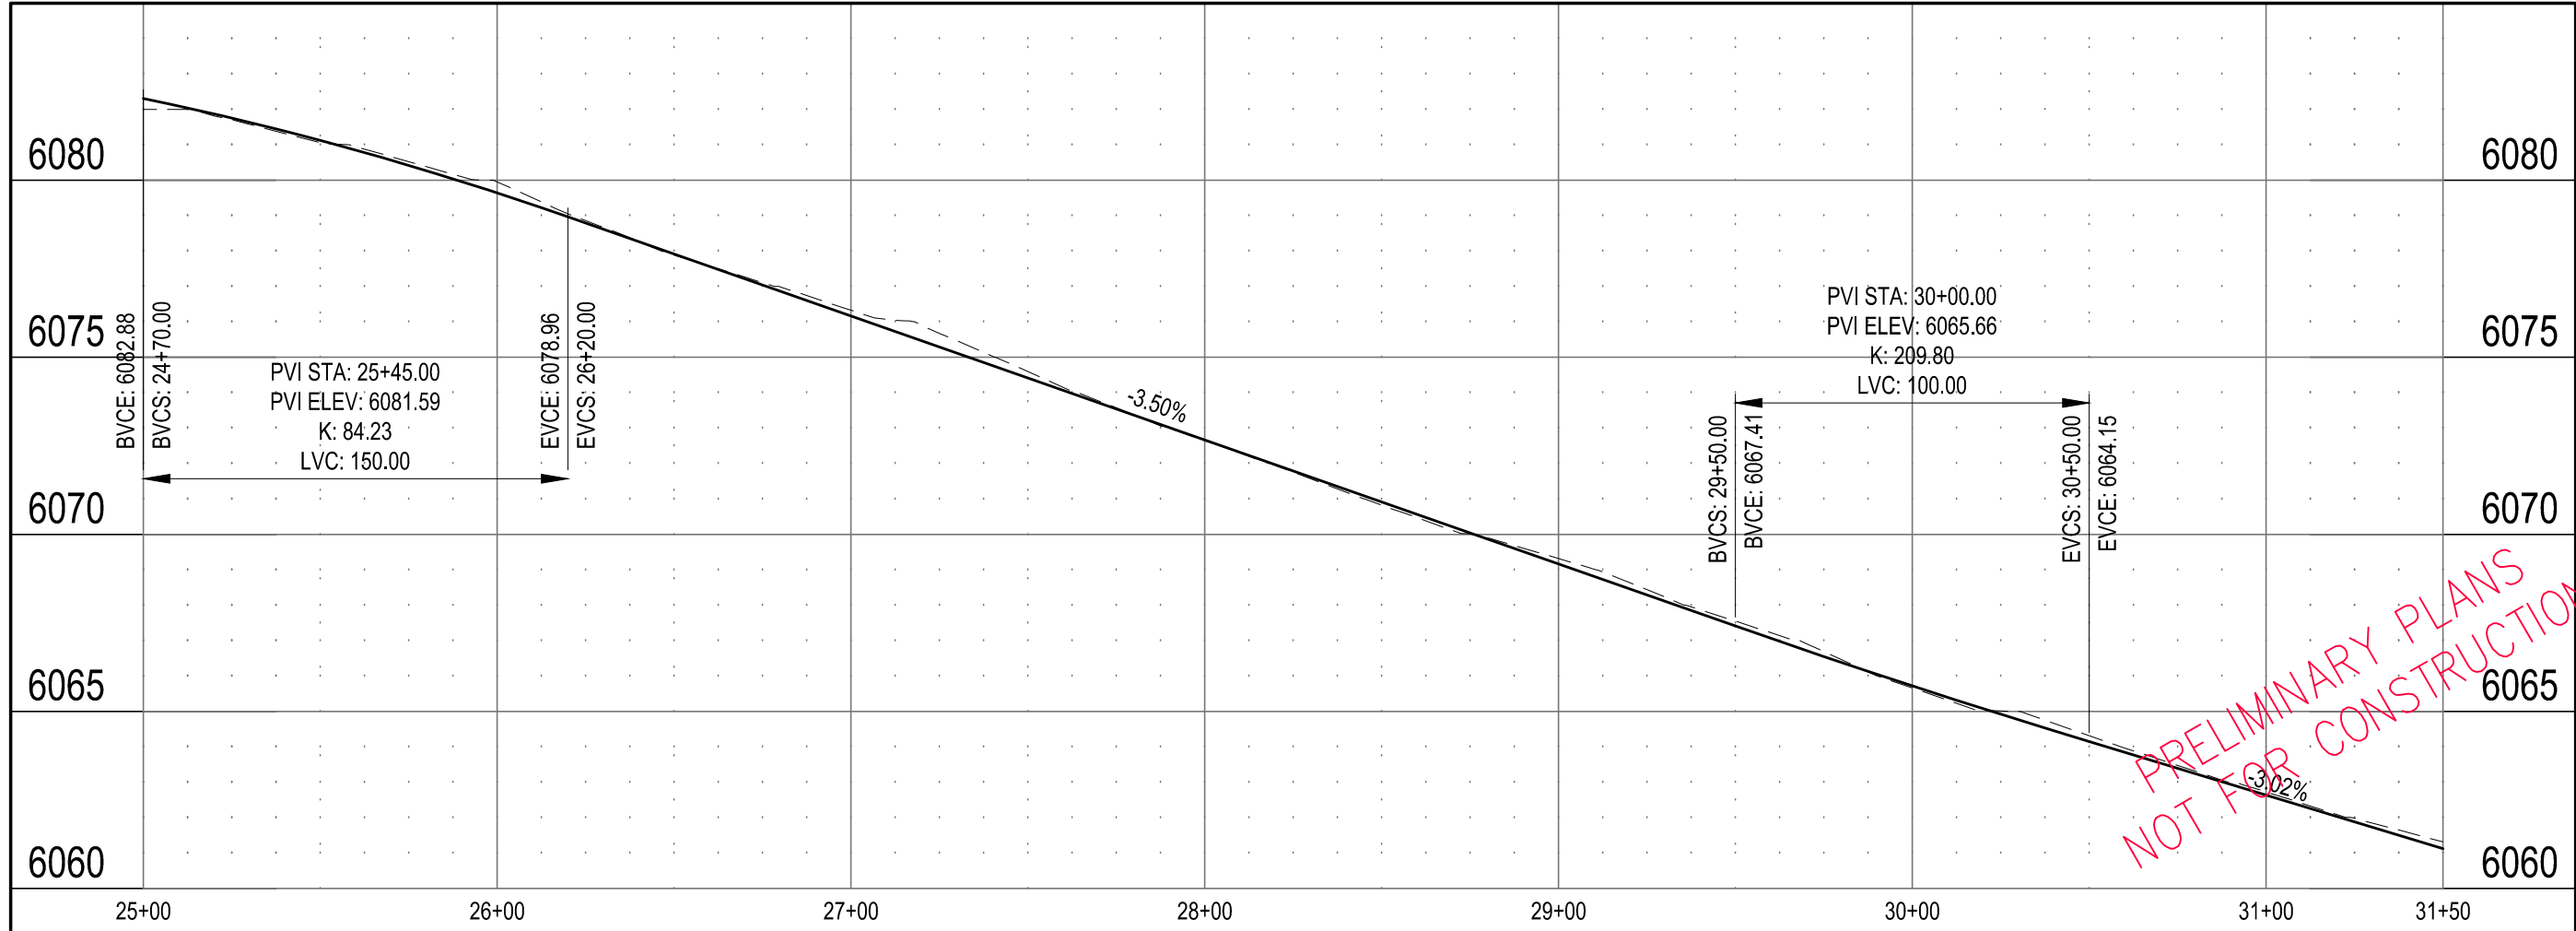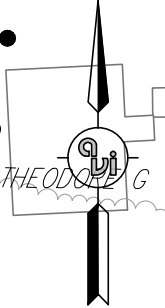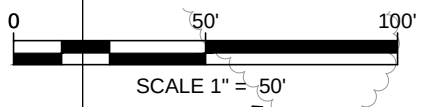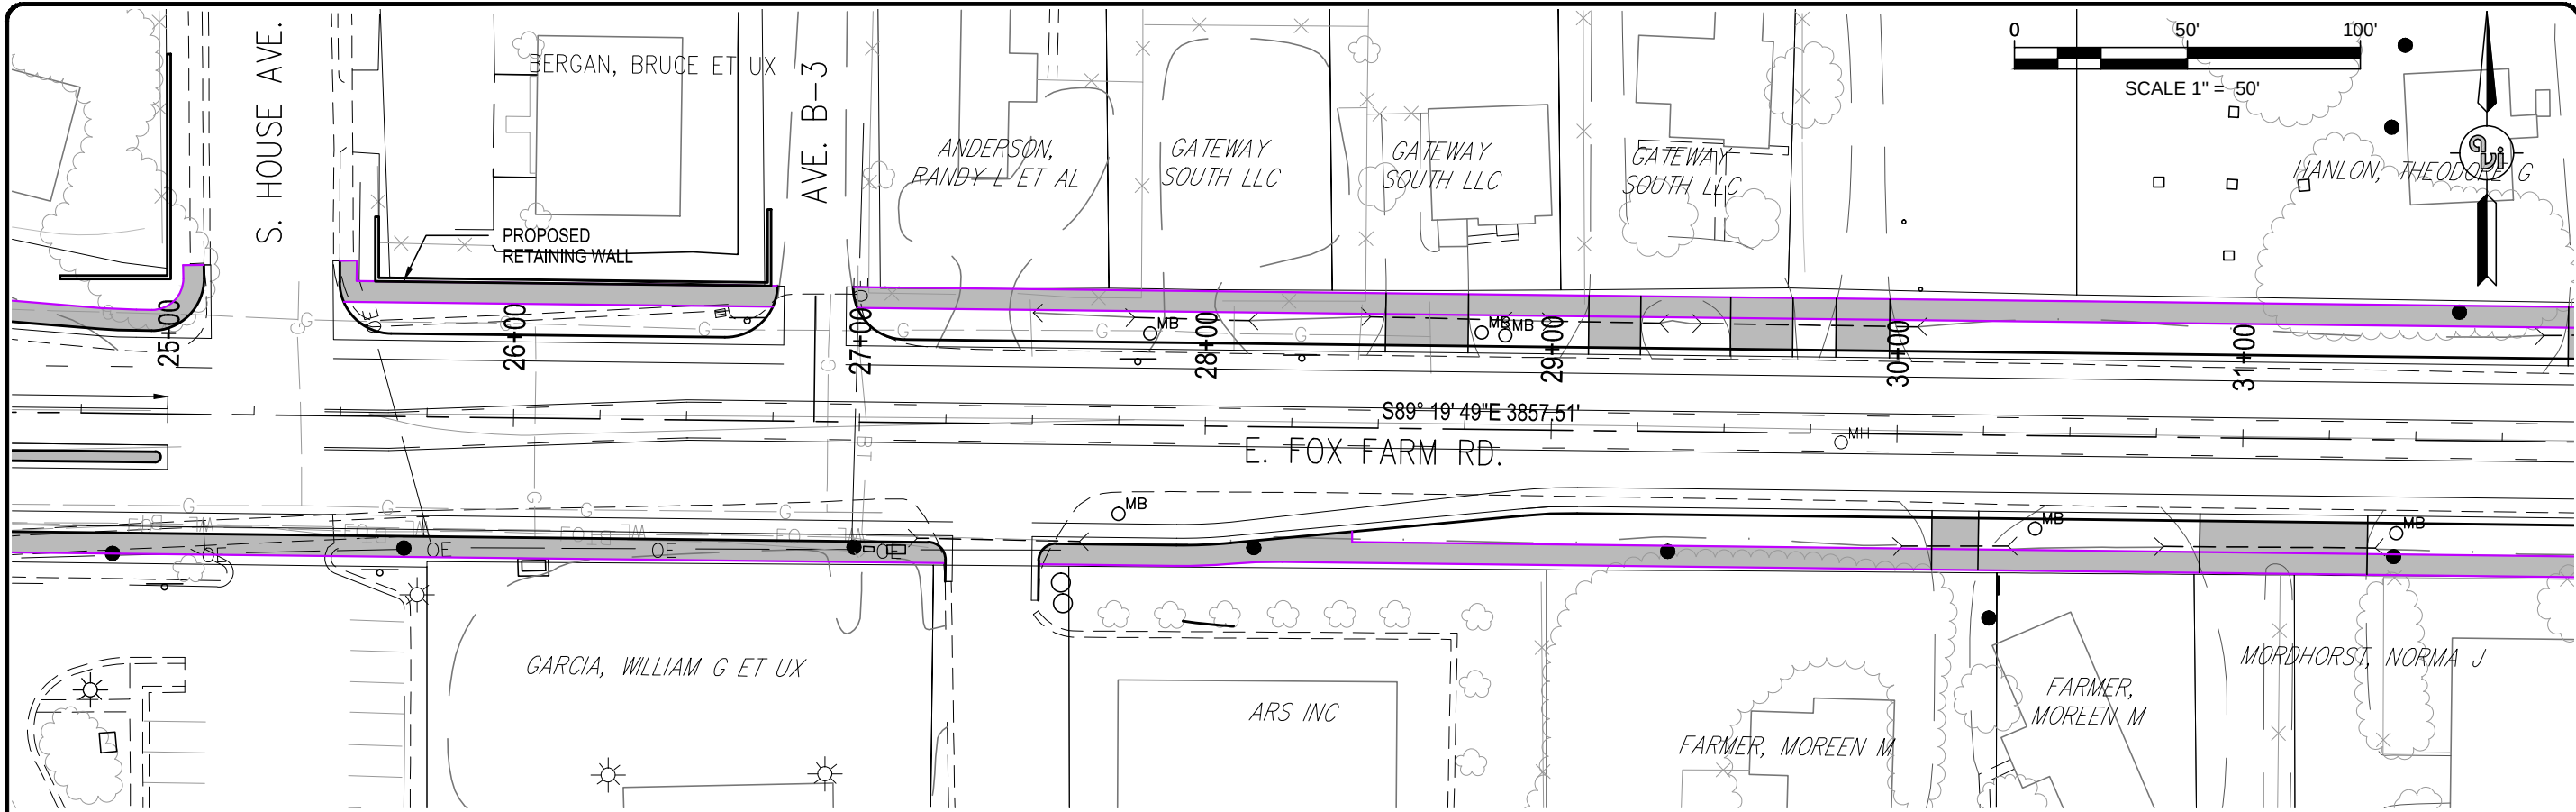

PRELIMINARY PLANS  
NOT FOR CONSTRUCTION

|     |          |      |
|-----|----------|------|
| NO. | REVISION | DATE |
|     |          |      |
|     |          |      |
|     |          |      |

|                |                                   |
|----------------|-----------------------------------|
| PROJECT:       | FOX FARM ROAD STREET IMPROVEMENTS |
| DRAWING TITLE: | FOX FARM RD. PLAN AND PROFILE     |
| STA.           | 25+00 - 31+50                     |

|               |                                                         |
|---------------|---------------------------------------------------------|
| PREPARED FOR: | MPO<br>2101 ONEIL AVE.<br>RM 205<br>CHEYENNE, WY. 82001 |
|---------------|---------------------------------------------------------|

|              |         |
|--------------|---------|
| DATE:        | 6-20-13 |
| DRAWN BY:    | SRL     |
| DESIGNED BY: | TC      |
| CHECKED BY:  | TC      |




  

|          |          |
|----------|----------|
| JOB NO.: | 2-3211-B |
|----------|----------|

|           |    |
|-----------|----|
| ST-05     | 83 |
| SHEET NO. | OF |

H:\3211\design\3211B FOX FARM STREET IMP.dwg Aug 30, 2013 4:09pm jwilson

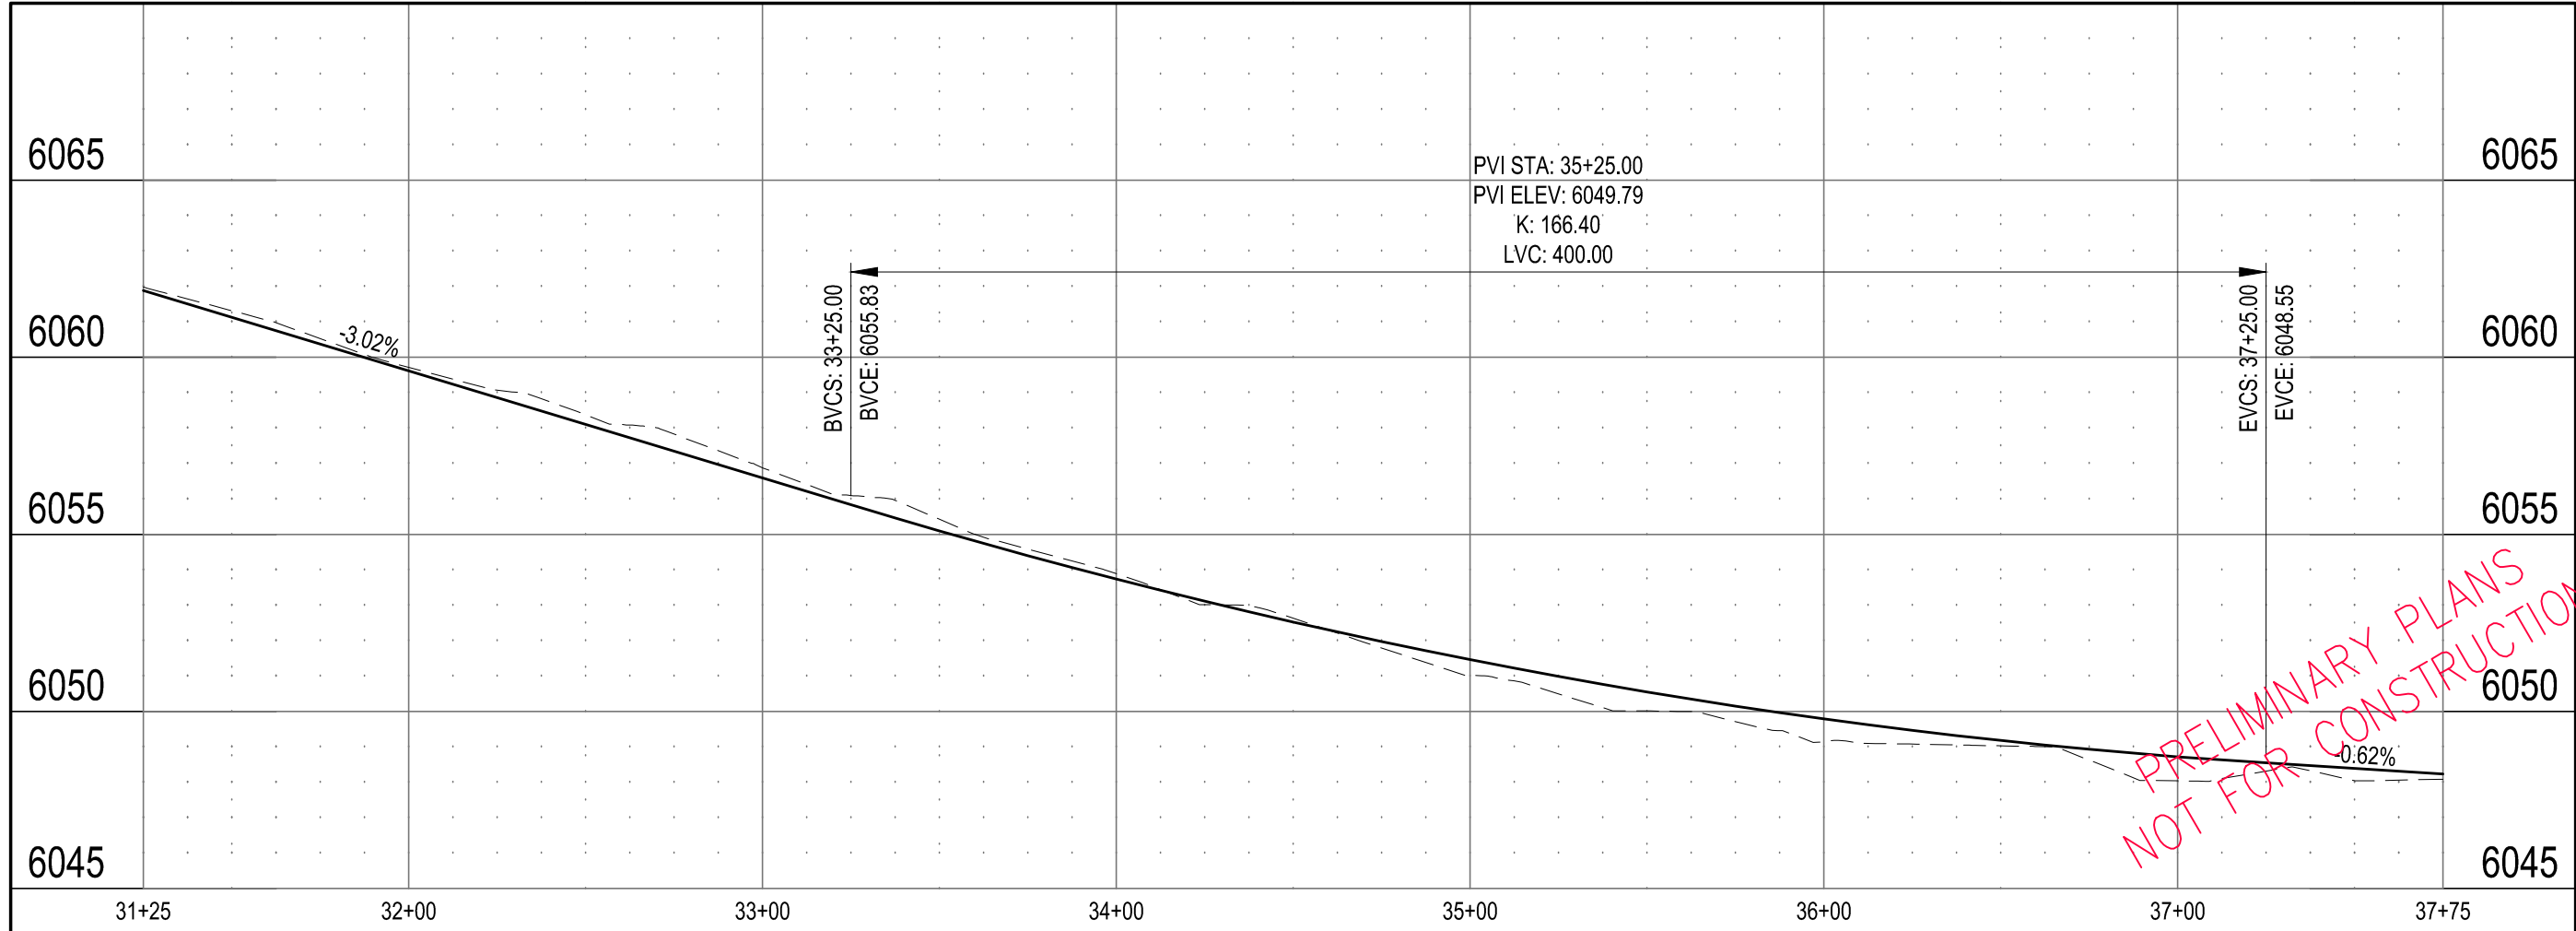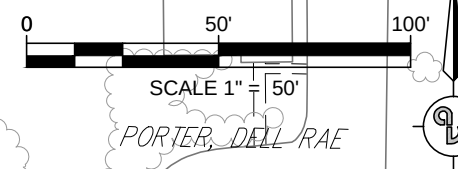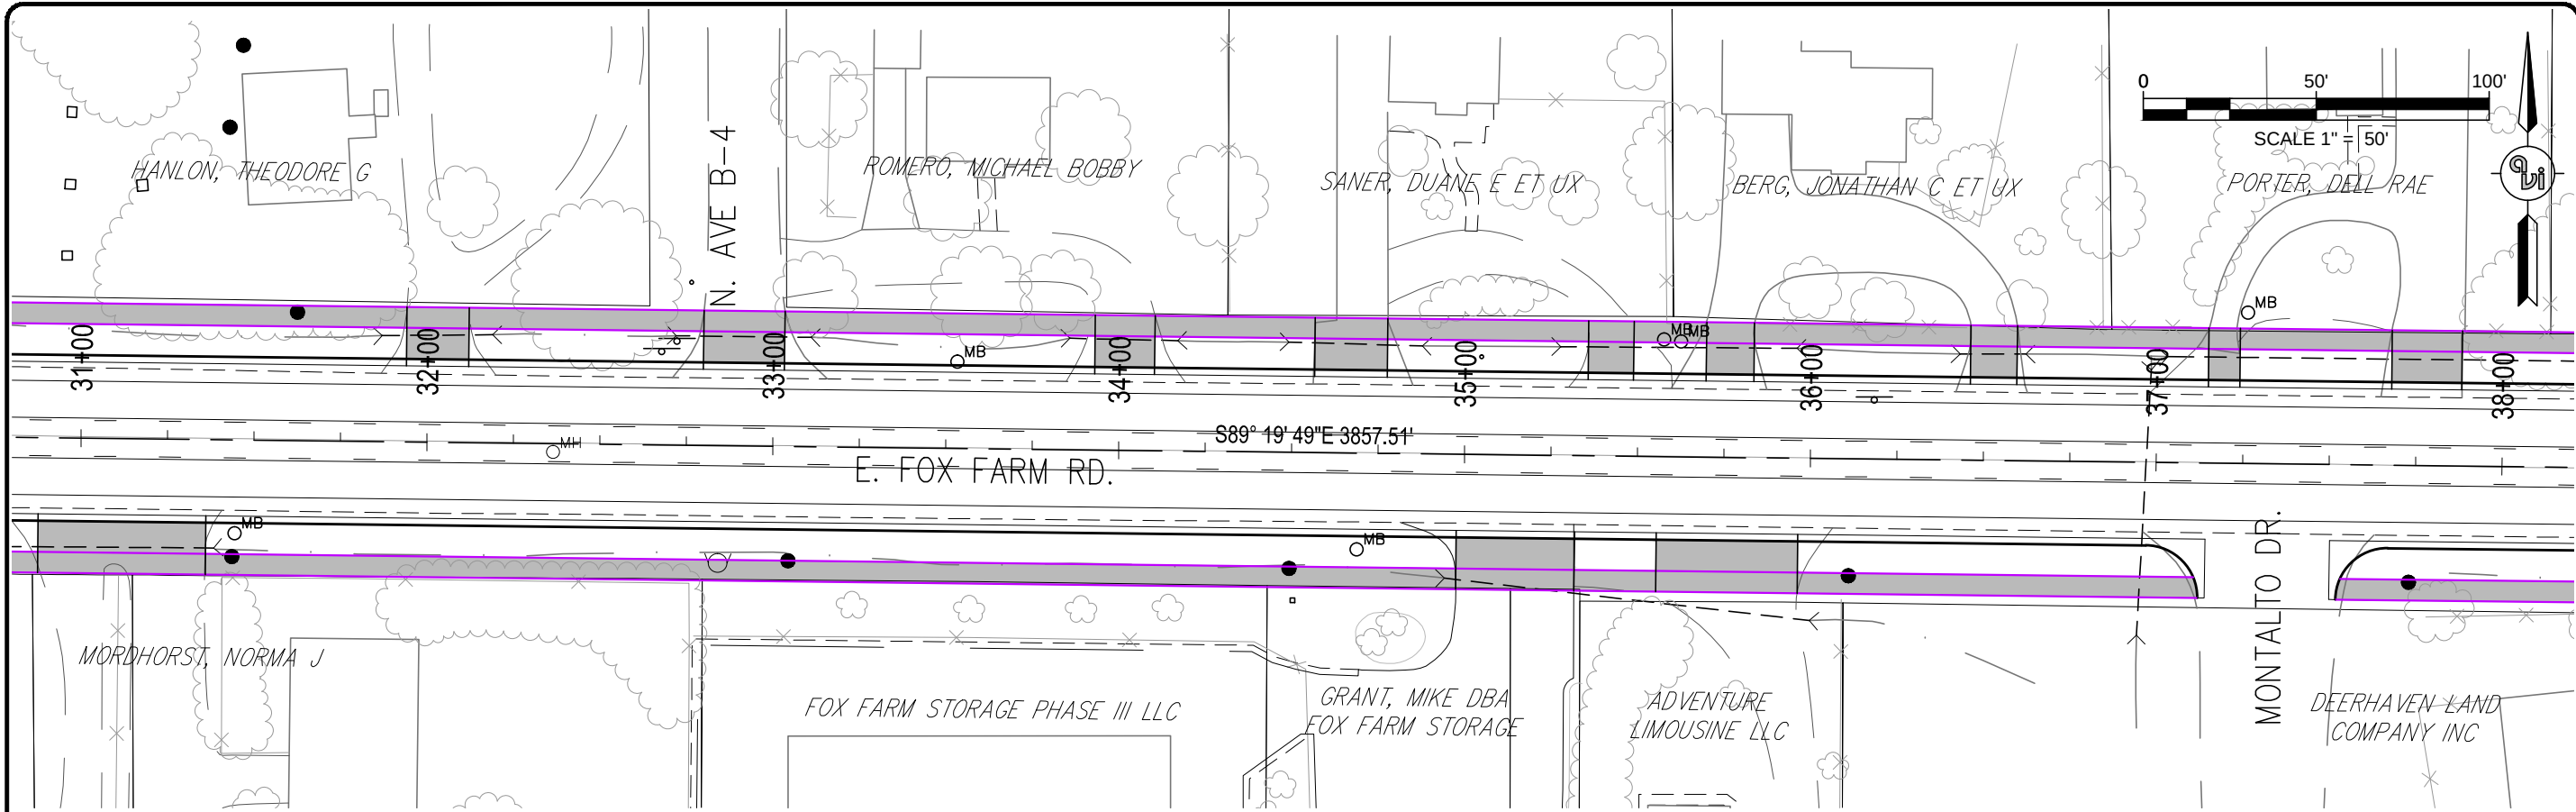

PRELIMINARY PLANS  
NOT FOR CONSTRUCTION

| NO. | REVISION | DATE |
|-----|----------|------|
|     |          |      |
|     |          |      |
|     |          |      |
|     |          |      |

PREPARED FOR:  
MPO  
2101 ONEIL AVE.  
RM 205  
CHEYENNE, WY. 82001

PROJECT: FOX FARM ROAD STREET IMPROVEMENTS  
DRAWING TITLE: FOX FARM RD. PLAN AND PROFILE  
STA. 31+25 - 37+75



**avi** p.c.  
engineering  
planning  
surveying  
PHONE (307) 637-6017  
1103 OLD TOWN LANE, SUITE 101  
CHEYENNE, WY 82009  
AVI@AVIPC.COM

DATE: 6-20-13  
DRAWN BY: SRL  
DESIGNED BY: TC  
CHECKED BY: TC

JOB NO.: 2-3211-B

ST-06 83  
SHEET NO. OF

H:\3211\design\3211B FOX FARM STREET IMP.dwg Aug 30, 2013 4:10pm jwilson

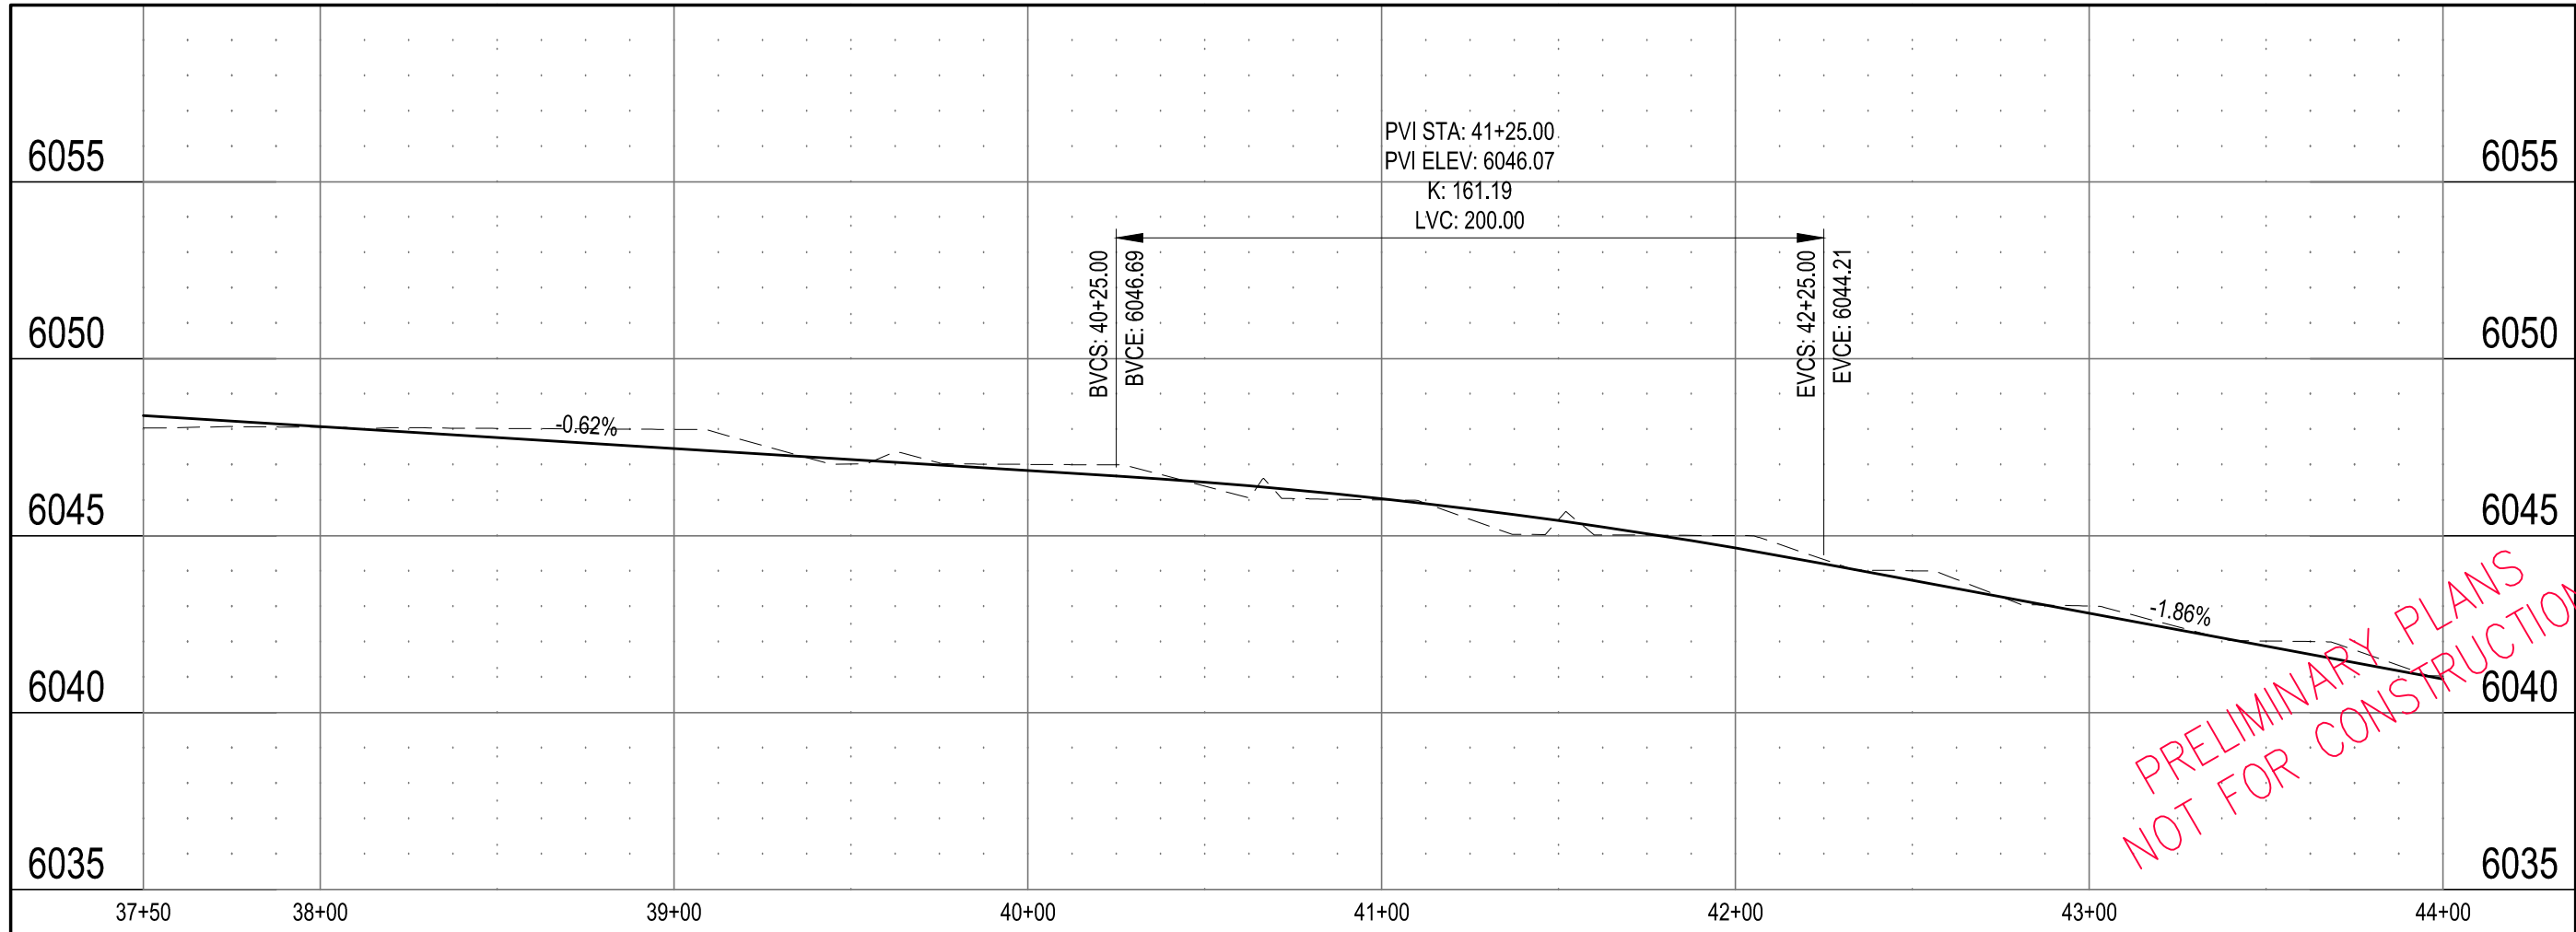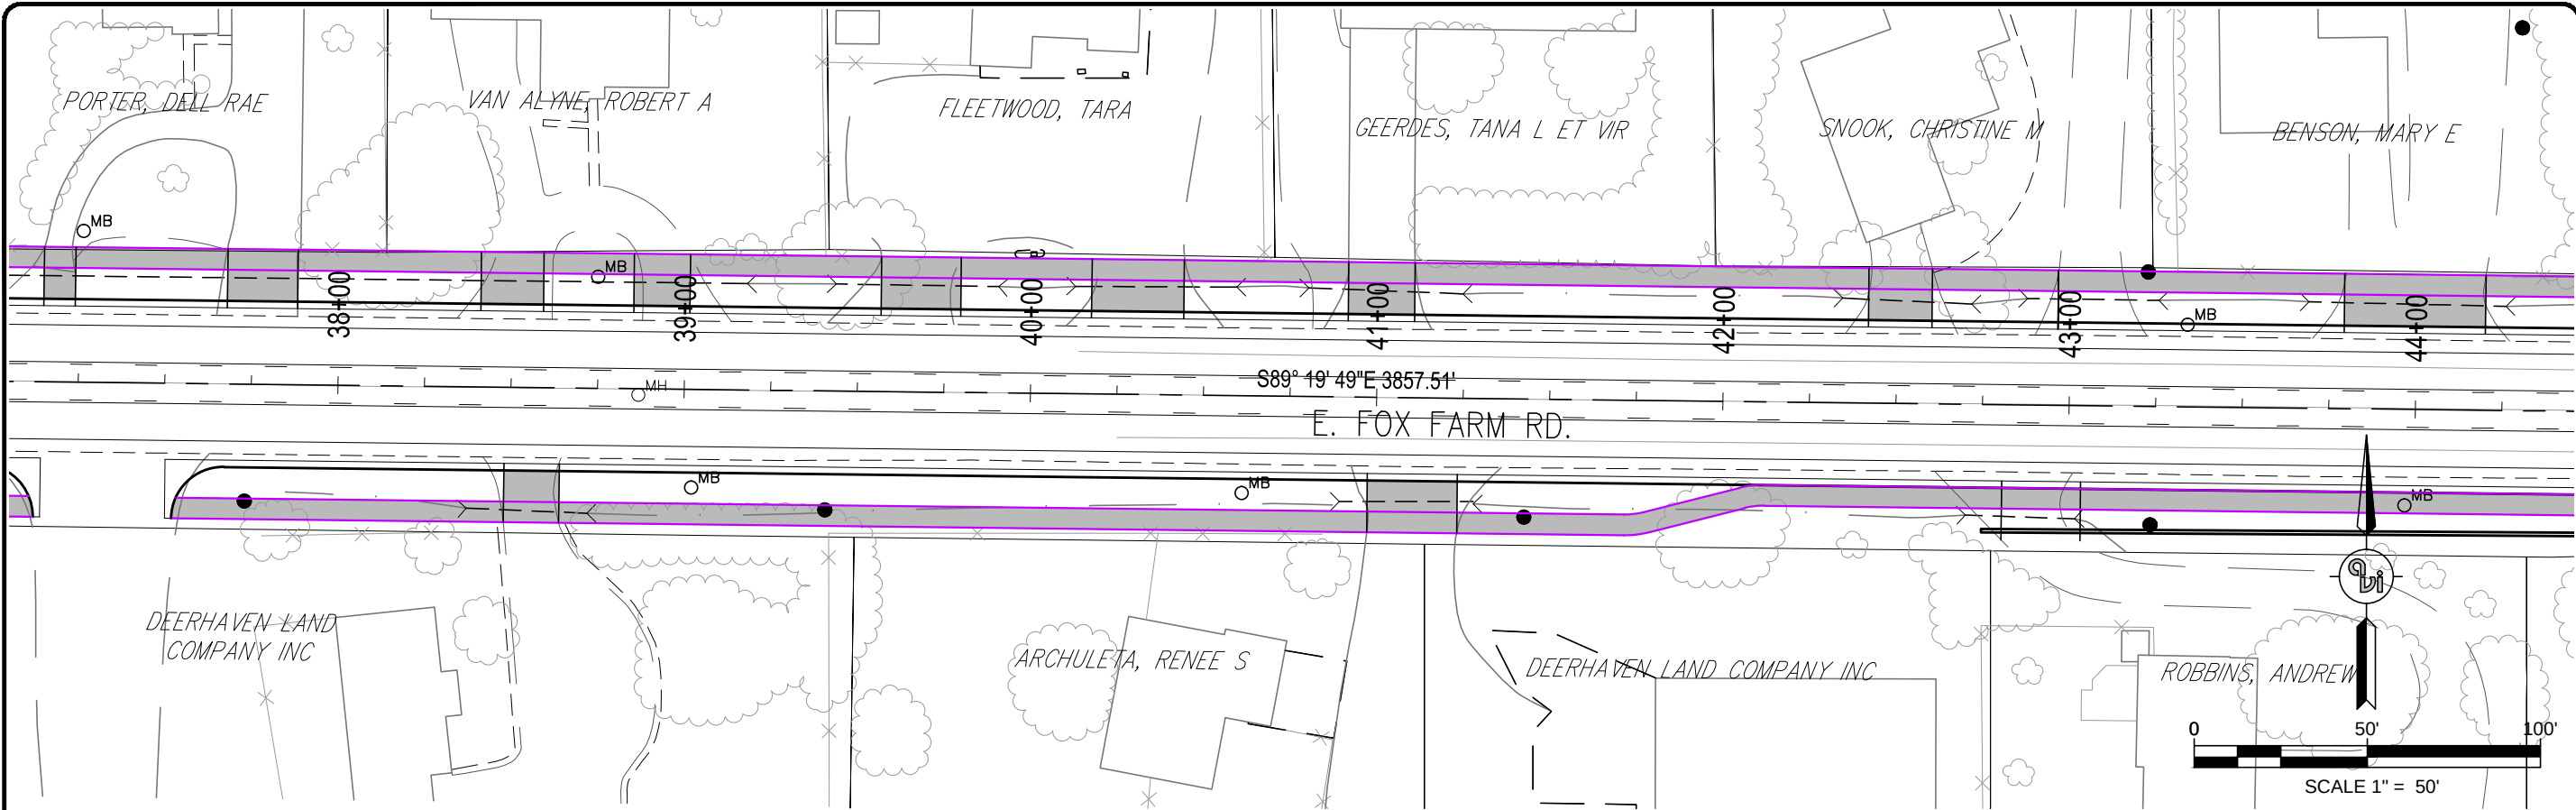

| NO. | REVISION | DATE |
|-----|----------|------|
|     |          |      |
|     |          |      |
|     |          |      |

PREPARED FOR:  
MPO  
2101 ONEIL AVE.  
RM 205  
CHEYENNE, WY. 82001

PROJECT:  
FOX FARM ROAD STREET  
IMPROVEMENTS

DRAWING TITLE:  
FOX FARM RD. PLAN AND PROFILE  
STA. 37+50 - 44+00



**avi** p.c.  
engineering  
planning  
surveying  
PHONE (307) 637-6017  
1103 OLD TOWN LANE, SUITE 101  
CHEYENNE, WY 82009  
AVI@AVIPC.COM

DATE:  
6-20-13  
DRAWN BY:  
SRL  
DESIGNED BY:  
TC  
CHECKED BY:  
TC

JOB NO.:  
2-3211-B

ST-07 83  
SHEET NO. OF

H:\3211\design\3211B FOX FARM STREET IMP.dwg Aug 30, 2013 4:10pm jwilson

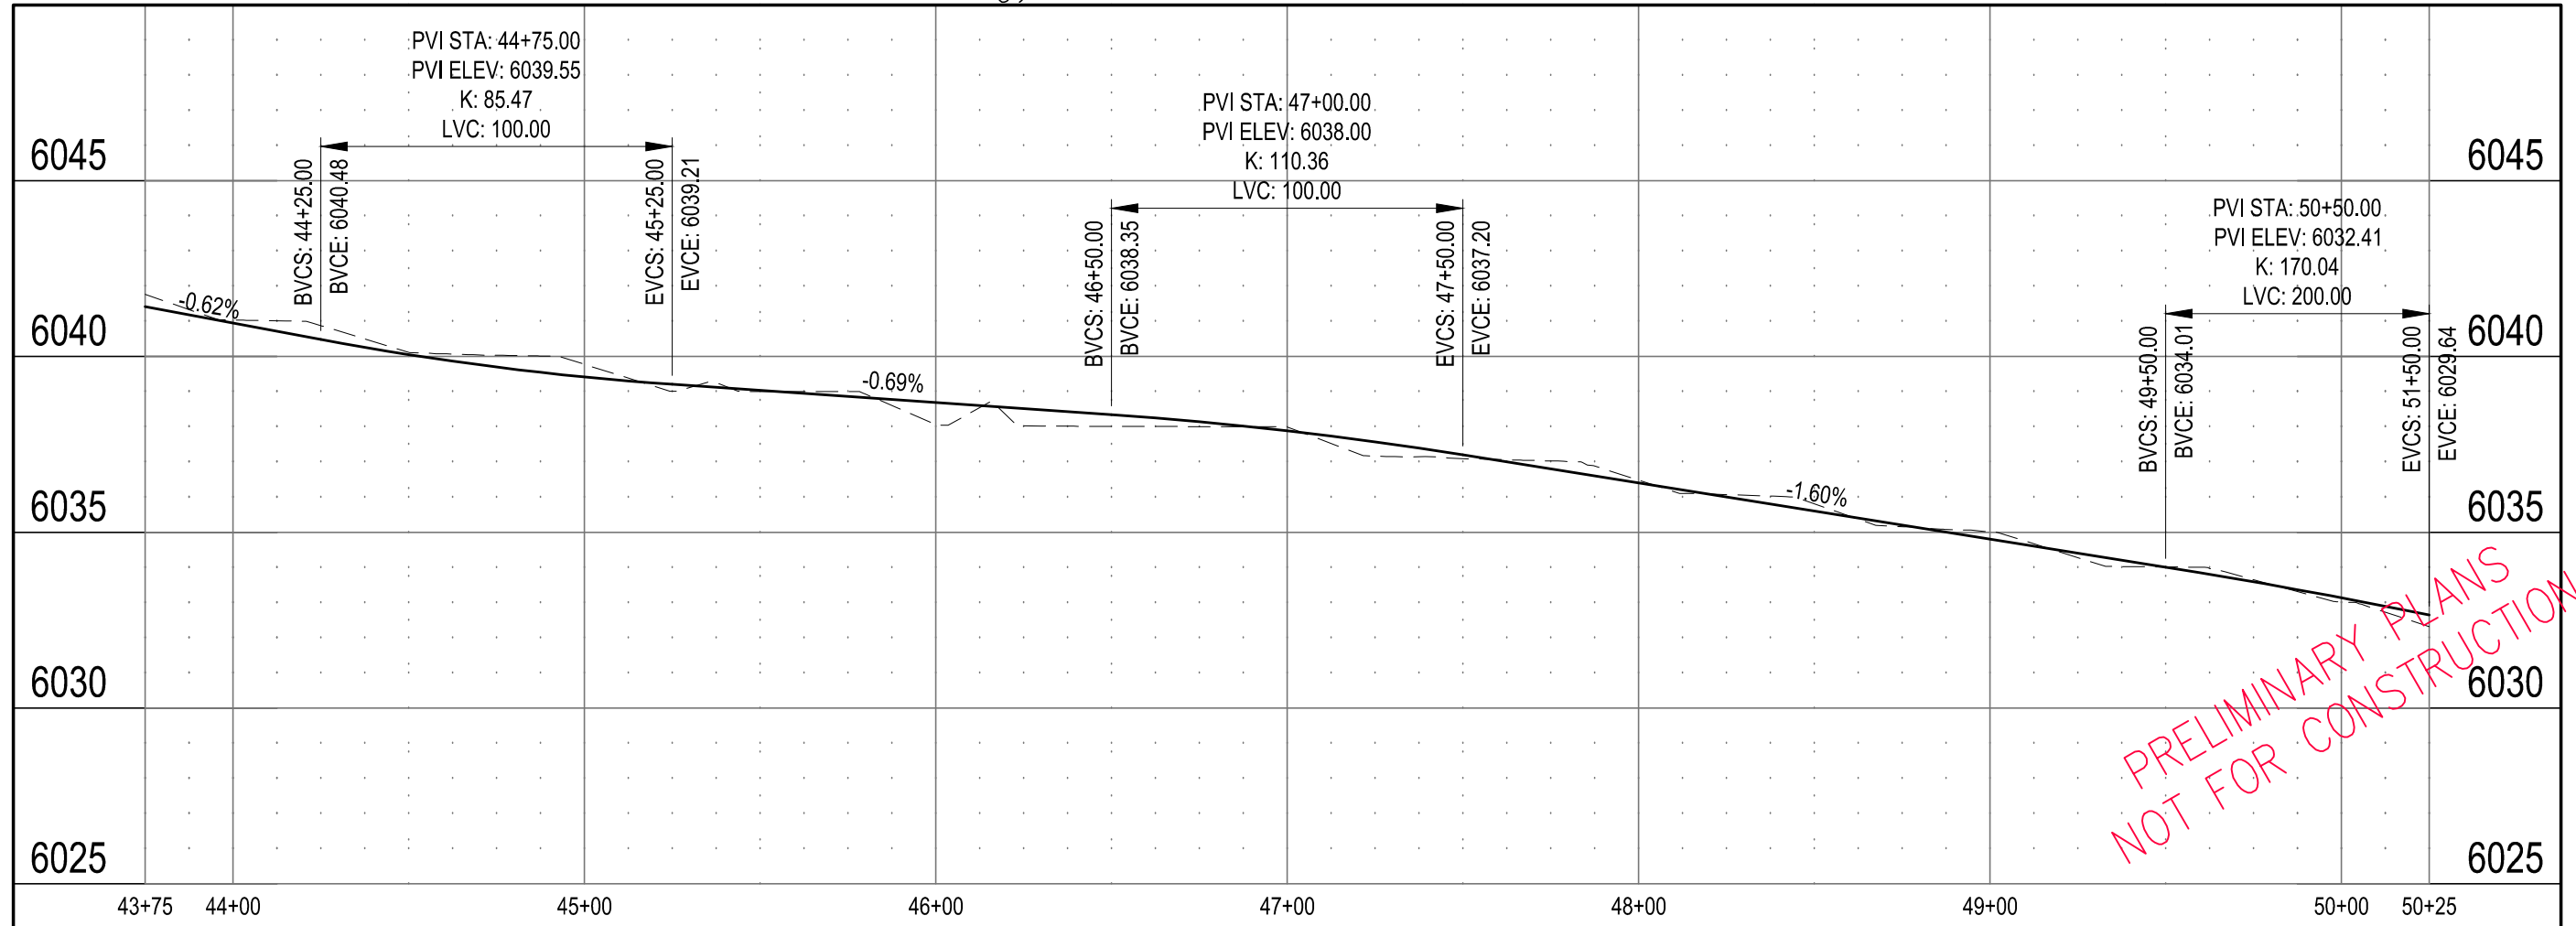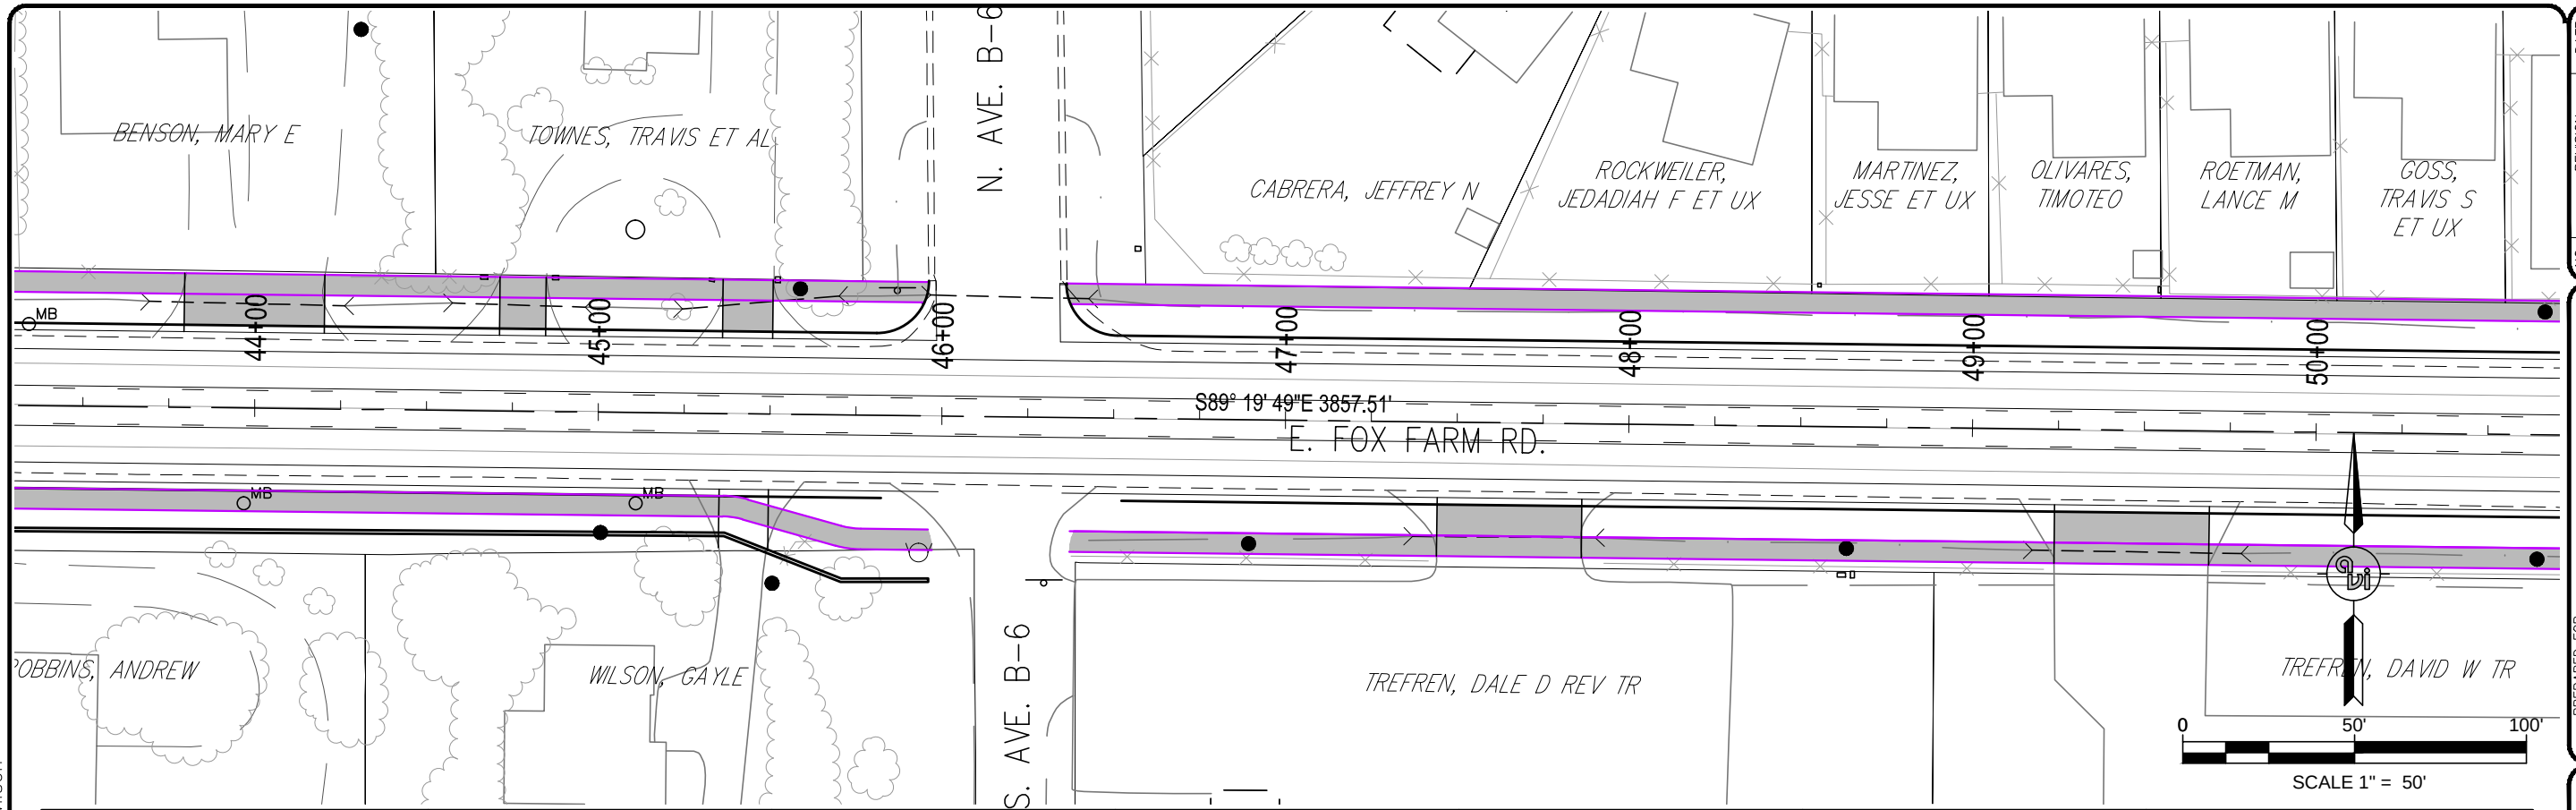

| NO. | REVISION | DATE |
|-----|----------|------|
|     |          |      |
|     |          |      |
|     |          |      |

PREPARED FOR:  
MPO  
2101 O'NEIL AVE.  
RM 205  
CHEYENNE, WY. 82001

PROJECT:  
FOX FARM ROAD STREET IMPROVEMENTS

DRAWING TITLE:  
FOX FARM RD. PLAN AND PROFILE  
STA. 43+75 - 50+25



engineering planning surveying  
avi p.c.  
PHONE (307) 637-6017  
1103 OLD TOWN LANE, SUITE 101  
CHEYENNE, WY 82009  
AVI@AVIFPC.COM

DATE:  
6-20-13  
DRAWN BY:  
SRL  
DESIGNED BY:  
TC  
CHECKED BY:  
TC

JOB NO.:  
2-3211-B

ST-08 83  
SHEET NO. OF

H:\3211\design\3211B FOX FARM STREET IMP.dwg Aug 30, 2013 4:10pm jwilson

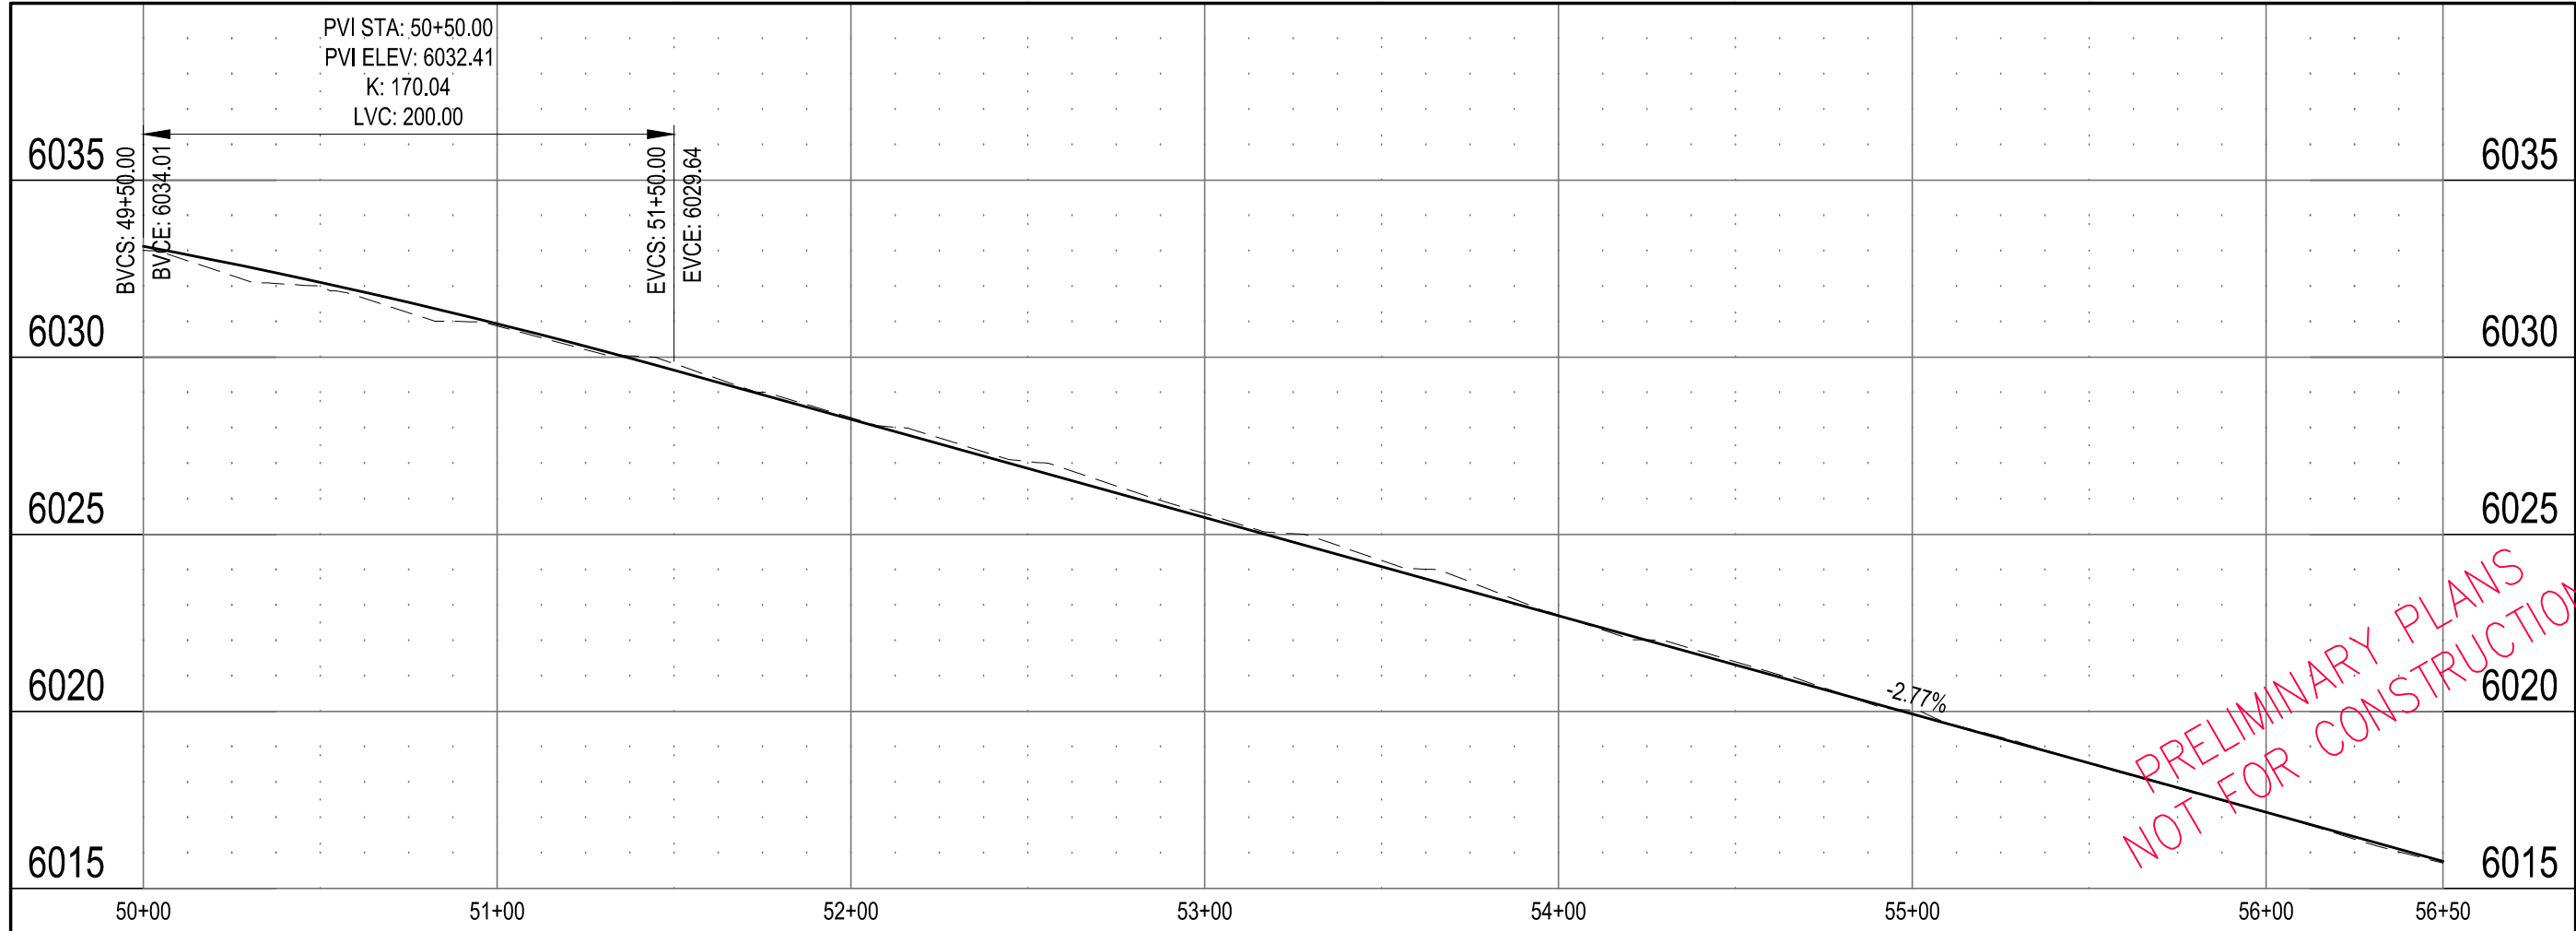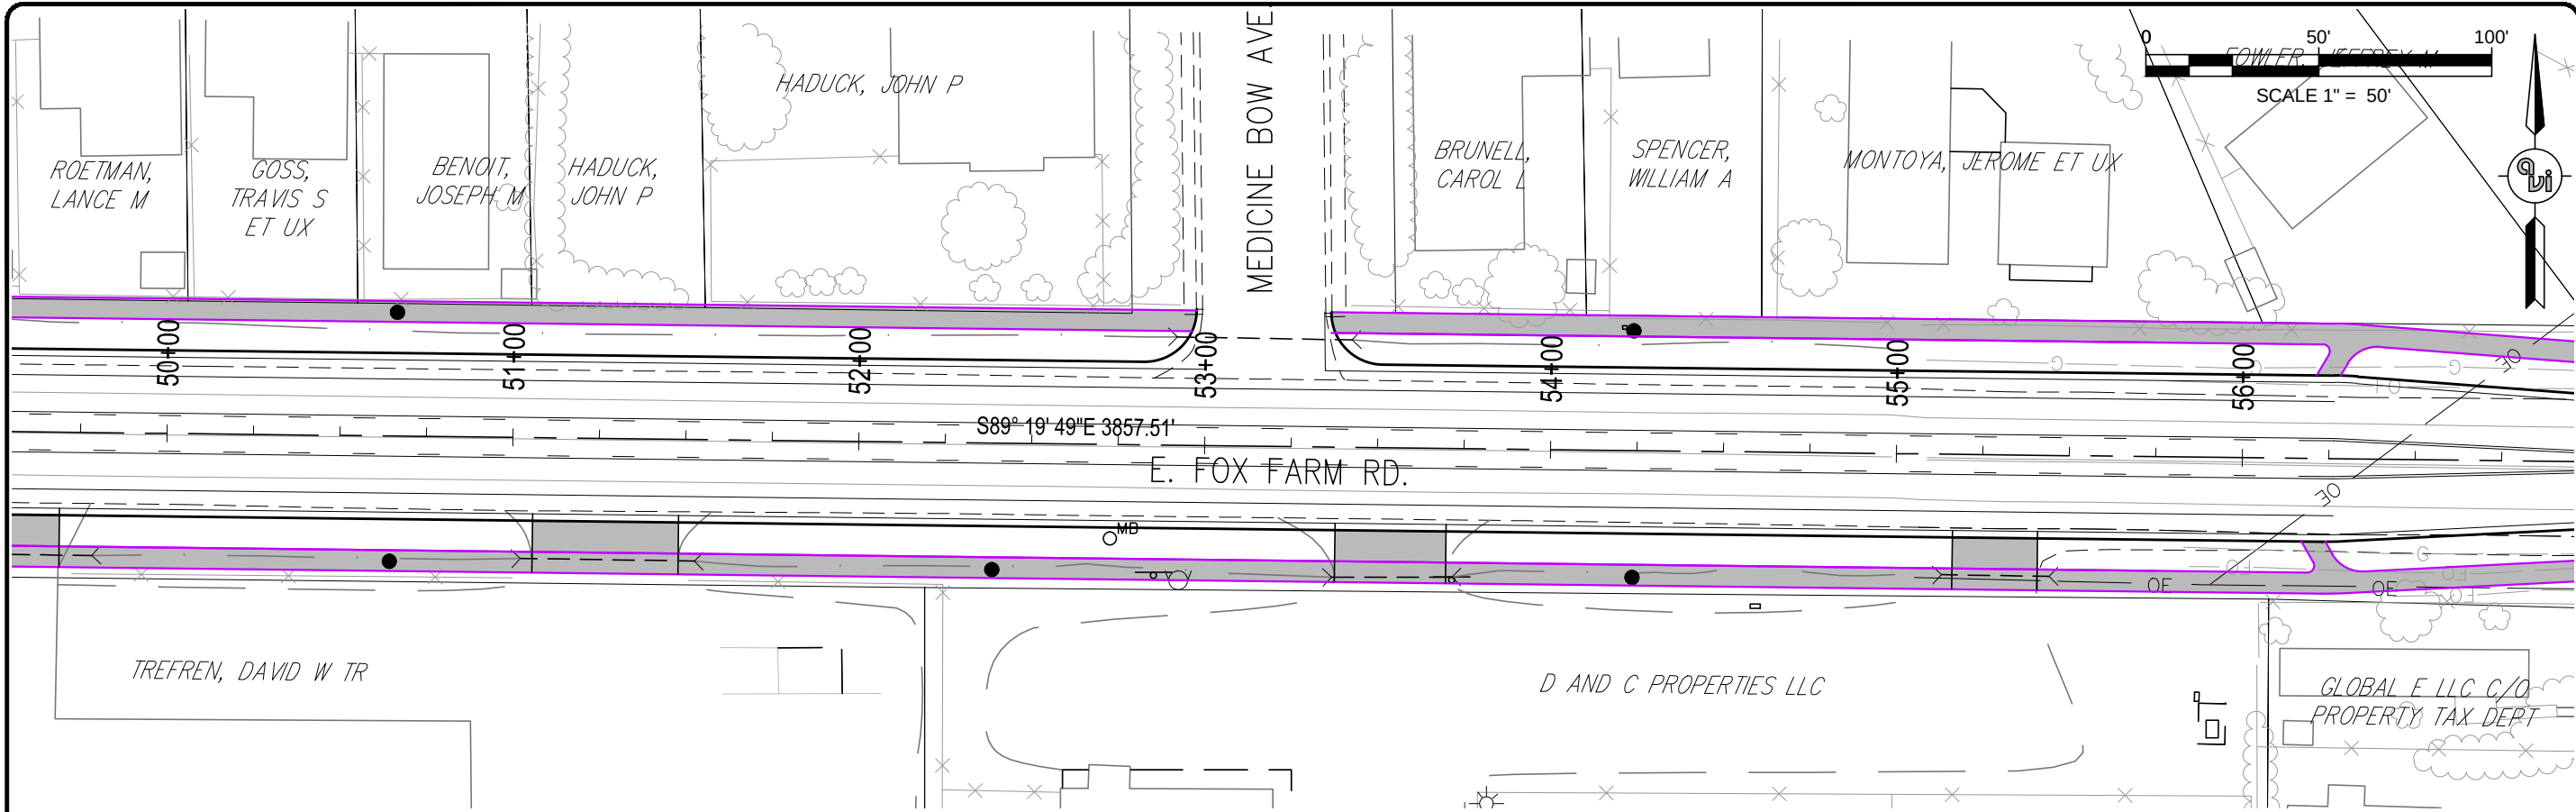

PRELIMINARY PLANS  
NOT FOR CONSTRUCTION

|          |  |
|----------|--|
| DATE     |  |
| REVISION |  |
| NO.      |  |

PREPARED FOR:  
MPO  
2101 ONEIL AVE.  
RM 205  
CHEYENNE, WY. 82001

PROJECT:  
FOX FARM ROAD STREET  
IMPROVEMENTS

DRAWING TITLE:  
FOX FARM RD. PLAN AND PROFILE  
STA. 50+00 - 56+50



**avi** p.c.  
engineering  
planning  
surveying  
PHONE (307) 637-6017  
1103 OLD TOWN LANE, SUITE 101  
CHEYENNE, WY 82009  
AVI@AVIPC.COM

DATE:  
6-20-13  
DRAWN BY:  
SRL  
DESIGNED BY:  
TC  
CHECKED BY:  
TC

JOB NO.:  
2-3211-B

ST-09 83  
SHEET NO. OF

H:\3211\design\3211B FOX FARM STREET IMP.dwg Aug 30, 2013 4:11pm jwilson

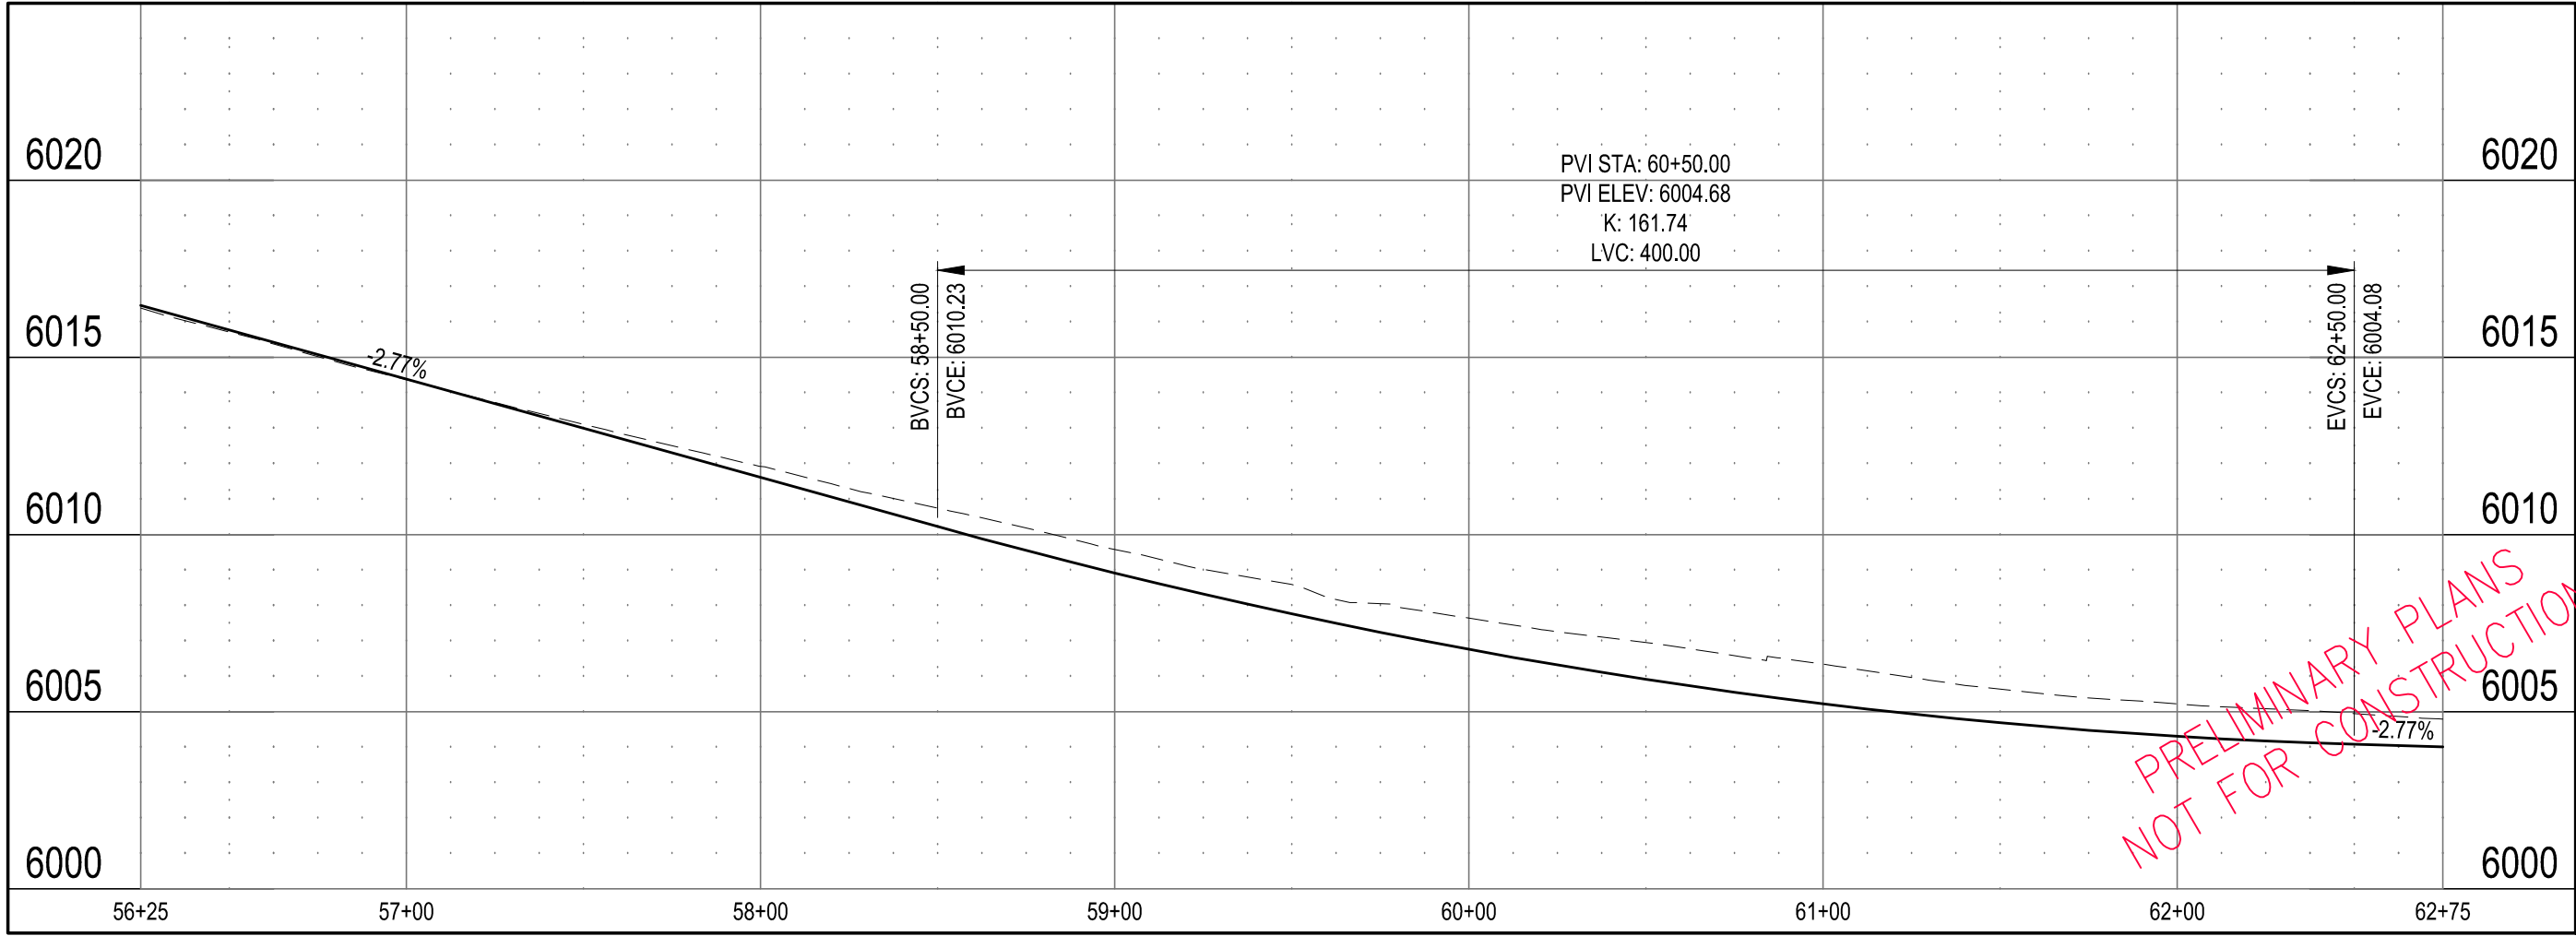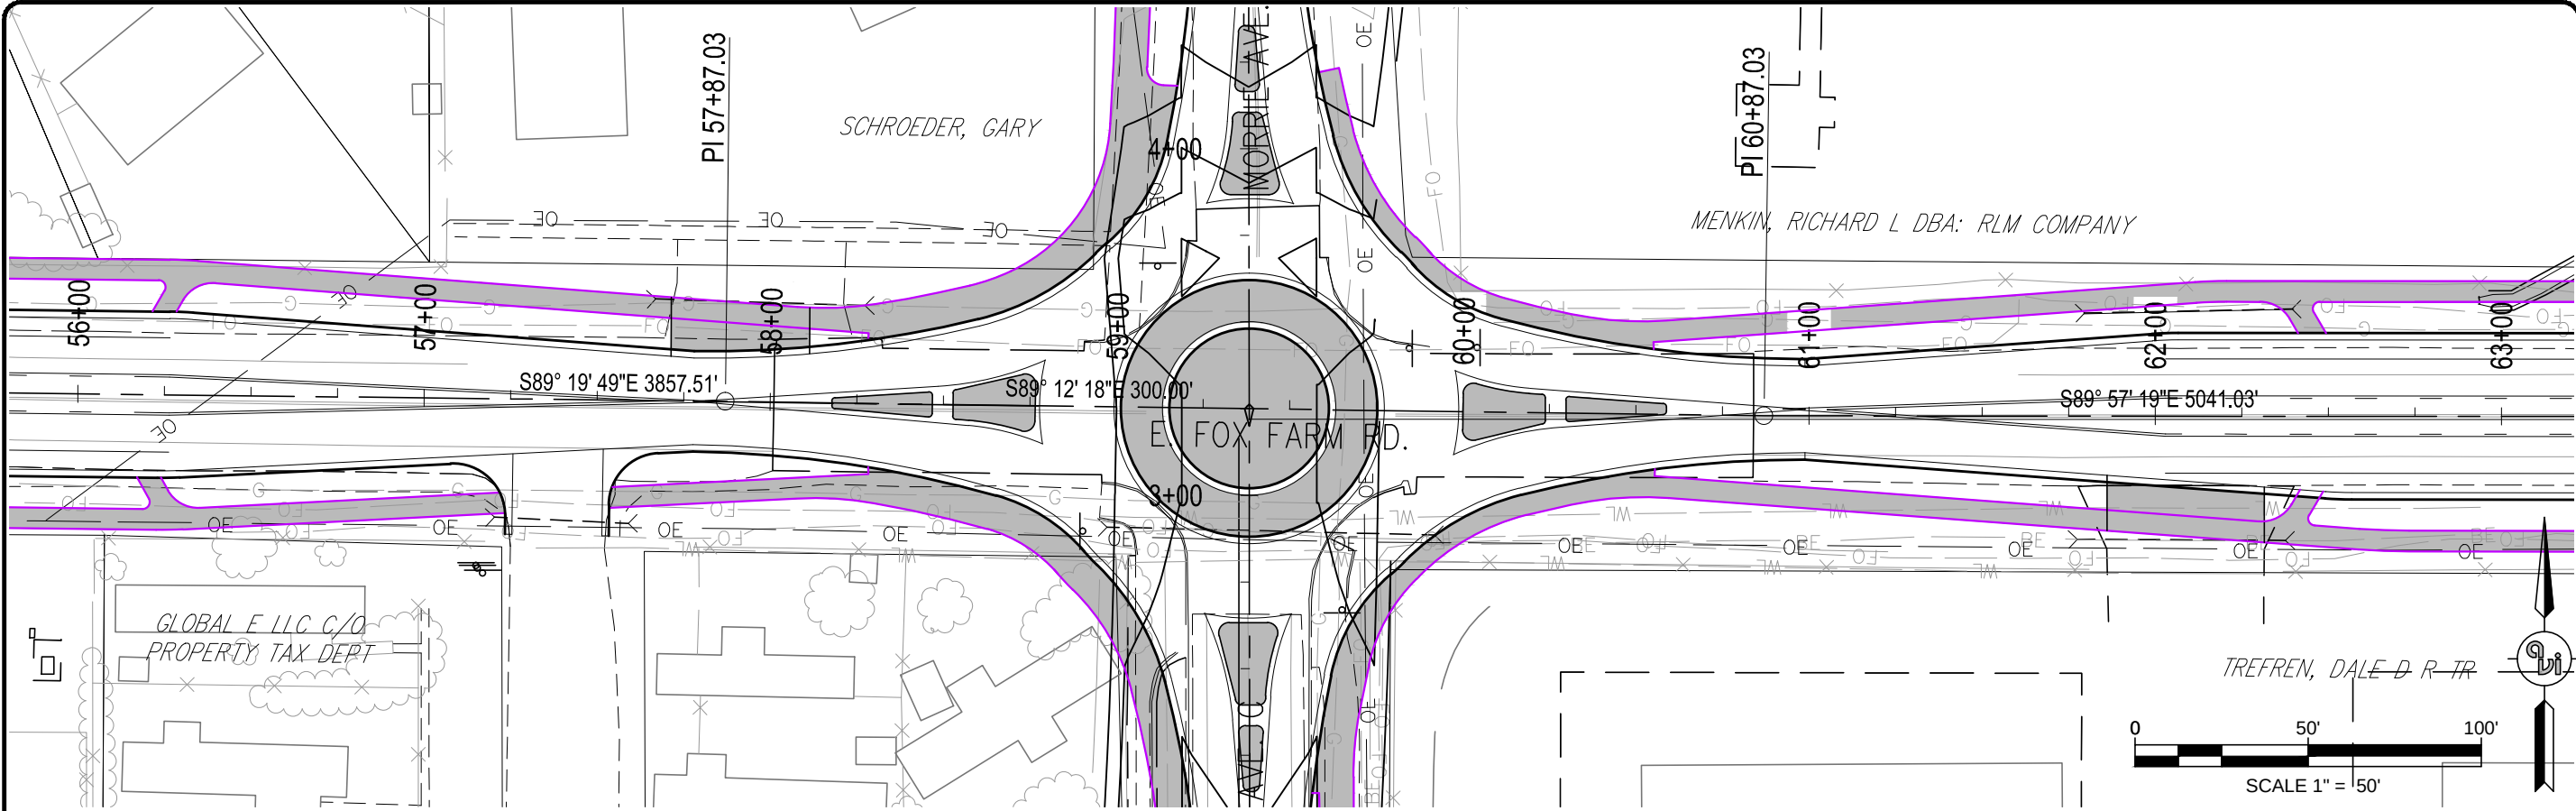

PRELIMINARY PLANS  
NOT FOR CONSTRUCTION

| NO. | REVISION | DATE |
|-----|----------|------|
|     |          |      |
|     |          |      |
|     |          |      |
|     |          |      |

PREPARED FOR:  
MPO 2101 ONEIL AVE.  
RM 205  
CHEYENNE, WY. 82001

PROJECT: FOX FARM ROAD STREET IMPROVEMENTS


DRAWING TITLE: FOX FARM RD. PLAN AND PROFILE  
STA. 56+25 - 62+75

**avi** p.c.  
engineering  
planning  
surveying  
PHONE (307) 637-6017  
1103 OLD TOWN LANE, SUITE 101  
CHEYENNE, WY 82009  
AVI@AVIPC.COM

DATE: 6-20-13  
DRAWN BY: SRL  
DESIGNED BY: TC  
CHECKED BY: TC

JOB NO.: 2-3211-B

ST-10 83  
SHEET NO. OF


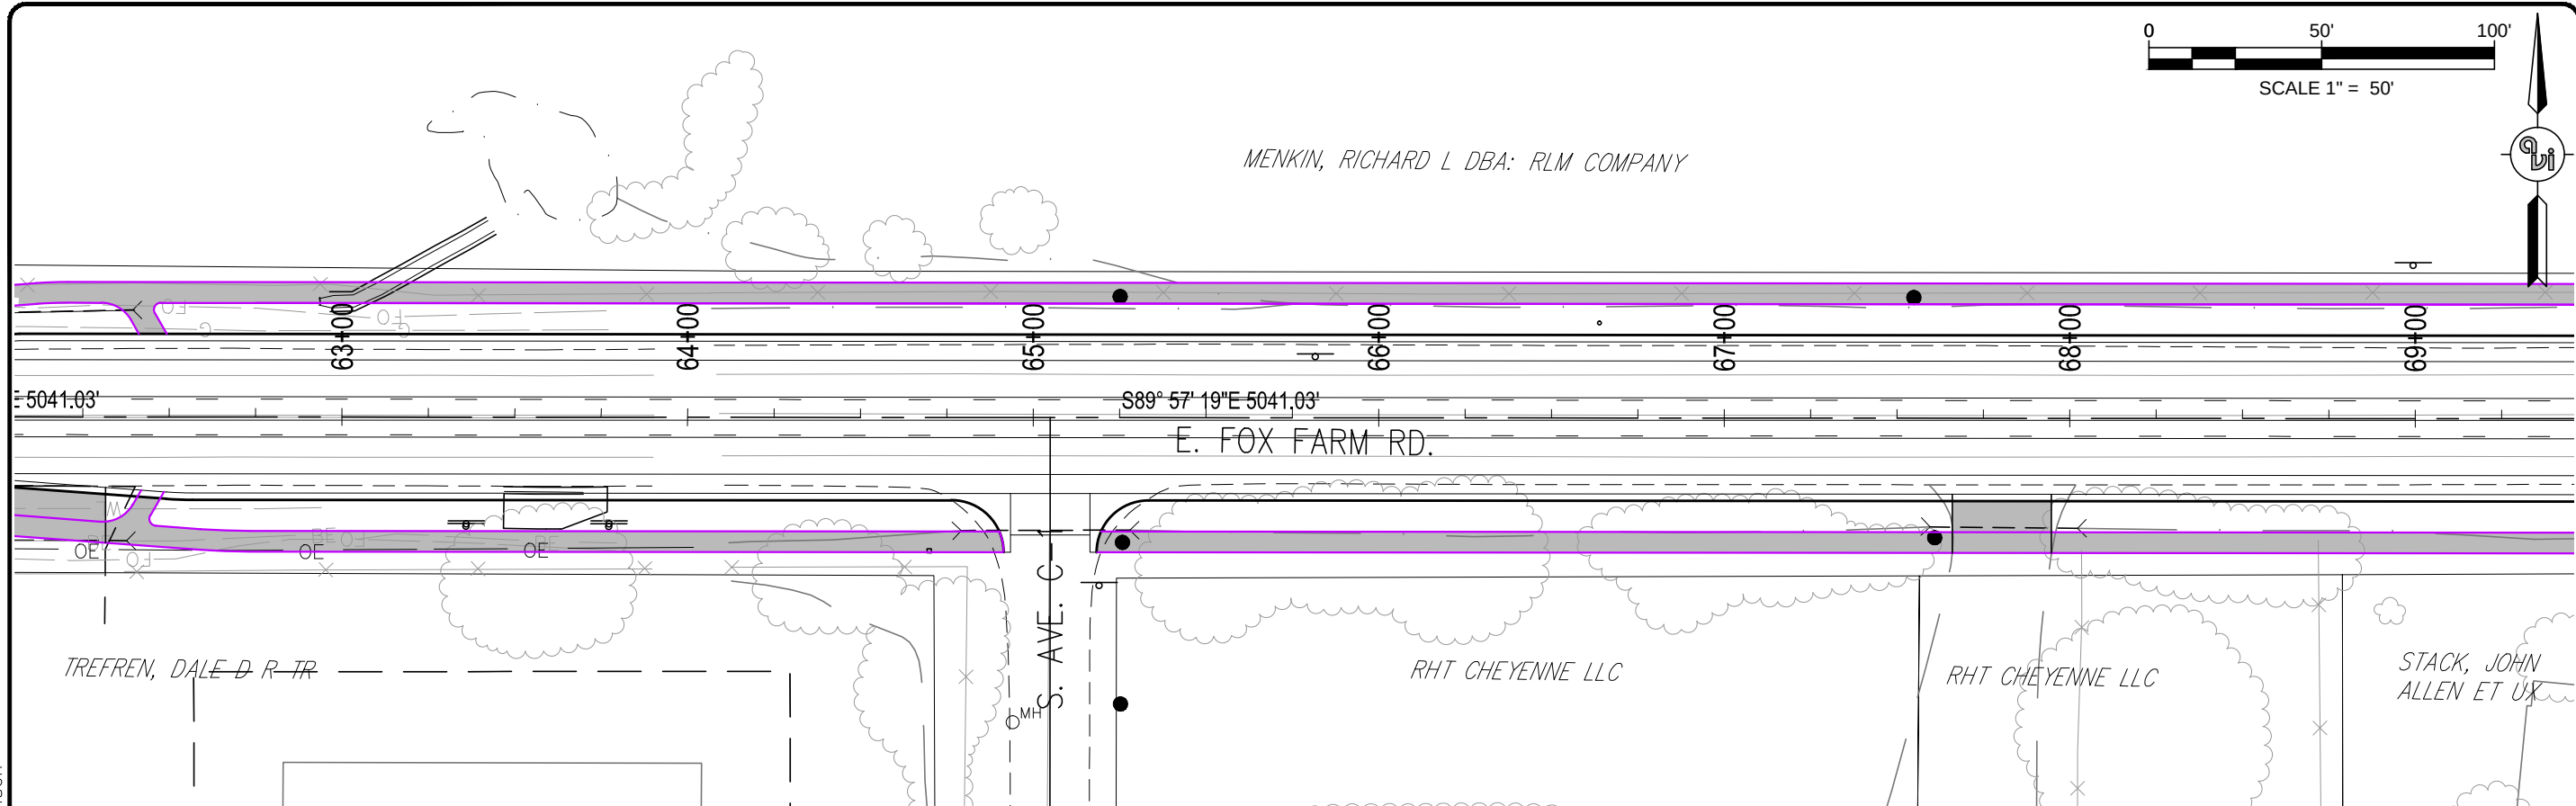


|      |       |       |       |       |       |       |       |       |      |
|------|-------|-------|-------|-------|-------|-------|-------|-------|------|
| 6010 |       |       |       |       |       |       |       |       | 6010 |
| 6005 |       |       |       |       |       |       |       |       | 6005 |
| 6000 |       |       |       |       |       |       |       |       | 6000 |
| 5995 |       |       |       |       |       |       |       |       | 5995 |
| 5990 |       |       |       |       |       |       |       |       | 5990 |
|      | 62+50 | 63+00 | 64+00 | 65+00 | 66+00 | 67+00 | 68+00 | 69+00 |      |

|  |      |
|--|------|
|  | 5995 |
|  | 5990 |

[illegible]

H:\3211\design\3211B FOX FARM STREET IMP.dwg Aug 30, 2013 4:12pm jwilson

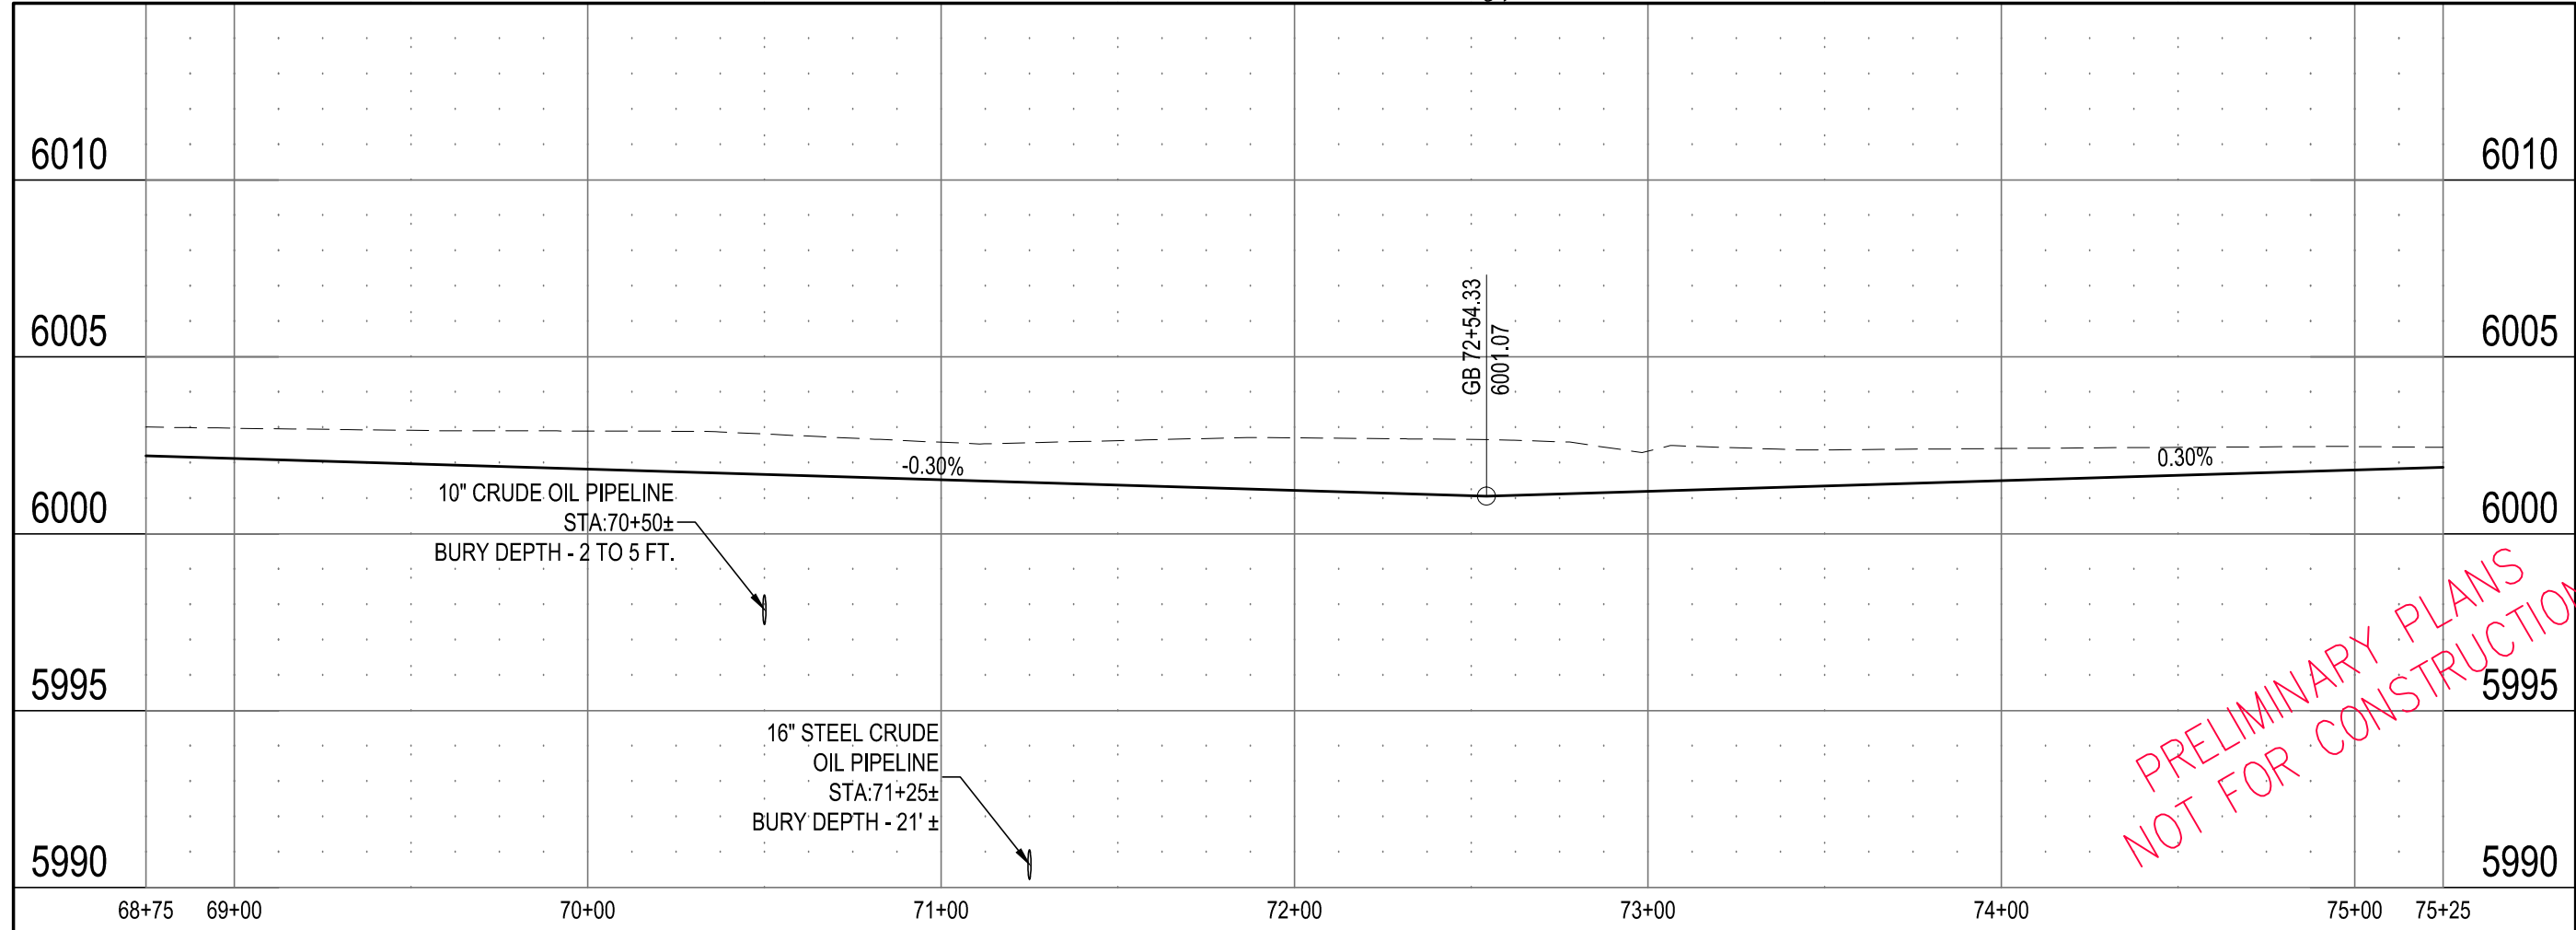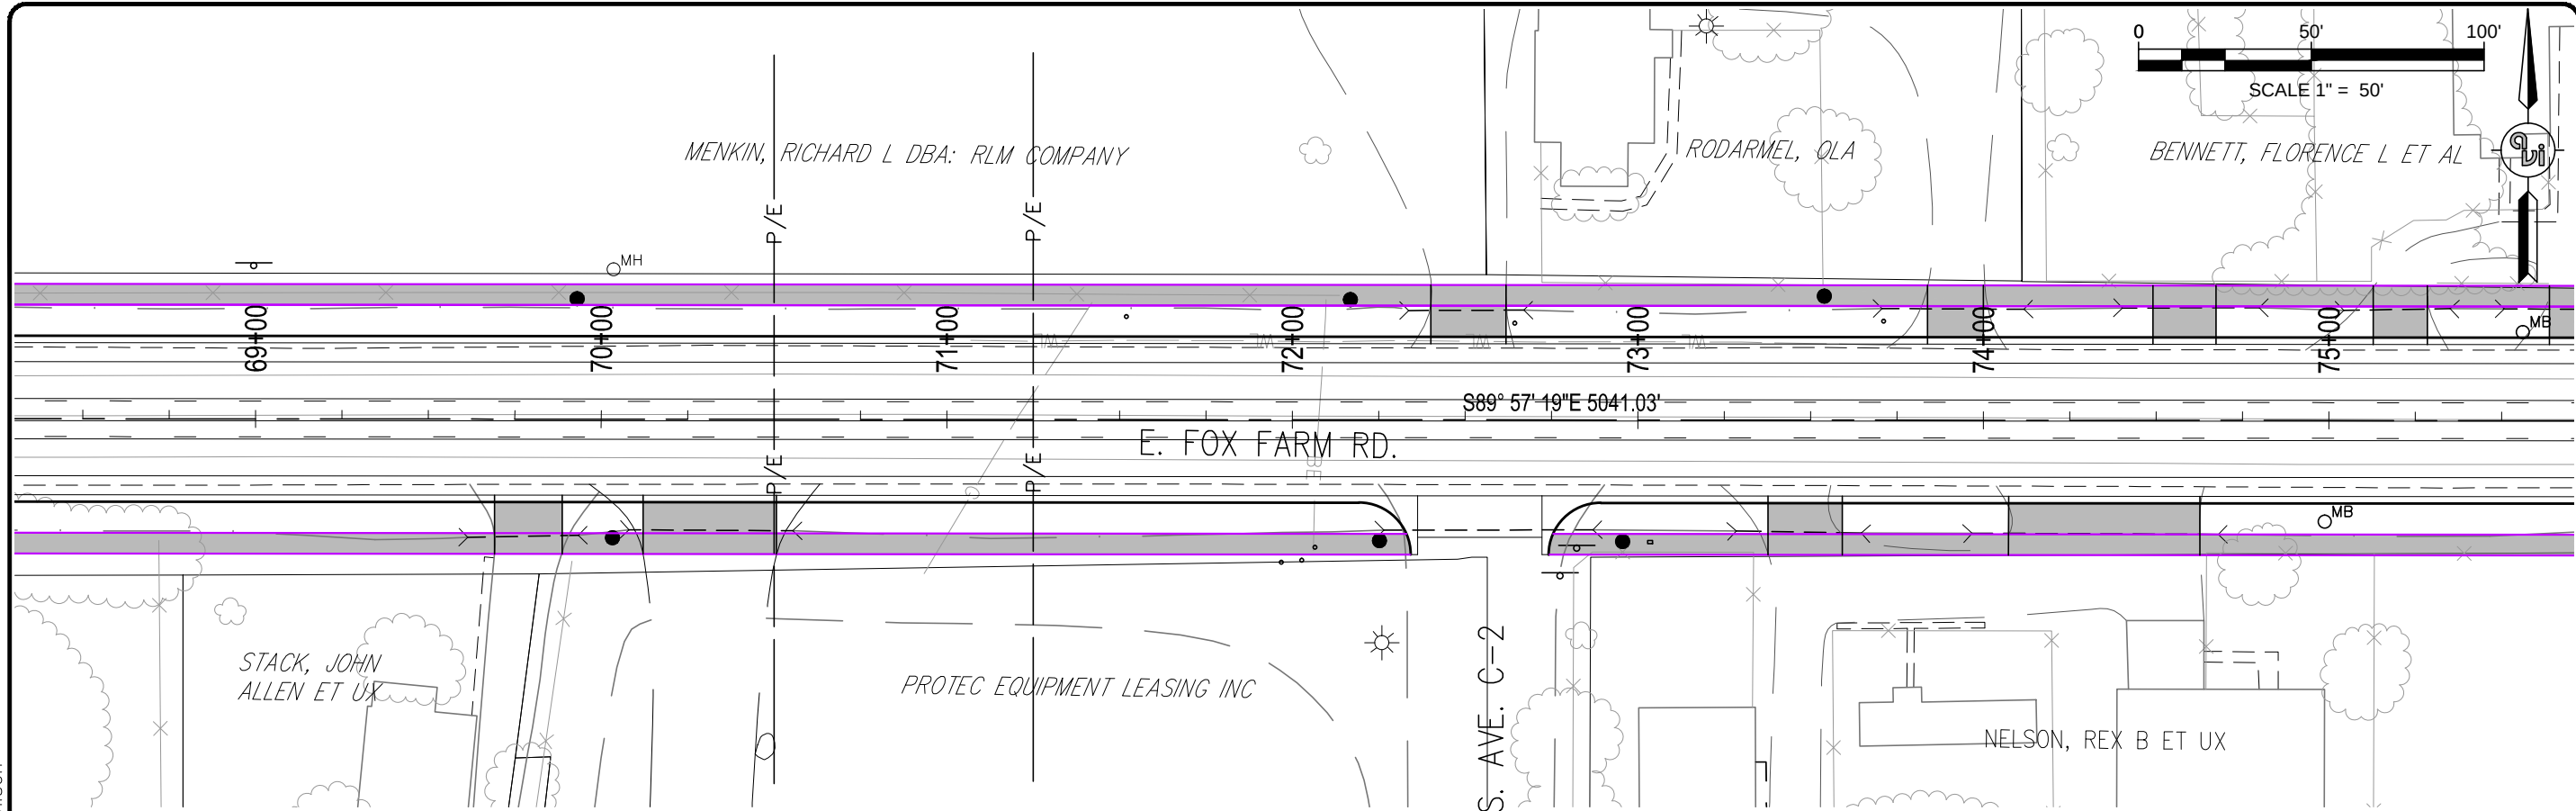

| NO. | REVISION | DATE |
|-----|----------|------|
|     |          |      |
|     |          |      |
|     |          |      |
|     |          |      |

PREPARED FOR:  
MPO 2101 O'NEIL AVE.  
RM 205  
CHEYENNE, WY. 82001

PROJECT: FOX FARM ROAD STREET IMPROVEMENTS  
DRAWING TITLE: FOX FARM RD. PLAN AND PROFILE  
STA. 6878 - 75+25



avi p.c.  
engineering  
planning  
surveying  
PHONE (307) 637-6017  
1103 OLD TOWN LANE, SUITE 101  
CHEYENNE, WY 82009  
AVI@AVIPC.COM

DATE: 6-20-13  
DRAWN BY: SRL  
DESIGNED BY: TC  
CHECKED BY: TC

JOB NO.: 2-3211-B

ST-12 83  
SHEET NO. OF

H:\3211\design\3211B FOX FARM STREET IMP.dwg Aug 30, 2013 4:12pm jwilson

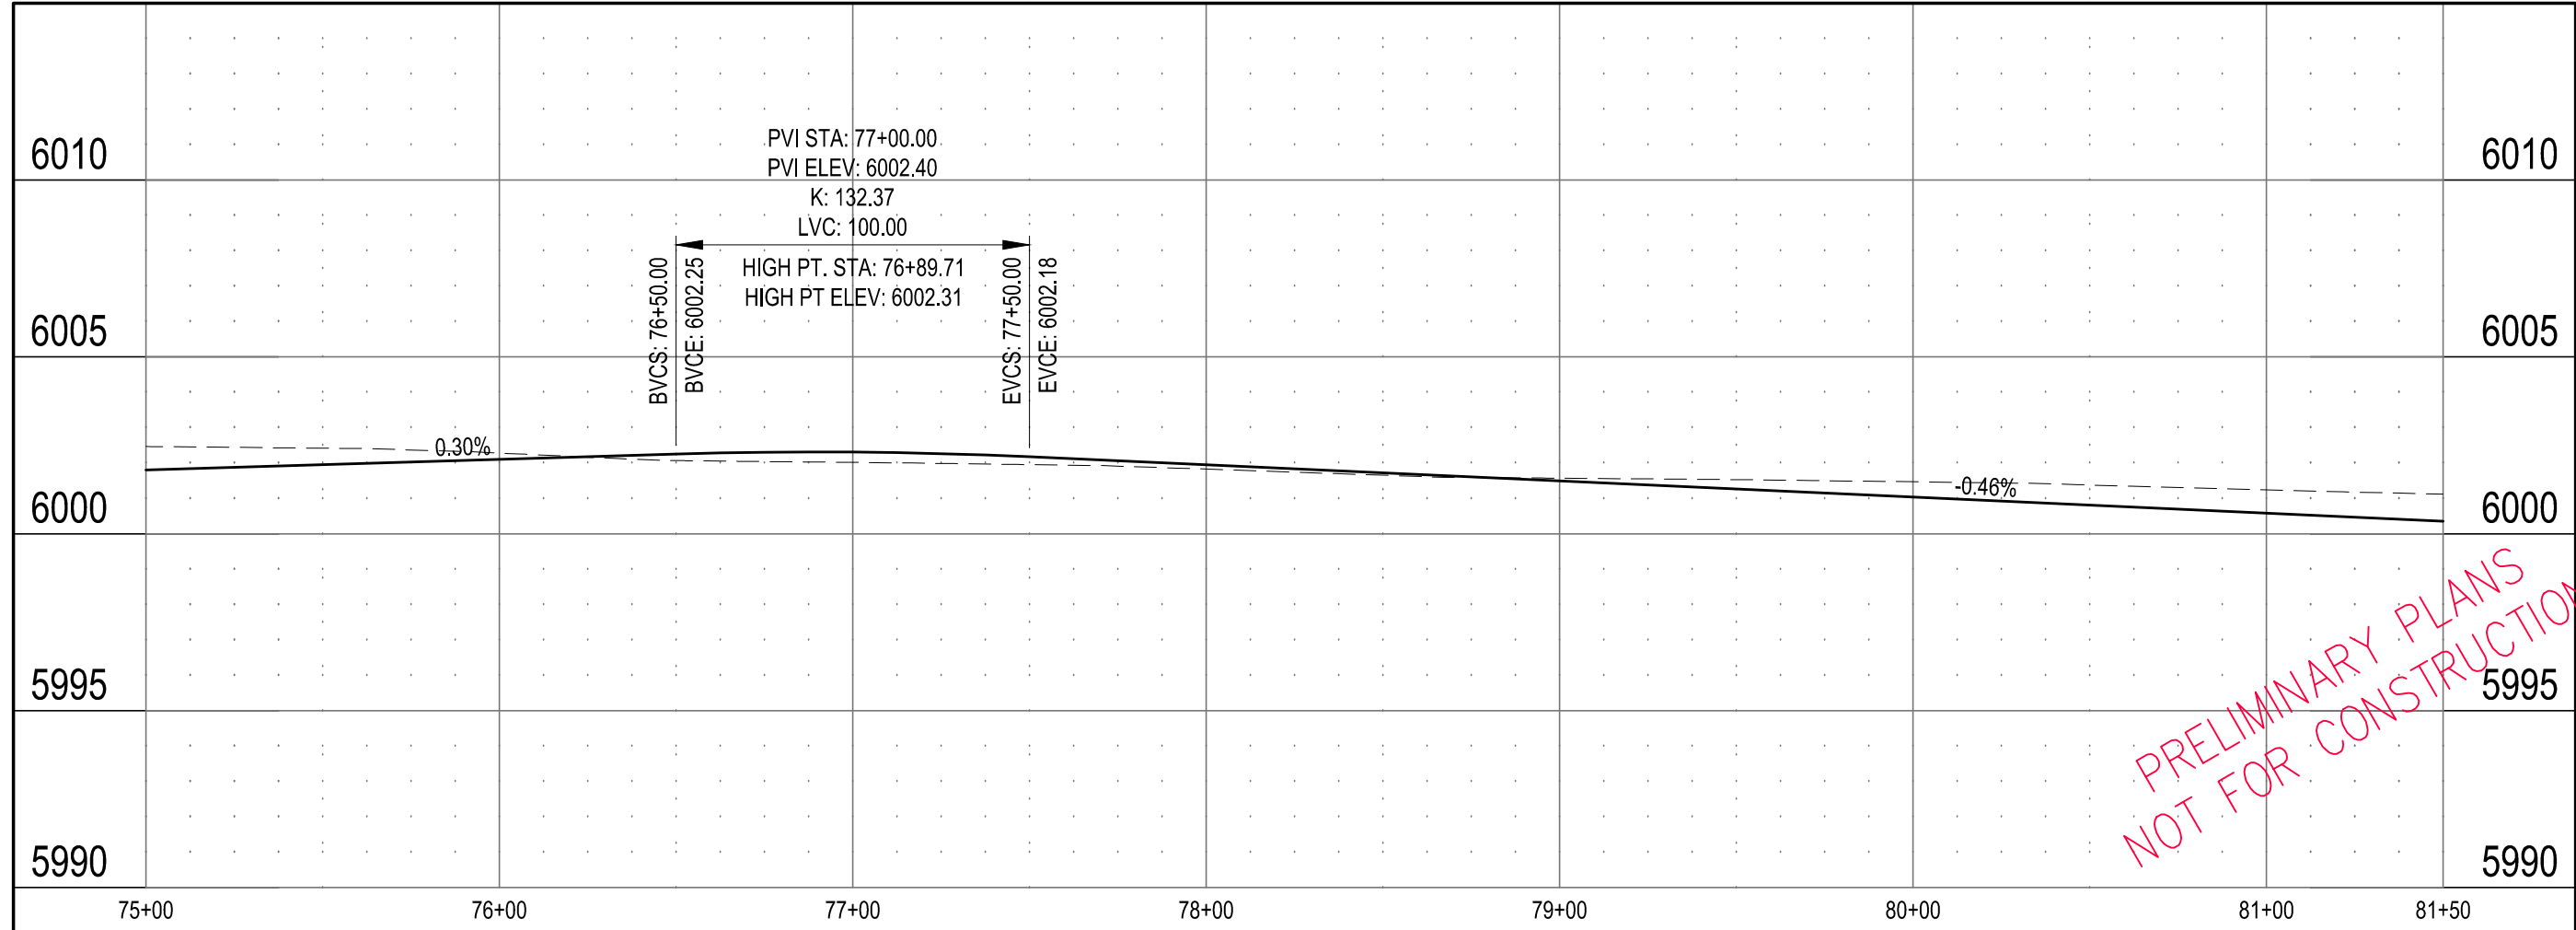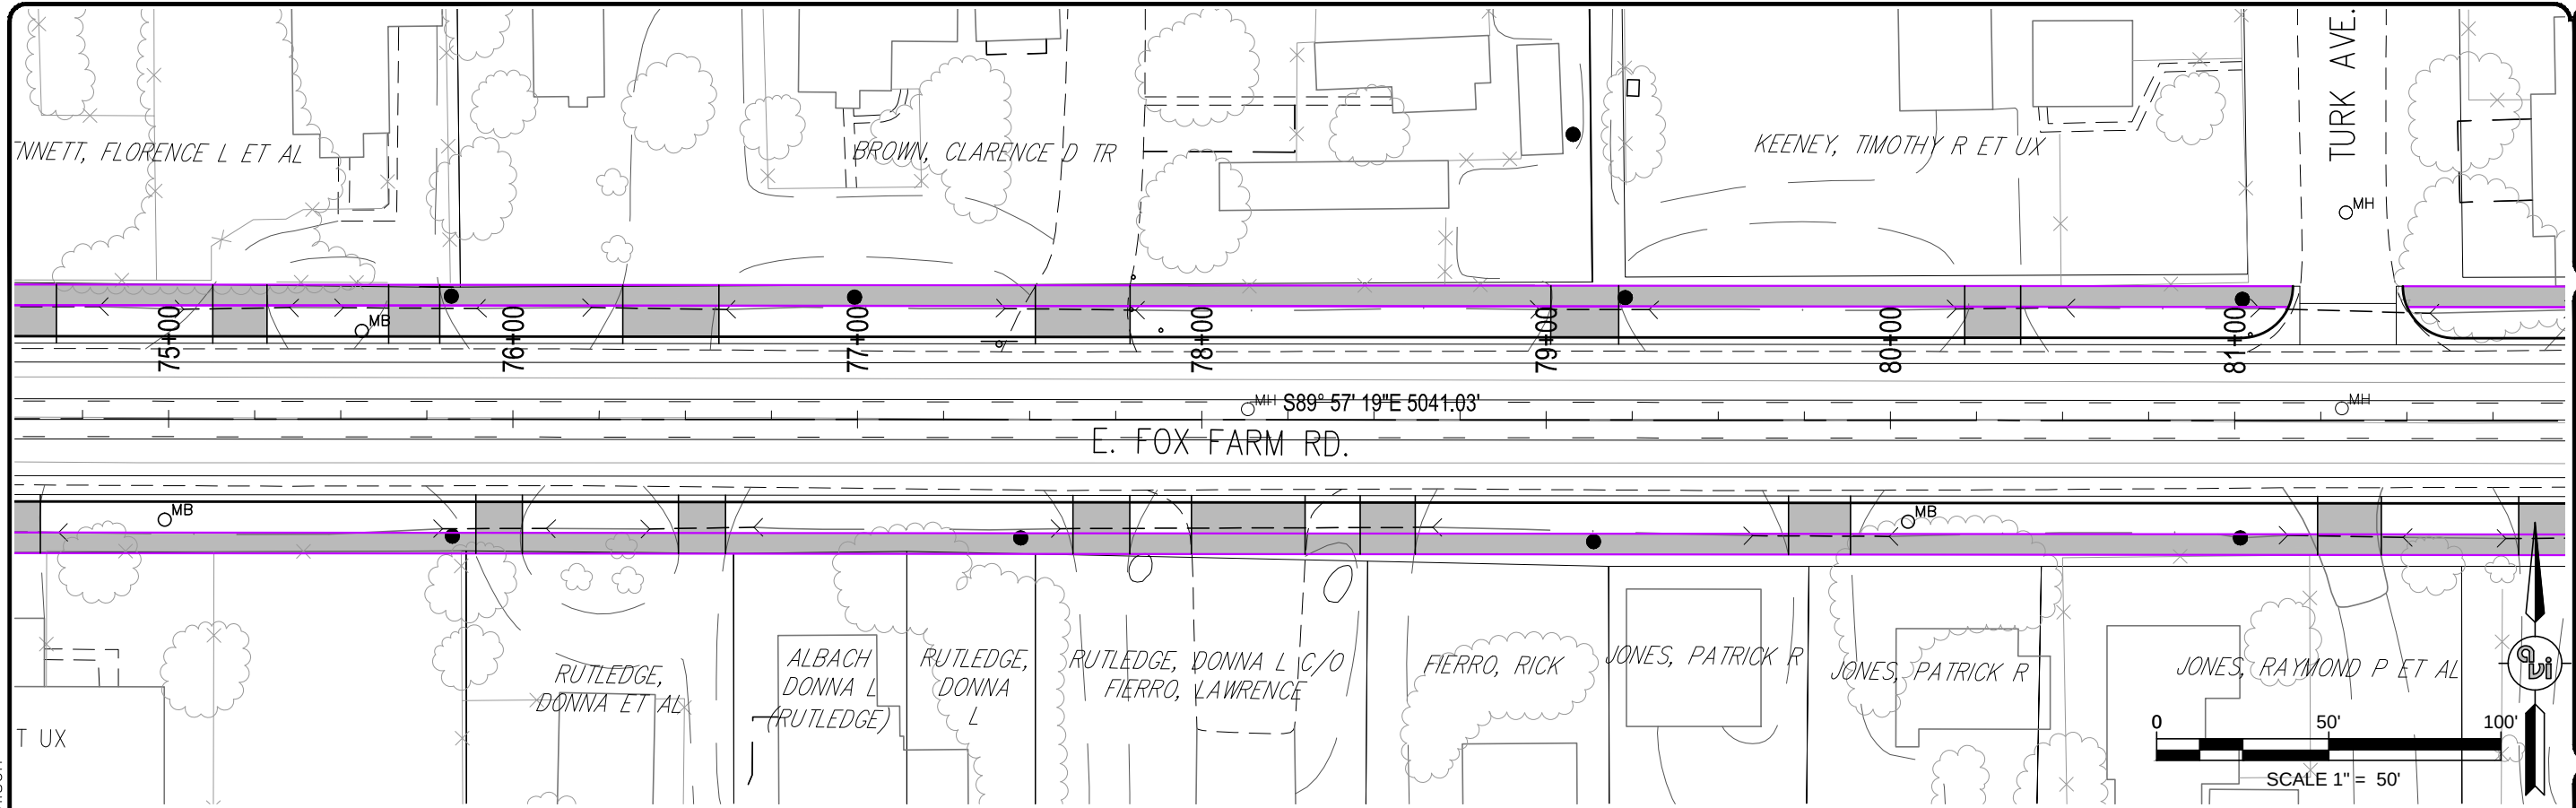

PRELIMINARY PLANS  
NOT FOR CONSTRUCTION

| NO. | REVISION | DATE |
|-----|----------|------|
|     |          |      |
|     |          |      |
|     |          |      |
|     |          |      |

PROJECT: FOX FARM ROAD STREET IMPROVEMENTS

PREPARED FOR: MPO 2101 O'NEIL AVE. RM 205 CHEYENNE, WY. 82001

DRAWING TITLE: FOX FARM RD. PLAN AND PROFILE STA. 75+00 - 81+50

engineering planning surveying **avi** p.c.


PHONE (307) 637-6017  
1103 OLD TOWN LANE, SUITE 101  
CHEYENNE, WY 82009  
AVI@AVIFC.COM

DATE: 6-20-13  
DRAWN BY: SRL  
DESIGNED BY: TC  
CHECKED BY: TC

JOB NO.: 2-3211-B

ST-13 83  
SHEET NO. OF

H:\3211\design\3211B FOX FARM STREET IMP.dwg Aug 30, 2013 4:13pm jwilson

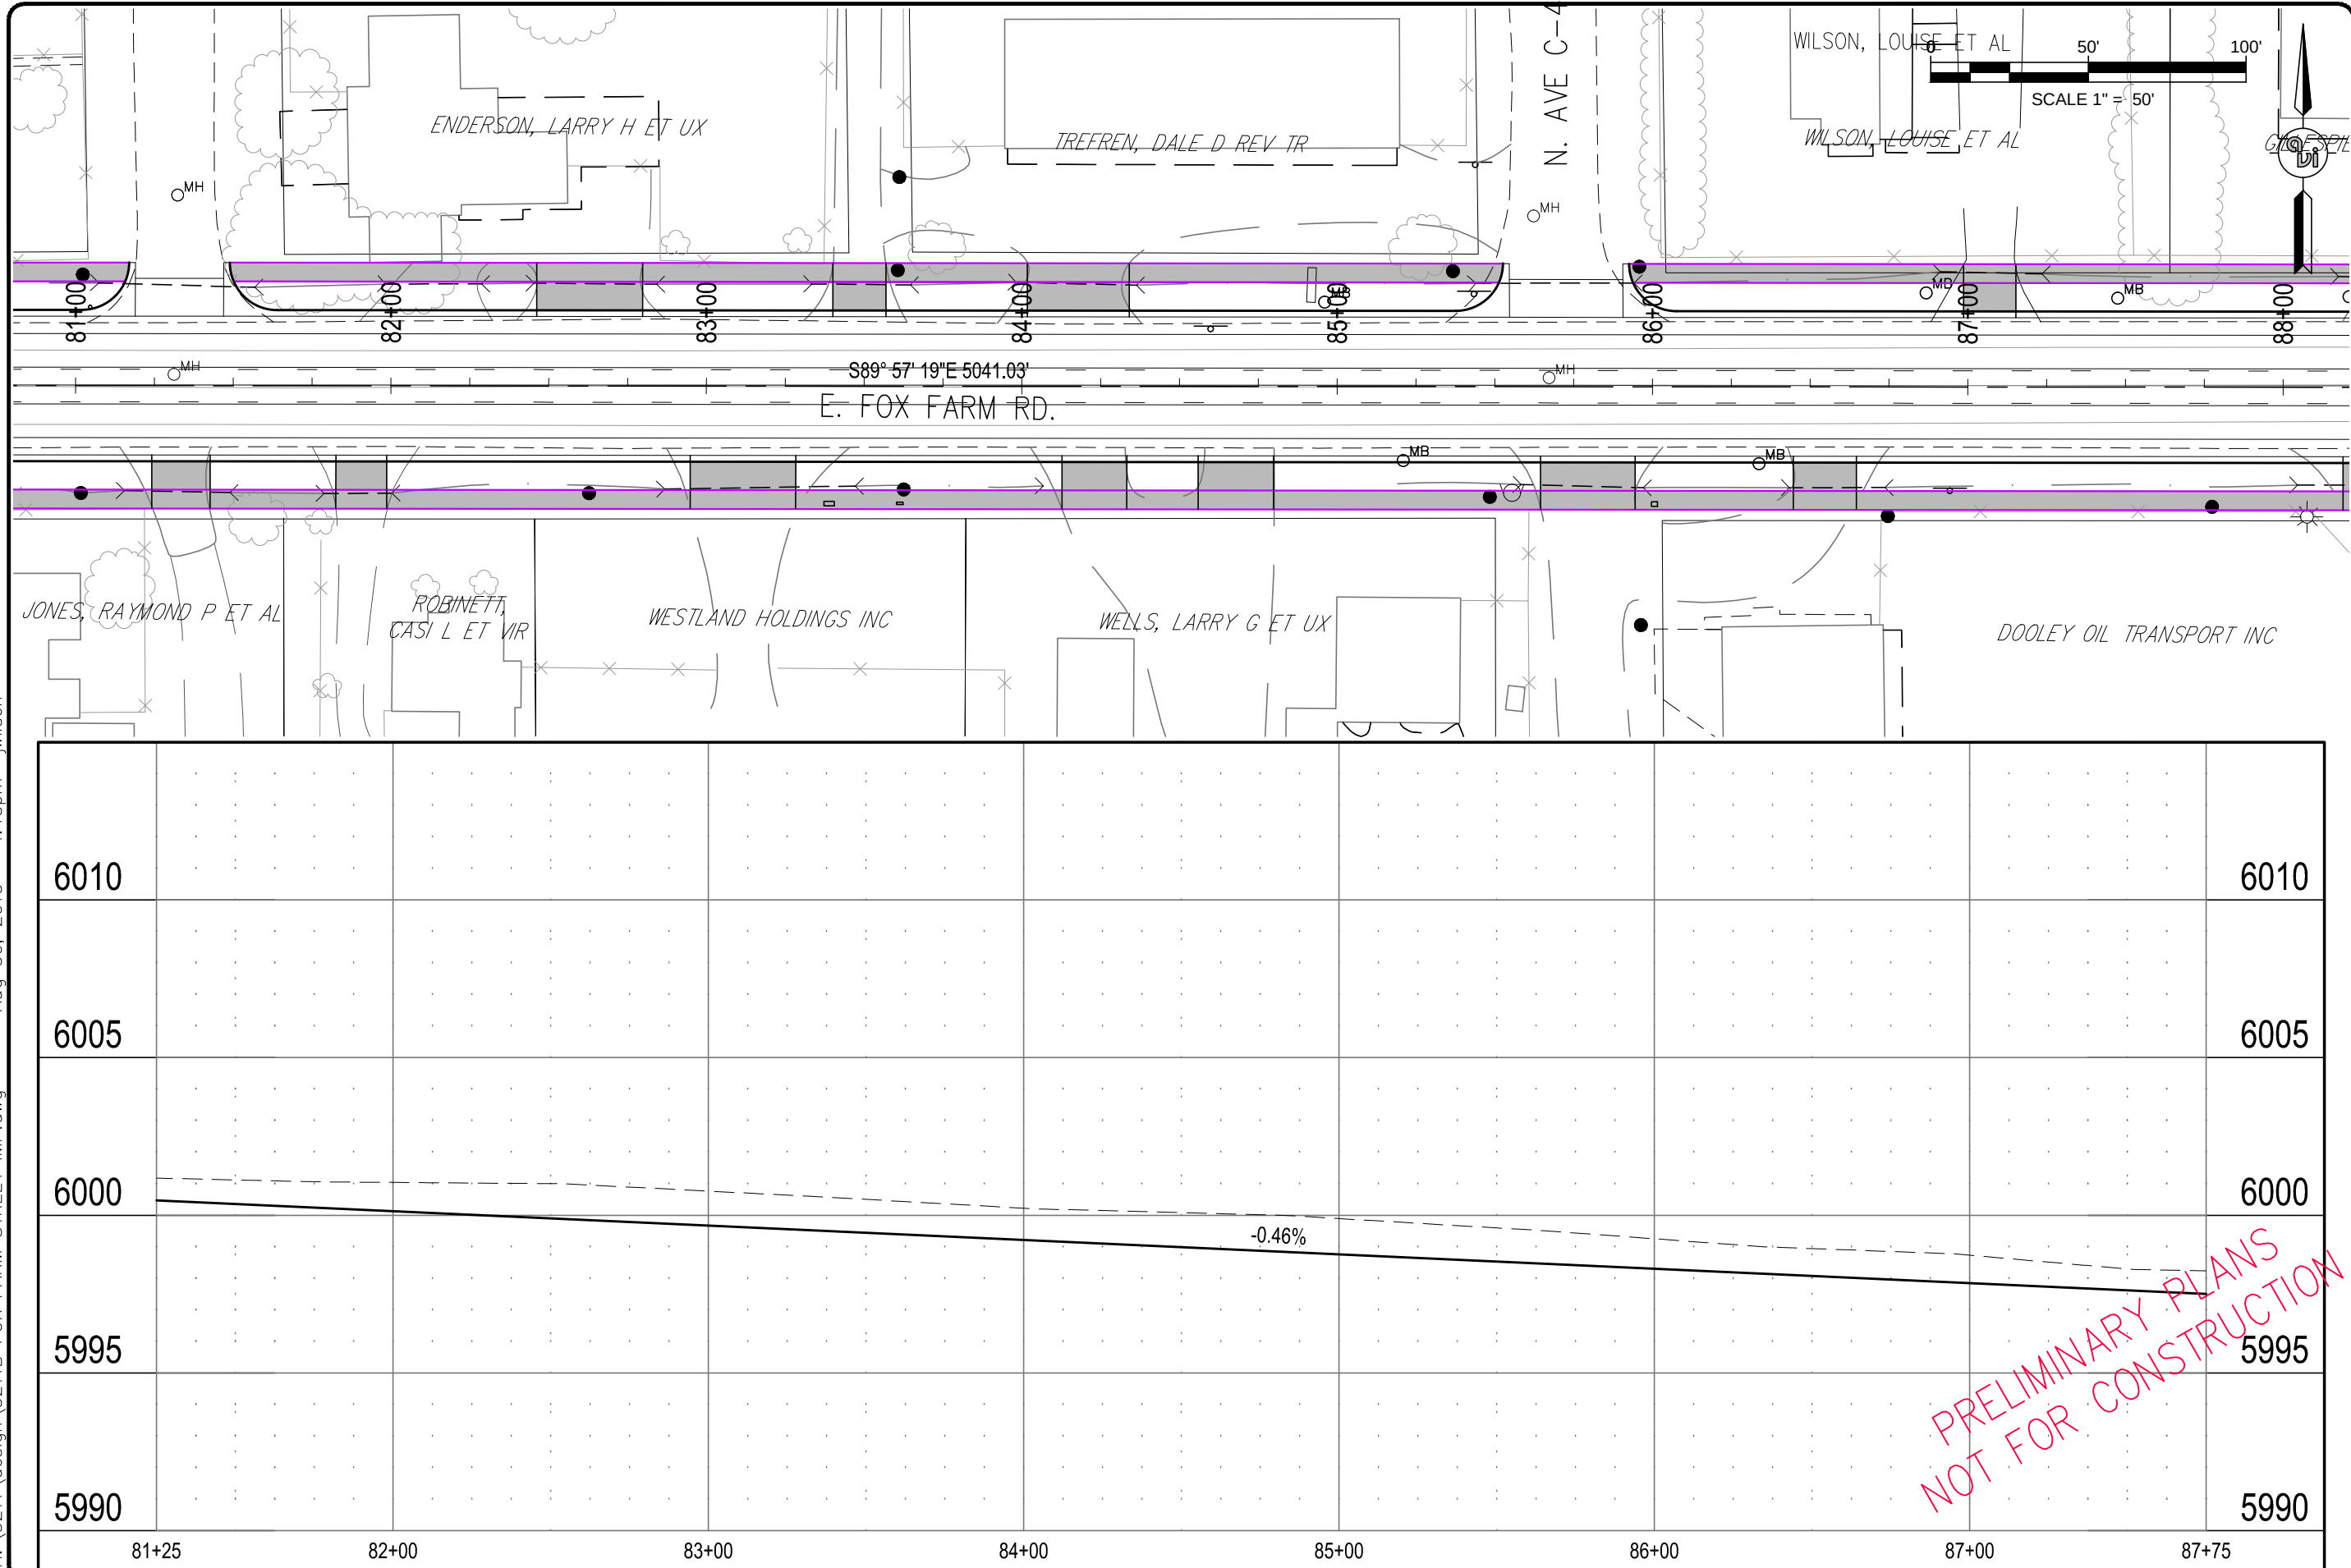

|     |          |      |
|-----|----------|------|
| NO. | REVISION | DATE |
|     |          |      |
|     |          |      |
|     |          |      |

PREPARED FOR:

MPO 2101 O'NEIL AVE.  
RM 205  
CHEYENNE, WY. 82001

PROJECT: FOX FARM ROAD STREET IMPROVEMENTS

DRAWING TITLE: FOX FARM RD. PLAN AND PROFILE  
STA. 81+25 - 87+75

**avi** p.c.  
engineering  
planning  
surveying



PHONE (307) 637-6017  
1103 OLD TOWN LANE, SUITE 101  
CHEYENNE, WY 82009  
AVI@AVIPC.COM

DATE: 6-20-13  
DRAWN BY: SRL  
DESIGNED BY: TC  
CHECKED BY: TC


JOB NO.: 2-3211-B

ST-14 83  
SHEET NO. OF

H:\3211\design\3211B FOX FARM STREET IMP.dwg Aug 30, 2013 4:13pm jwilson

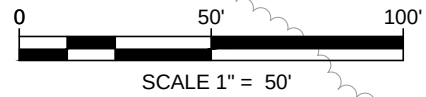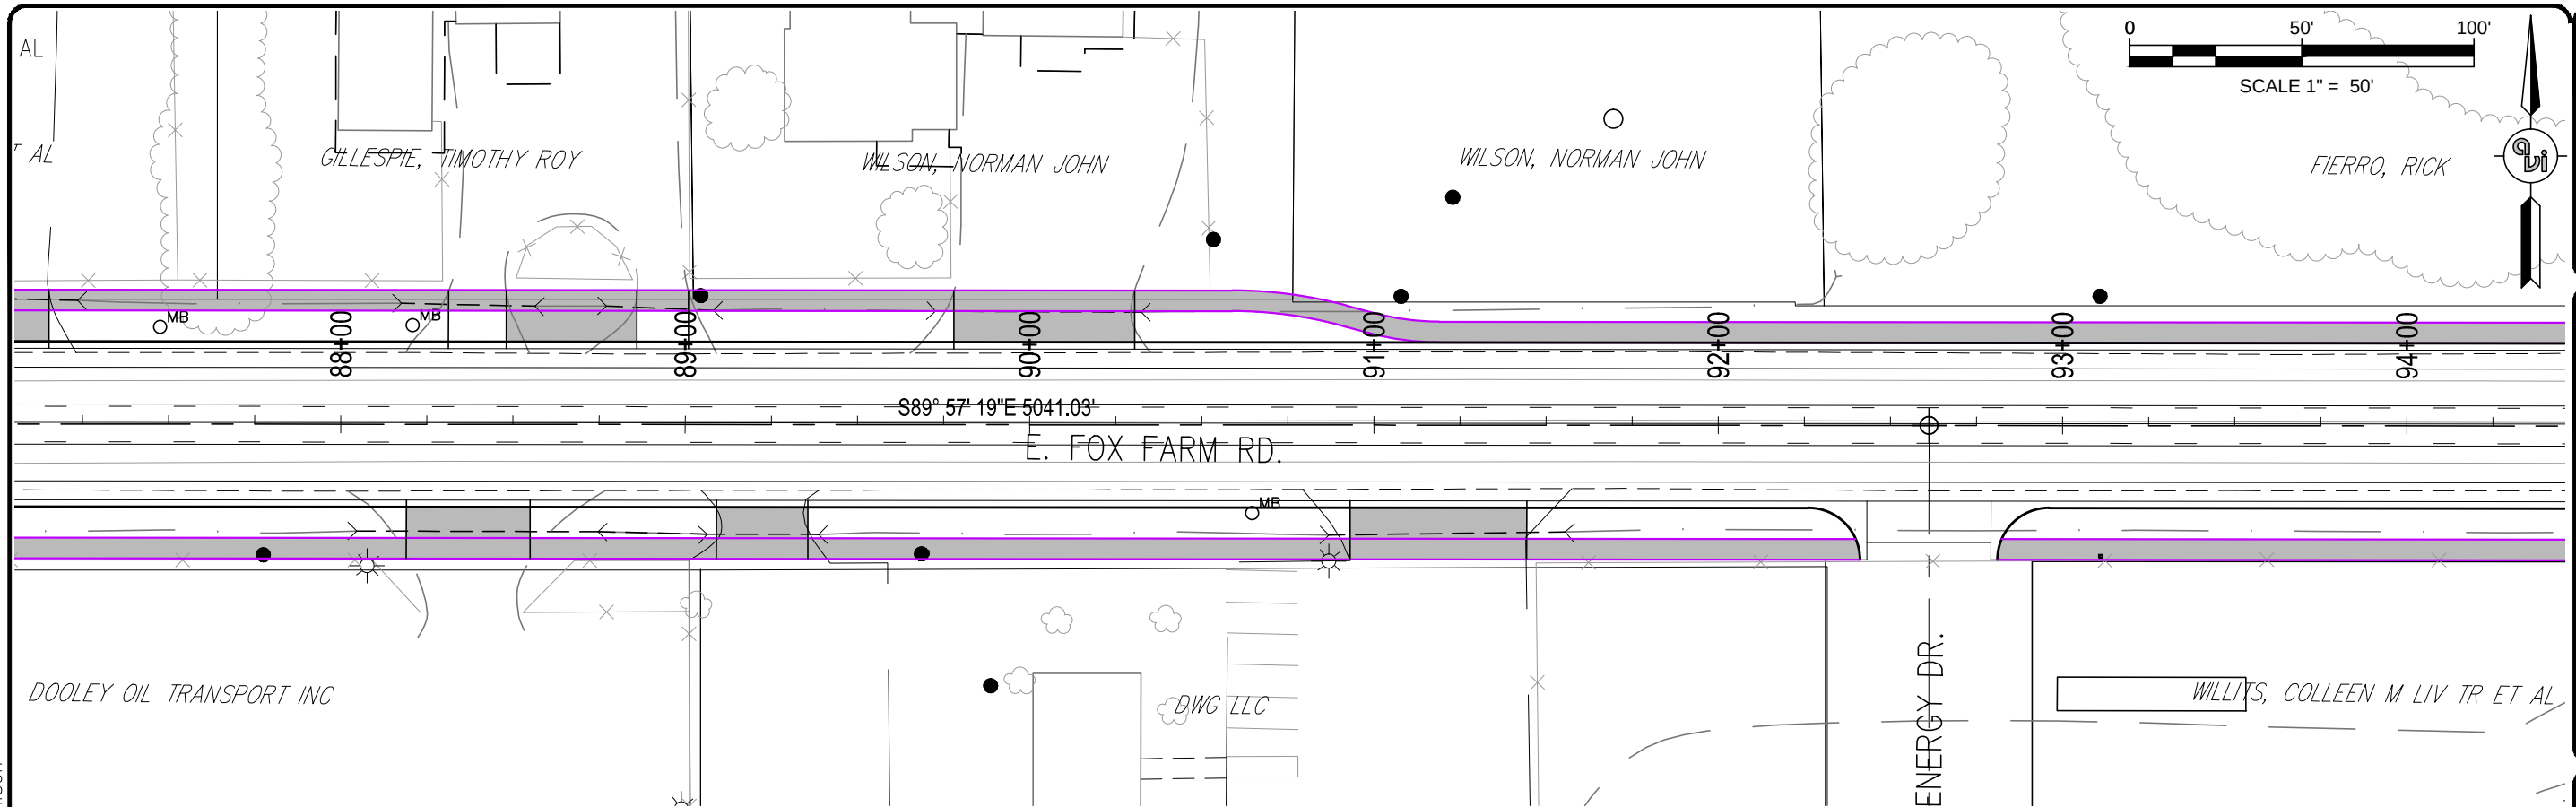

| NO. | REVISION | DATE |
|-----|----------|------|
|     |          |      |
|     |          |      |
|     |          |      |
|     |          |      |

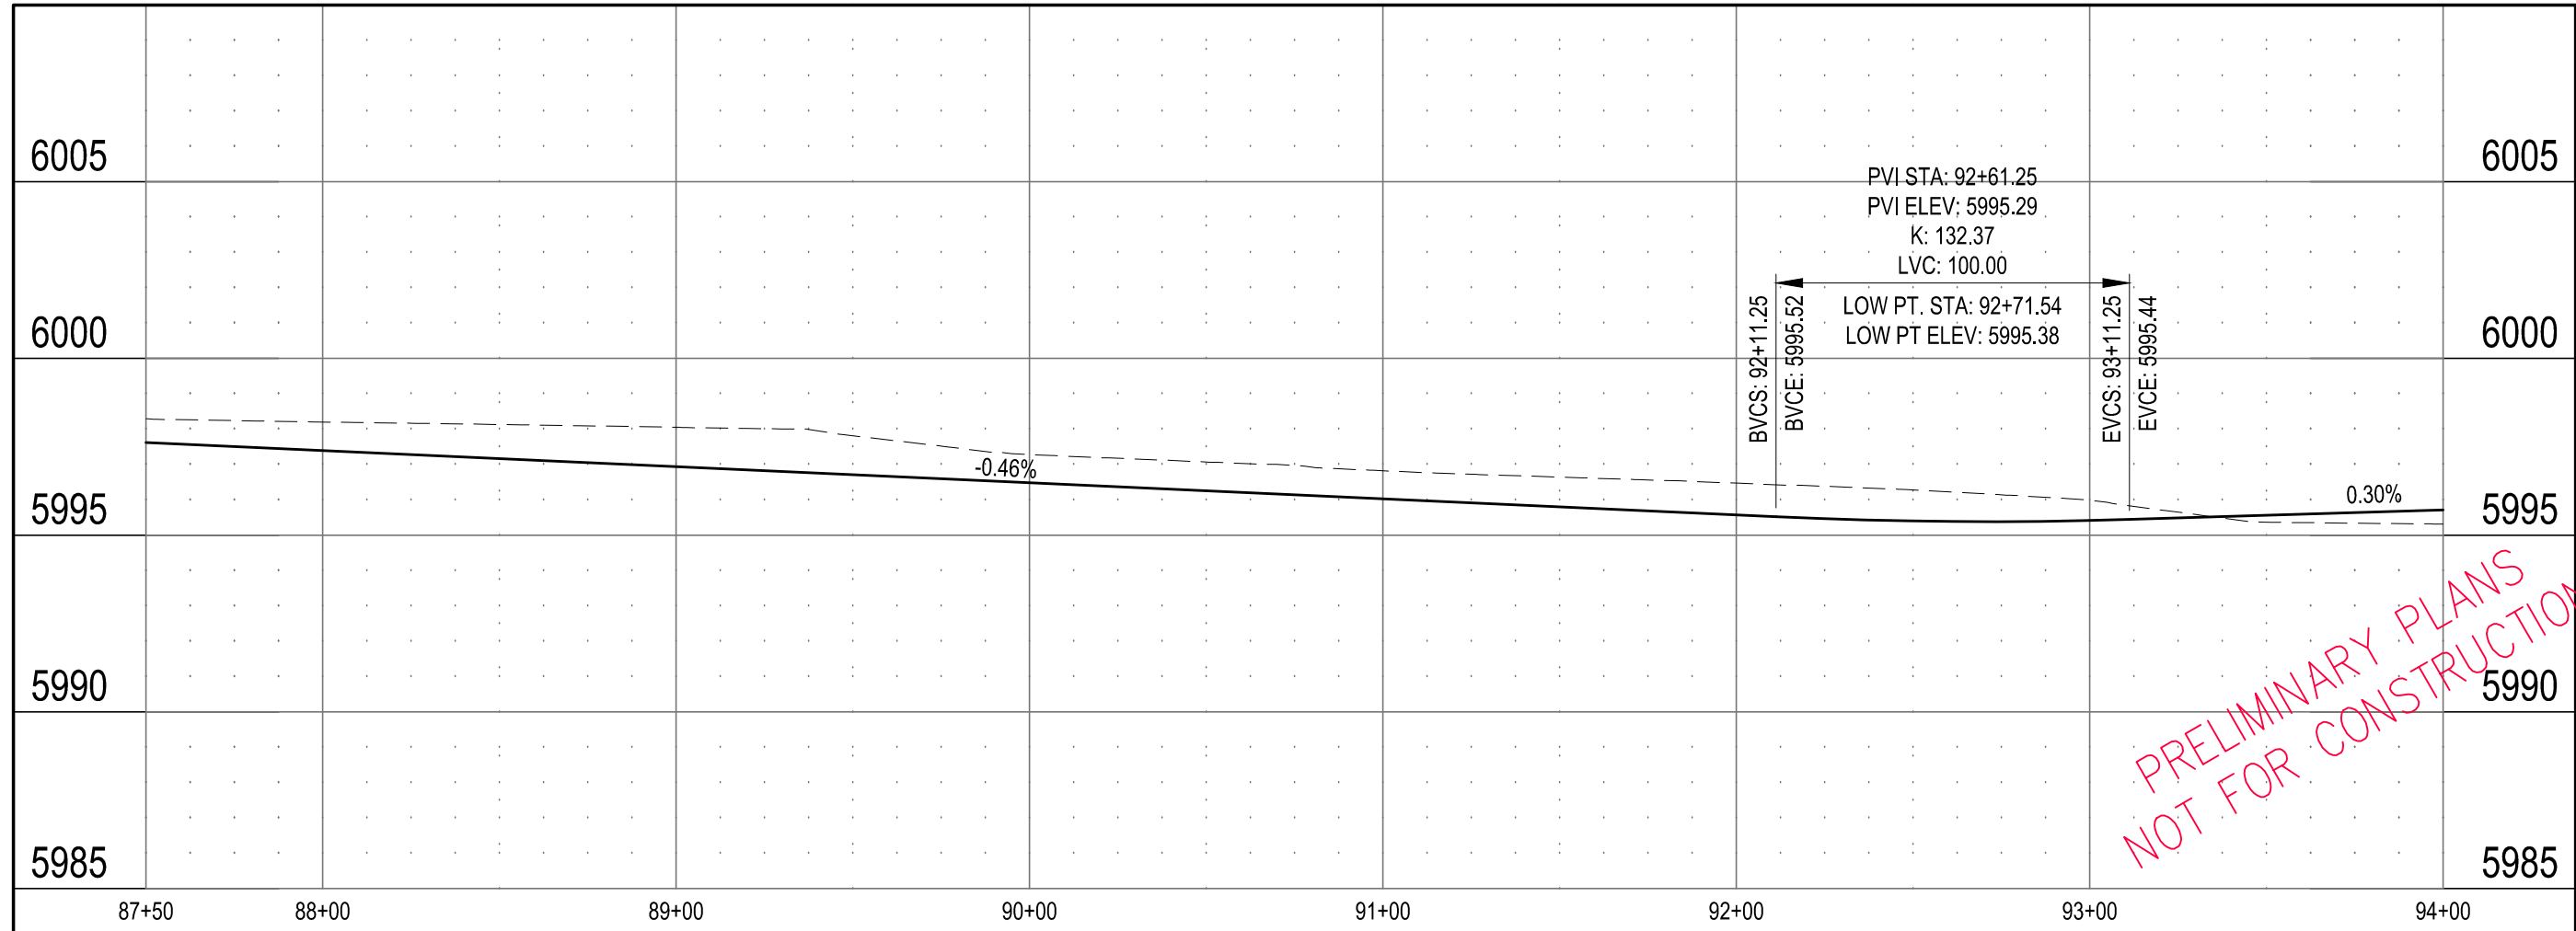

PREPARED FOR:  
MPO  
2101 ONEIL AVE.  
RM 205  
CHEYENNE, WY. 82001

PROJECT: FOX FARM ROAD STREET IMPROVEMENTS  
DRAWING TITLE: FOX FARM RD. PLAN AND PROFILE  
STA. 87+50 - 94+00



**avi** p.c.  
engineering  
planning  
surveying  
PHONE (307) 637-6017  
1103 OLD TOWN LANE, SUITE 101  
CHEYENNE, WY 82009  
AVI@AVIFC.COM

DATE: 6-20-13  
DRAWN BY: SRL  
DESIGNED BY: TC  
CHECKED BY: TC

JOB NO.: 2-3211-B


ST-15 83  
SHEET NO. OF

H:\3211\design\3211B FOX FARM STREET IMP.dwg Aug 30, 2013 4:13pm jwilson

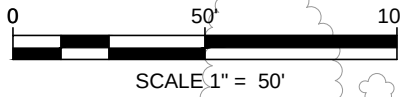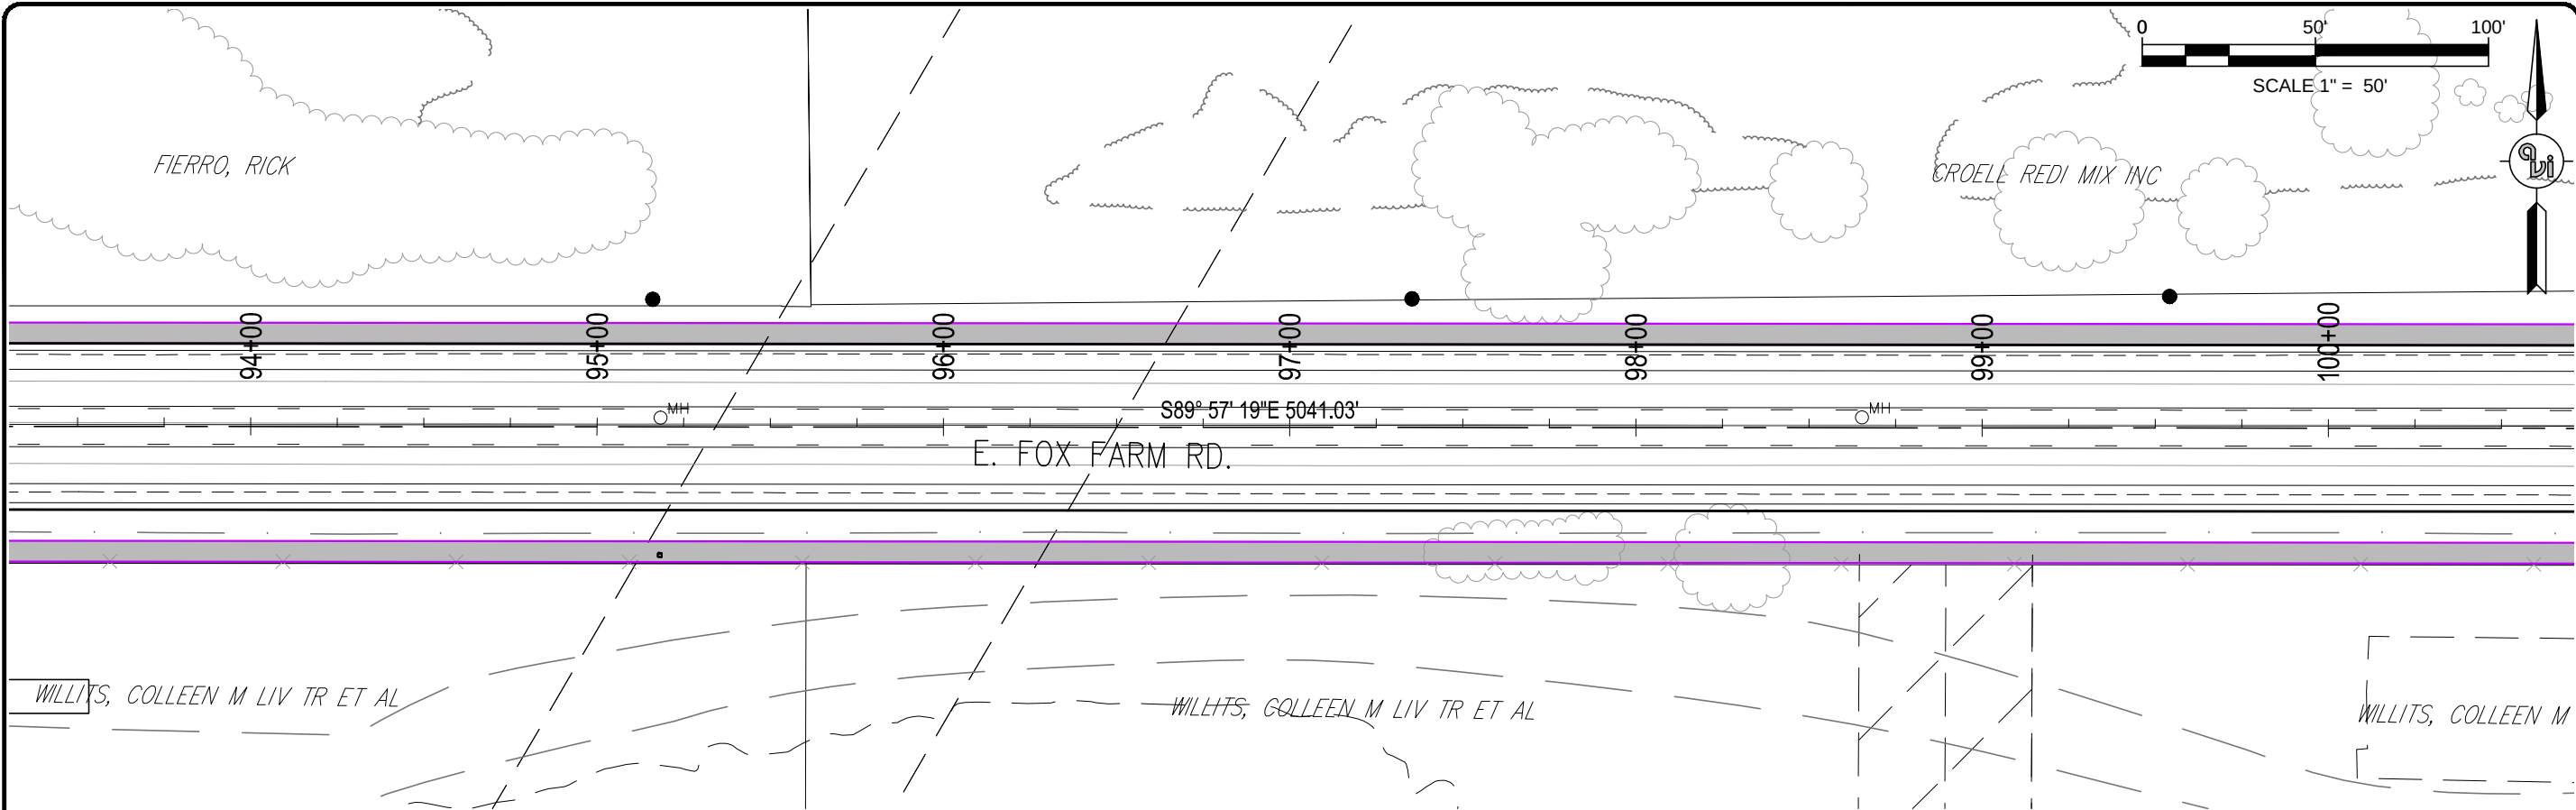

| NO. | REVISION | DATE |
|-----|----------|------|
|     |          |      |
|     |          |      |
|     |          |      |
|     |          |      |

PREPARED FOR:  
MPO  
2101 O'NEIL AVE.  
RM 205  
CHEYENNE, WY. 82001

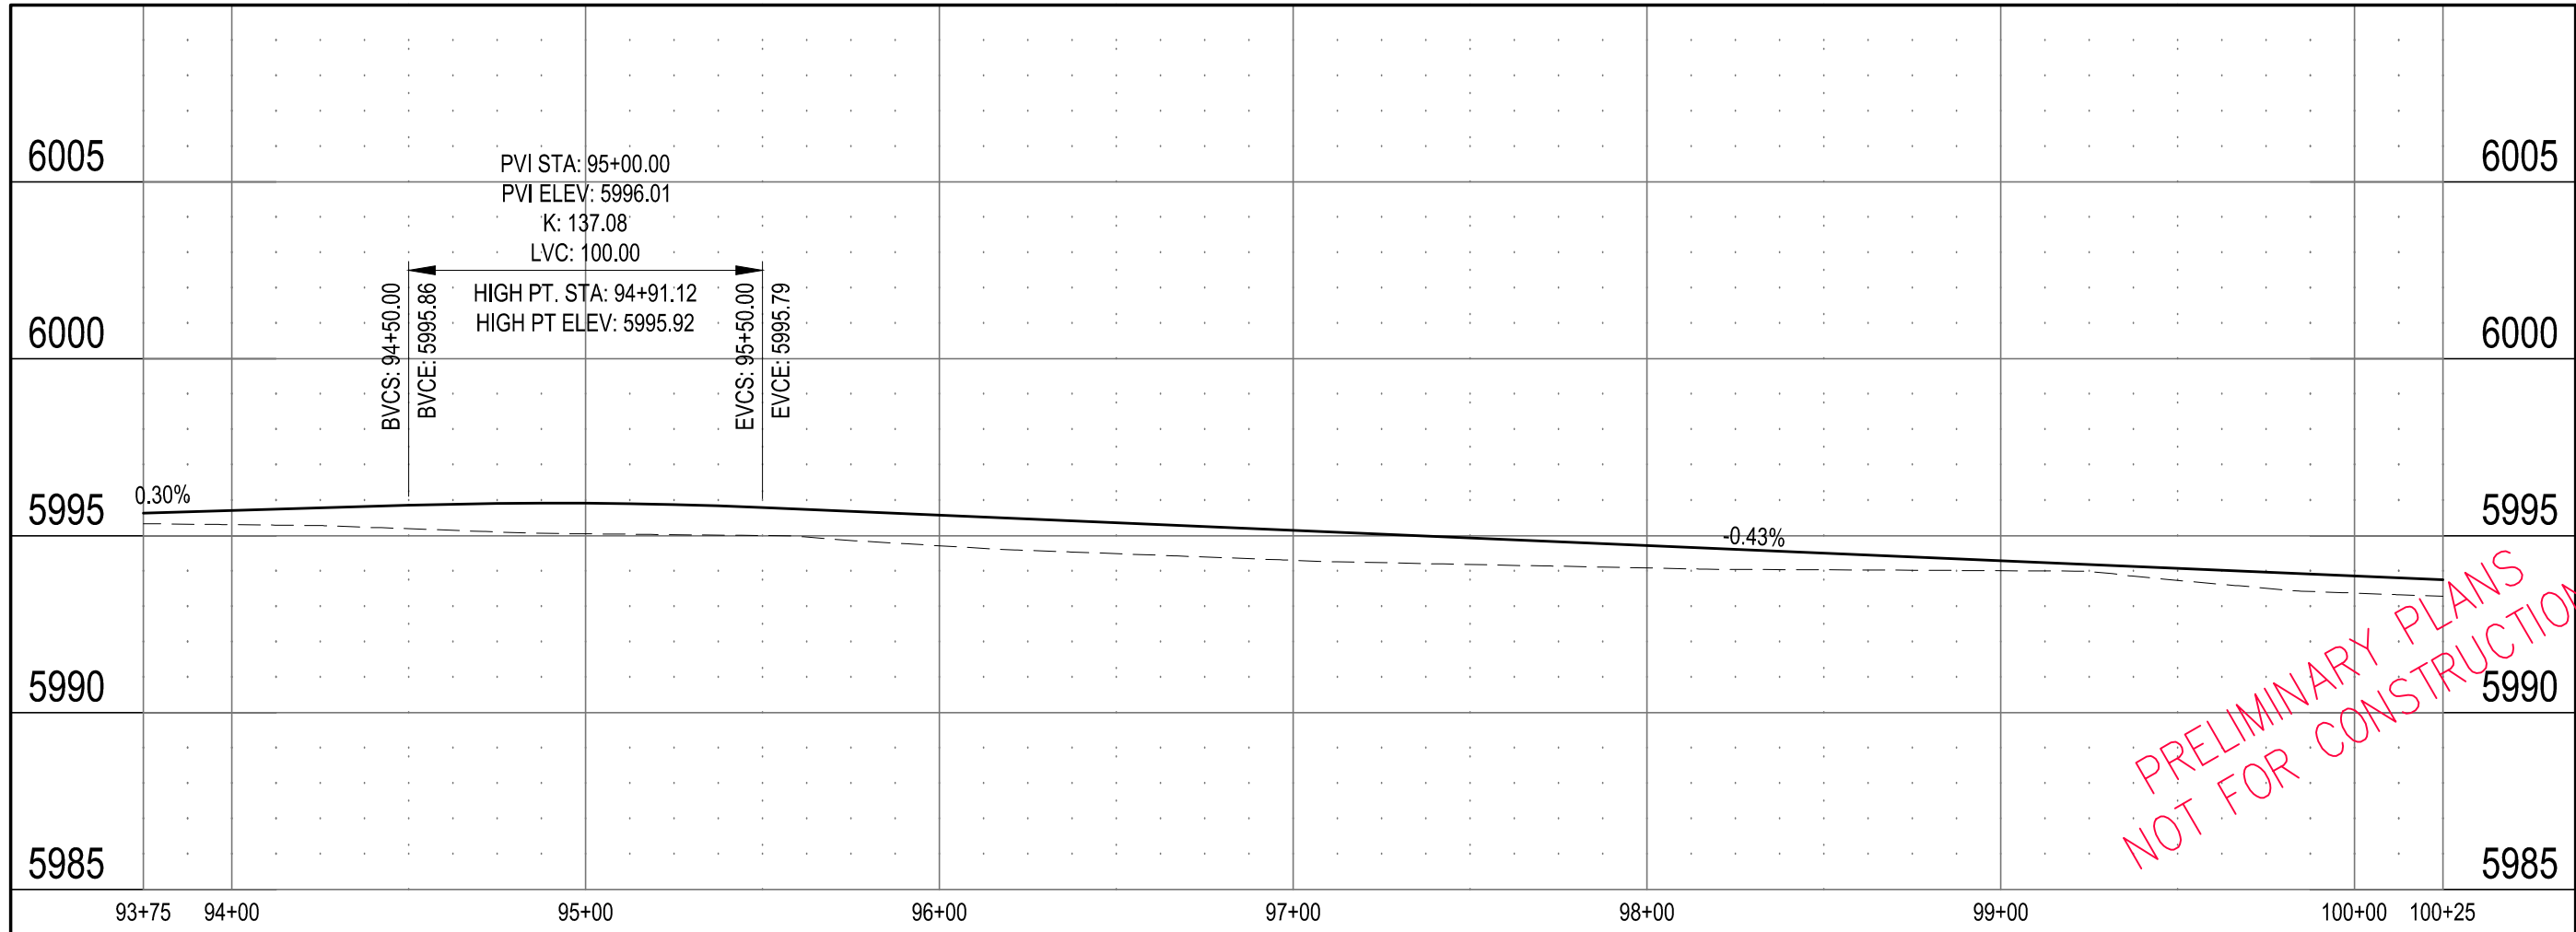

PRELIMINARY PLANS  
NOT FOR CONSTRUCTION

PROJECT: FOX FARM ROAD STREET IMPROVEMENTS  
DRAWING TITLE: FOX FARM RD. PLAN AND PROFILE  
STA. 93+75 - 100+25



avi p.c.  
engineering  
planning  
surveying  
PHONE (307) 637-6017  
1103 OLD TOWN LANE, SUITE 101  
CHEYENNE, WY 82009  
AVI@AVIPC.COM

DATE: 6-20-13  
DRAWN BY: SRL  
DESIGNED BY: TC  
CHECKED BY: TC

JOB NO.: 2-3211-B

ST-16 83  
SHEET NO. OF

H:\3211\design\3211B FOX FARM STREET IMP.dwg Aug 30, 2013 4:14pm jwilson

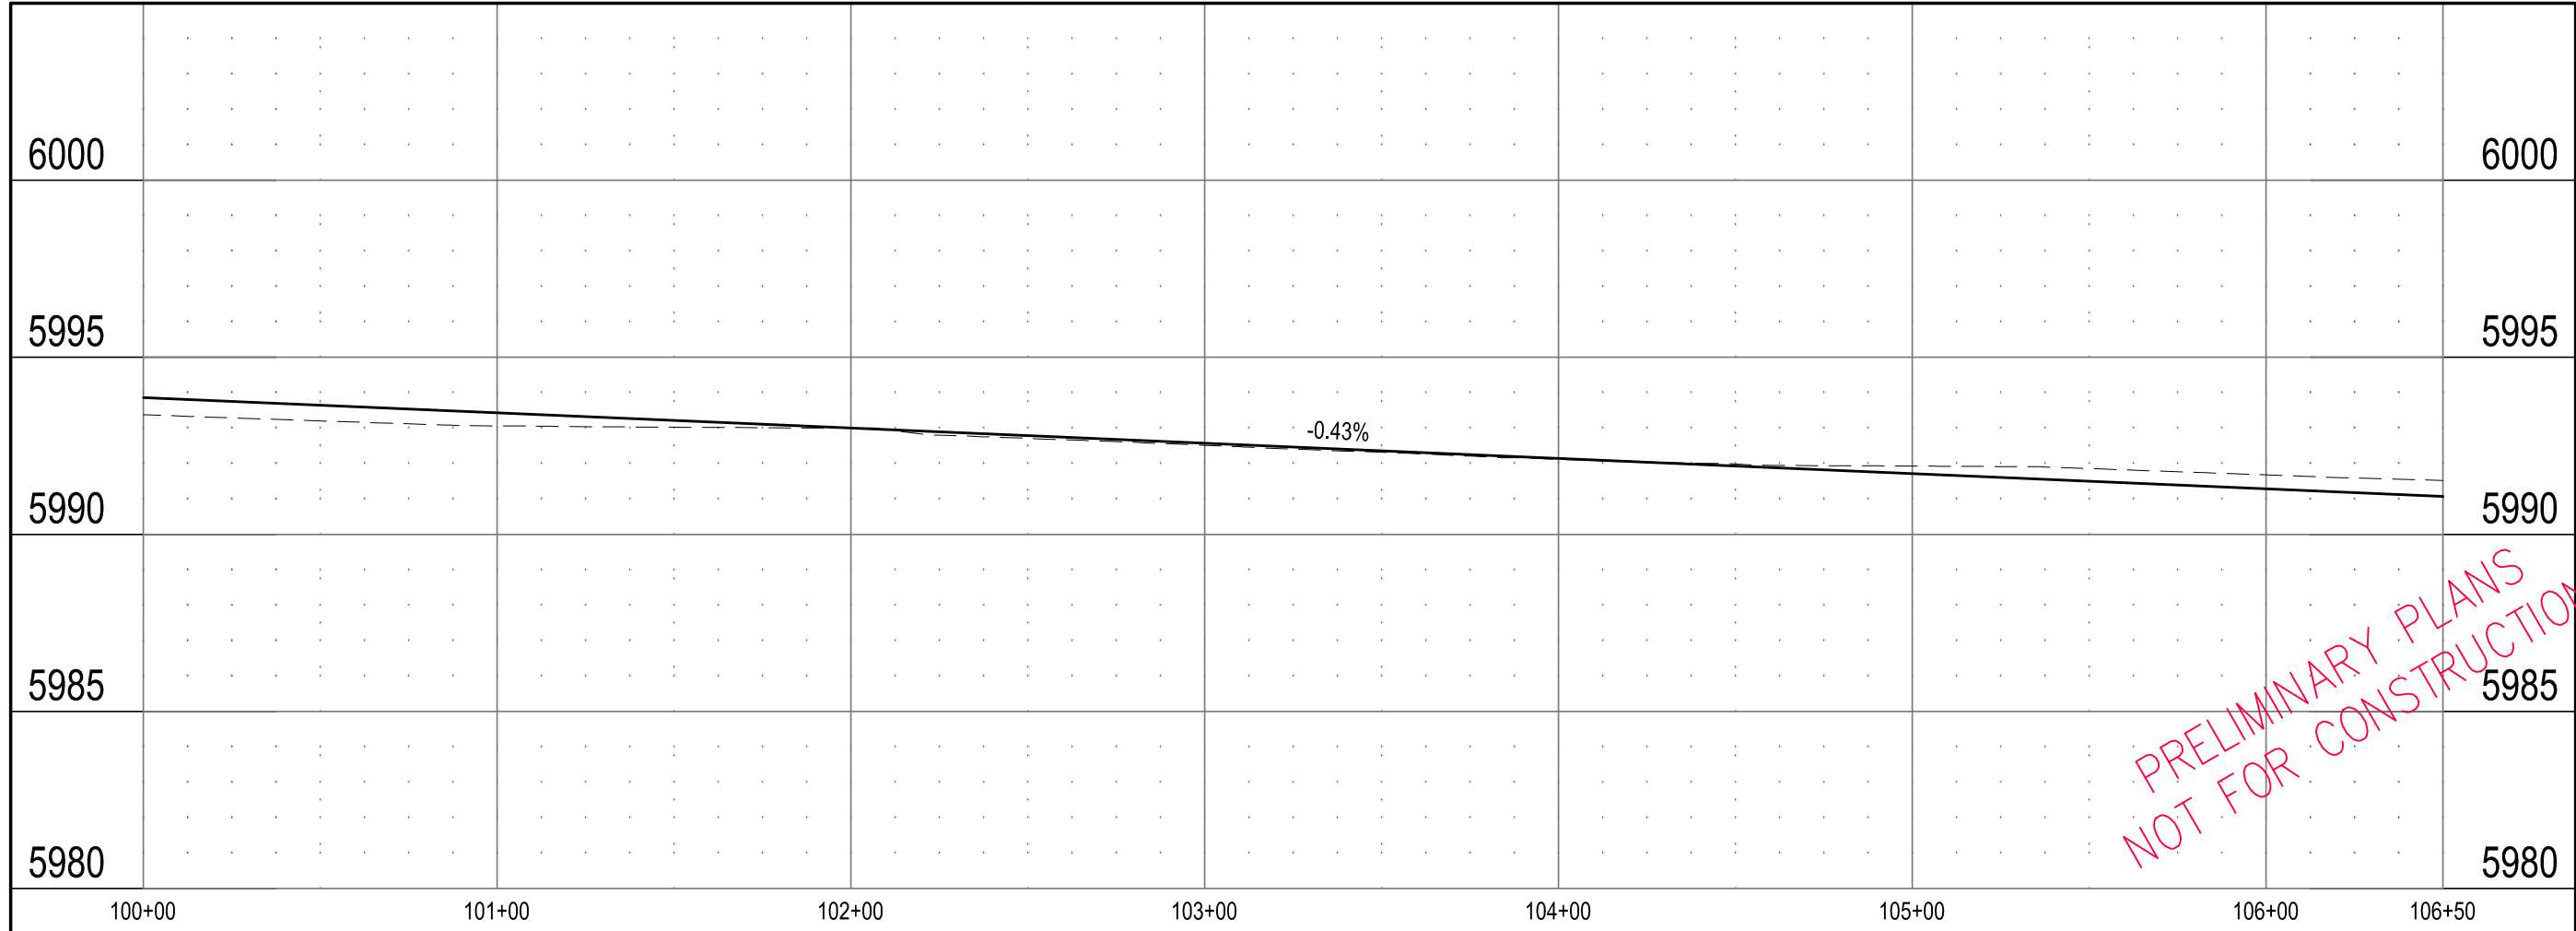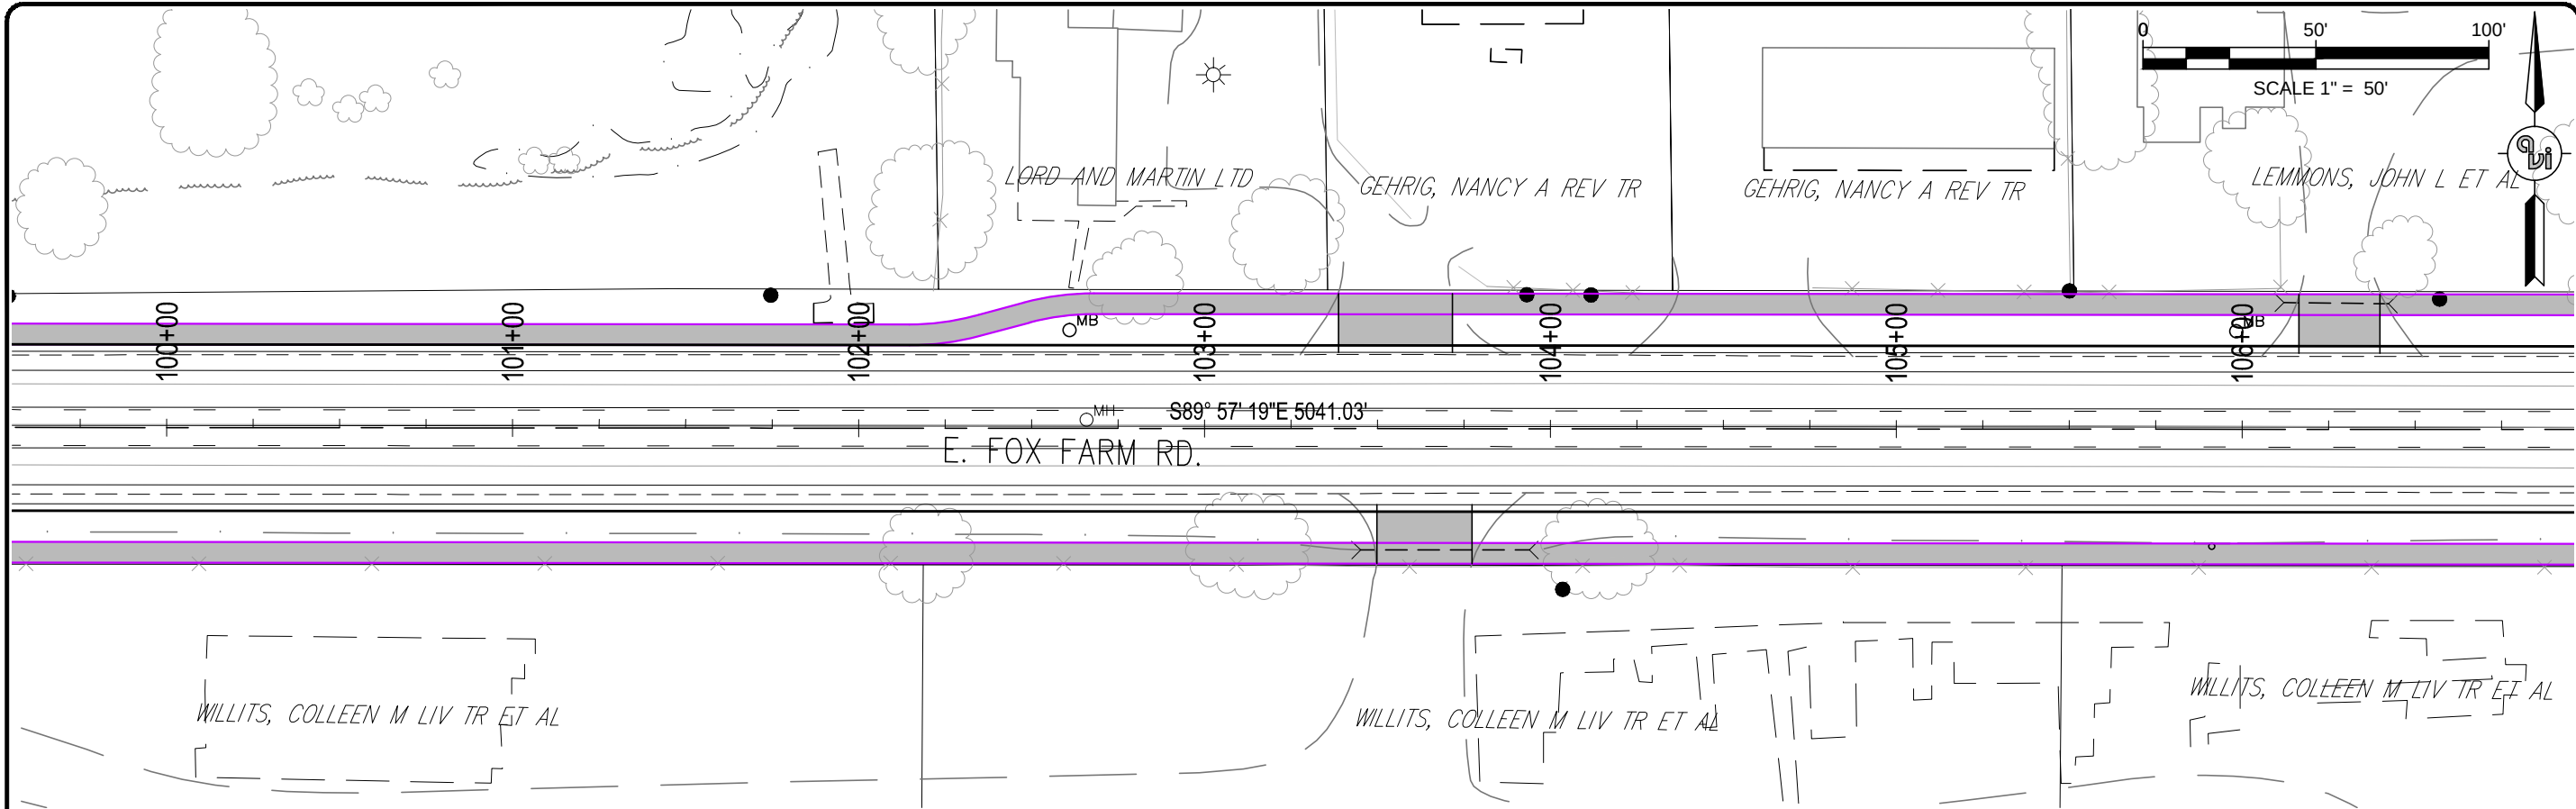

PRELIMINARY PLANS  
NOT FOR CONSTRUCTION

| NO. | REVISION | DATE |
|-----|----------|------|
|     |          |      |
|     |          |      |
|     |          |      |
|     |          |      |

PROJECT: MPO  
2101 O'NEIL AVE.  
RM 205  
CHEYENNE, WY. 82001

PROJECT: FOX FARM ROAD STREET IMPROVEMENTS  
DRAWING TITLE: FOX FARM RD. PLAN AND PROFILE  
STA. 100+00 - 106+50




avi p.c.  
engineering  
planning  
surveying  
PHONE (307) 637-6017  
1103 OLD TOWN LANE, SUITE 101  
CHEYENNE, WY 82009  
AVI@AVIPC.COM

DATE: 6-20-13  
DRAWN BY: SRL  
DESIGNED BY: TC  
CHECKED BY: TC

JOB NO.: 2-3211-B

ST-17 83  
SHEET NO. OF

H:\3211\design\3211B FOX FARM STREET IMP.dwg Aug 30, 2013 4:14pm jwilson

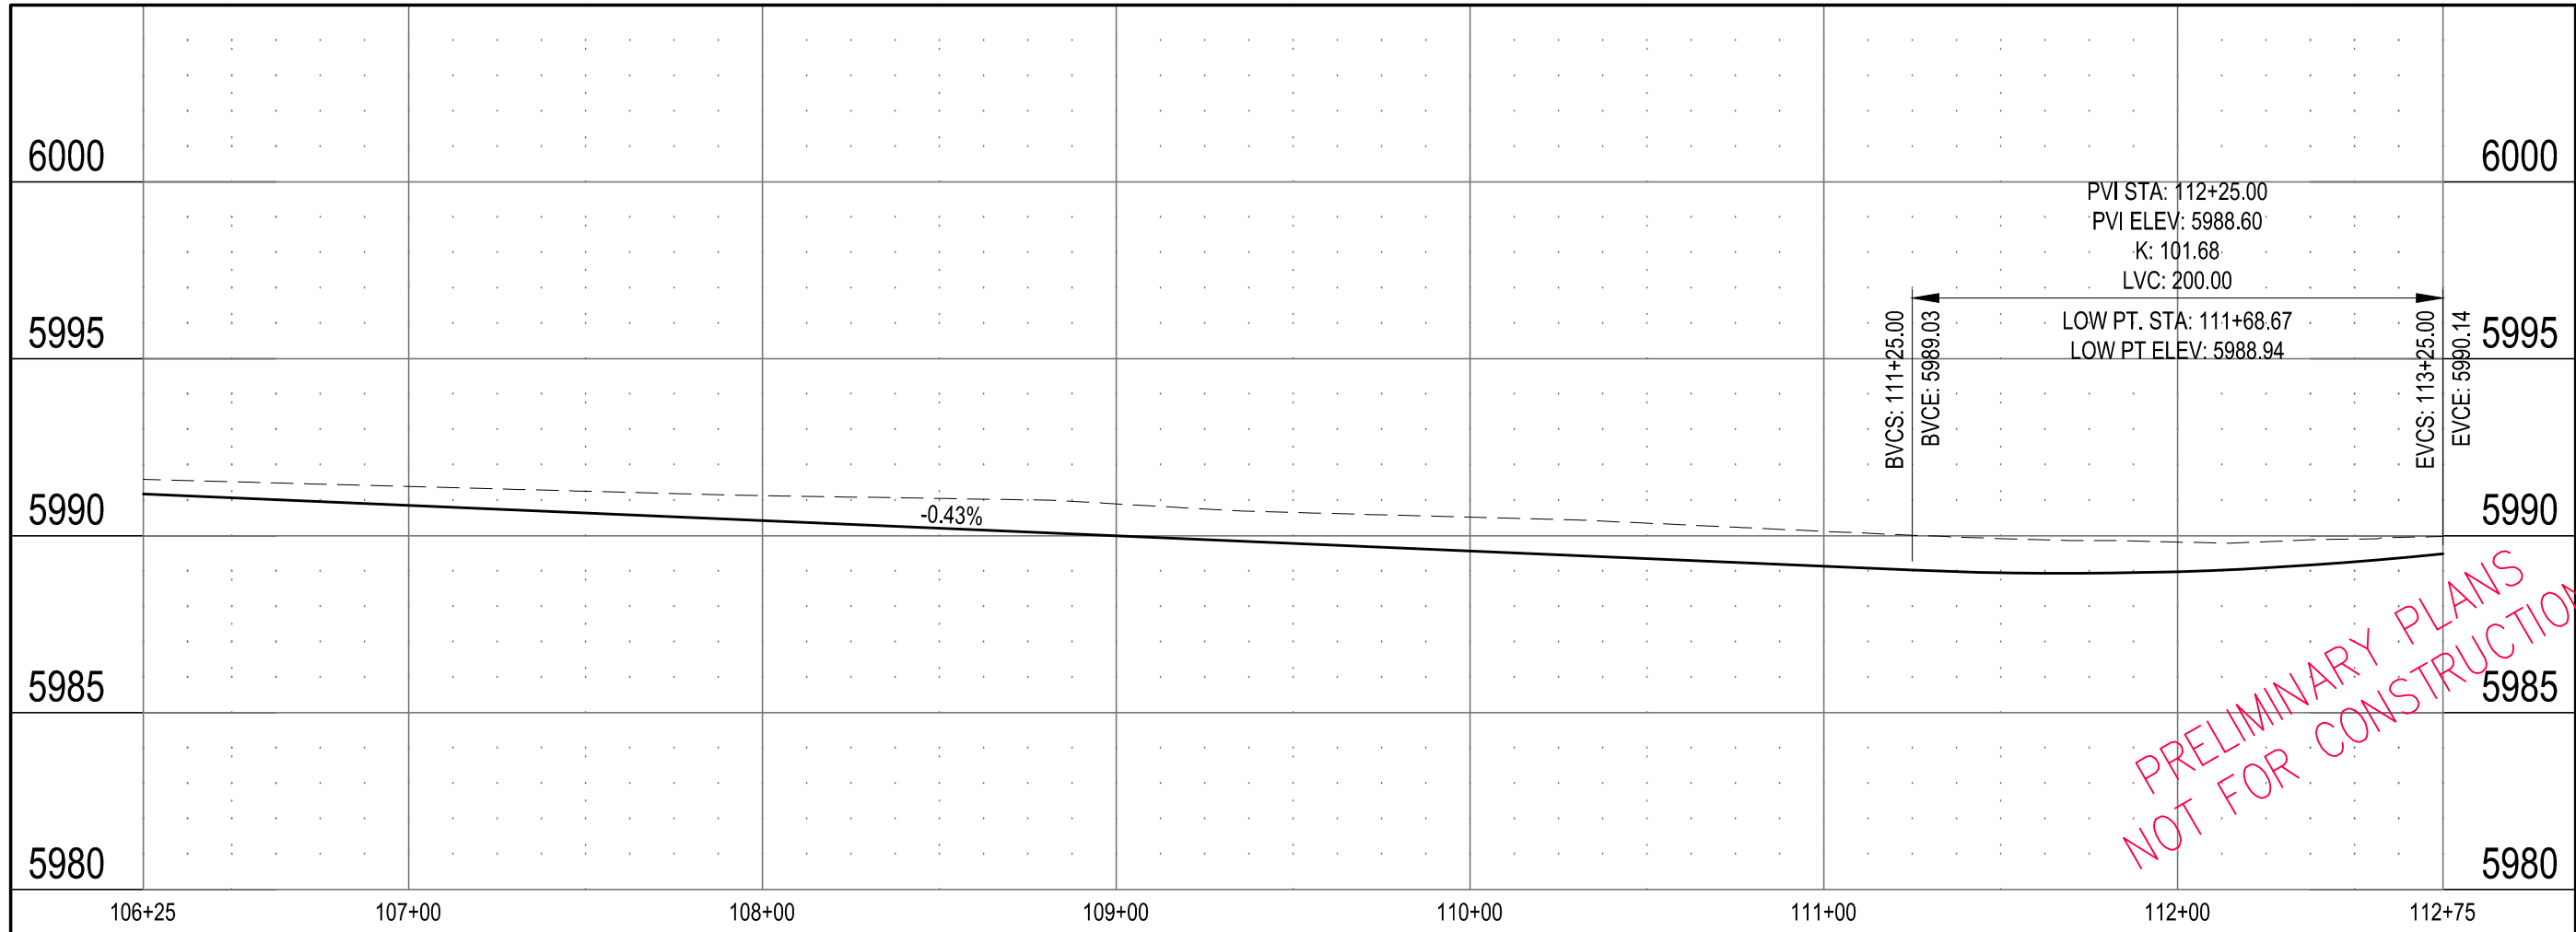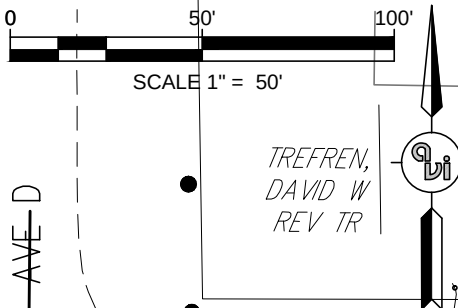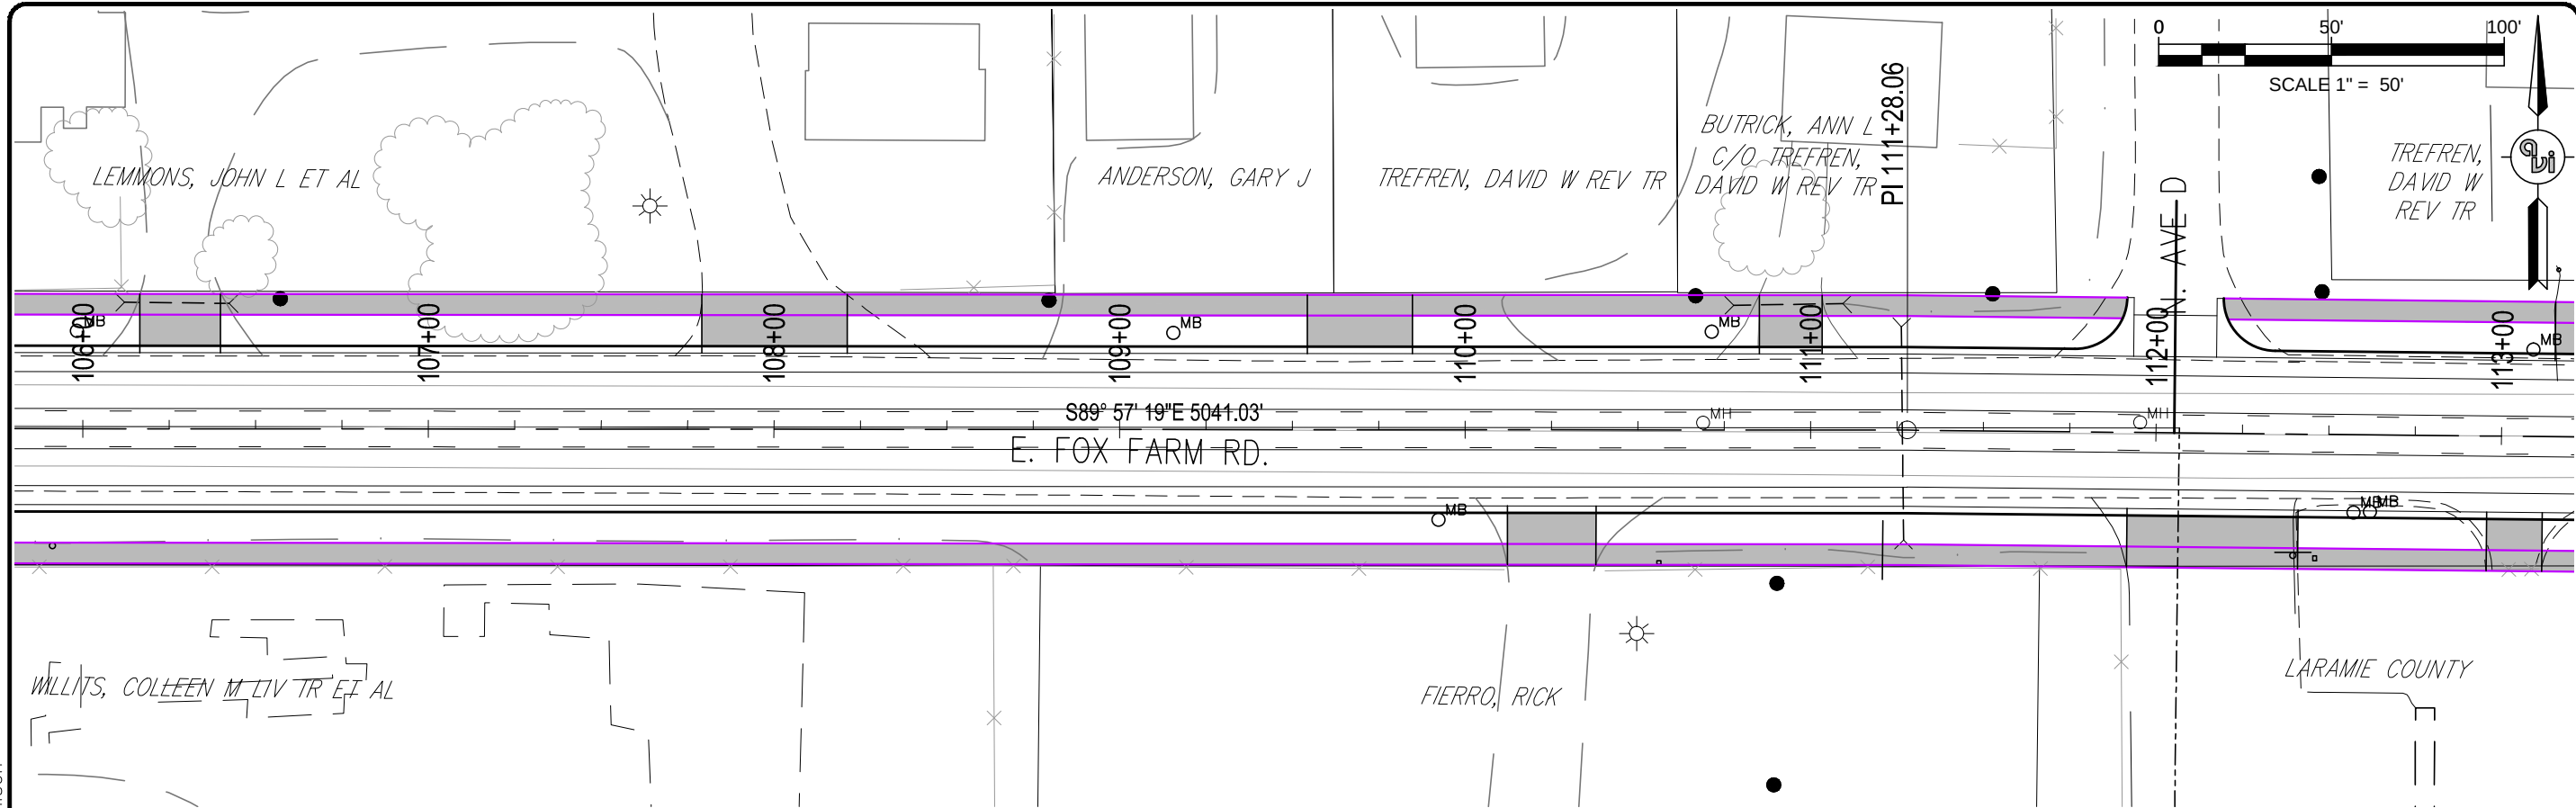

PRELIMINARY PLANS  
NOT FOR CONSTRUCTION

| NO. | REVISION | DATE |
|-----|----------|------|
|     |          |      |
|     |          |      |
|     |          |      |
|     |          |      |

PREPARED FOR:  
MPO  
2101 O'NEIL AVE.  
RM 205  
CHEYENNE, WY. 82001

PROJECT: FOX FARM ROAD STREET IMPROVEMENTS  
DRAWING TITLE: FOX FARM RD. PLAN AND PROFILE  
STA. 106+25 - 112+75



engineering  
planning  
surveying



PHONE (307) 637-6017  
1103 OLD TOWN LANE, SUITE 101  
CHEYENNE, WY 82009  
AVI@AVI.PC.COM

|                    |
|--------------------|
| DATE:<br>6-20-13   |
| DRAWN BY:<br>SRL   |
| DESIGNED BY:<br>TC |
| CHECKED BY:<br>TC  |

JOB NO.:  
2-3211-B

ST-18 83  
SHEET NO. OF

H:\3211\design\3211B FOX FARM STREET IMP.dwg Aug 30, 2013 4:15pm jwilson

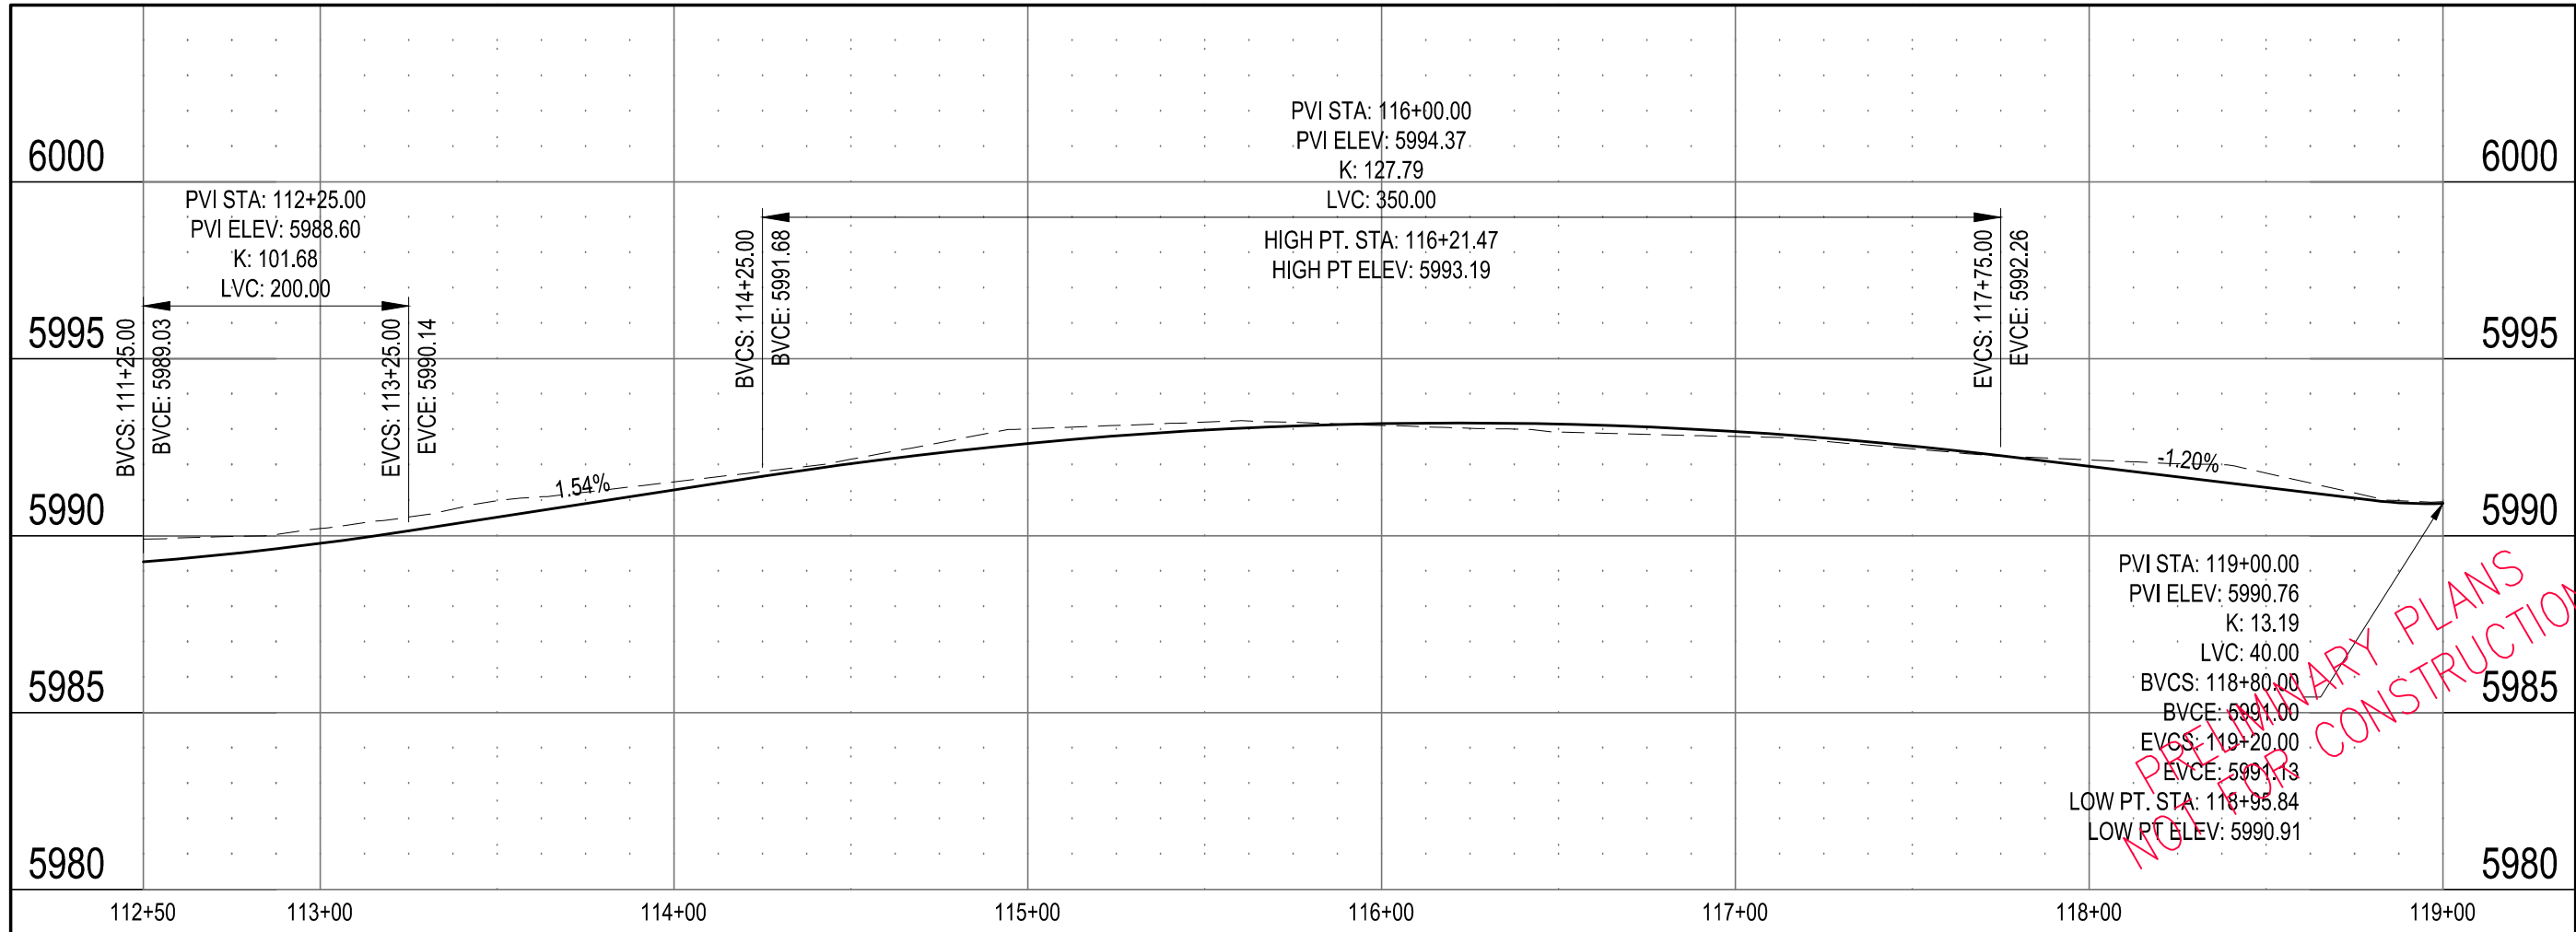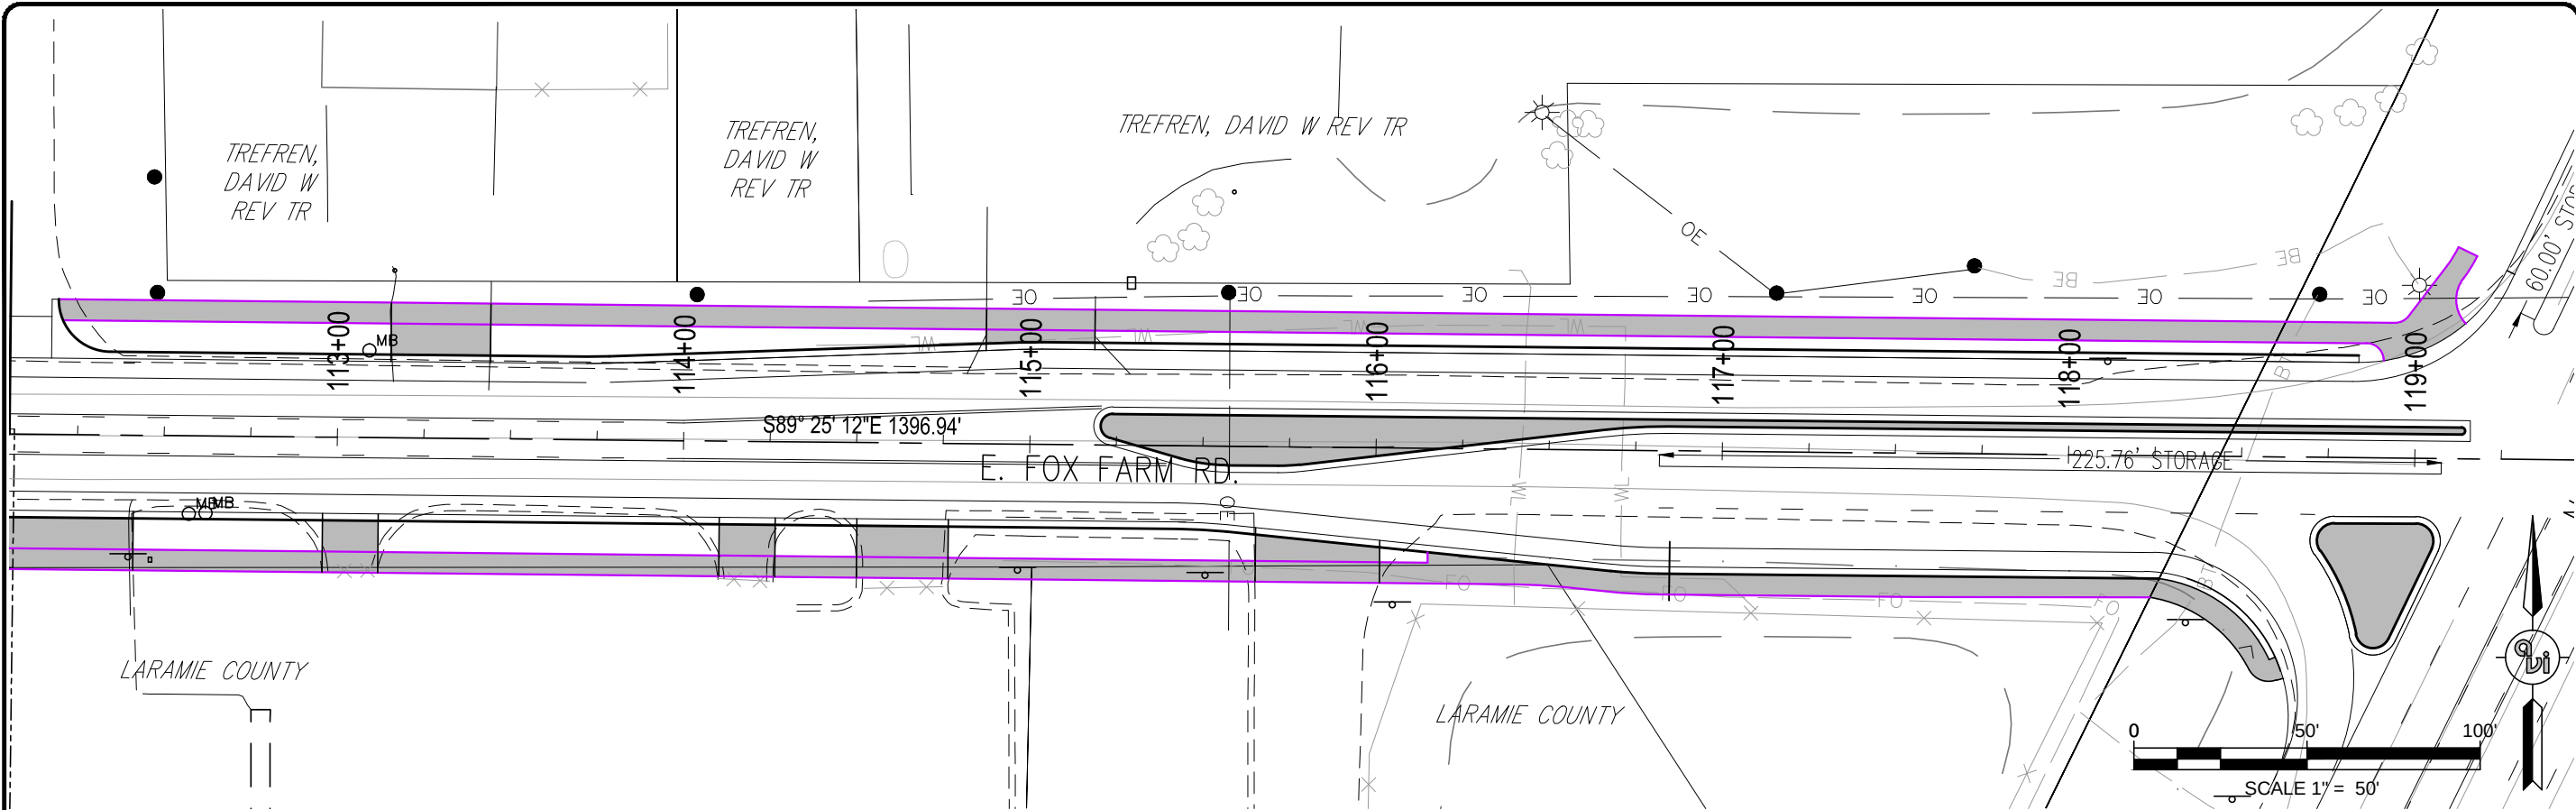

NOT FOR CONSTRUCTION

| NO. | REVISION | DATE |
|-----|----------|------|
|     |          |      |
|     |          |      |
|     |          |      |
|     |          |      |

PREPARED FOR:  
MPO 2101 ONEIL AVE.  
RM 205  
CHEYENNE, WY. 82001

PROJECT: FOX FARM ROAD STREET IMPROVEMENTS

DRAWING TITLE: FOX FARM RD. PLAN AND PROFILE  
STA. 112+50 - 119+00



avi p.c.  
engineering  
planning  
surveying  
PHONE (307) 637-6017  
1103 OLD TOWN LANE, SUITE 101  
CHEYENNE, WY 82009  
AVI@AVIPC.COM

DATE: 6-20-13  
DRAWN BY: SRL  
DESIGNED BY: TC  
CHECKED BY: TC

JOB NO.: 2-3211-B

ST-19 83  
SHEET NO. OF

H:\3211\design\3211B FOX FARM STREET IMP.dwg Aug 30, 2013 4:15pm jwilson

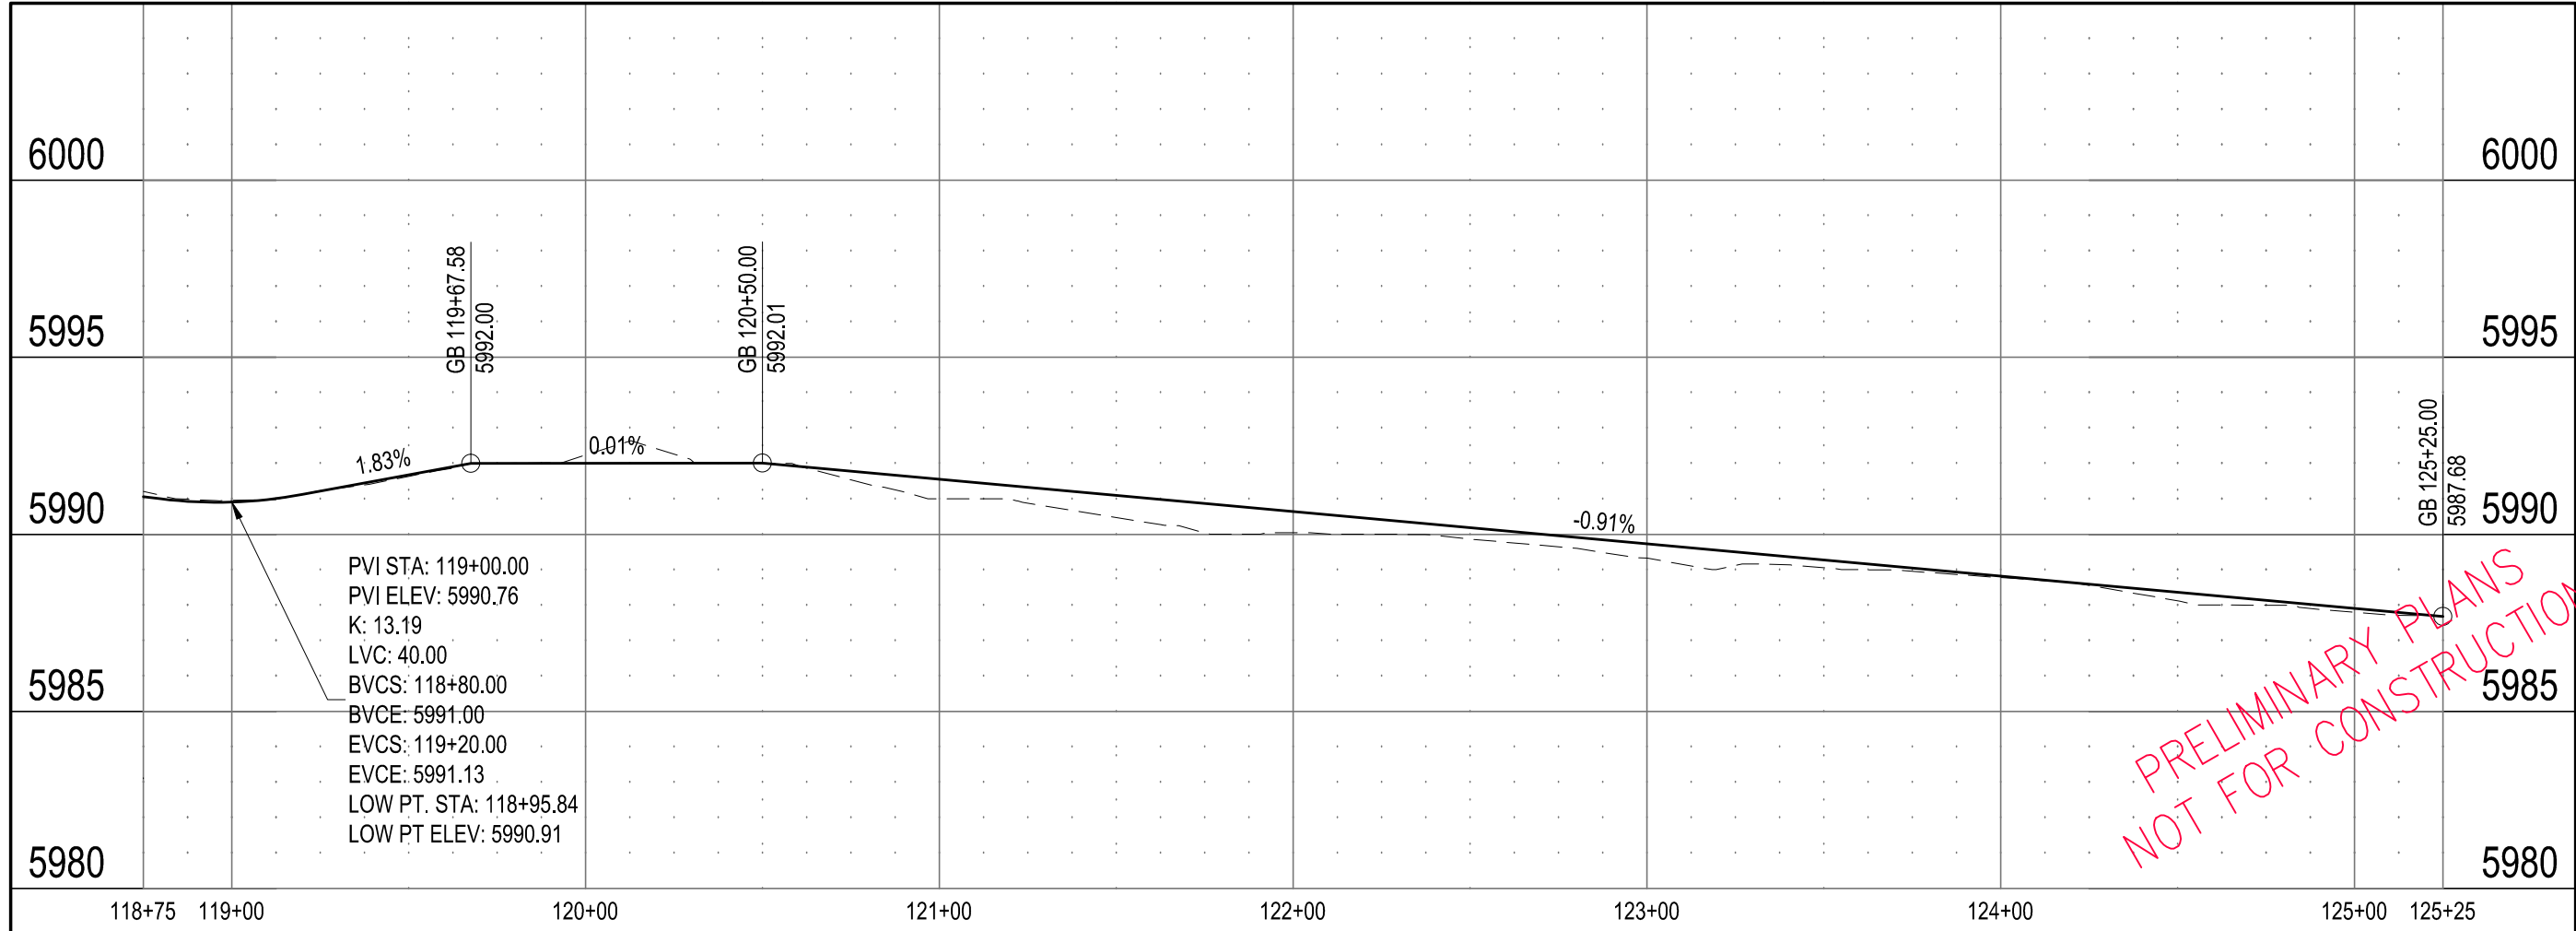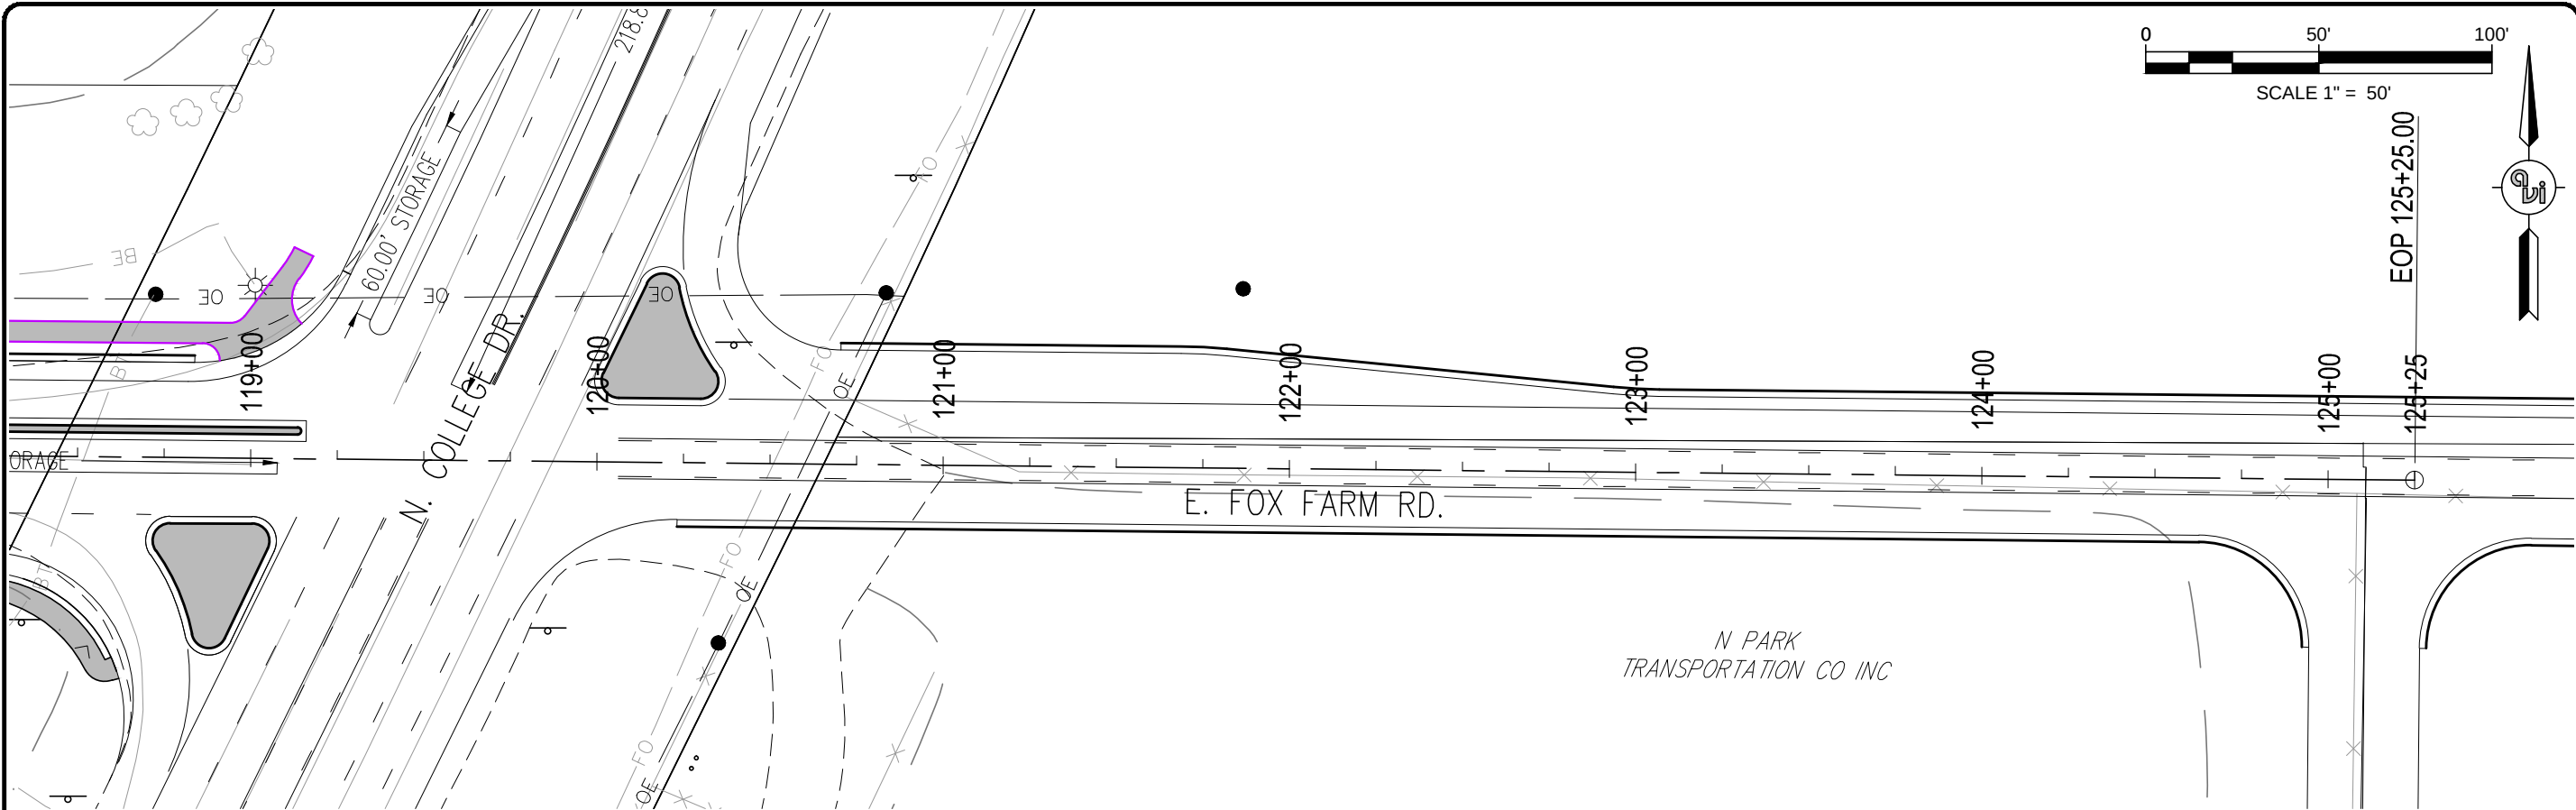

PRELIMINARY PLANS  
NOT FOR CONSTRUCTION

DATE: 6-20-13  
DRAWN BY: SRL  
DESIGNED BY: TC  
CHECKED BY: TC

JOB NO.: 2-3211-B

SHEET NO. 83 OF



PROJECT: FOX FARM ROAD STREET IMPROVEMENTS

DRAWING TITLE: FOX FARM RD. PLAN AND PROFILE  
STA. 118+75 - 125+25

PREPARED FOR: MPO  
2101 ONEIL AVE.  
RM 205  
CHEYENNE, WY. 82001

AVI engineering planning surveying p.c.  
PHONE (307) 637-6017  
1103 OLD TOWN LANE, SUITE 101  
CHEYENNE, WY 82009  
AVI@AVIIPC.COM



| NO. | REVISION | DATE |
|-----|----------|------|
|     |          |      |
|     |          |      |
|     |          |      |
|     |          |      |
|     |          |      |

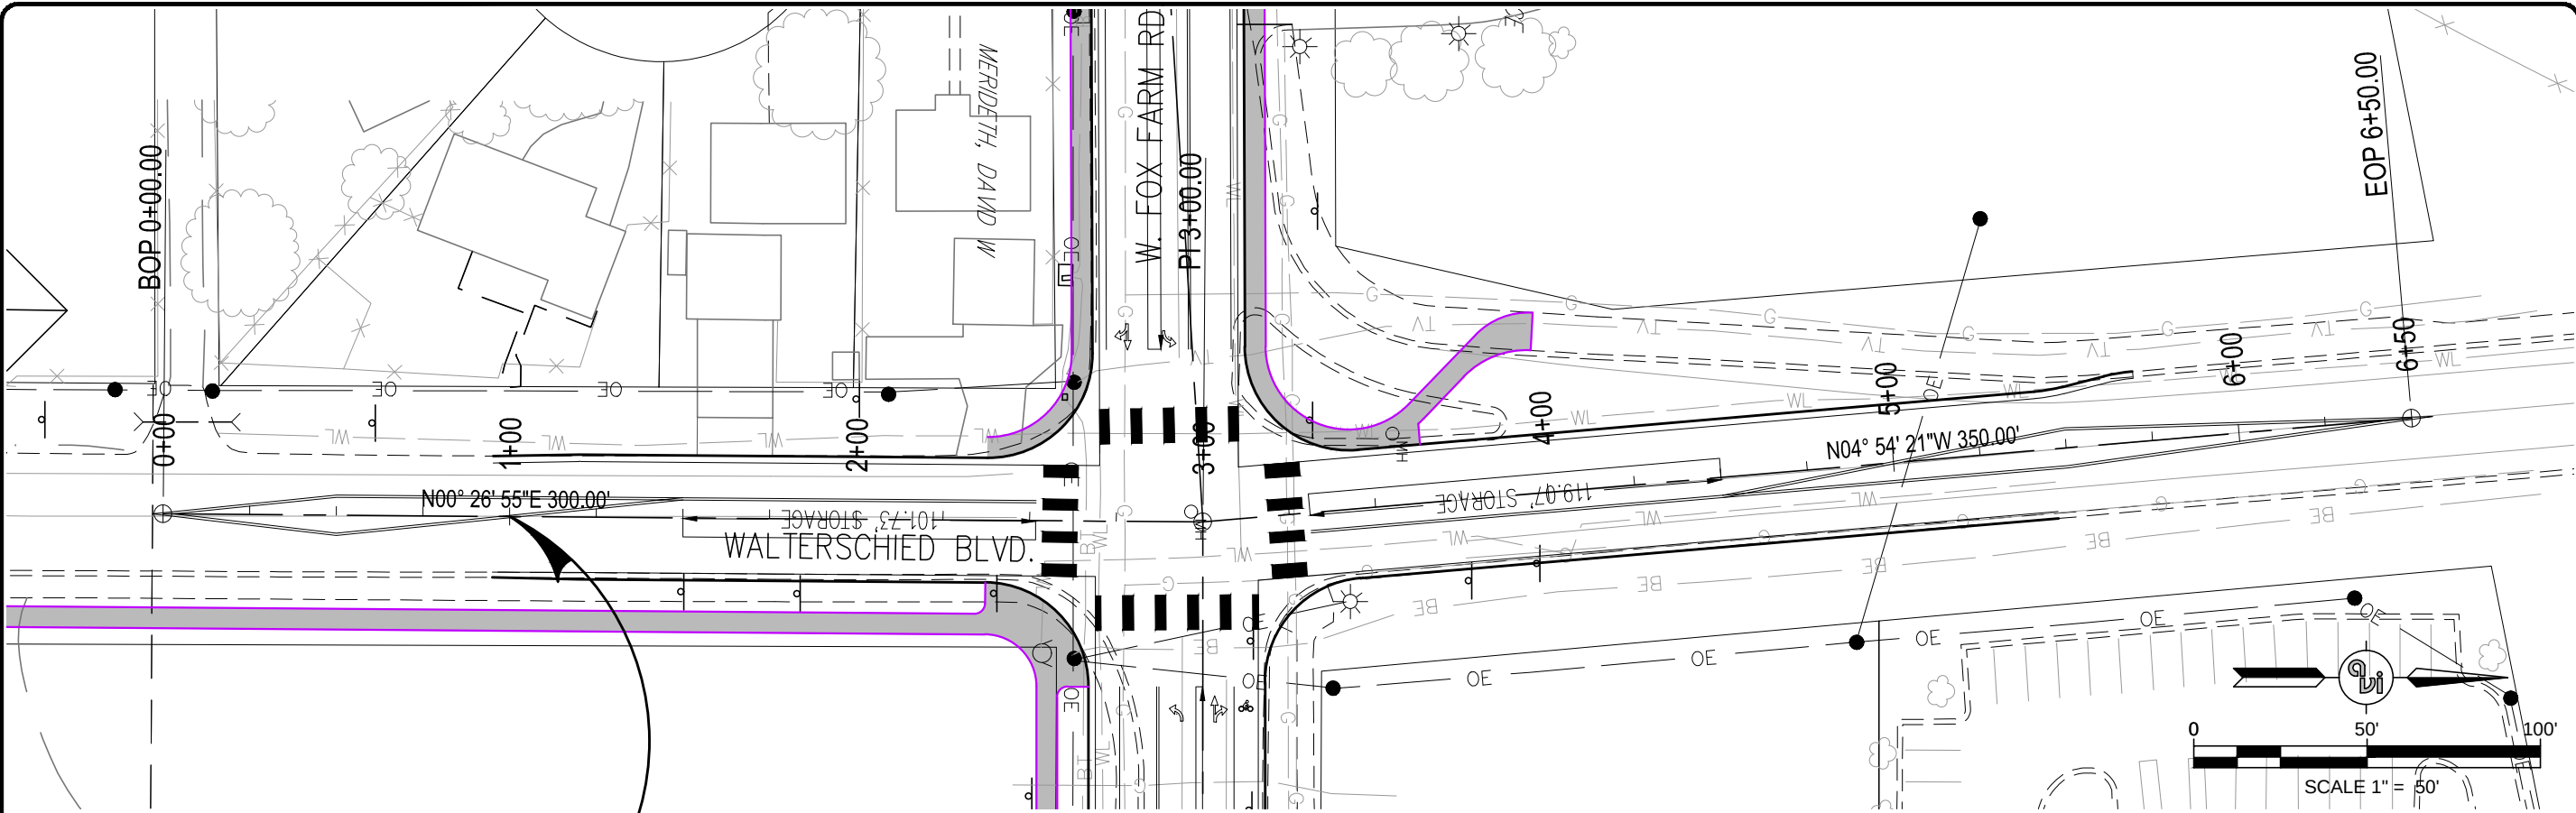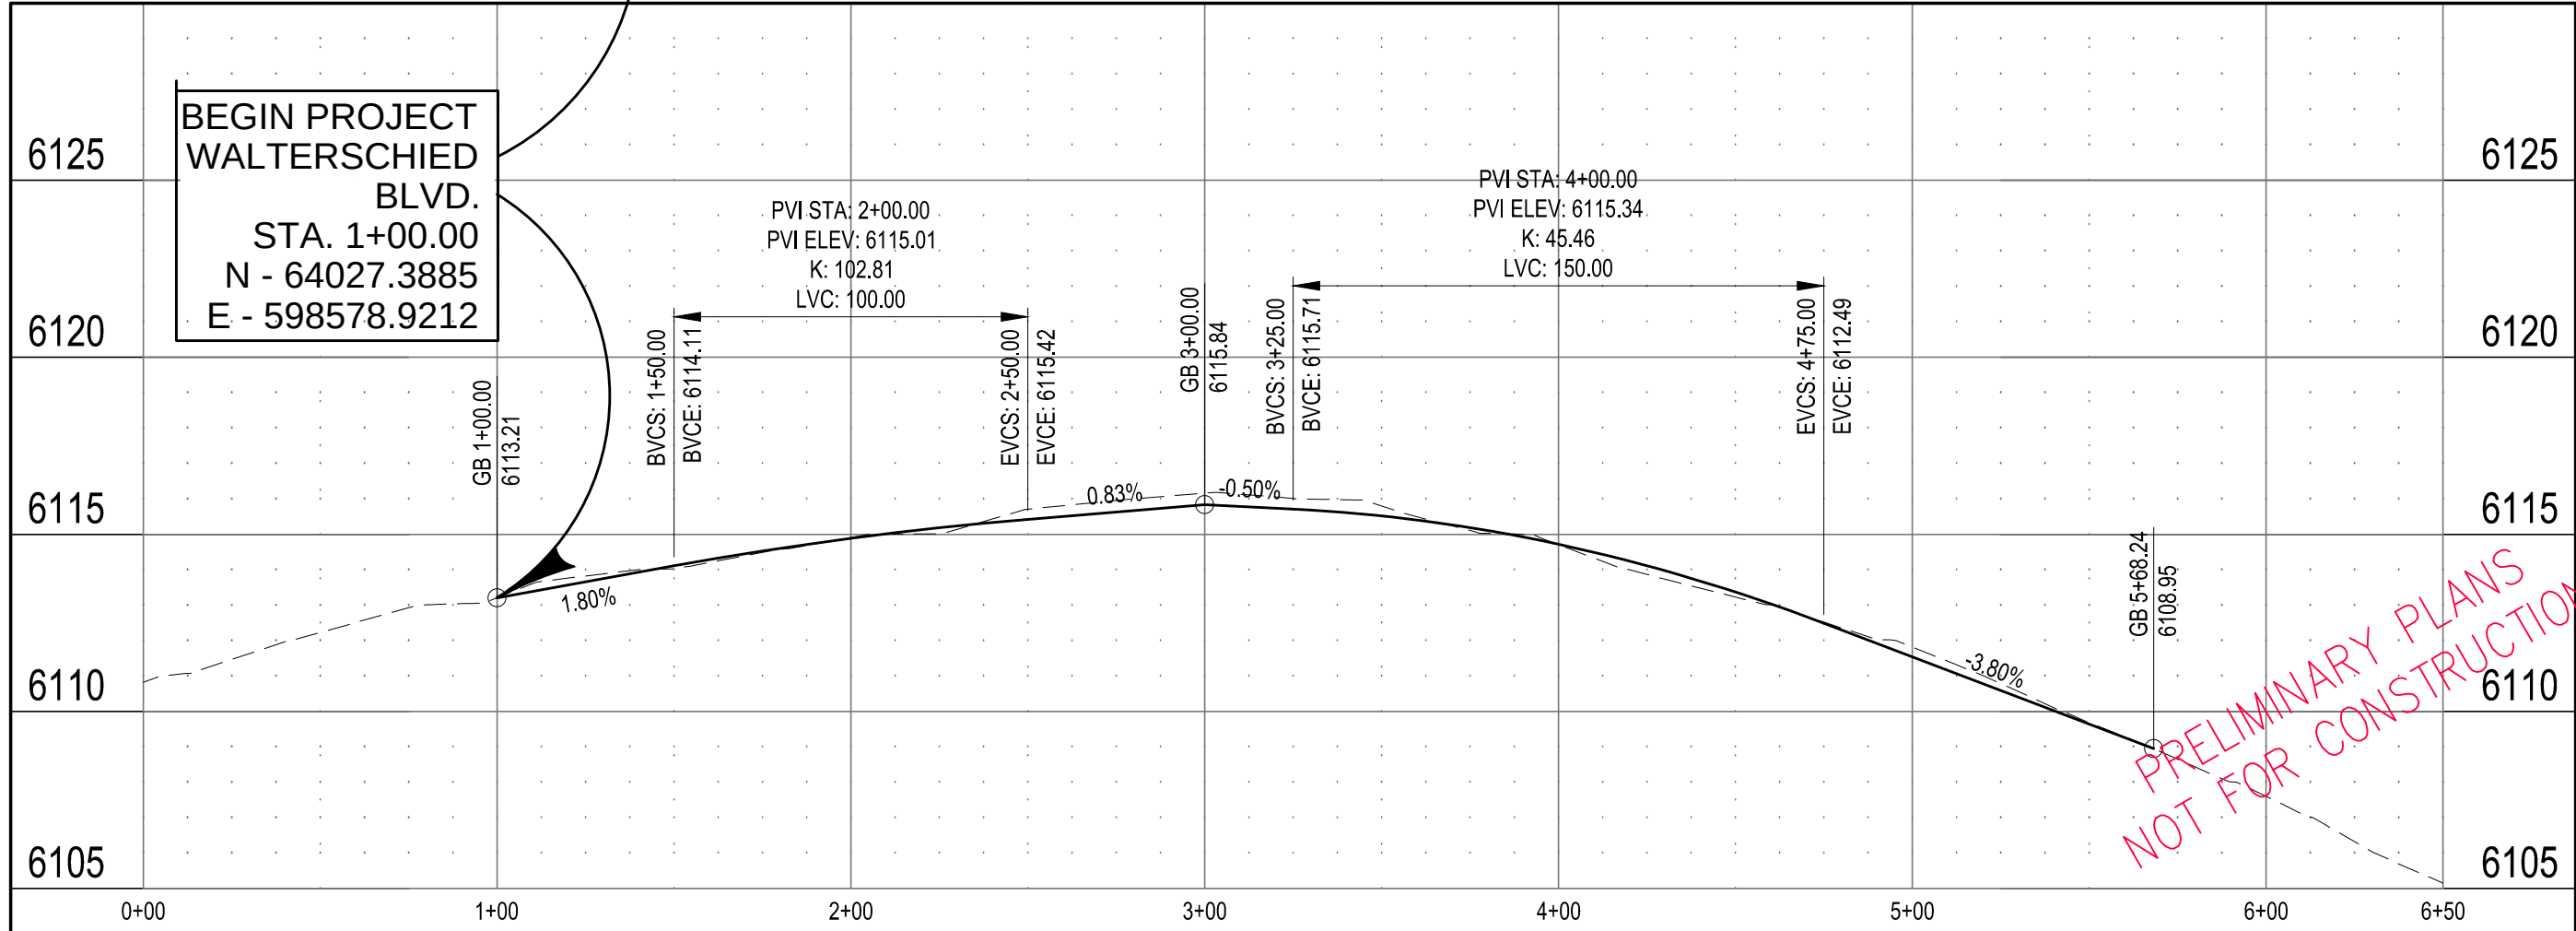

PRELIMINARY PLANS  
NOT FOR CONSTRUCTION

|                                                                    |  |                                                              |  |
|--------------------------------------------------------------------|--|--------------------------------------------------------------|--|
| PROJECT: FOX FARM ROAD STREET IMPROVEMENTS                         |  | PREPARED FOR: MPO 2101 ONEIL AVE. RM 205 CHEYENNE, WY. 82001 |  |
| DRAWING TITLE: WALTERSCHIED BLVD. PLAN AND PROFILE STA. 0+00 - 650 |  | DATE: _____                                                  |  |
| DATE: 6-20-13                                                      |  | REVISION: _____                                              |  |
| DRAWN BY: SRL                                                      |  | NO.: _____                                                   |  |
| DESIGNED BY: TC                                                    |  | DATE: _____                                                  |  |
| CHECKED BY: TC                                                     |  | NO.: _____                                                   |  |
| JOB NO.: 2-3211-B                                                  |  | NO.: _____                                                   |  |
| SHEET NO. 83                                                       |  | NO.: _____                                                   |  |
| OF                                                                 |  | NO.: _____                                                   |  |

H:\3211\design\3211B FOX FARM STREET IMP.dwg Aug 30, 2013 4:16pm jwilson

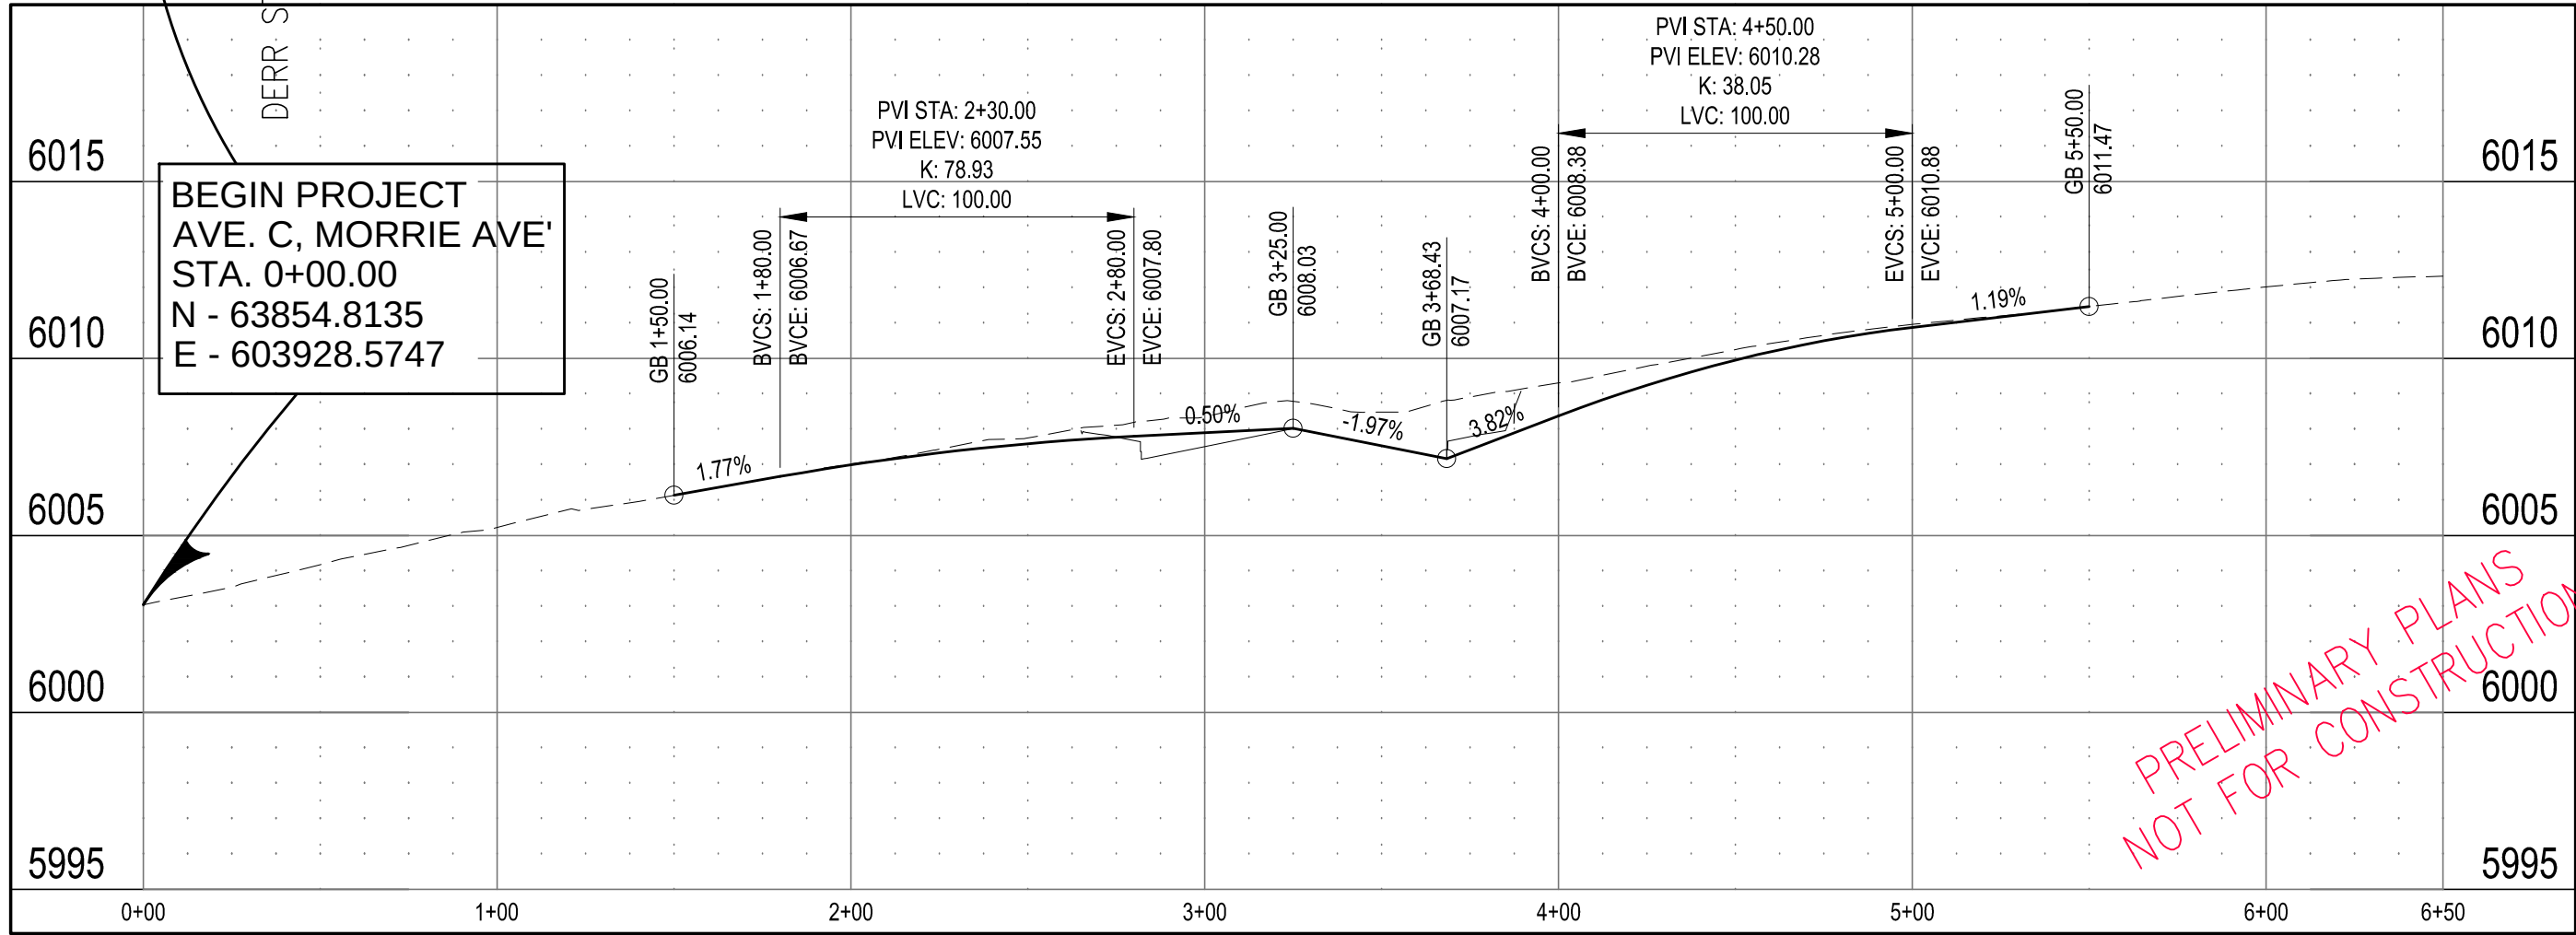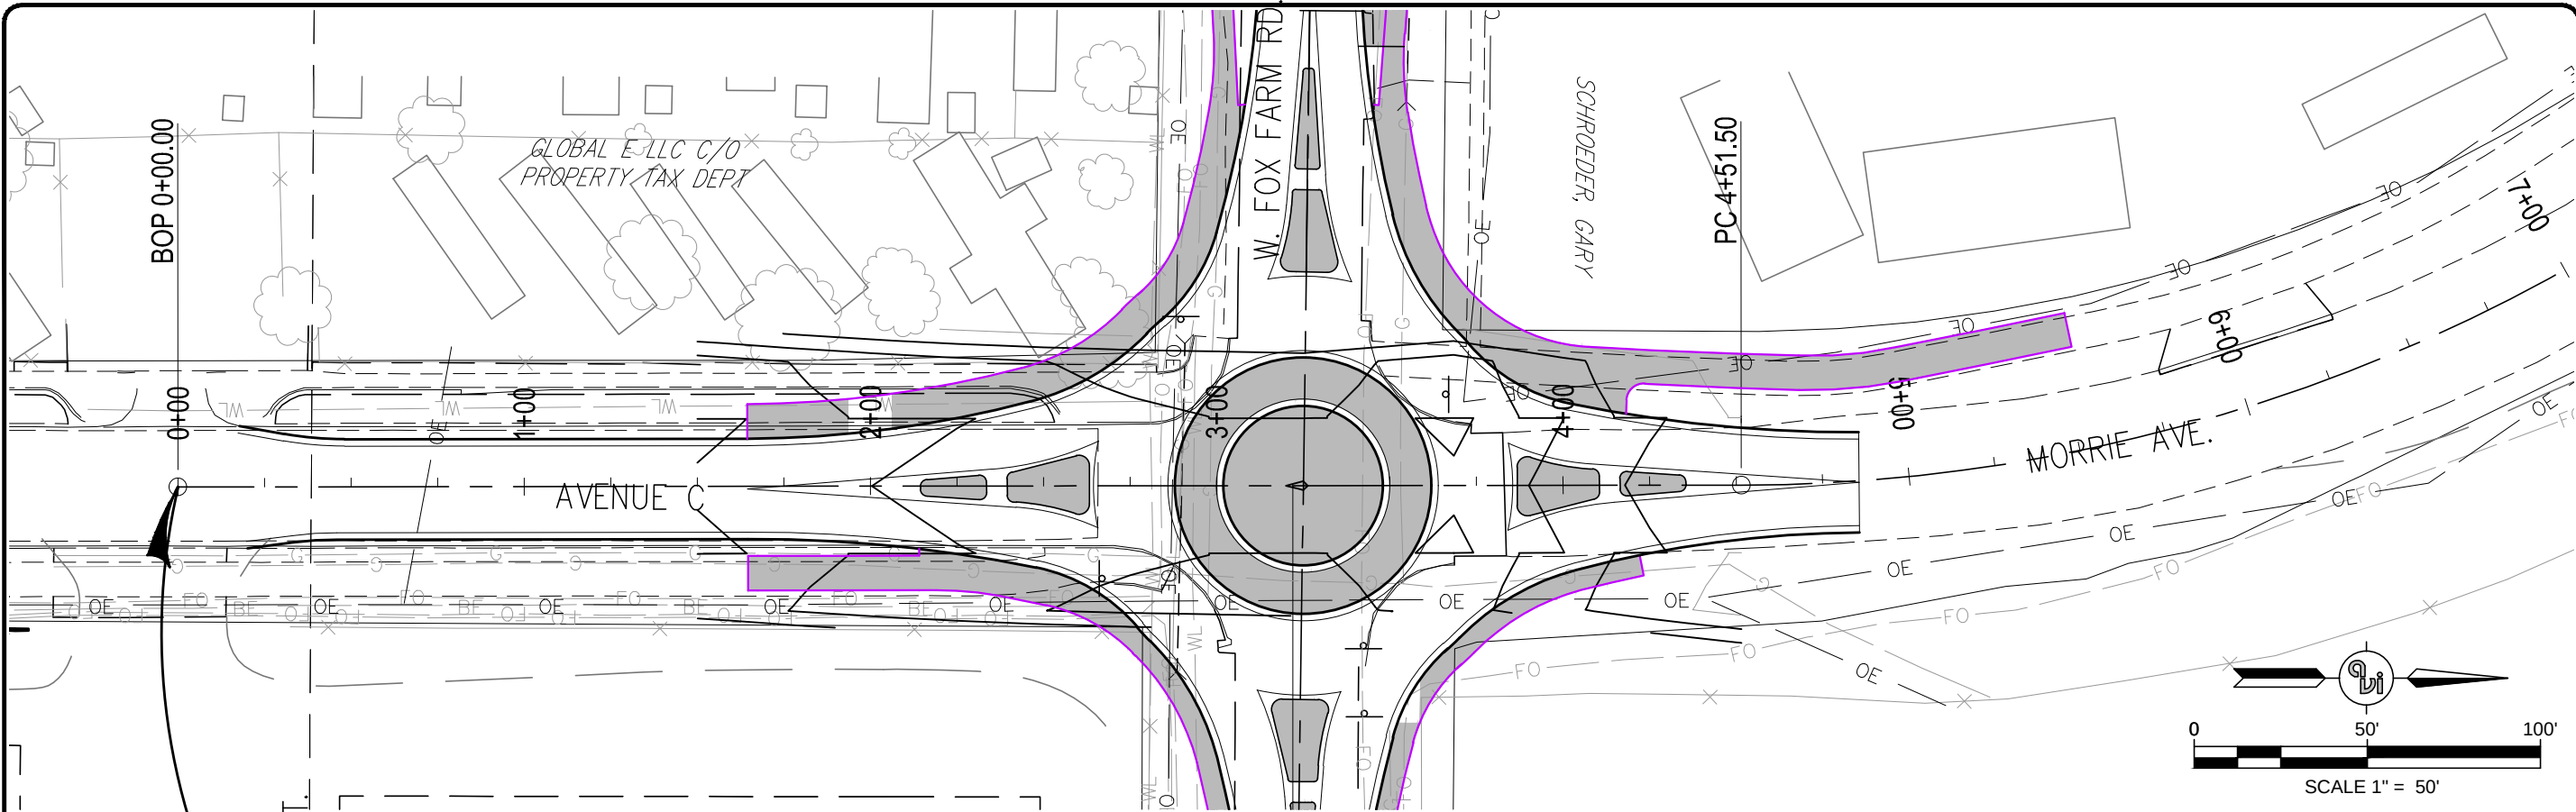

PRELIMINARY PLANS  
NOT FOR CONSTRUCTION

|     |          |      |
|-----|----------|------|
| NO. | REVISION | DATE |
|     |          |      |

PREPARED FOR:  
MPO 2101 ONEIL AVE.  
RM 205  
CHEYENNE, WY. 82001

PROJECT: FOX FARM ROAD STREET IMPROVEMENTS


DRAWING TITLE: AVENUE C PLAN AND PROFILE STA. 0+00 - 6+50

**avi** p.c.  
engineering planning surveying  
PHONE (307) 637-6017  
1103 OLD TOWN LANE, SUITE 101  
CHEYENNE, WY 82009  
AVI@AVIPC.COM

DATE: 6-20-13  
DRAWN BY: SRL  
DESIGNED BY: TC  
CHECKED BY: TC

JOB NO.: 2-3211-B

SHEET NO. 83 OF

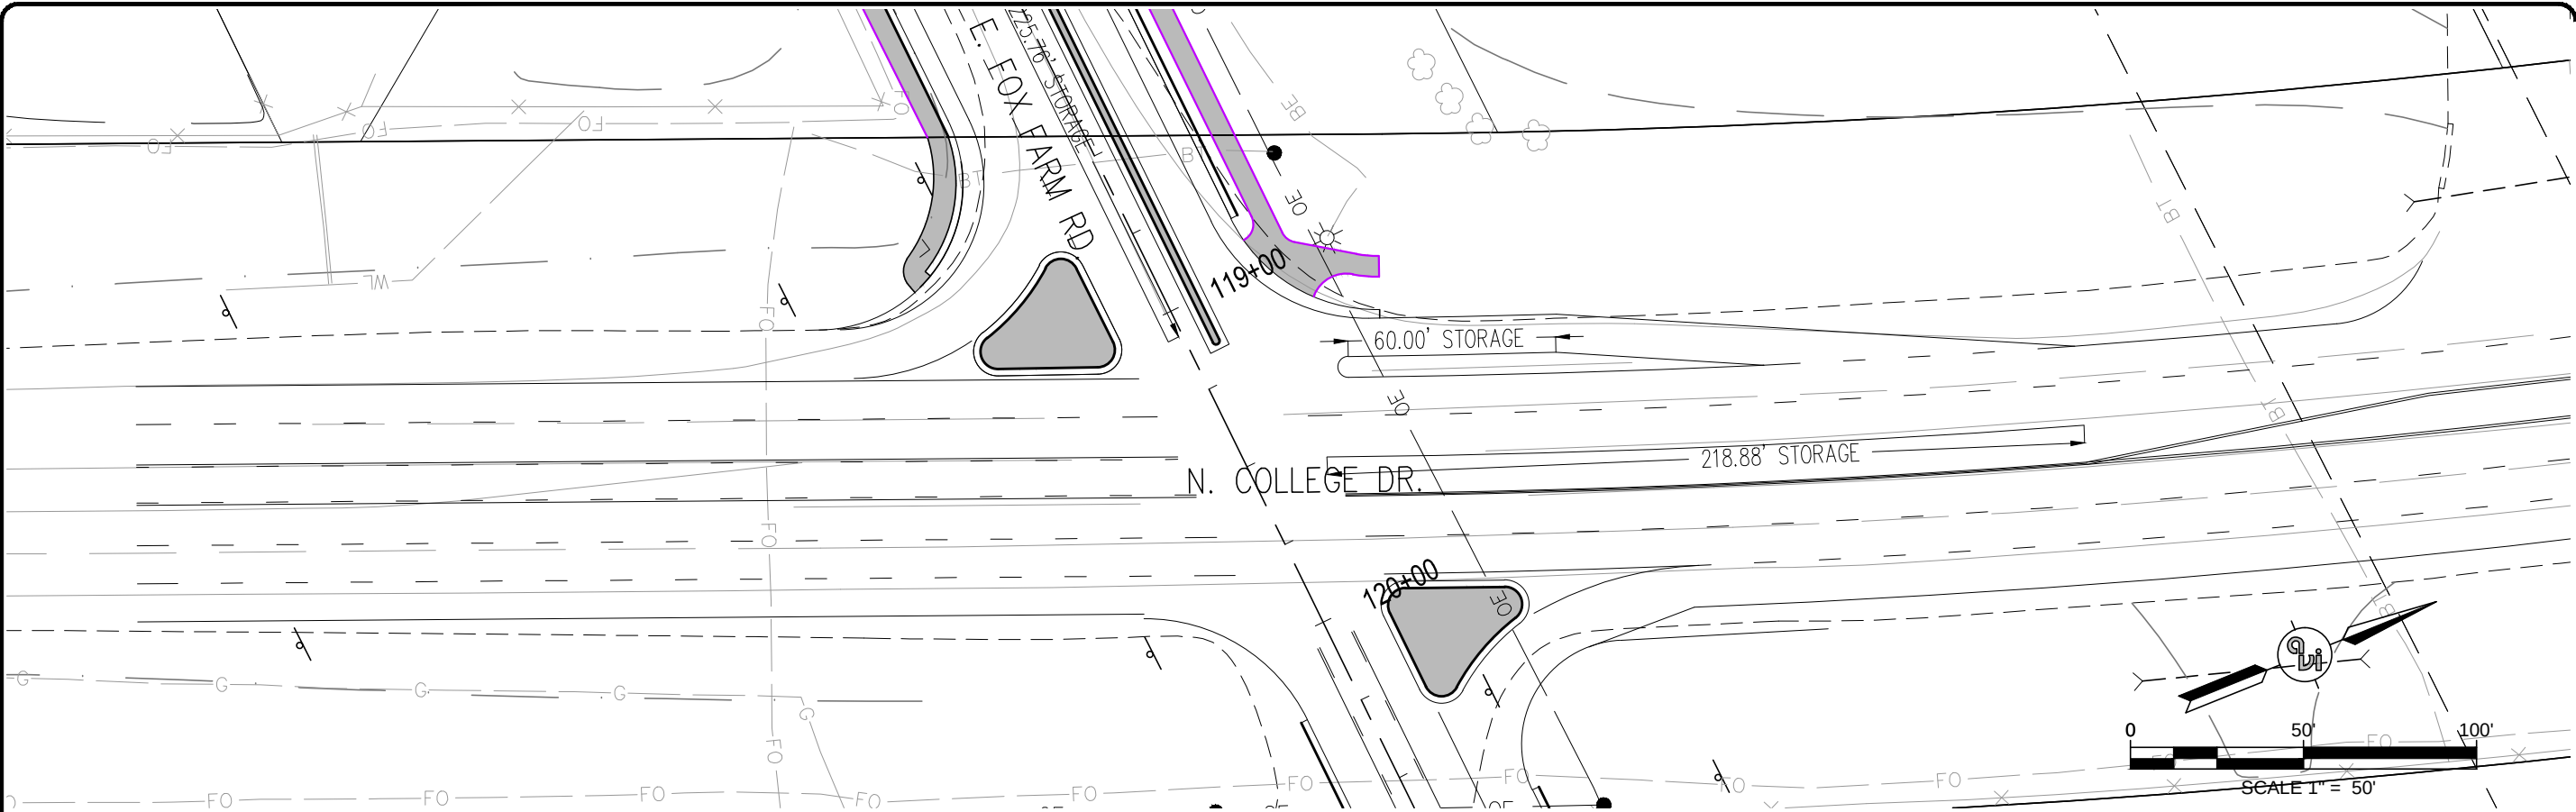



PRELIMINARY PLANS  
NOT FOR CONSTRUCTION

|                |              |                                                         |          |
|----------------|--------------|---------------------------------------------------------|----------|
| PROJECT:       |              | FOX FARM ROAD STREET IMPROVEMENTS                       |          |
| DRAWING TITLE: |              | COLLEGE DRIVE PLAN                                      |          |
| PREPARED FOR:  |              | MPO<br>2101 ONEIL AVE.<br>RM 205<br>CHEYENNE, WY. 82001 |          |
| DATE:          | REVISION     | NO.                                                     |          |
| 6-20-13        |              |                                                         |          |
| DRAWN BY:      | DESIGNED BY: | CHECKED BY:                                             | JOB NO.: |
| SRL            | TC           | TC                                                      | 2-3211-B |
| ST-23          |              | 83                                                      |          |
| SHEET NO.      |              | OF                                                      |          |

**avi** p.c.  
engineering  
planning  
surveying

PHONE (307) 637-6017  
1103 OLD TOWN LANE, SUITE 101  
CHEYENNE, WY 82009  
AVI@AVIFC.COM

H:\3211\design\3211B FOX FARM STREET IMP.dwg Aug 30, 2013 4:17pm jwilson

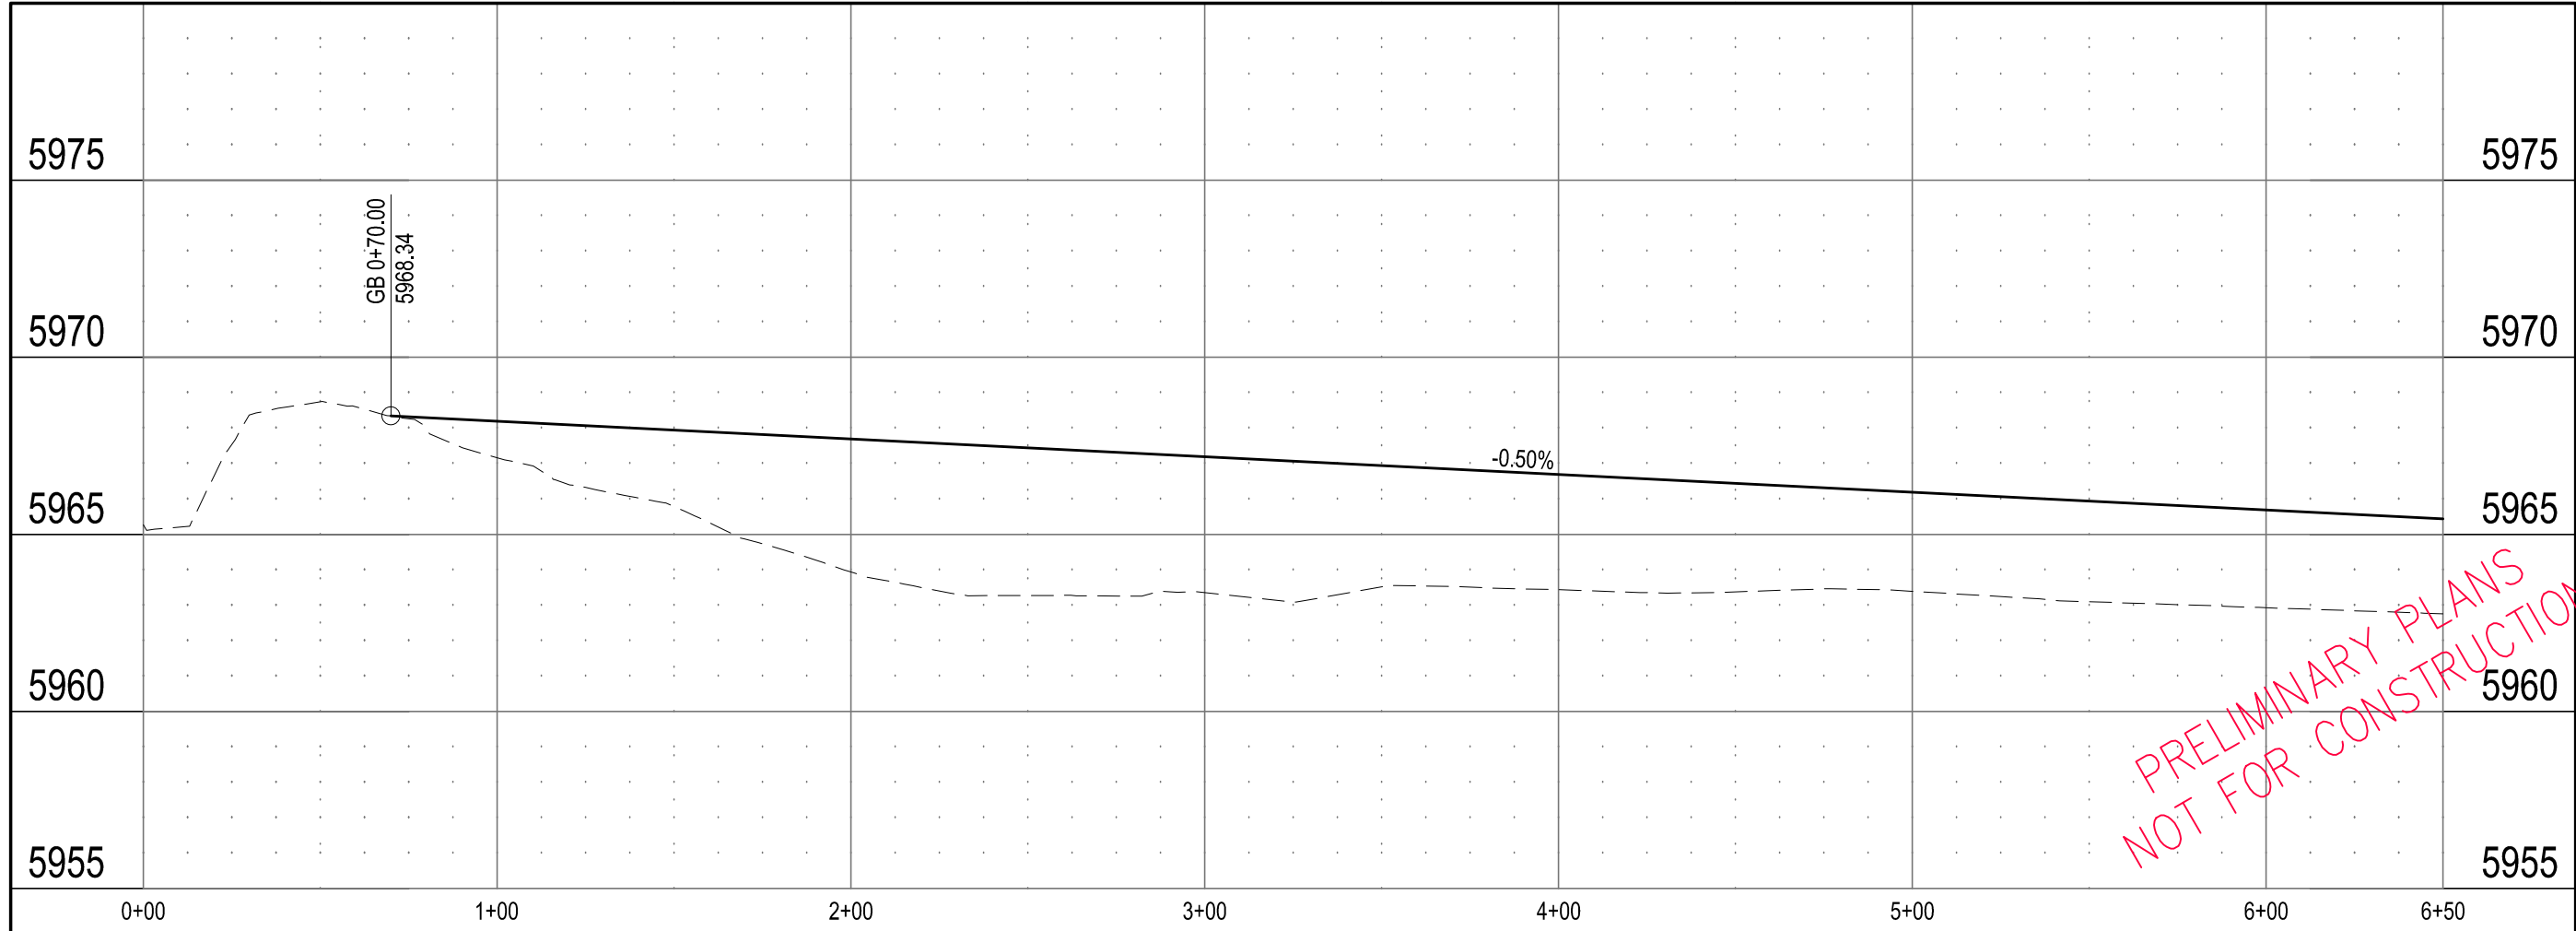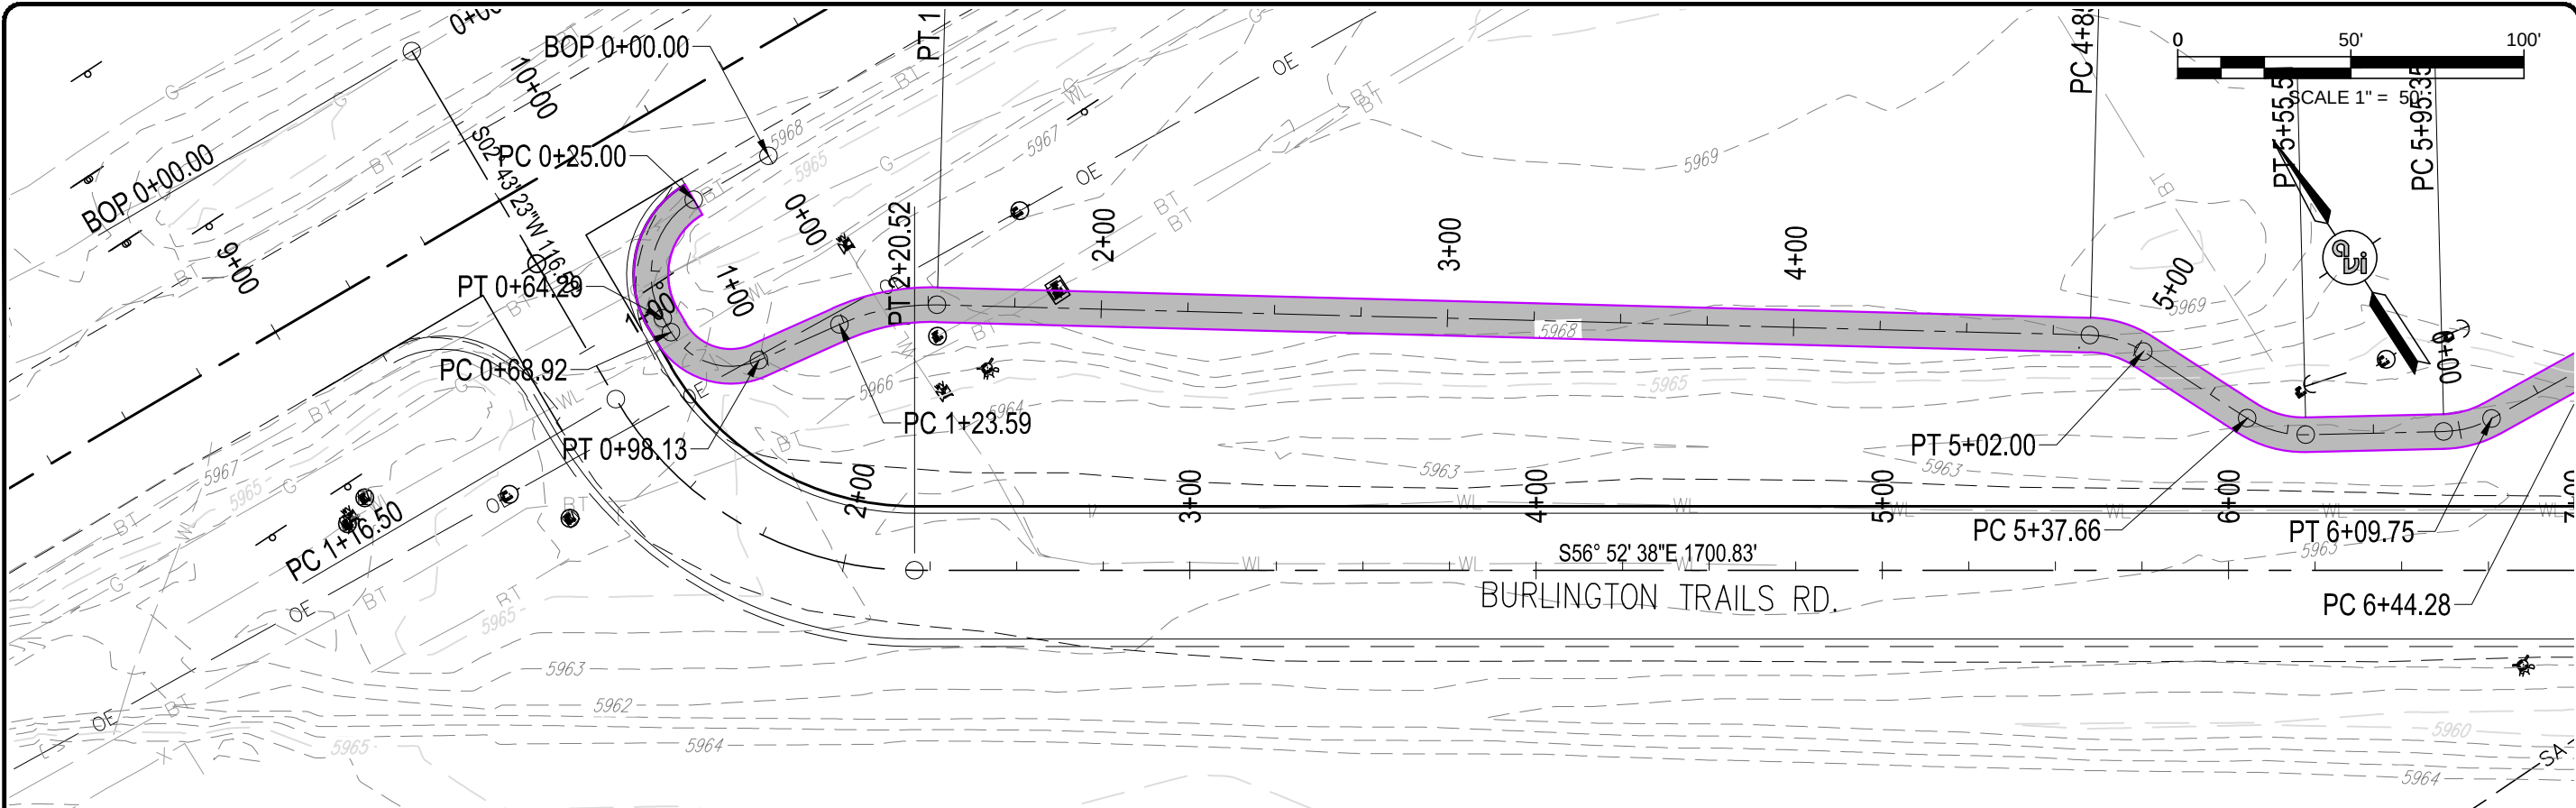

PRELIMINARY PLANS  
NOT FOR CONSTRUCTION

| NO. | REVISION | DATE |
|-----|----------|------|
|     |          |      |
|     |          |      |
|     |          |      |
|     |          |      |

PREPARED FOR:  
MPO  
2101 ONEIL AVE.  
RM 205  
CHEYENNE, WY. 82001

PROJECT: FOX FARM ROAD STREET IMPROVEMENTS  
DRAWING TITLE: BURLINGTON TRAILS RD. PLAN AND PROFILE STA. 0+00 - 6+50



avi p.c.  
engineering  
planning  
surveying  
PHONE (307) 637-6017  
1103 OLD TOWN LANE, SUITE 101  
CHEYENNE, WY 82009  
AVI@AVIFC.COM

DATE: 6-20-13  
DRAWN BY: SRL  
DESIGNED BY: TC  
CHECKED BY: TC

JOB NO.: 2-3211-B

ST-24 83  
SHEET NO. OF

H:\3211\design\3211B FOX FARM STREET IMP.dwg Aug 30, 2013 4:17pm jwilson

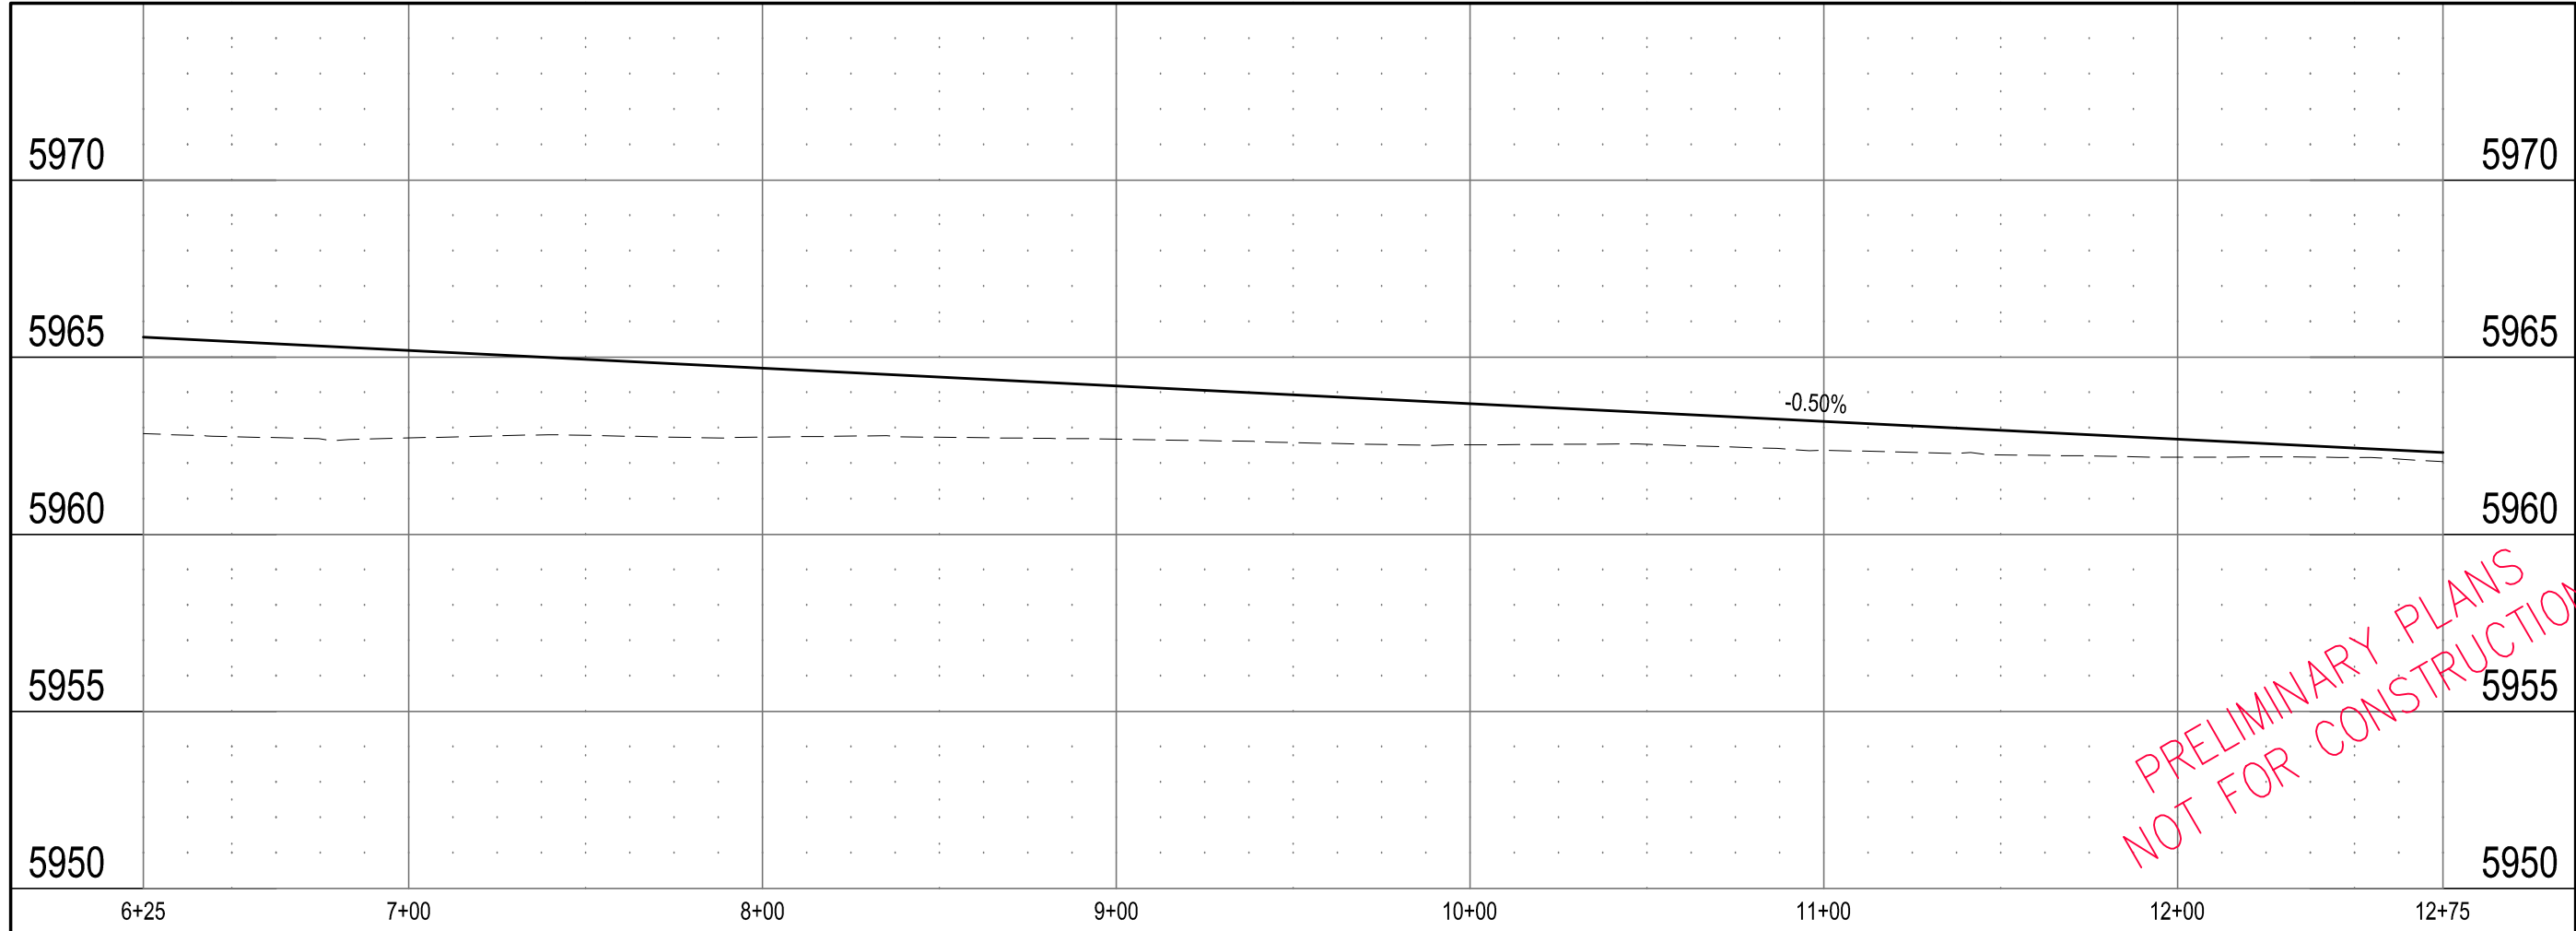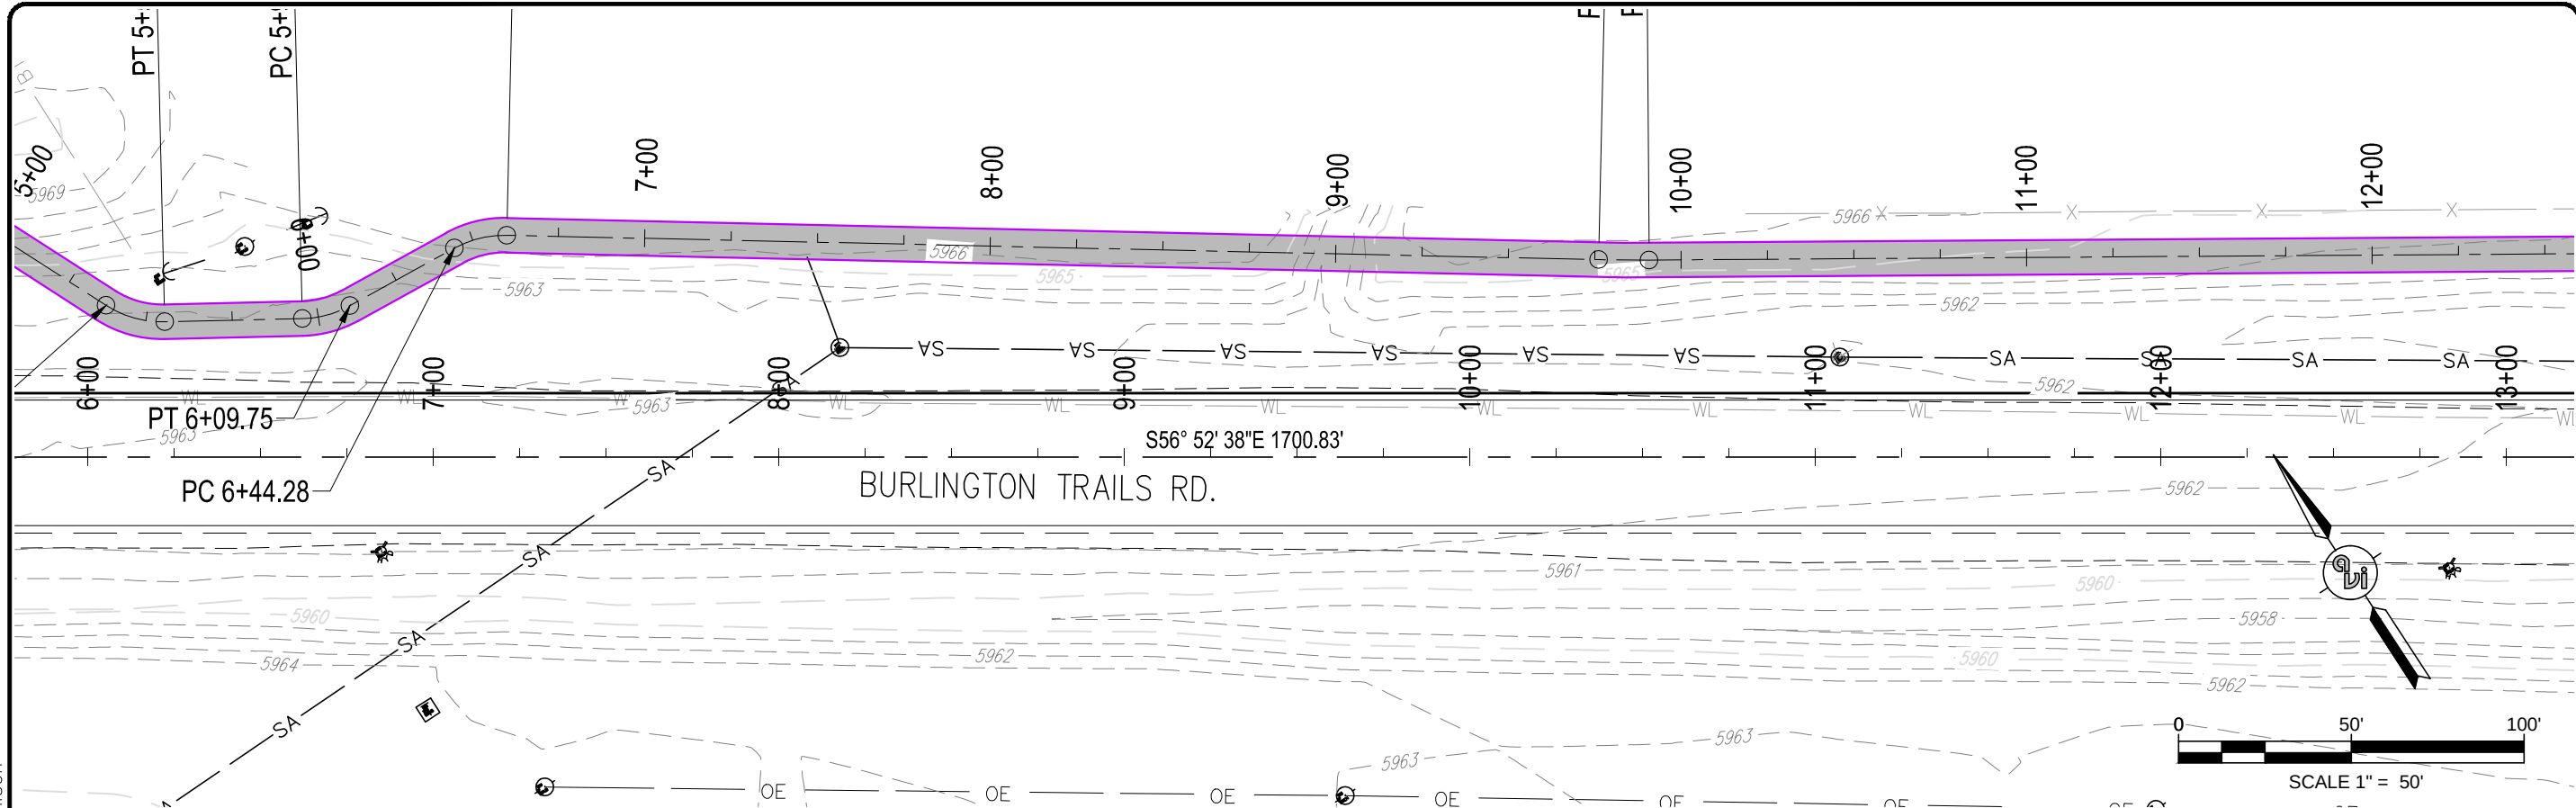

PRELIMINARY PLANS  
NOT FOR CONSTRUCTION

| NO. | REVISION | DATE |
|-----|----------|------|
|     |          |      |
|     |          |      |
|     |          |      |
|     |          |      |

PREPARED FOR:  
MPO  
2101 ONEIL AVE.  
RM 205  
CHEYENNE, WY. 82001

PROJECT: FOX FARM ROAD STREET IMPROVEMENTS  
DRAWING TITLE: BURLINGTON TRAILS RD. PLAN AND PROFILE STA. 6+25 - 12+75



avi p.c.  
engineering  
planning  
surveying  
PHONE (307) 637-6017  
1103 OLD TOWN LANE, SUITE 101  
CHEYENNE, WY 82009  
AVI@AVIPC.COM

DATE: 6-20-13  
DRAWN BY: SRL  
DESIGNED BY: TC  
CHECKED BY: TC

JOB NO.: 2-3211-B

ST-25 83  
SHEET NO. OF

H:\3211\design\3211B FOX FARM STREET IMP.dwg Aug 30, 2013 4:17pm jwilson

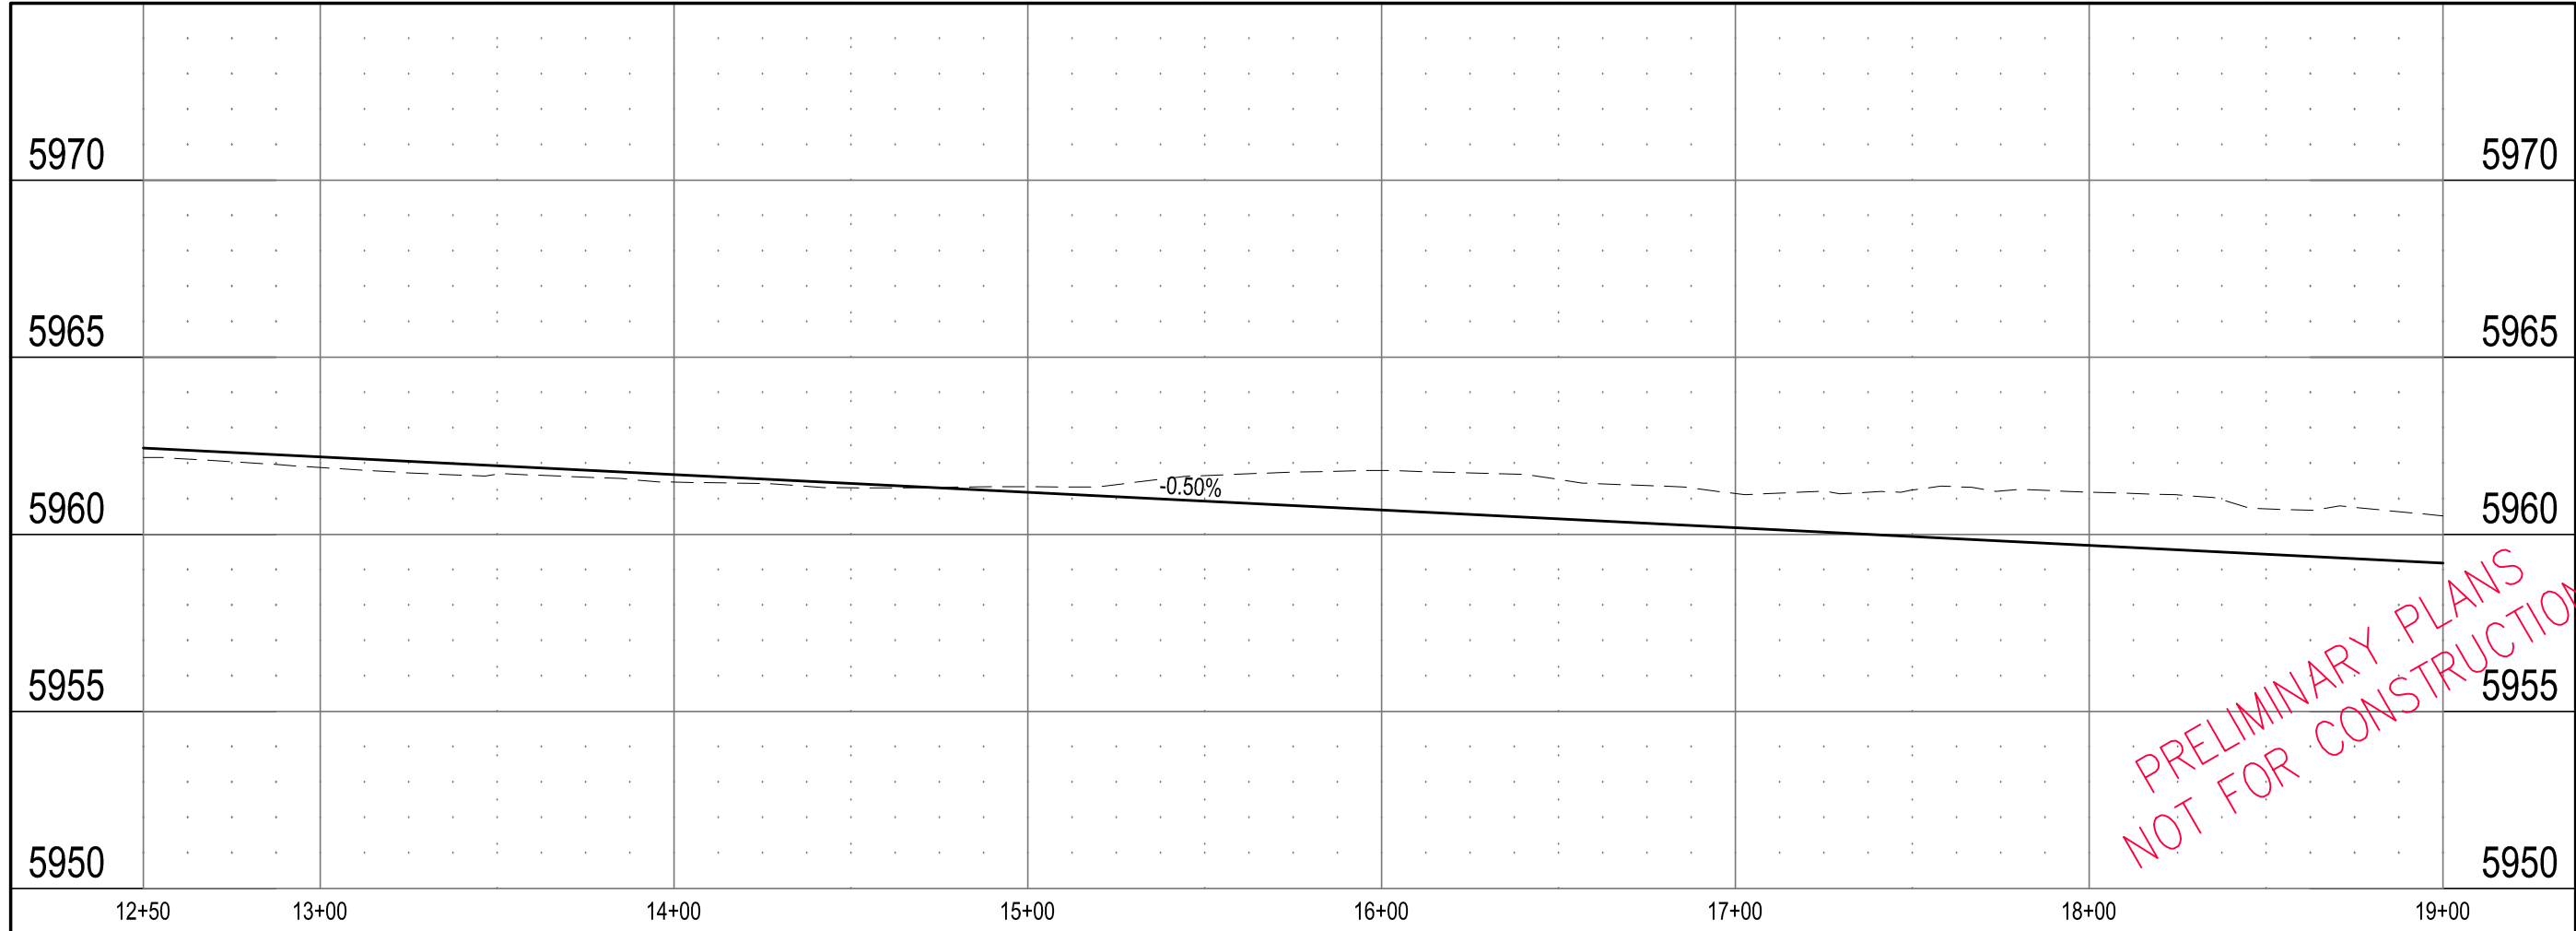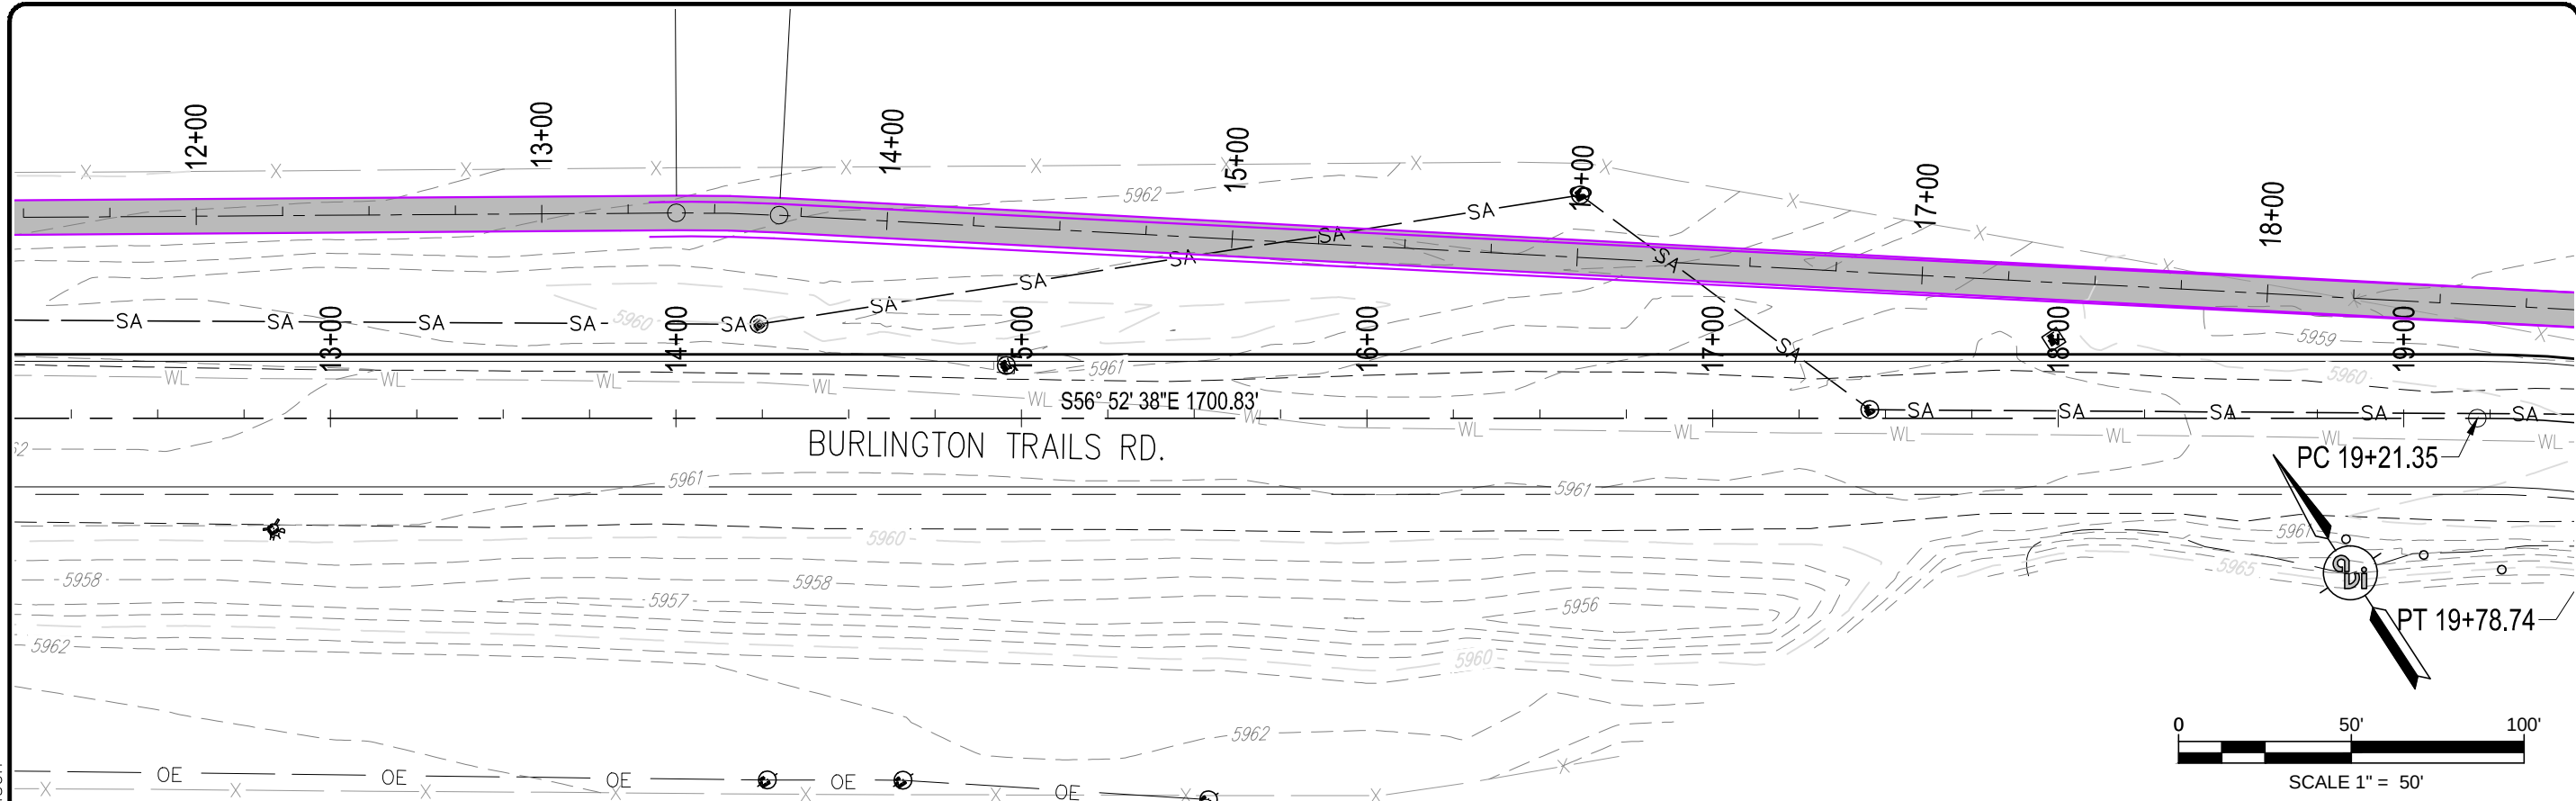

| NO. | REVISION | DATE |
|-----|----------|------|
|     |          |      |
|     |          |      |
|     |          |      |
|     |          |      |

PREPARED FOR:  
MPO  
2101 ONEIL AVE.  
RM 205  
CHEYENNE, WY. 82001

PROJECT: FOX FARM ROAD STREET IMPROVEMENTS  
DRAWING TITLE: BURLINGTON TRAILS RD. PLAN AND PROFILE STA. 12+50 - 19+00

**avi** p.c.  
engineering  
planning  
surveying  
PHONE (307) 637-6017  
1103 OLD TOWN LANE, SUITE 101  
CHEYENNE, WY 82009  
AVI@AVIFC.COM



DATE: 6-20-13  
DRAWN BY: SRL  
DESIGNED BY: TC  
CHECKED BY: TC

JOB NO.: 2-3211-B

ST-26 83  
SHEET NO. OF

PRELIMINARY PLANS  
NOT FOR CONSTRUCTION

H:\3211\design\3211B FOX FARM STREET IMP.dwg Aug 30, 2013 4:18pm jwilson

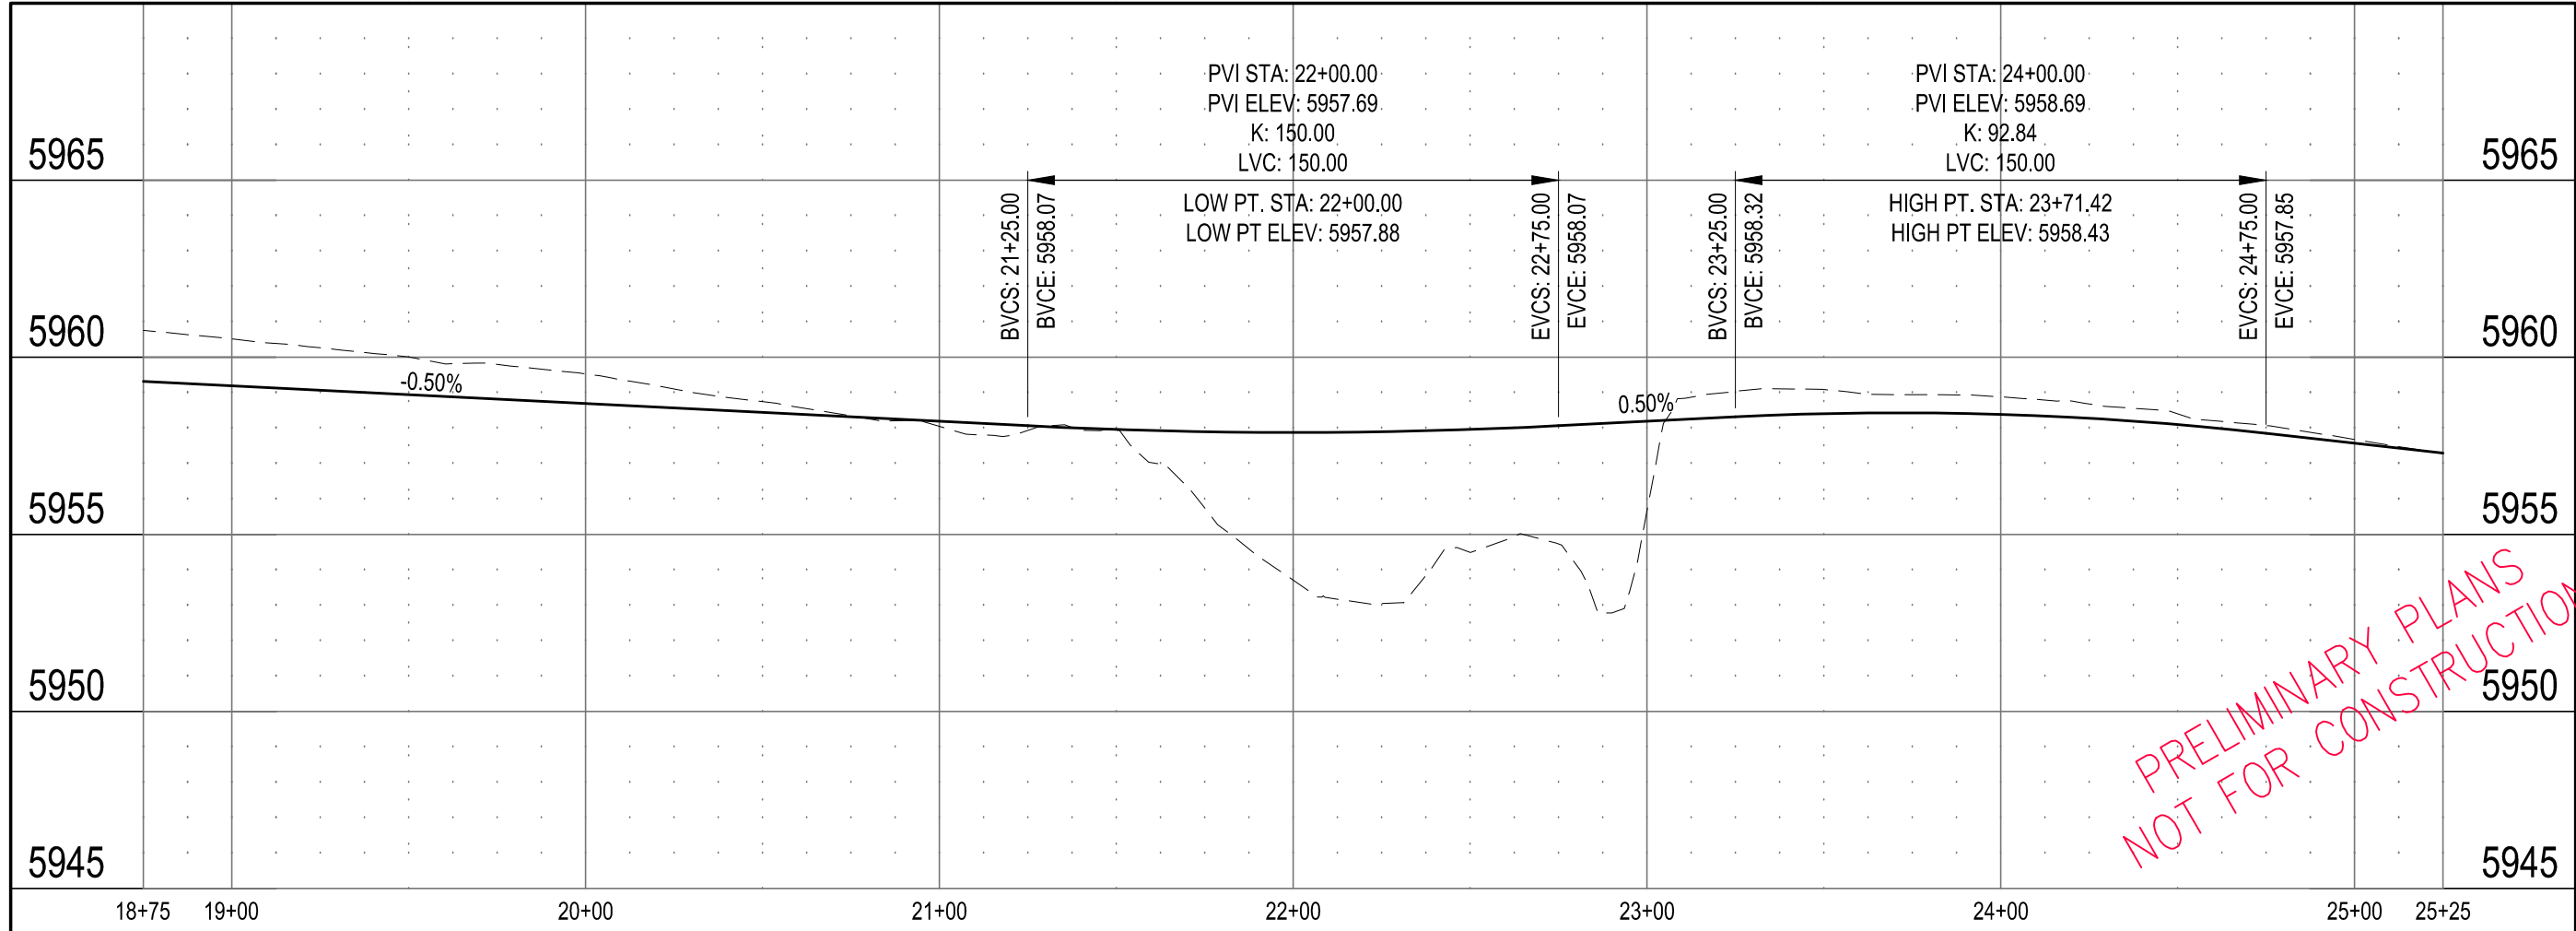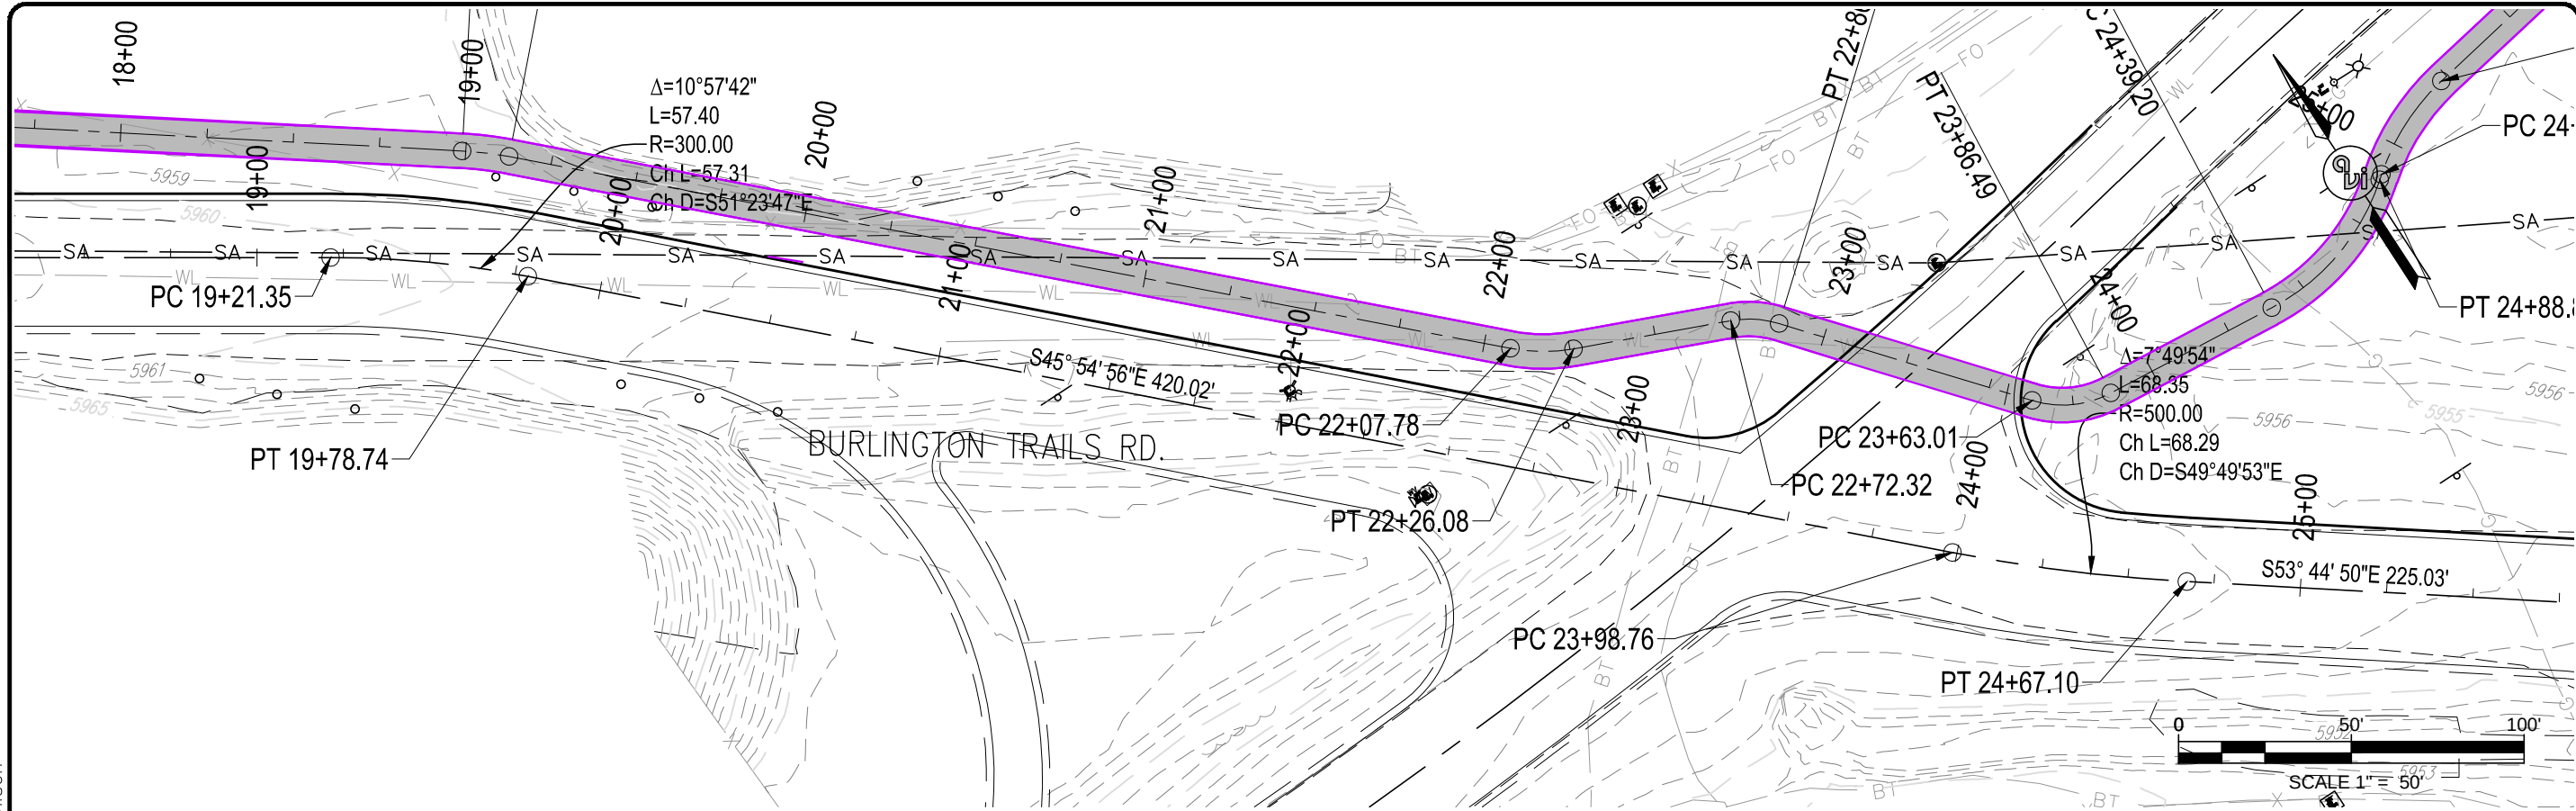

| NO. | REVISION | DATE |
|-----|----------|------|
|     |          |      |
|     |          |      |
|     |          |      |

PREPARED FOR:  
MPO  
2101 ONEIL AVE.  
RM 205  
CHEYENNE, WY. 82001

PROJECT: FOX FARM ROAD STREET IMPROVEMENTS

DRAWING TITLE: BURLINGTON TRAILS RD. PLAN AND PROFILE STA. 18+75 - 25+25

**avi** p.c.  
engineering  
planning  
surveying  
PHONE (307) 637-6017  
1103 OLD TOWN LANE, SUITE 101  
CHEYENNE, WY 82009  
AVI@AVIIPC.COM

DATE: 6-20-13  
DRAWN BY: SRL  
DESIGNED BY: TC  
CHECKED BY: TC



JOB NO.: 2-3211-B

ST-27 83  
SHEET NO. OF

[illegible]

|  |  |      |
|--|--|------|
|  |  | 5950 |
|  |  | 5945 |

H:\3211\design\3211B FOX FARM STREET IMP.dwg Aug 30, 2013 4:19pm jwilson

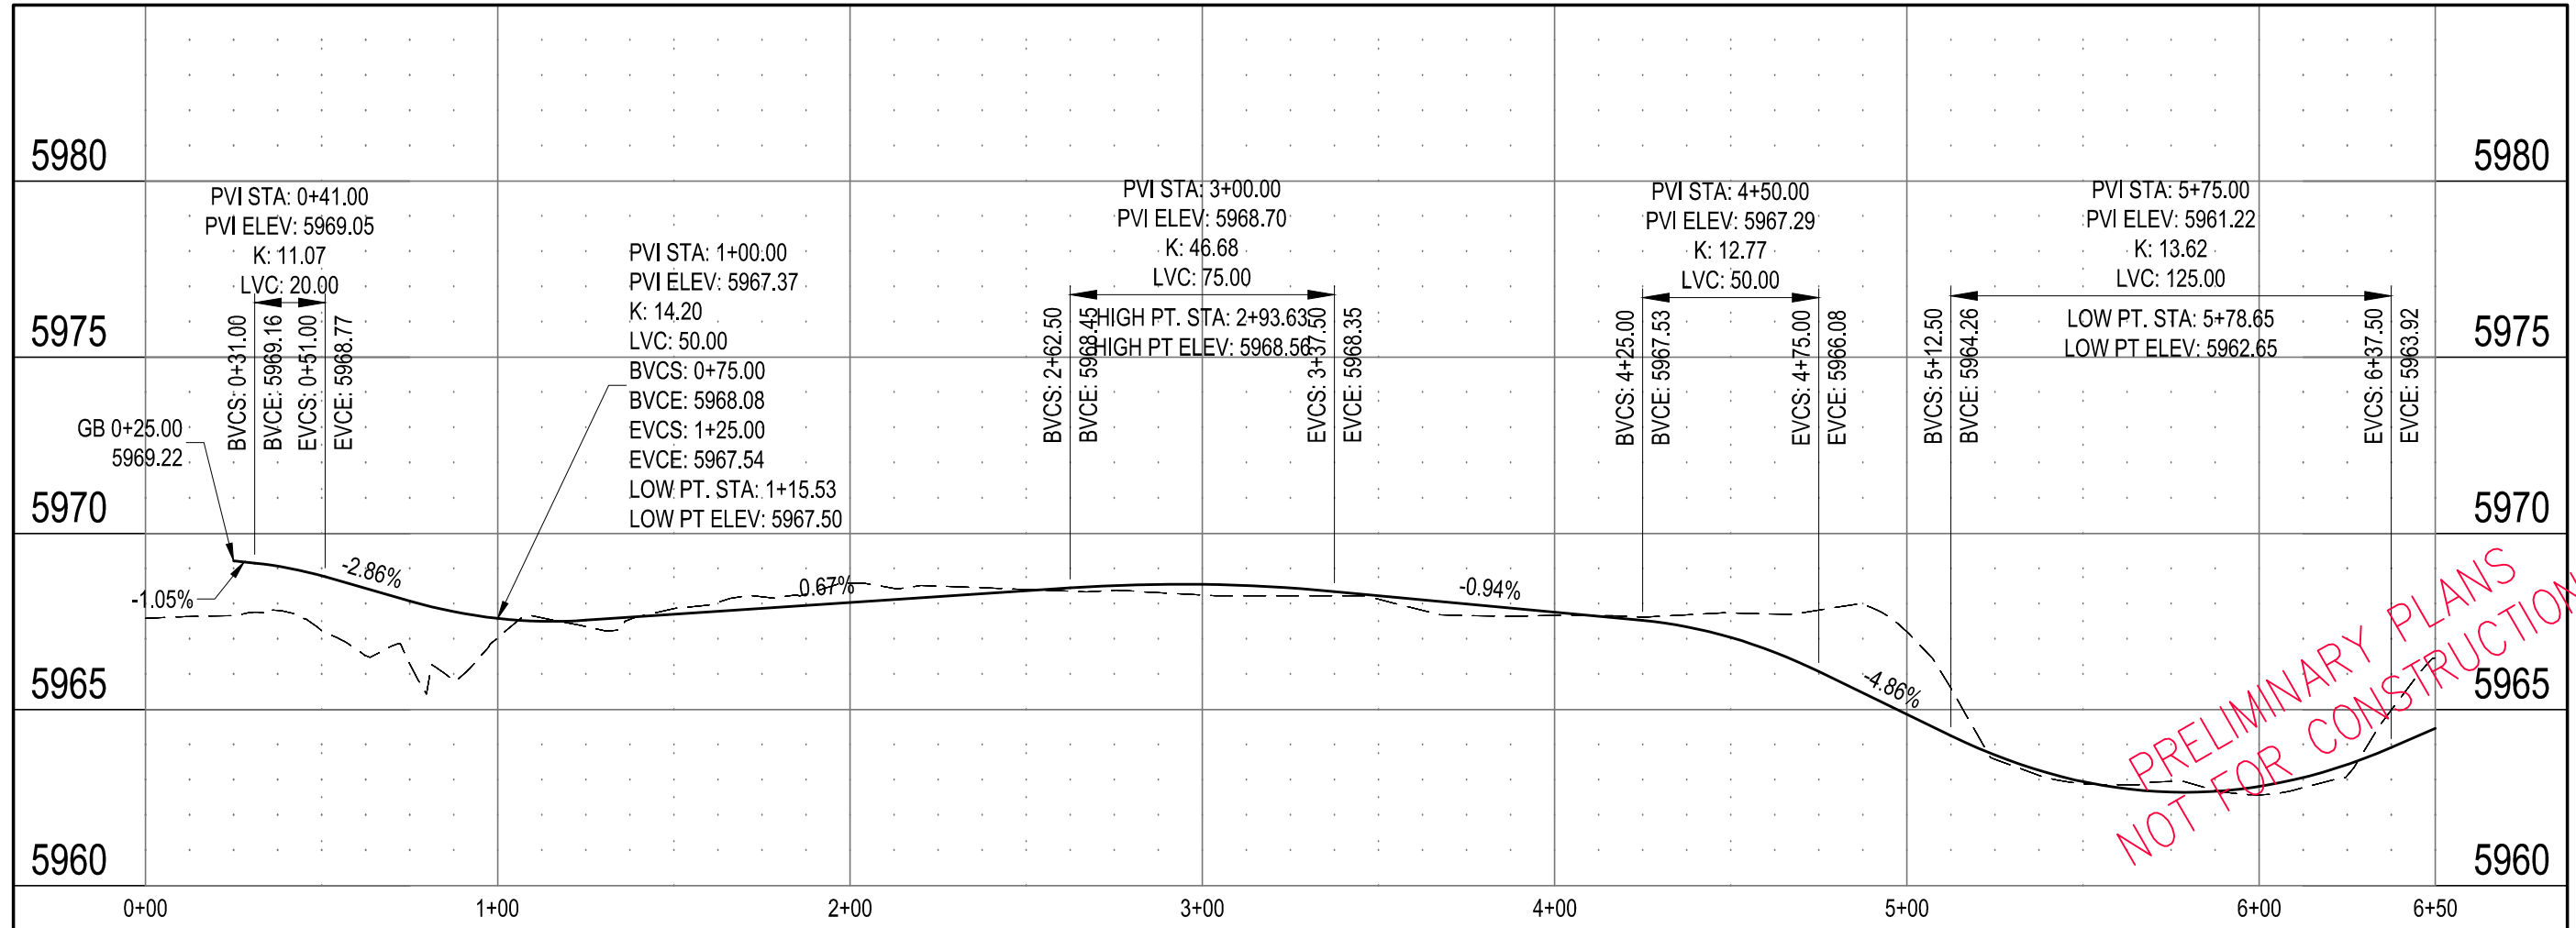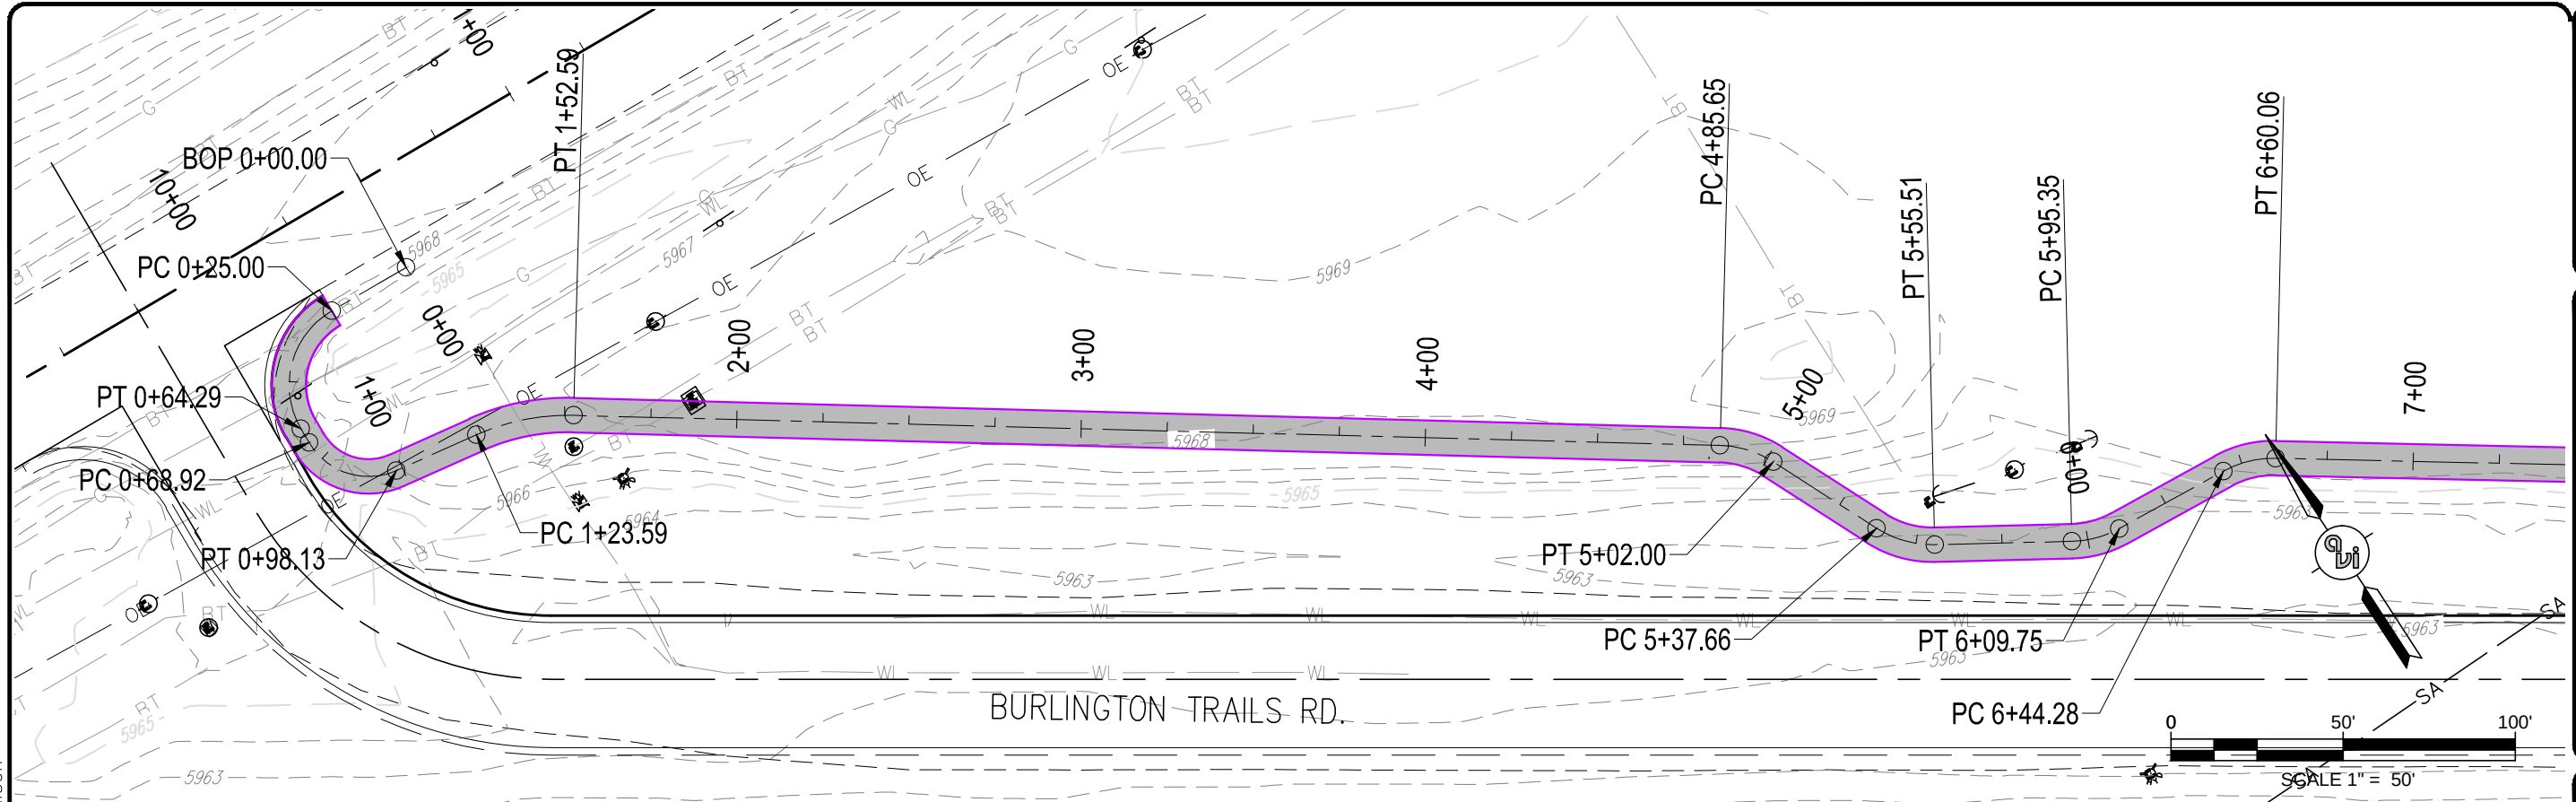

PRELIMINARY PLANS  
NOT FOR CONSTRUCTION

| NO. | REVISION | DATE |
|-----|----------|------|
|     |          |      |
|     |          |      |
|     |          |      |
|     |          |      |

PREPARED FOR:  
MPO  
2101 ONEIL AVE.  
RM 205  
CHEYENNE, WY. 82001

PROJECT:  
FOX FARM ROAD STREET  
IMPROVEMENTS  
DRAWING TITLE:  
BURLINGTON TRAILS SIDEWALK  
PLAN AND PROFILE STA. 0+00 - 6+50



engineering  
planning  
surveying  
**avi** p.c.  
PHONE (307) 637-6017  
1103 OLD TOWN LANE, SUITE 101  
CHEYENNE, WY 82009  
AVI@AVIPC.COM

DATE:  
6-20-13  
DRAWN BY:  
SRL  
DESIGNED BY:  
TC  
CHECKED BY:  
TC

JOB NO.:  
2-3211-B

ST-29 83  
SHEET NO. OF

H:\3211\design\3211B FOX FARM STREET IMP.dwg Aug 30, 2013 4:19pm jwilson

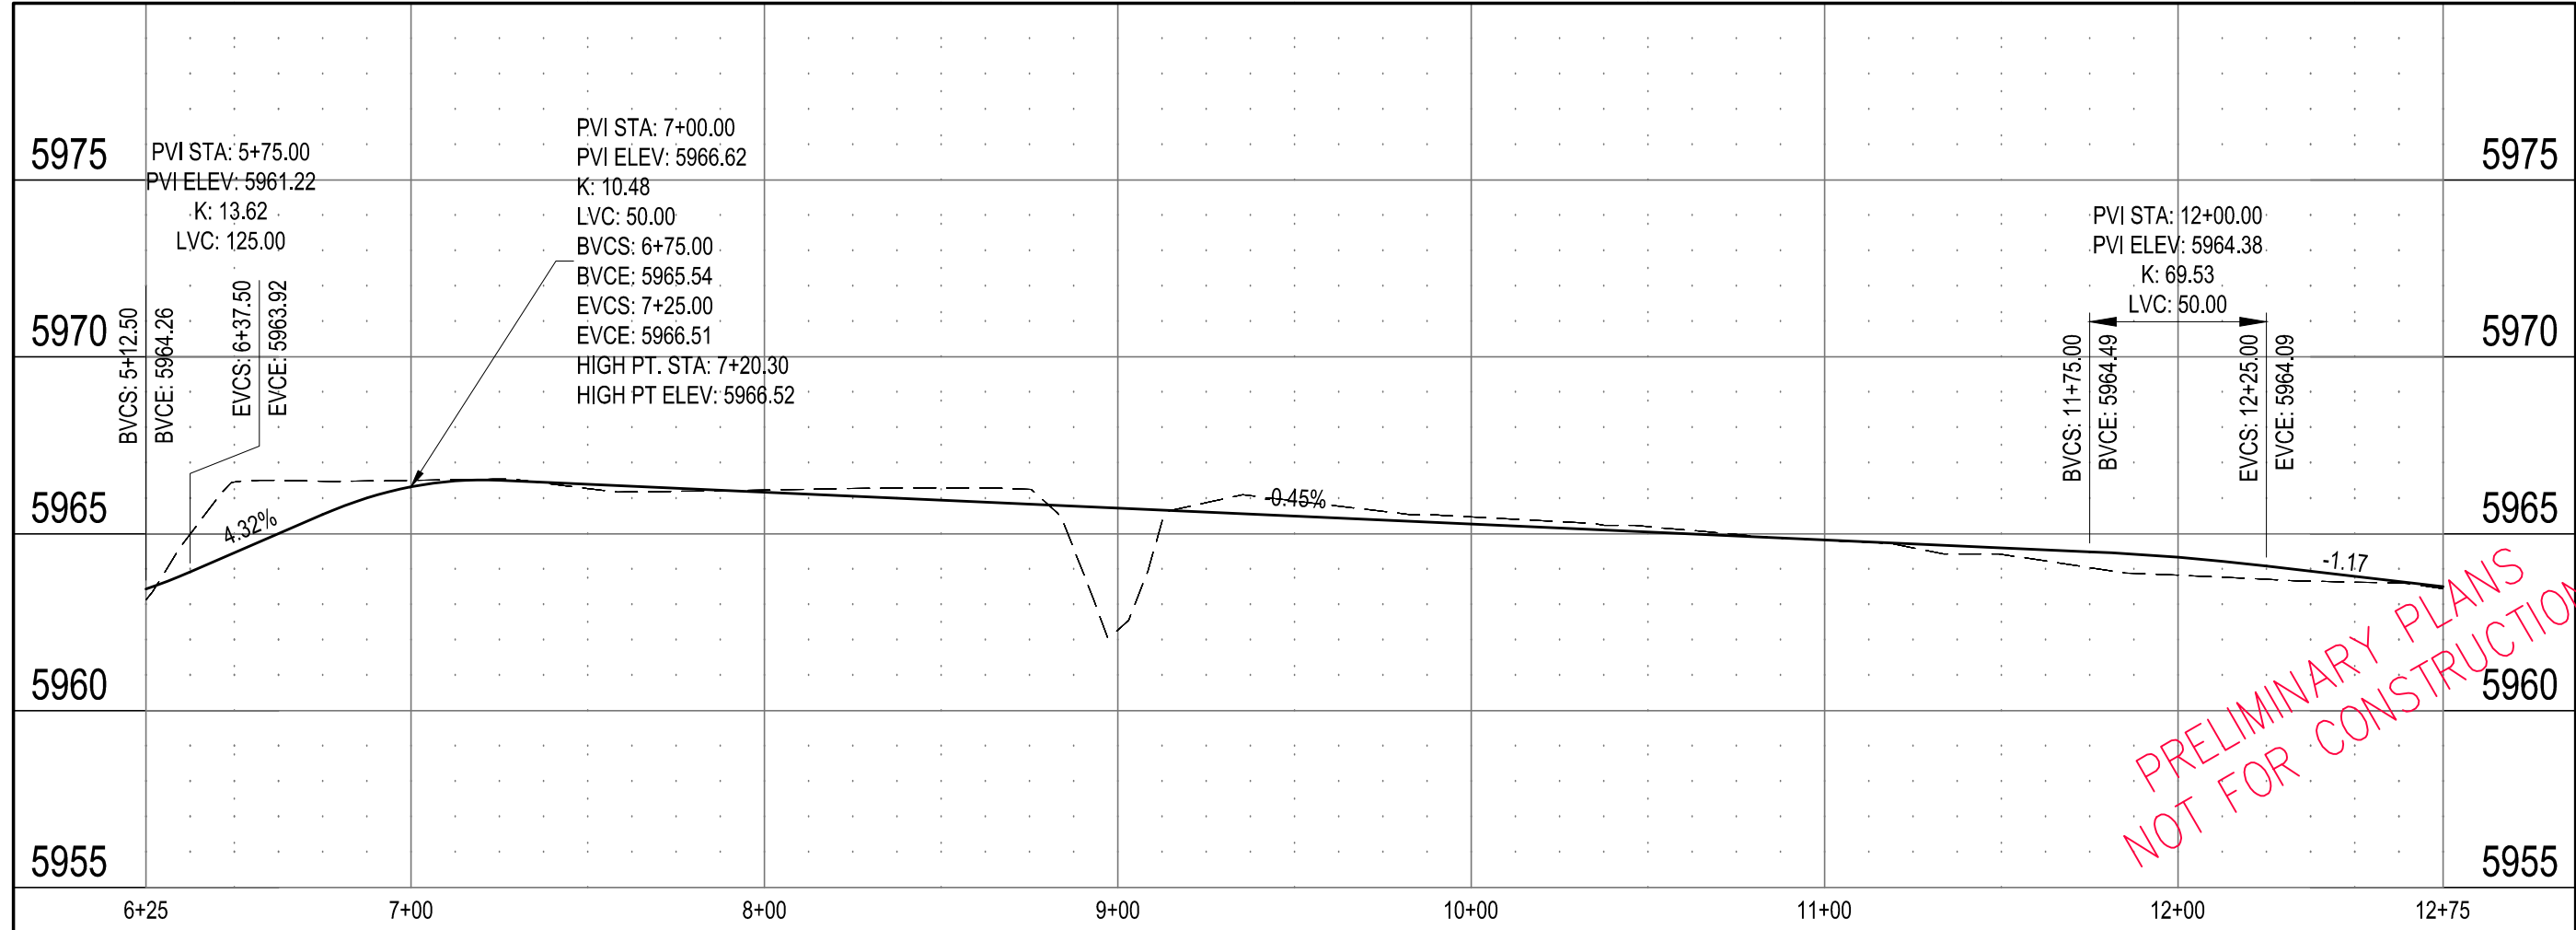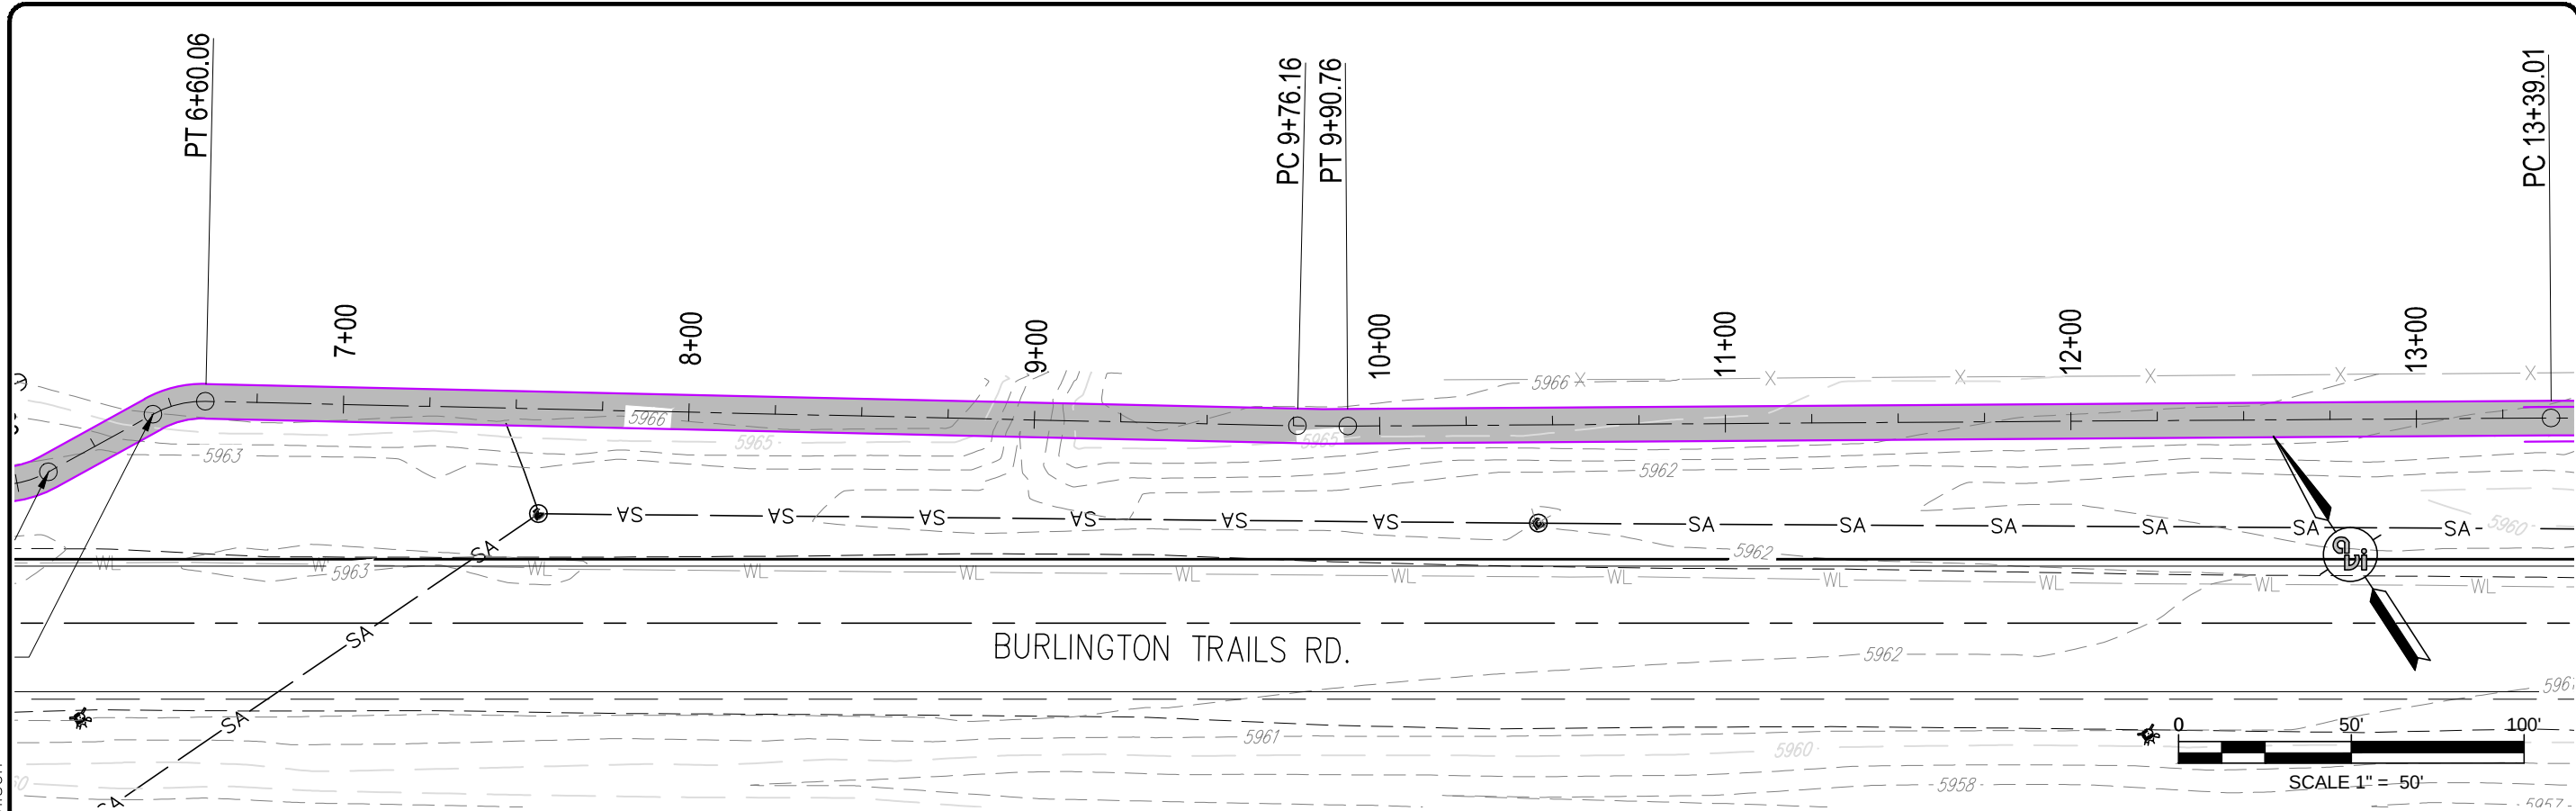

PRELIMINARY PLANS  
NOT FOR CONSTRUCTION

| NO. | REVISION | DATE |
|-----|----------|------|
|     |          |      |
|     |          |      |
|     |          |      |
|     |          |      |

PROJECT: FOX FARM ROAD STREET IMPROVEMENTS

DRAWING TITLE: BURLINGTON TRAILS SIDEWALK PLAN AND PROFILE STA. 6+25 - 12+75



PREPARED FOR: MPO 2101 ONEIL AVE. RM 205 CHEYENNE, WY. 82001

DATE: 6-20-13  
DRAWN BY: SRL  
DESIGNED BY: TC  
CHECKED BY: TC

JOB NO.: 2-3211-B

SHEET NO. 83 OF

H:\3211\design\3211B FOX FARM STREET IMP.dwg Aug 30, 2013 4:19pm jwilson

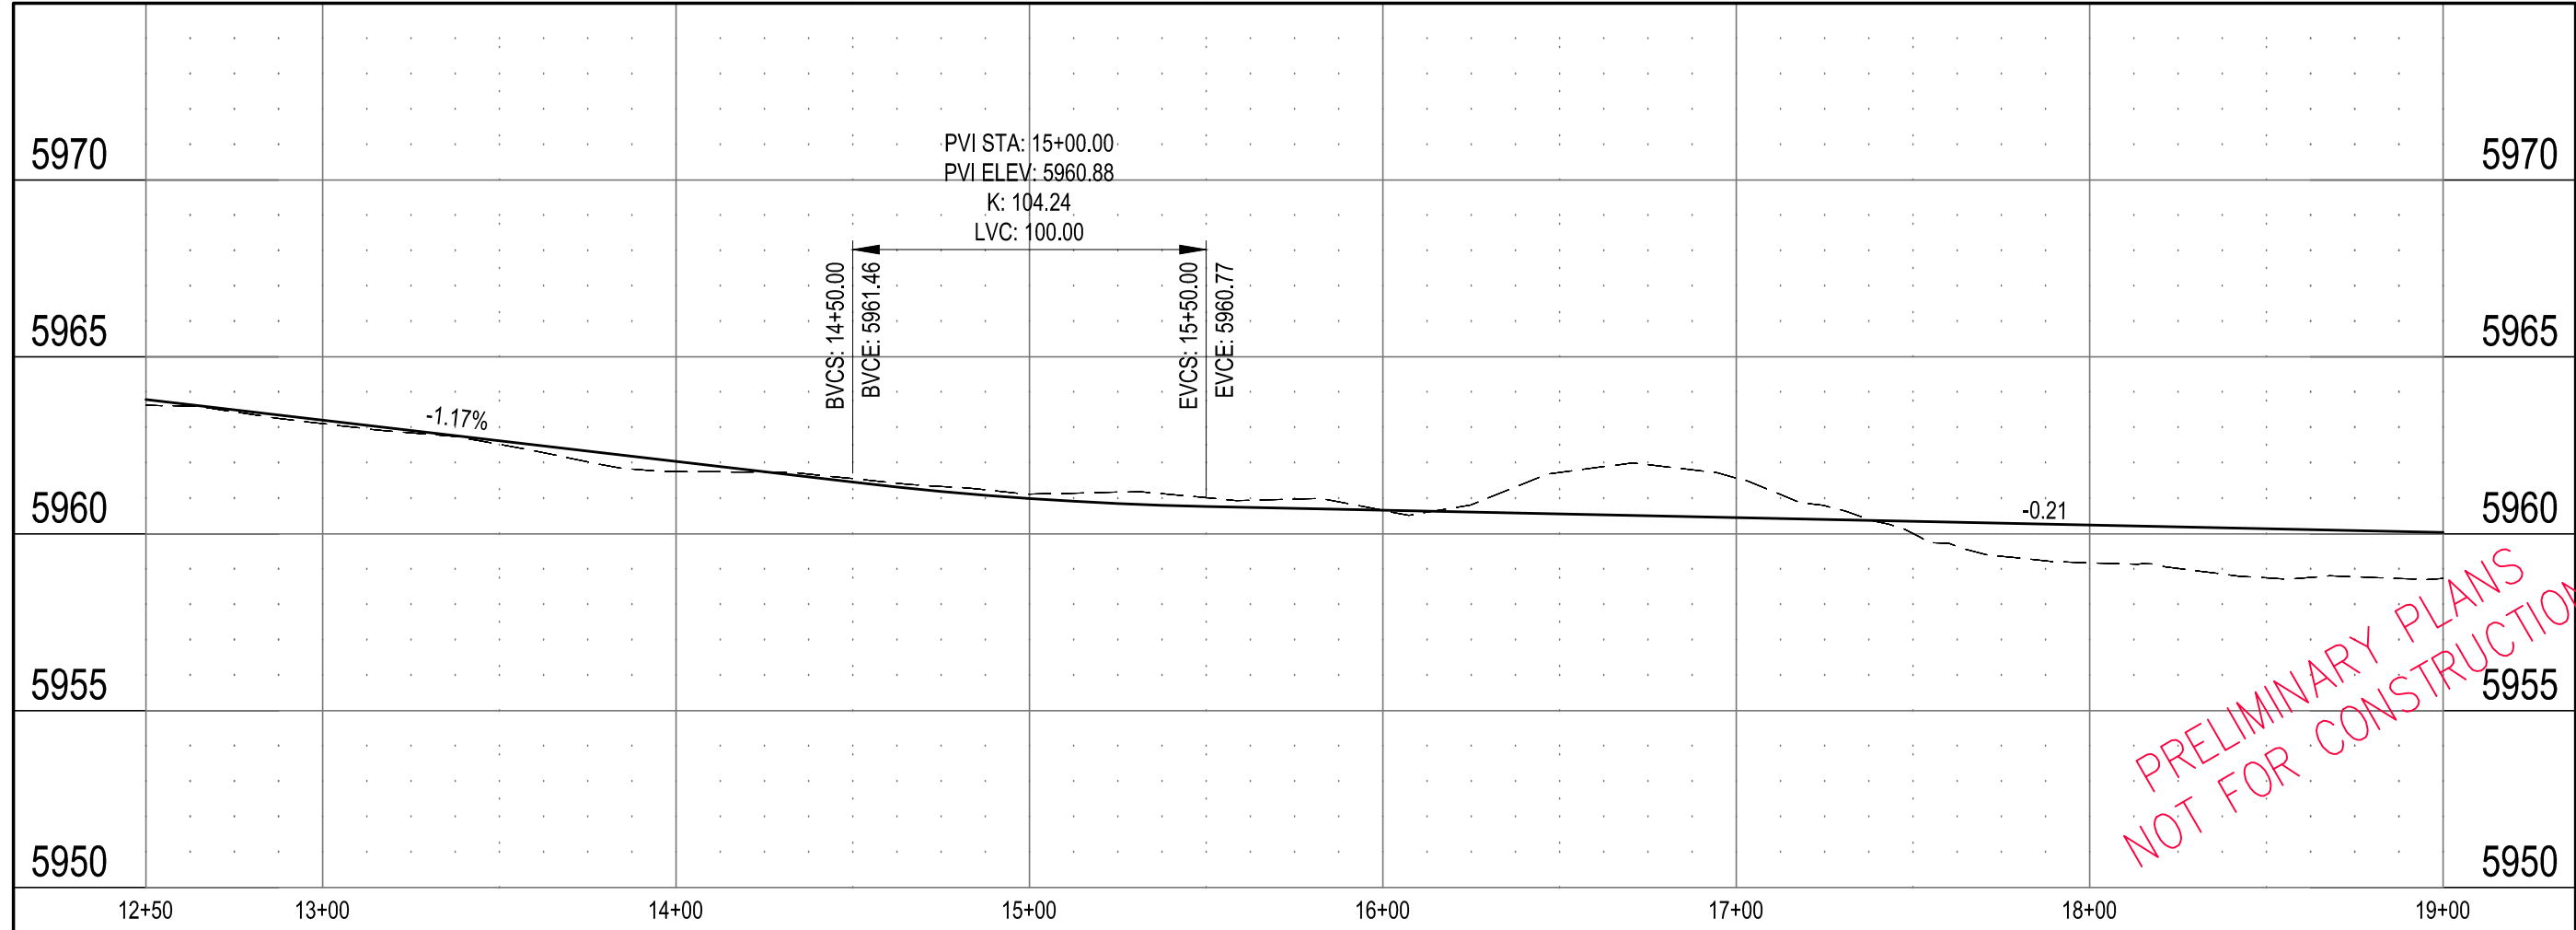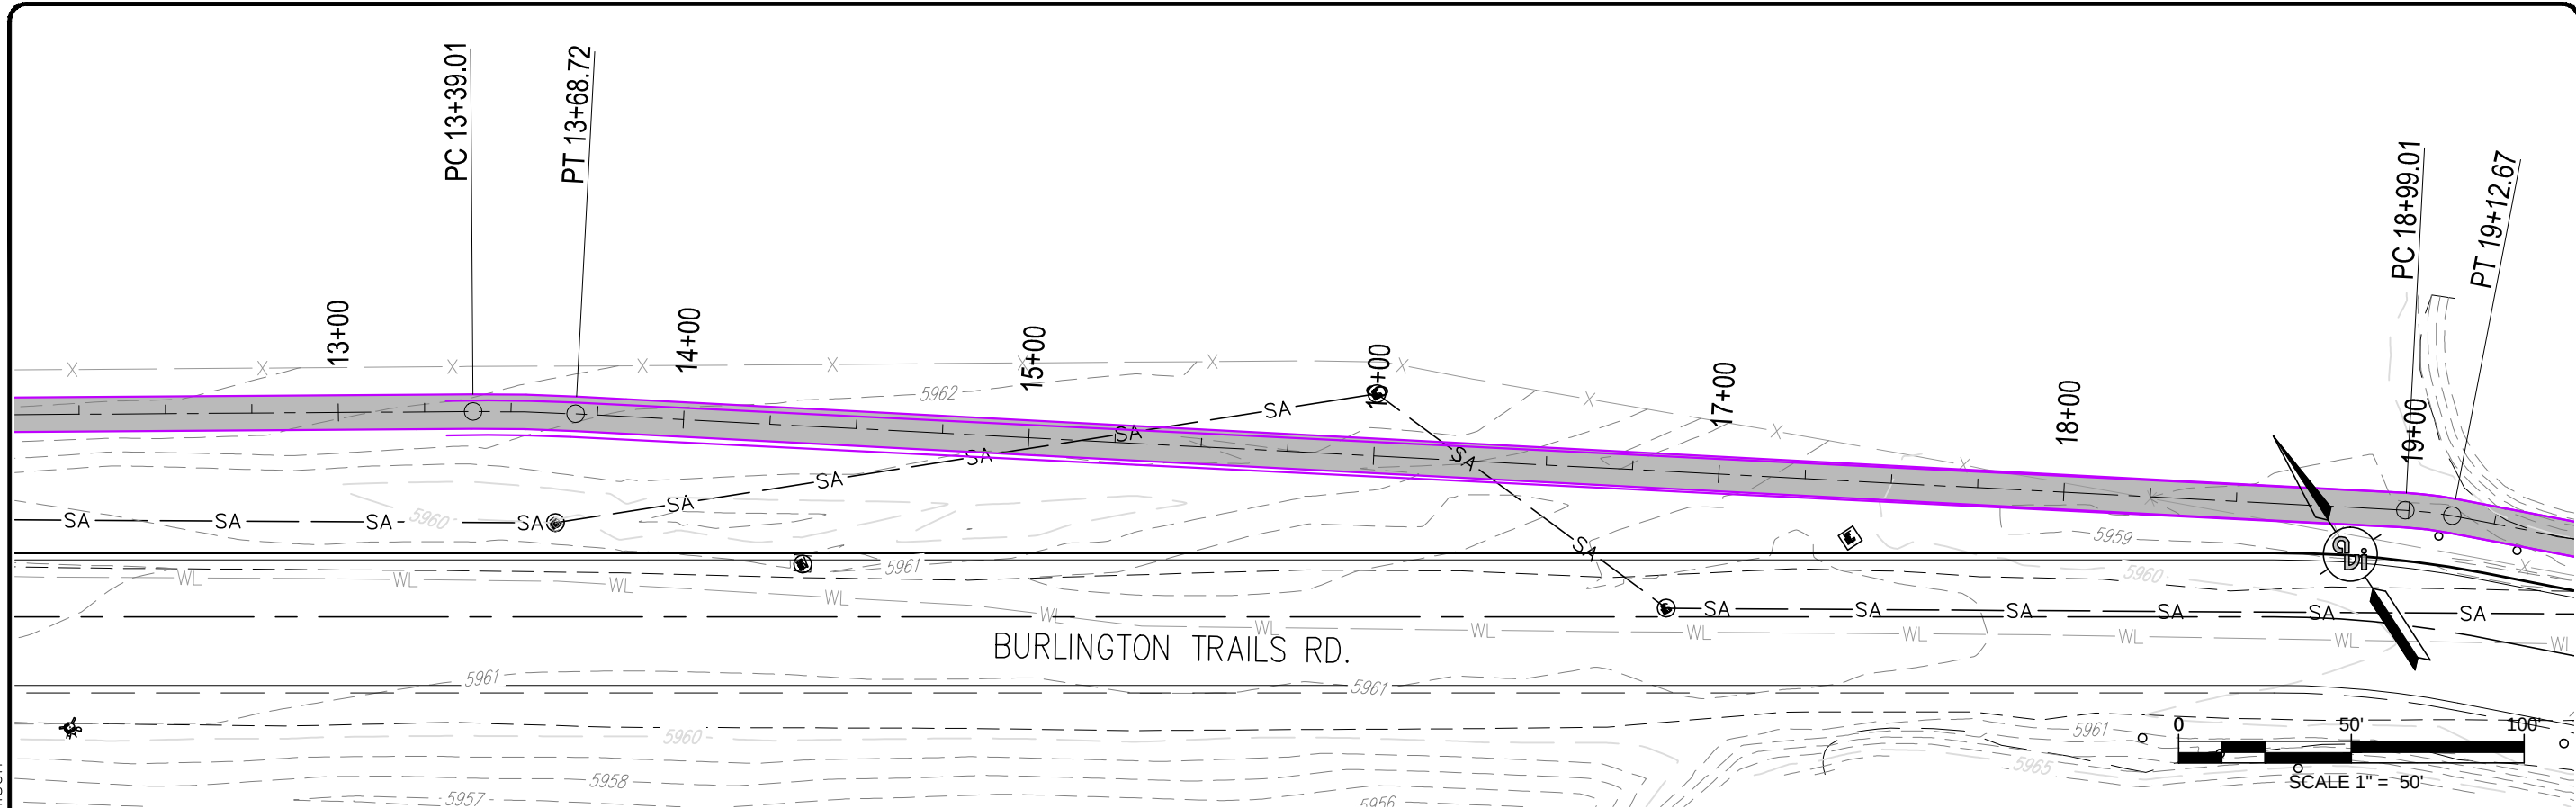

PRELIMINARY PLANS  
NOT FOR CONSTRUCTION

| NO. | REVISION | DATE |
|-----|----------|------|
|     |          |      |
|     |          |      |
|     |          |      |
|     |          |      |

PREPARED FOR:  
MPO  
2101 ONEIL AVE.  
RM 205  
CHEYENNE, WY. 82001

PROJECT: FOX FARM ROAD STREET IMPROVEMENTS  
DRAWING TITLE: BURLINGTON TRAILS SIDEWALK PLAN AND PROFILE STA. 12+50 - 19+00



avi p.c.  
engineering  
planning  
surveying  
PHONE (307) 637-6017  
1103 OLD TOWN LANE, SUITE 101  
CHEYENNE, WY 82009  
AVI@AVIIPC.COM

DATE: 6-20-13  
DRAWN BY: SRL  
DESIGNED BY: TC  
CHECKED BY: TC

JOB NO.: 2-3211-B

ST-31 83  
SHEET NO. OF

H:\3211\design\3211B FOX FARM STREET IMP.dwg Aug 30, 2013 4:20pm jwilson

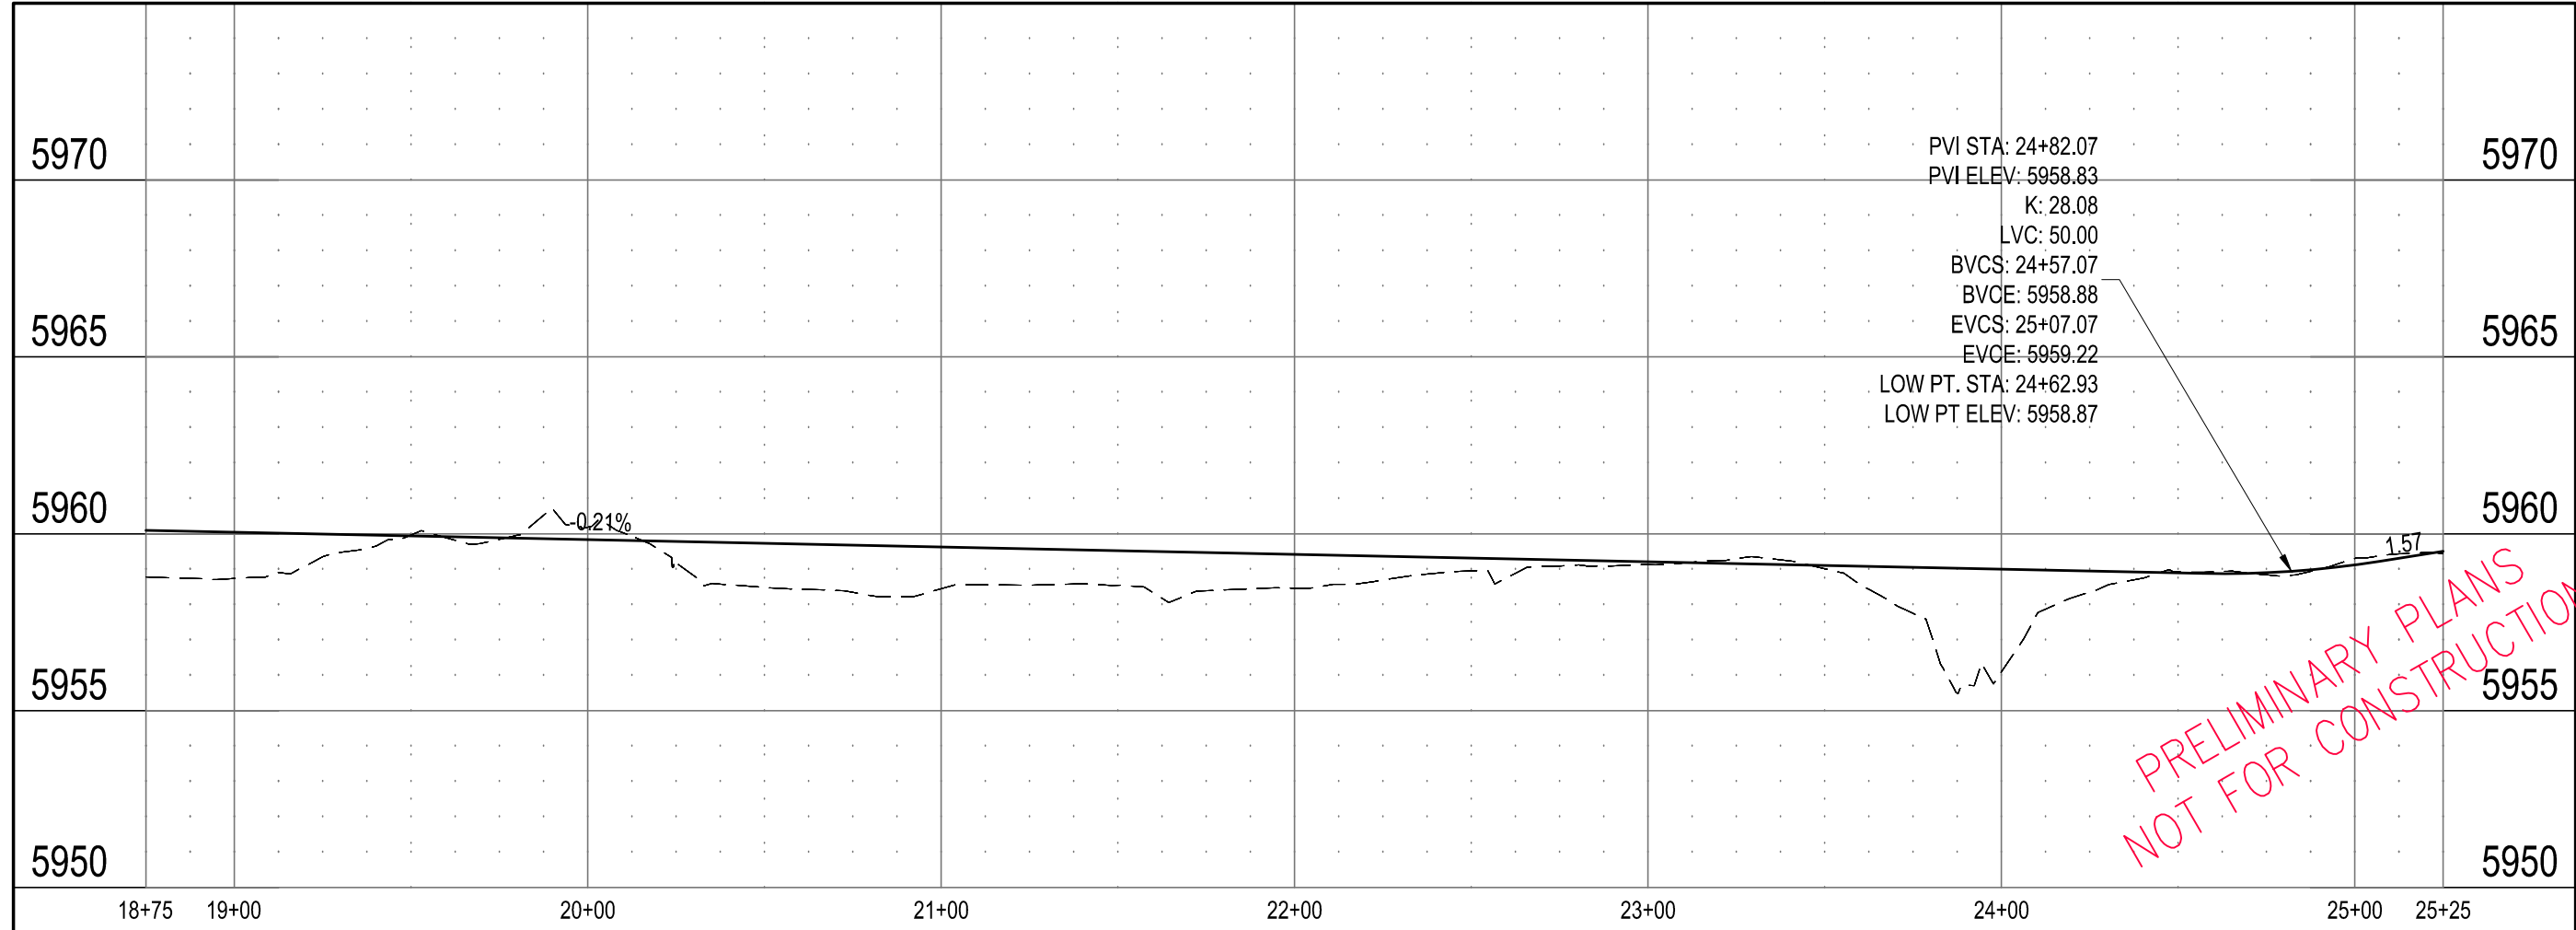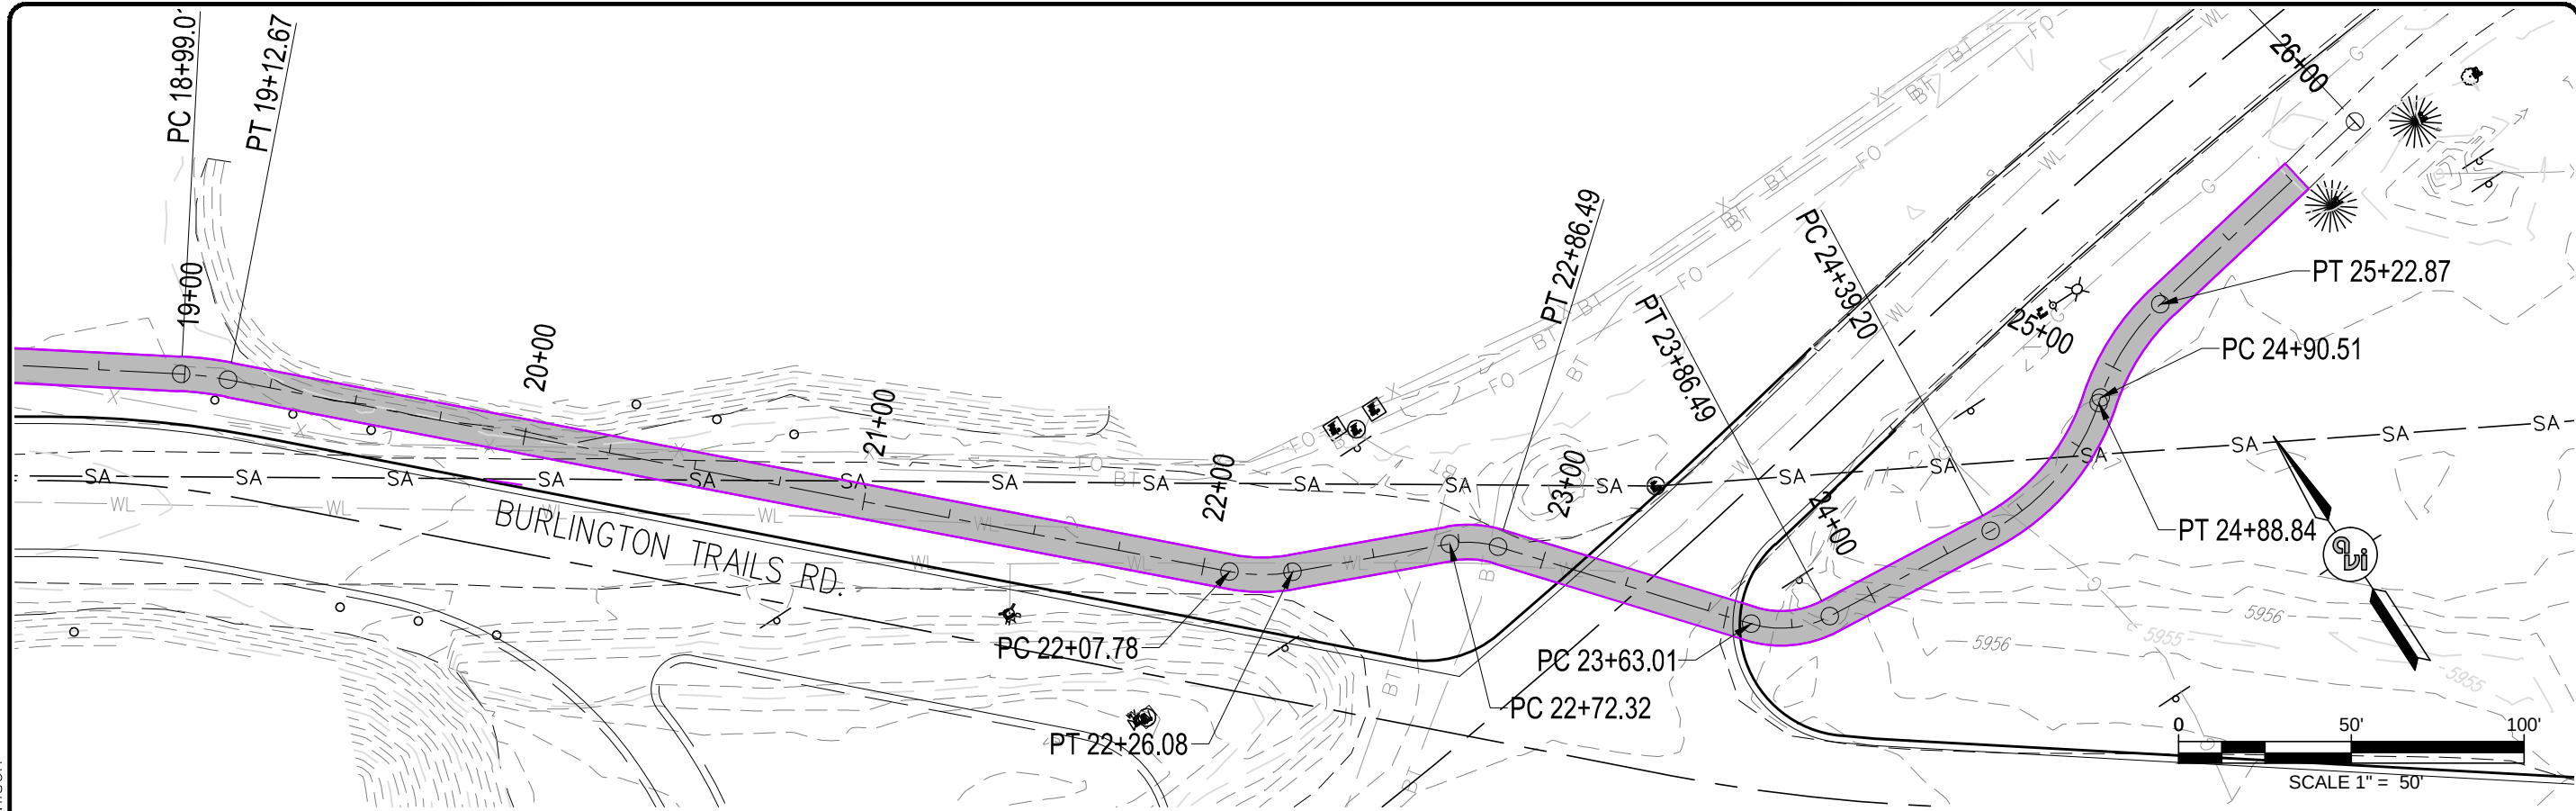

PRELIMINARY PLANS  
NOT FOR CONSTRUCTION

| NO. | REVISION | DATE |
|-----|----------|------|
|     |          |      |
|     |          |      |
|     |          |      |
|     |          |      |

PREPARED FOR:  
MPO  
2101 ONEIL AVE.  
RM 205  
CHEYENNE, WY. 82001

PROJECT: FOX FARM ROAD STREET IMPROVEMENTS  
DRAWING TITLE: BURLINGTON TRAILS SIDEWALK PLAN AND PROFILE STA. 18+75 - 25+25


avi p.c.  
engineering  
planning  
surveying  
PHONE (307) 637-6017  
1103 OLD TOWN LANE, SUITE 101  
CHEYENNE, WY 82009  
AVI@AVIIPC.COM

DATE: 6-20-13  
DRAWN BY: SRL  
DESIGNED BY: TC  
CHECKED BY: TC


JOB NO.: 2-3211-B

ST-32 83  
SHEET NO. OF


|  |  |      |
|--|--|------|
|  |  | 5955 |
|  |  | 5950 |

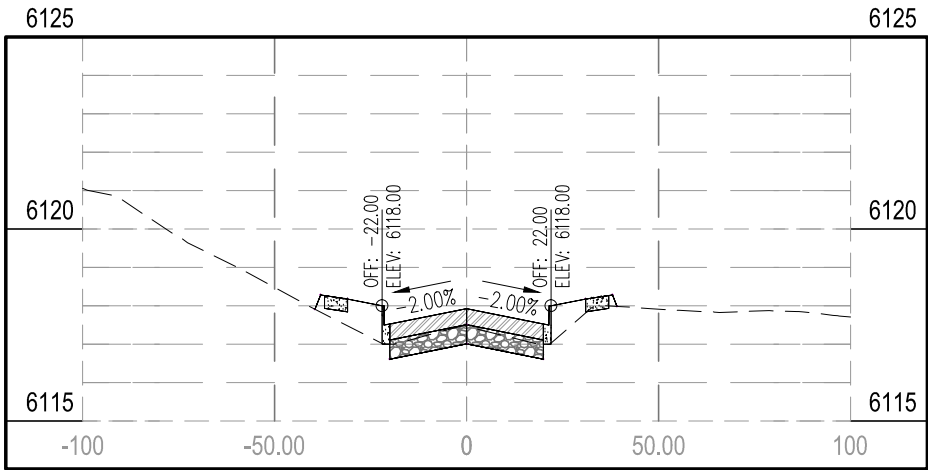


STA 3+00.00

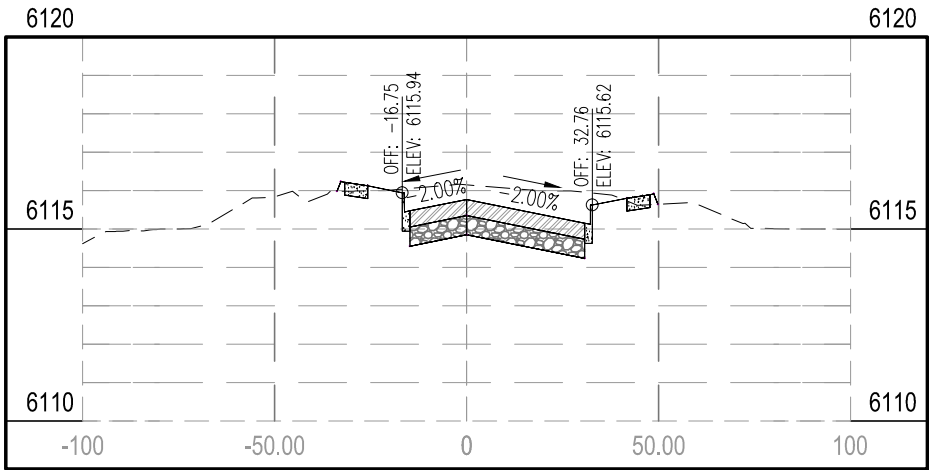


STA 6+00.00

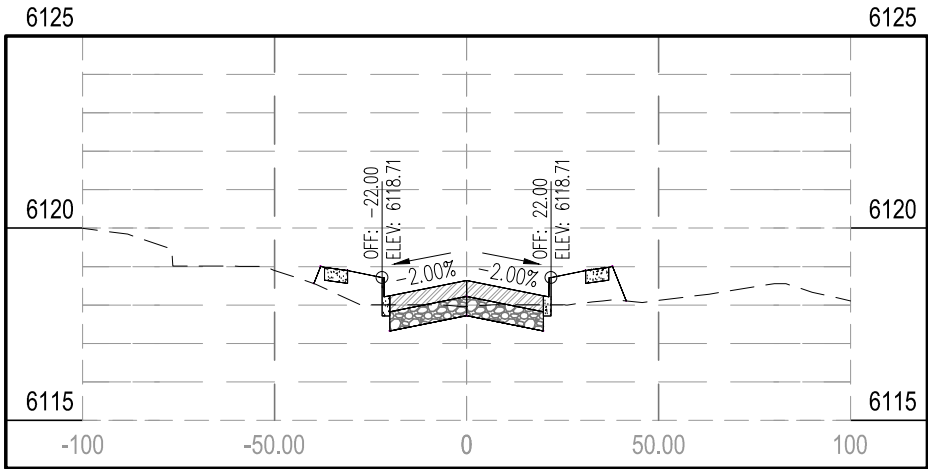


STA 2+00.00

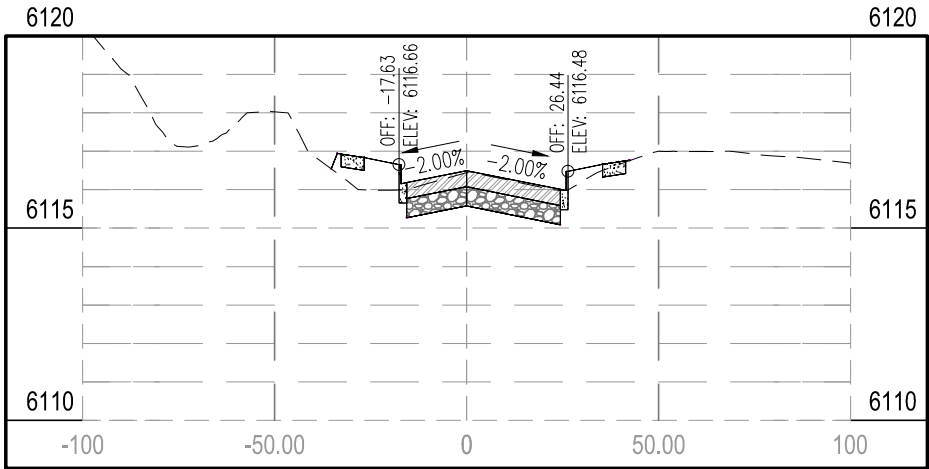

STA 5+00.00

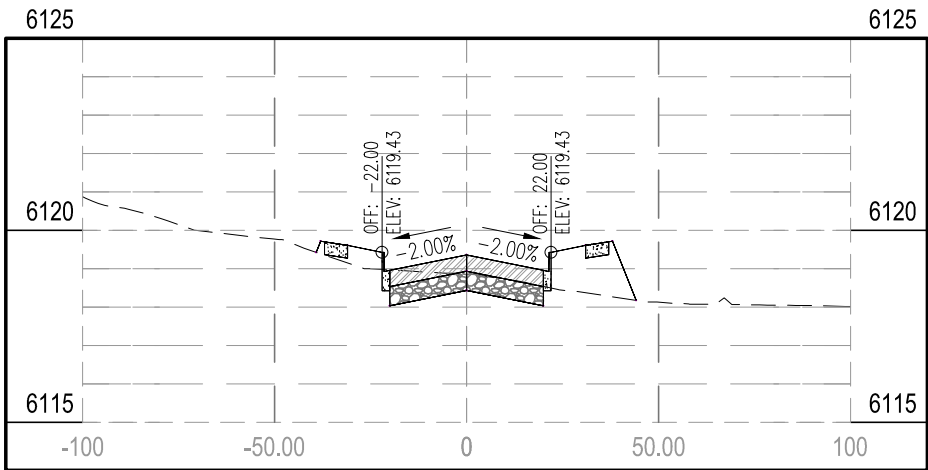

STA 1+00.00

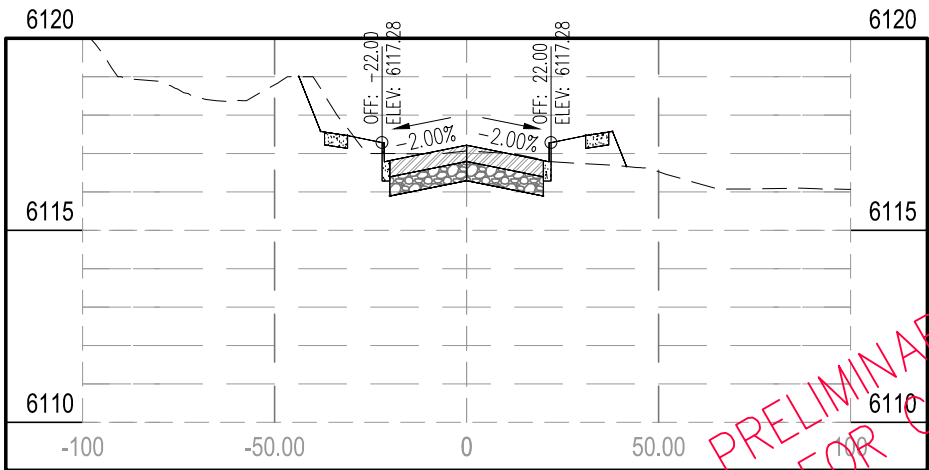

STA 4+00.00

PRELIMINARY PLANS  
NOT FOR CONSTRUCTION

| NO. |  | REVISION |  | DATE |  |
|-----|--|----------|--|------|--|
|     |  |          |  |      |  |
|     |  |          |  |      |  |
|     |  |          |  |      |  |
|     |  |          |  |      |  |

PROJECT: FOX FARM ROAD STREET IMPROVEMENTS

DRAWING TITLE: FOX FARM RD. CROSS SECTIONS STA. 1+00 - 6+00

PREPARED FOR: MPO 2101 O'NEIL AVE. RM 205 CHEYENNE, WY. 82001

DATE: 6-20-13

DRAWN BY: SRL

DESIGNED BY: TC

CHECKED BY: TC


JOB NO.: 2-3211-B

XS-01 83


SHEET NO. OF

avi p.c. engineering planning surveying


PHONE (307) 637-6017 1103 OLD TOWN LANE, SUITE 101 CHEYENNE, WY 82009 AVI@AVIFC.COM

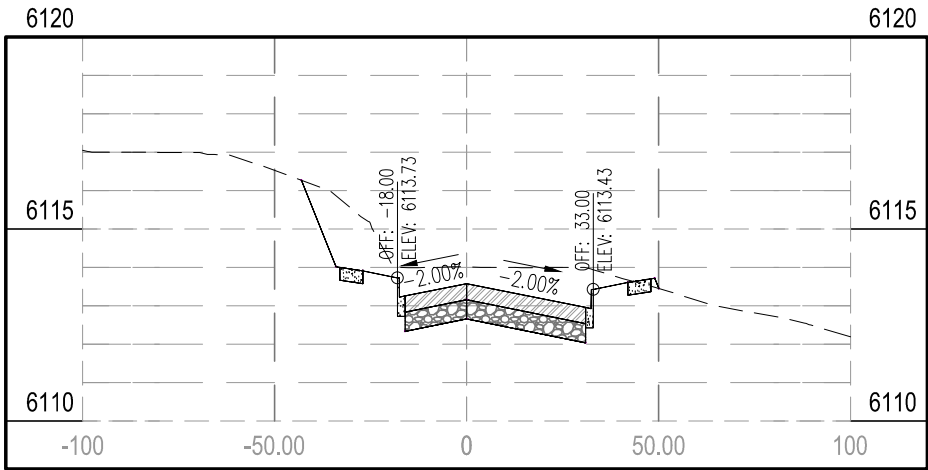


STA 9+00.00

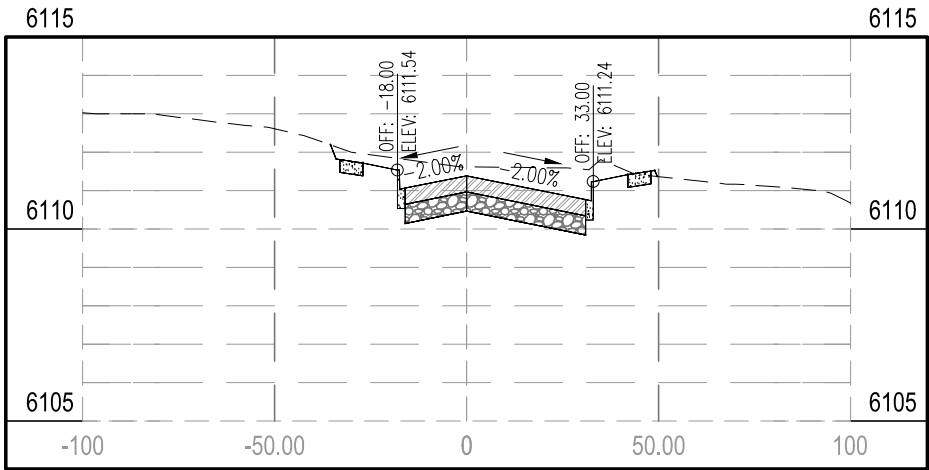


STA 12+00.00

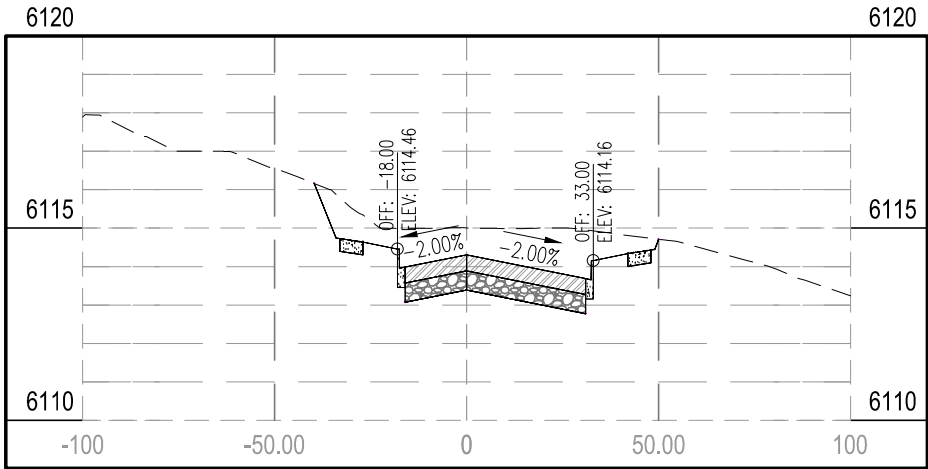


STA 8+00.00

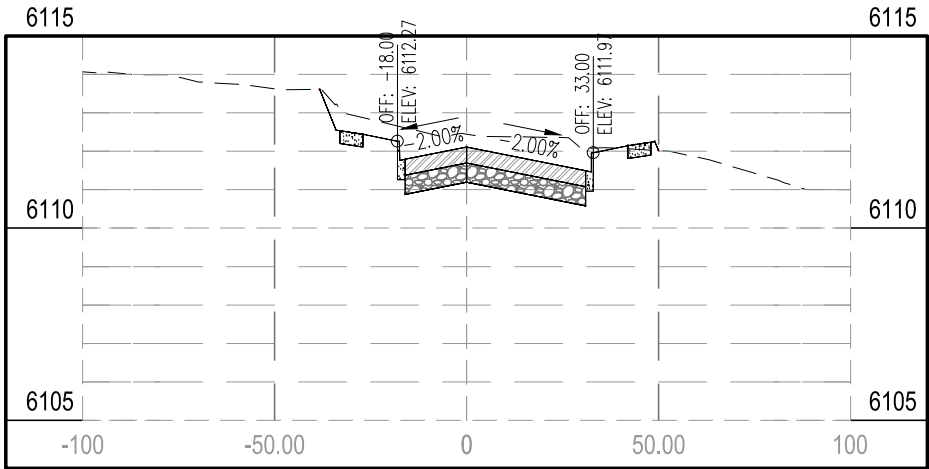

STA 11+00.00

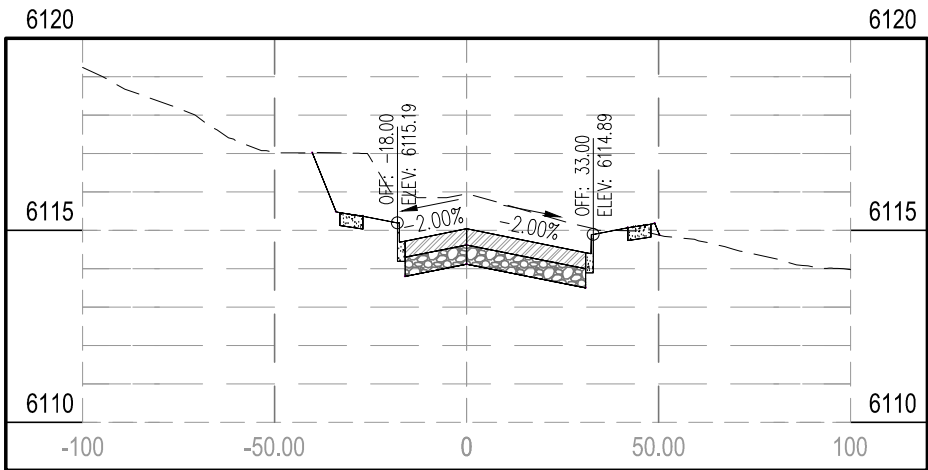

STA 7+00.00

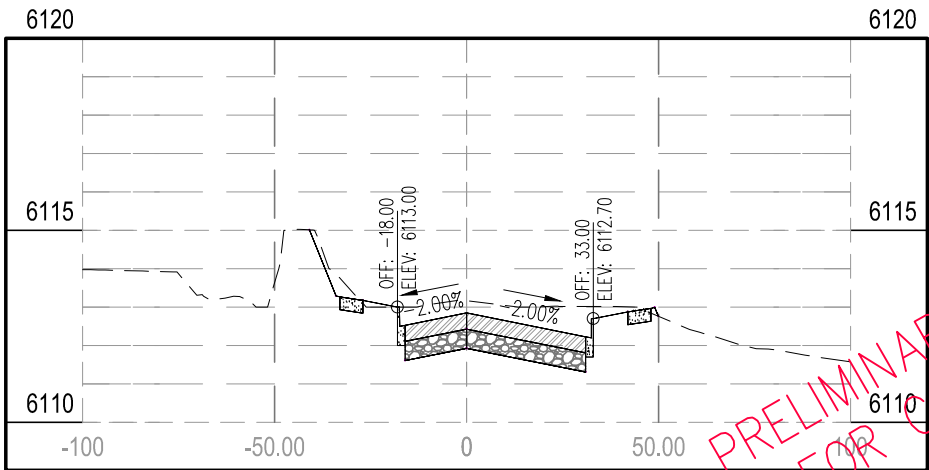

STA 10+00.00

PRELIMINARY PLANS  
NOT FOR CONSTRUCTION

| NO. | REVISION | DATE |
|-----|----------|------|
|     |          |      |
|     |          |      |
|     |          |      |
|     |          |      |

PREPARED FOR:  
MPO  
2101 ONEIL AVE.  
RM 205  
CHEYENNE, WY. 82001


PROJECT: FOX FARM ROAD STREET IMPROVEMENTS  
DRAWING TITLE: FOX FARM RD. CROSS SECTIONS STA. 7+00 - 12+00

avi p.c.  
engineering  
planning  
surveying  
PHONE (307) 637-6017  
1103 OLD TOWN LANE, SUITE 101  
CHEYENNE, WY 82009  
AVI@AVIPC.COM


DATE: 6-20-13  
DRAWN BY: SRL  
DESIGNED BY: TC  
CHECKED BY: TC

JOB NO.: 2-3211-B


XS-02 83  
SHEET NO. OF

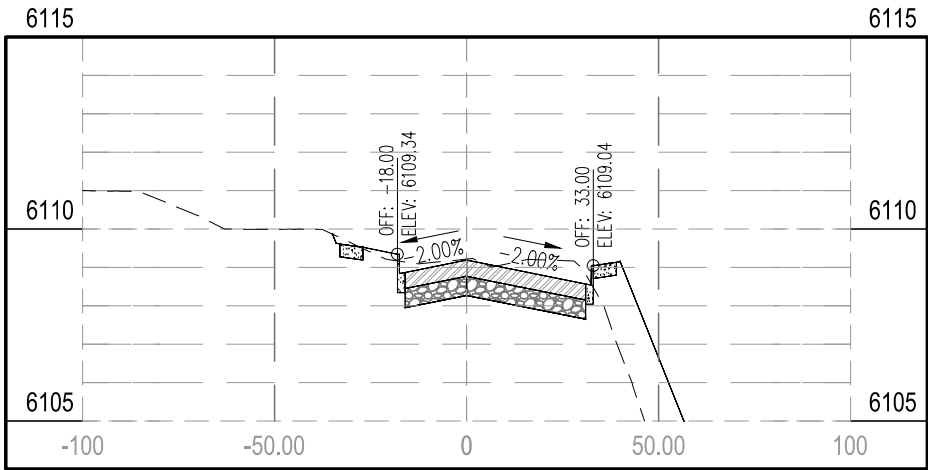


STA 15+00.00

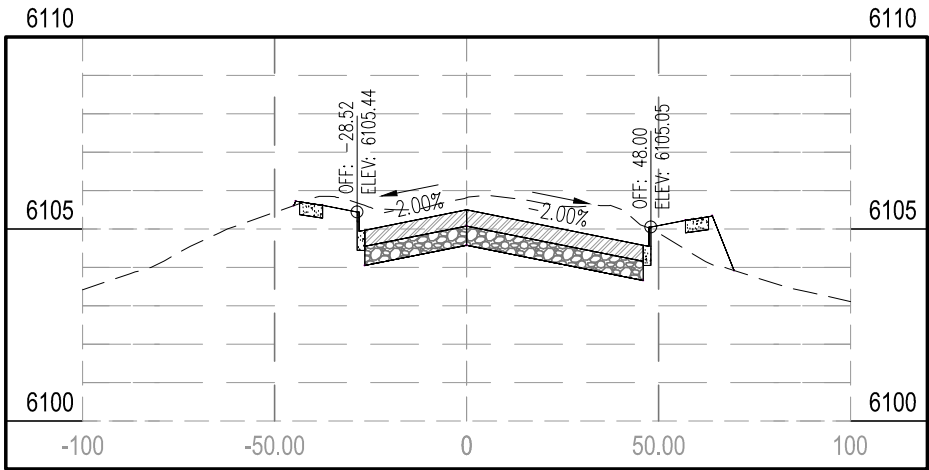


STA 18+00.00

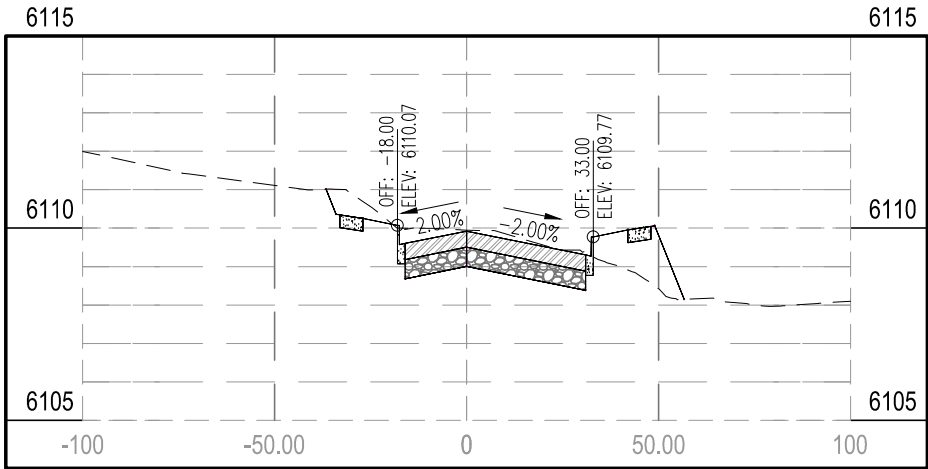


STA 14+00.00

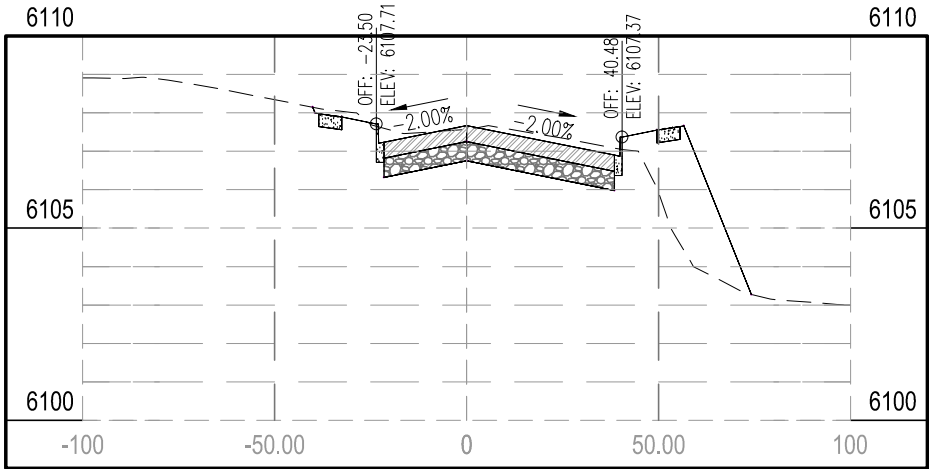

STA 17+00.00

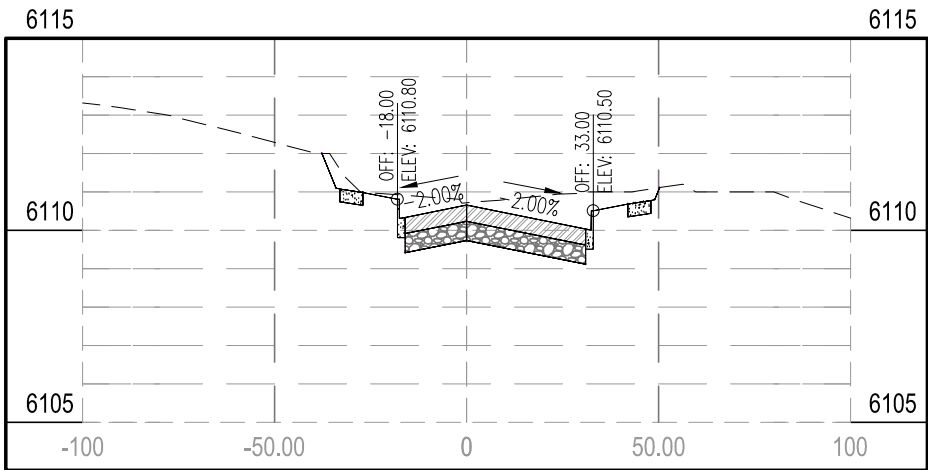

STA 13+00.00

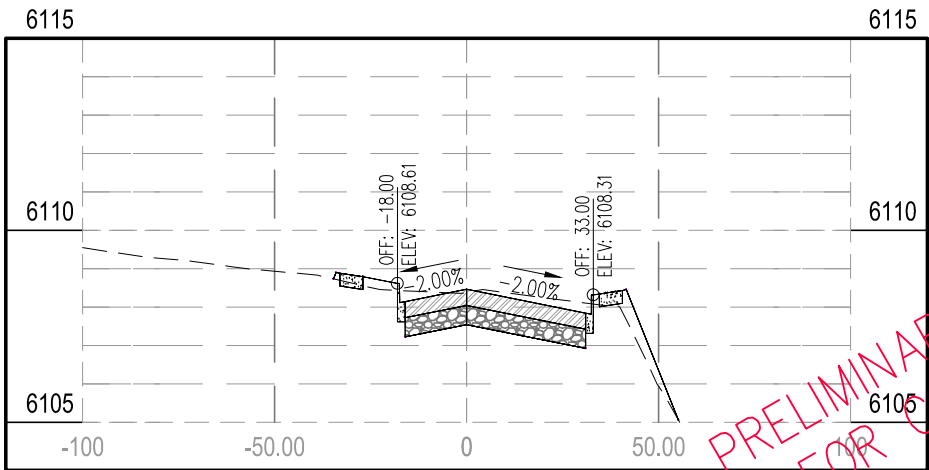

STA 16+00.00

PRELIMINARY PLANS  
NOT FOR CONSTRUCTION

| NO. | REVISION | DATE |
|-----|----------|------|
|     |          |      |
|     |          |      |
|     |          |      |
|     |          |      |

PREPARED FOR:  
MPO  
2101 ONEIL AVE.  
RM 205  
CHEYENNE, WY. 82001

PROJECT: FOX FARM ROAD STREET IMPROVEMENTS  
DRAWING TITLE: FOX FARM RD. CROSS SECTIONS STA. 13+00 - 18+00

avi p.c.  
engineering  
planning  
surveying  
PHONE (307) 637-6017  
1103 OLD TOWN LANE, SUITE 101  
CHEYENNE, WY 82009  
AVI@AVIIPC.COM


DATE: 6-20-13  
DRAWN BY: SRL  
DESIGNED BY: TC  
CHECKED BY: TC

JOB NO.: 2S-3211-B


XS-03 83  
SHEET NO. OF




STA 21+00.00

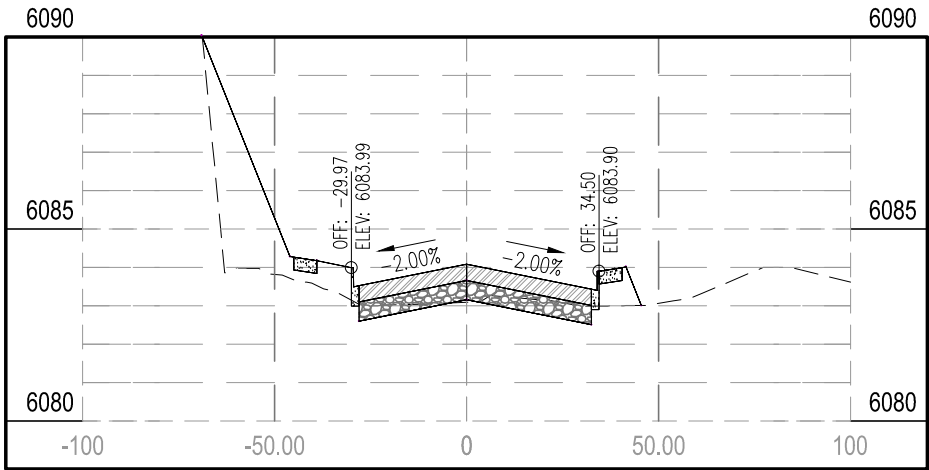


STA 24+00.00

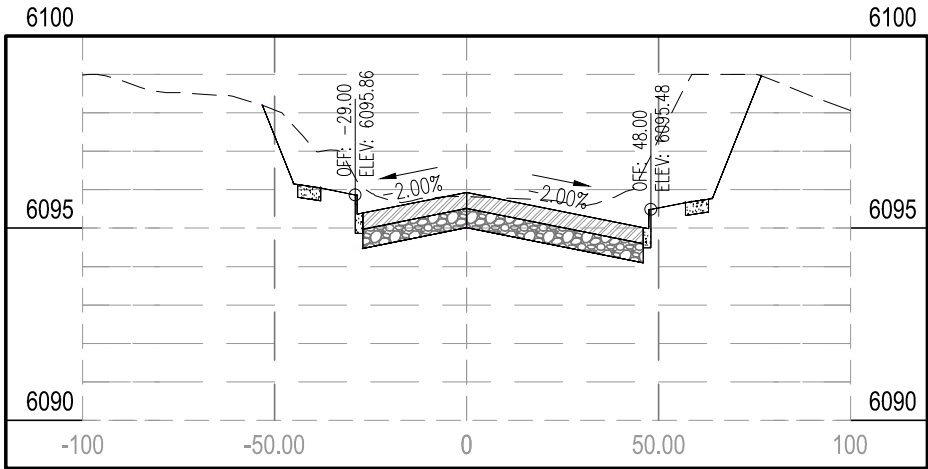


STA 20+00.00

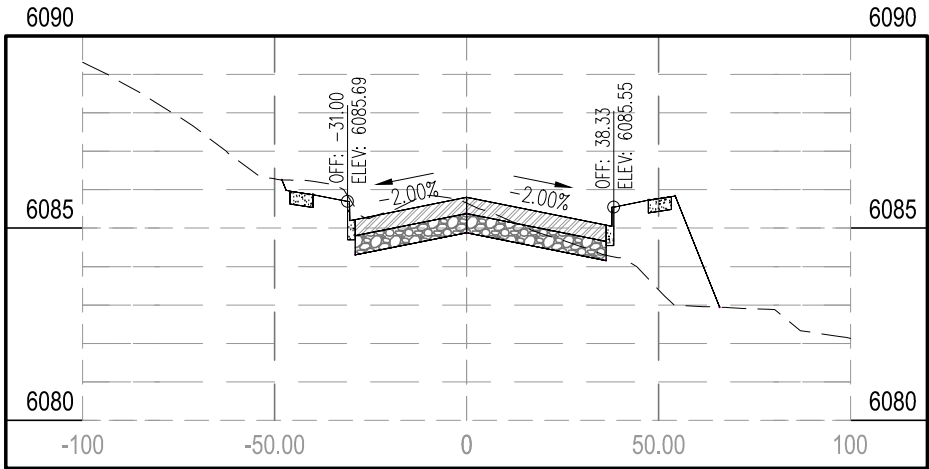

STA 23+00.00

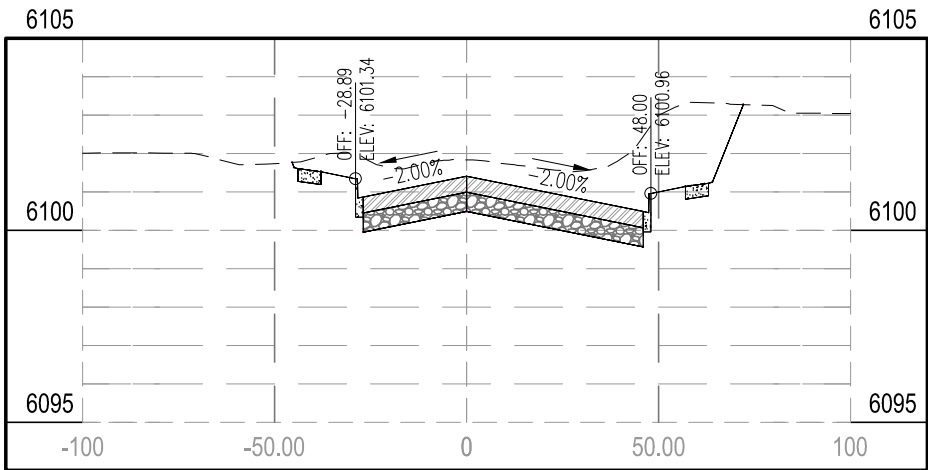

STA 19+00.00

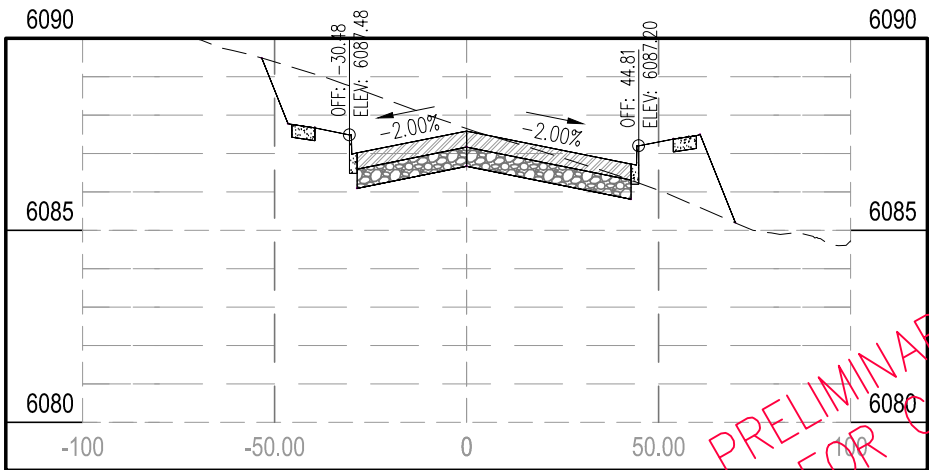

STA 22+00.00

PRELIMINARY PLANS  
NOT FOR CONSTRUCTION

| NO. | REVISION | DATE |
|-----|----------|------|
|     |          |      |
|     |          |      |
|     |          |      |
|     |          |      |

PREPARED FOR:  
MPO  
2101 ONEIL AVE.  
RM 205  
CHEYENNE, WY. 82001


PROJECT: FOX FARM ROAD STREET IMPROVEMENTS  
DRAWING TITLE: FOX FARM RD. CROSS SECTIONS STA. 19+00 - 24+00

avi p.c.  
engineering  
planning  
surveying  
PHONE (307) 637-6017  
1103 OLD TOWN LANE, SUITE 101  
CHEYENNE, WY 82009  
AVI@AVIIPC.COM


DATE: 6-20-13  
DRAWN BY: SRL  
DESIGNED BY: TC  
CHECKED BY: TC

JOB NO.: 2-3211-B


XS-04 83  
SHEET NO. OF

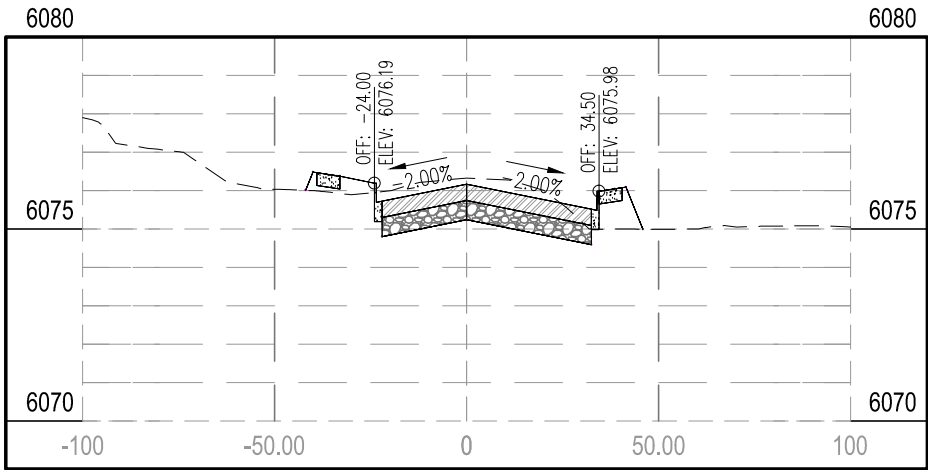


STA 27+00.00

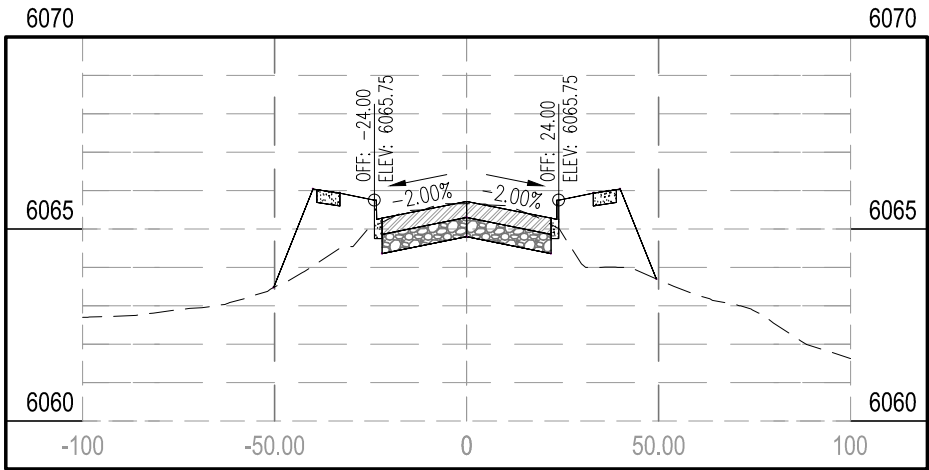


STA 30+00.00

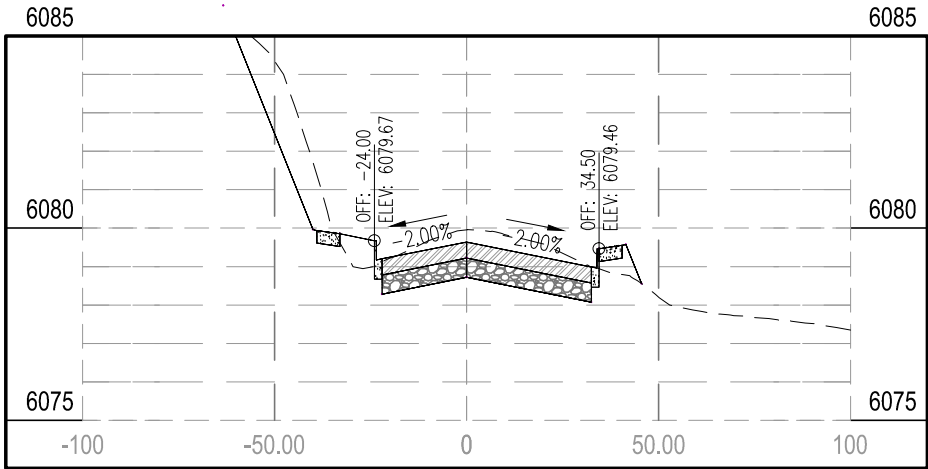


STA 26+00.00

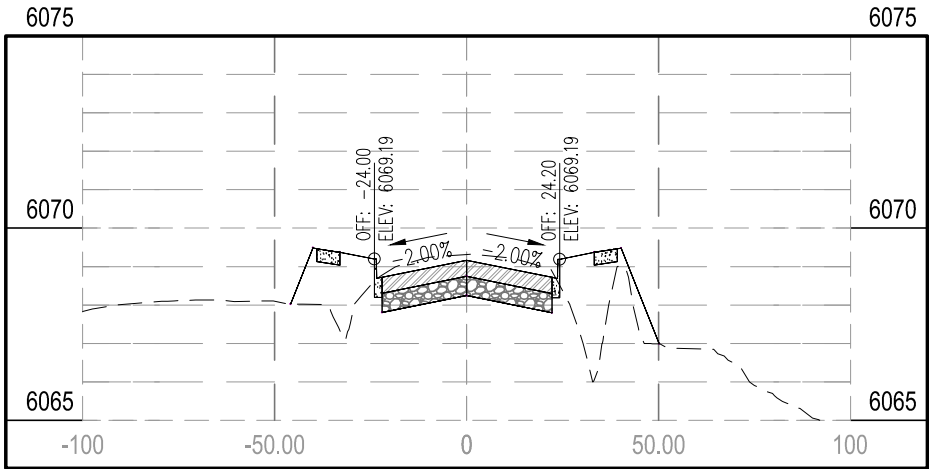

STA 29+00.00

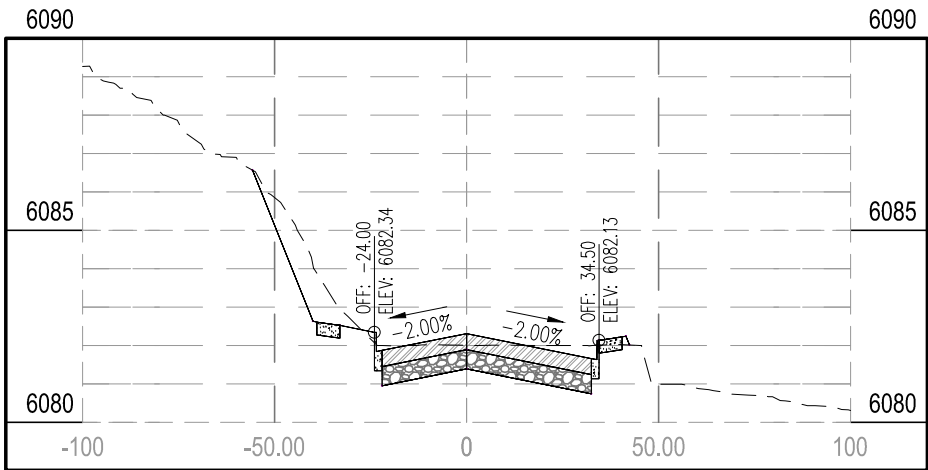

STA 25+00.00

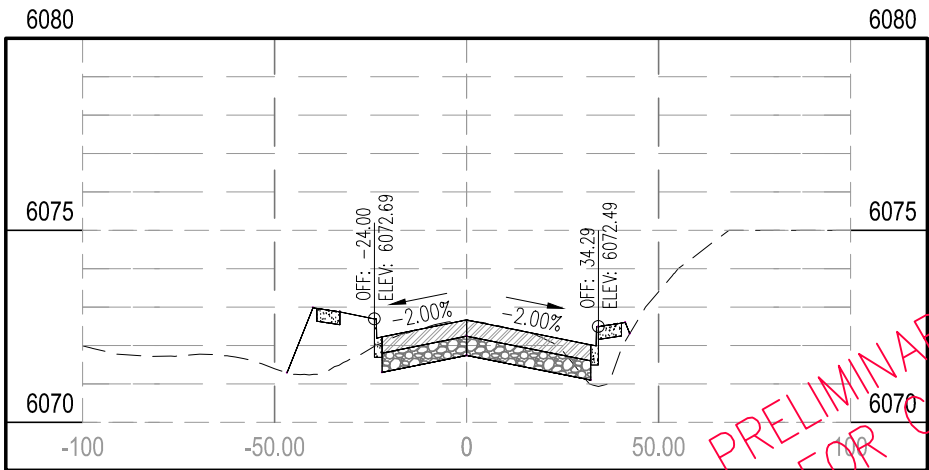

STA 28+00.00

PRELIMINARY PLANS  
NOT FOR CONSTRUCTION

| NO. | REVISION | DATE |
|-----|----------|------|
|     |          |      |
|     |          |      |
|     |          |      |
|     |          |      |

PREPARED FOR:  
MPO  
2101 ONEIL AVE.  
RM 205  
CHEYENNE, WY. 82001







PROJECT: FOX FARM ROAD STREET IMPROVEMENTS  
DRAWING TITLE: FOX FARM RD. CROSS SECTIONS STA. 25+00 - 30+00

avi p.c.  
engineering  
planning  
surveying  
PHONE (307) 637-6017  
1103 OLD TOWN LANE, SUITE 101  
CHEYENNE, WY 82009  
AVI@AVIPC.COM

DATE: 6-20-13  
DRAWN BY: SRL  
DESIGNED BY: TC  
CHECKED BY: TC

JOB NO.: 2-3211-B

XS-05 83  
SHEET NO. OF

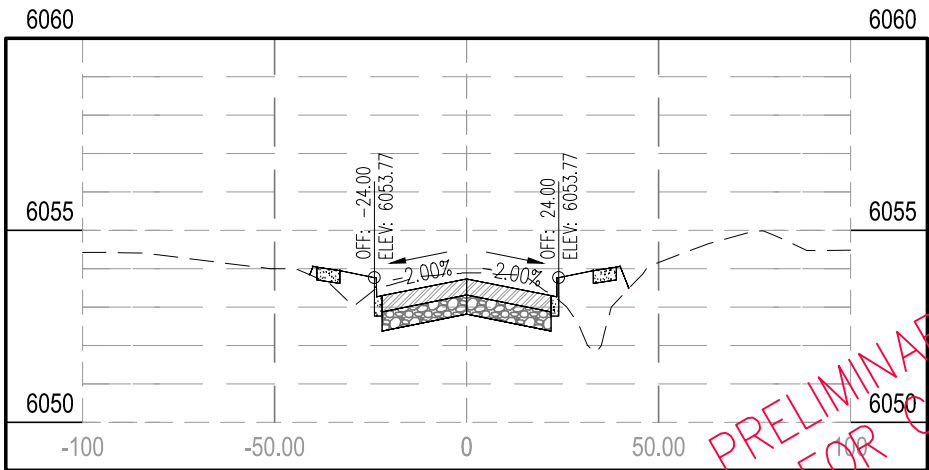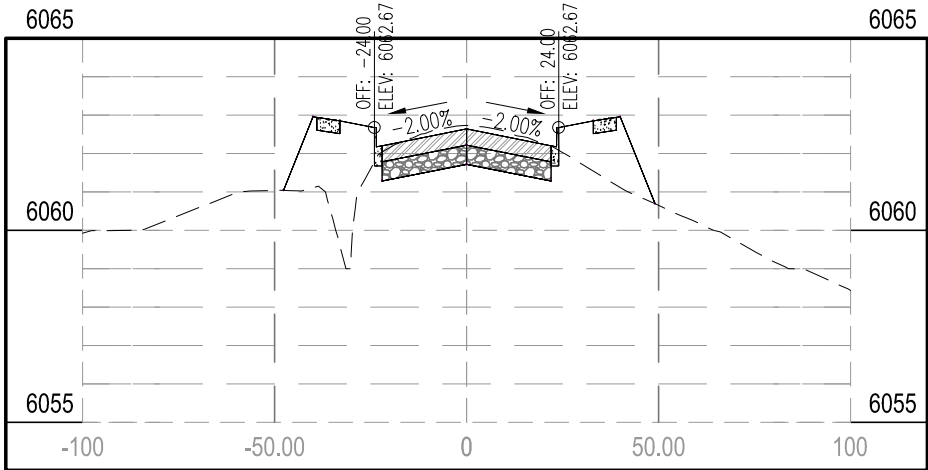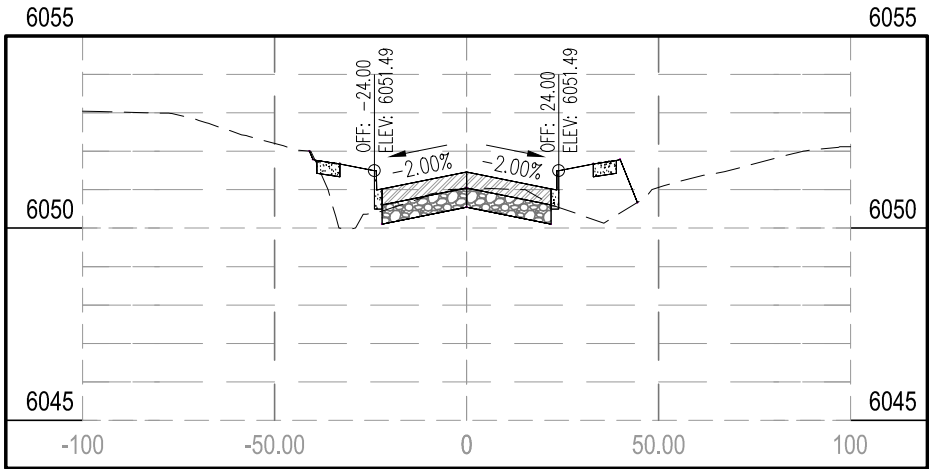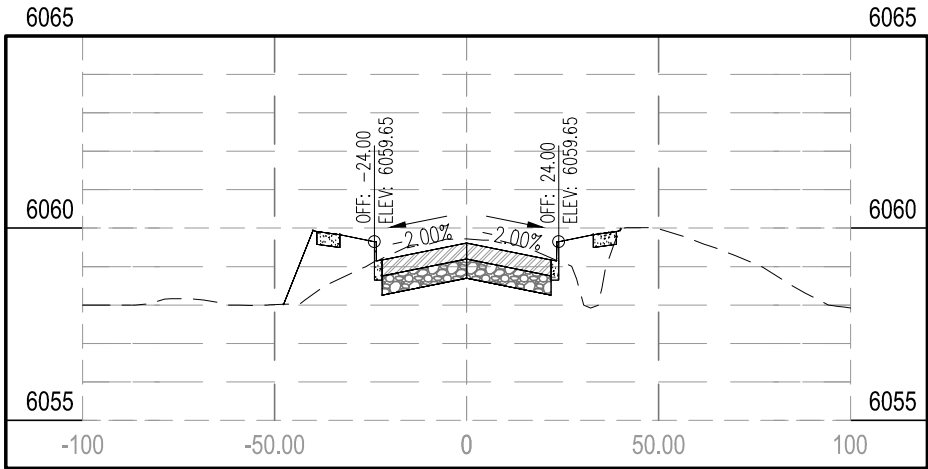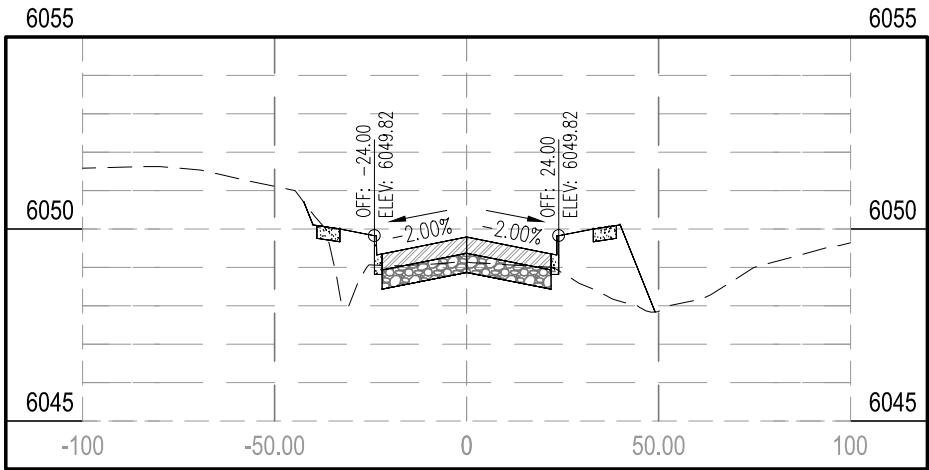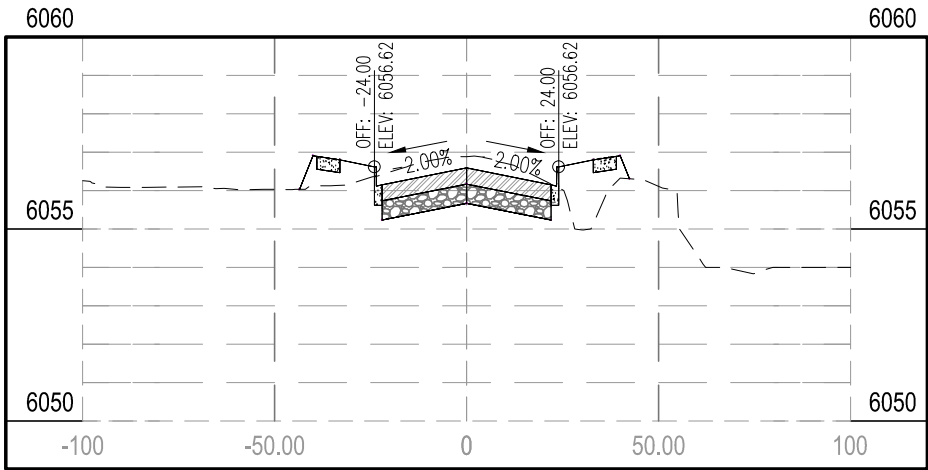

PRELIMINARY PLANS  
NOT FOR CONSTRUCTION

| NO. | REVISION | DATE |
|-----|----------|------|
|     |          |      |
|     |          |      |
|     |          |      |
|     |          |      |

PREPARED FOR:  
MPO  
2101 ONEIL AVE.  
RM 205  
CHEYENNE, WY. 82001


PROJECT: FOX FARM ROAD STREET IMPROVEMENTS  
DRAWING TITLE: FOX FARM RD. CROSS SECTIONS STA. 31+00 - 36+00

avi p.c.  
engineering  
planning  
surveying  
PHONE (307) 637-6017  
1103 OLD TOWN LANE, SUITE 101  
CHEYENNE, WY 82009  
AVI@AVIPC.COM


DATE: 6-20-13  
DRAWN BY: SRL  
DESIGNED BY: TC  
CHECKED BY: TC

JOB NO.: 2-3211-B


XS-06 83  
SHEET NO. OF

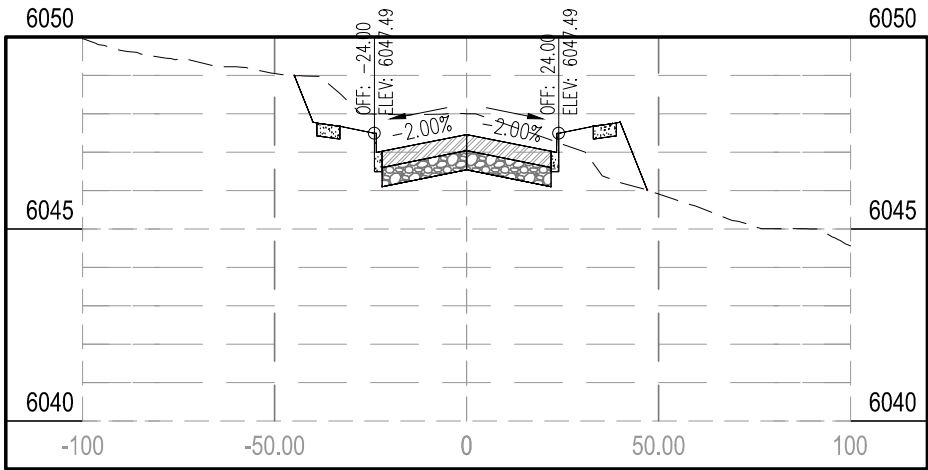


STA 39+00.00

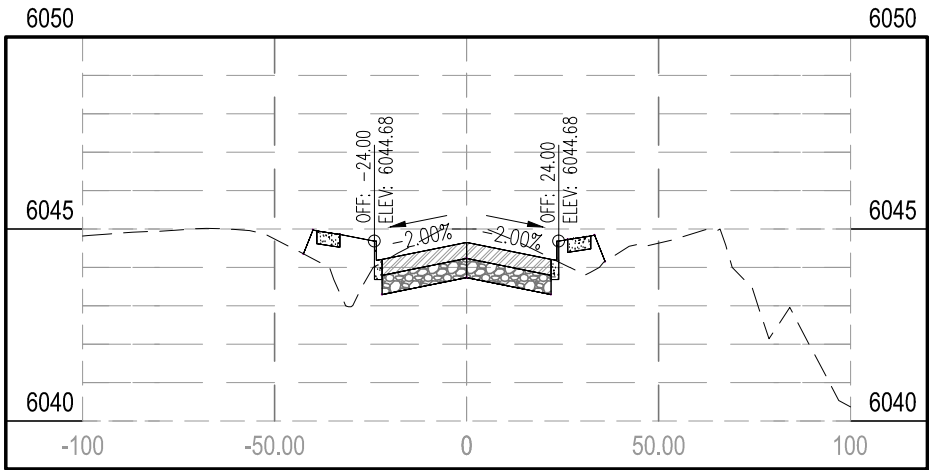


STA 42+00.00

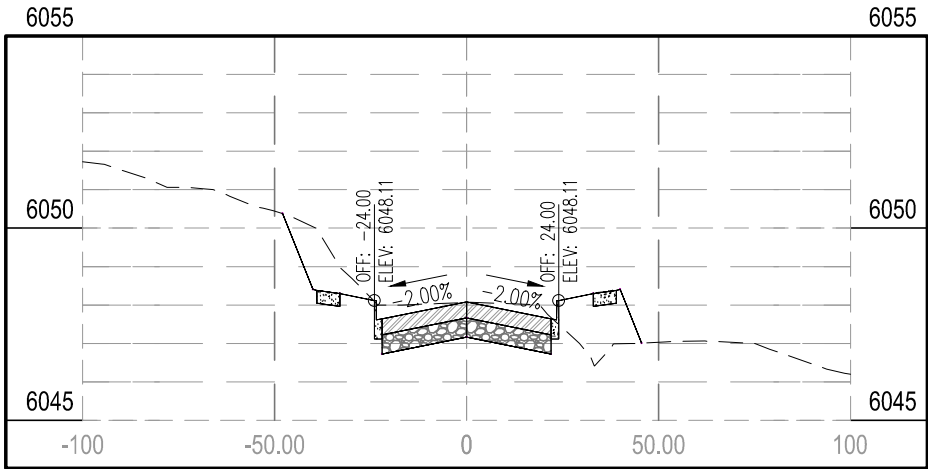


STA 38+00.00

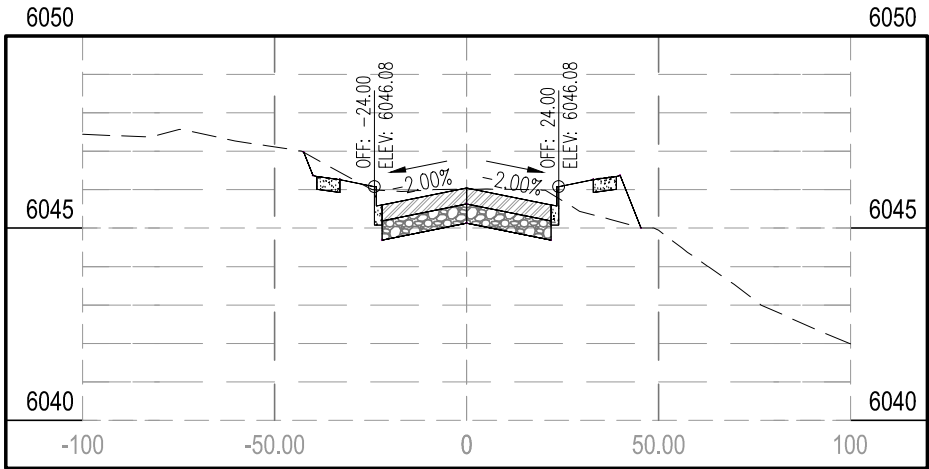

STA 41+00.00

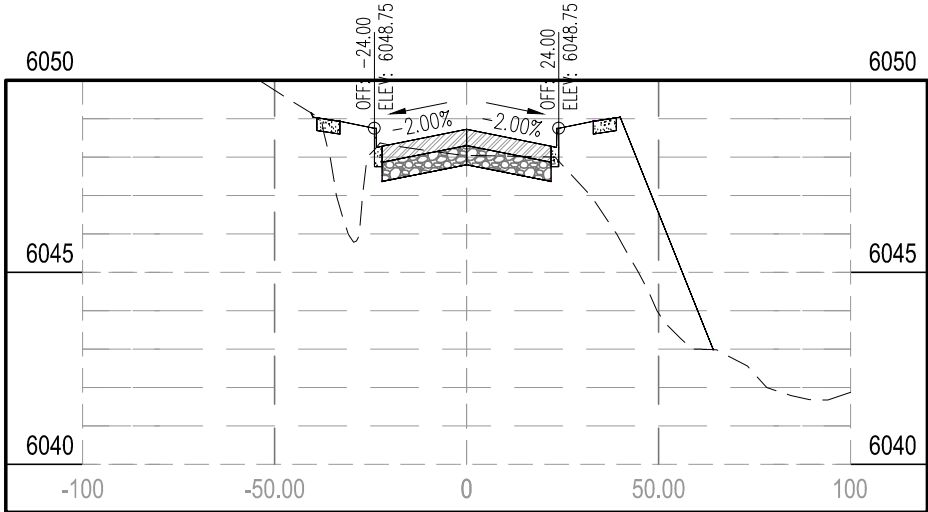

STA 37+00.00

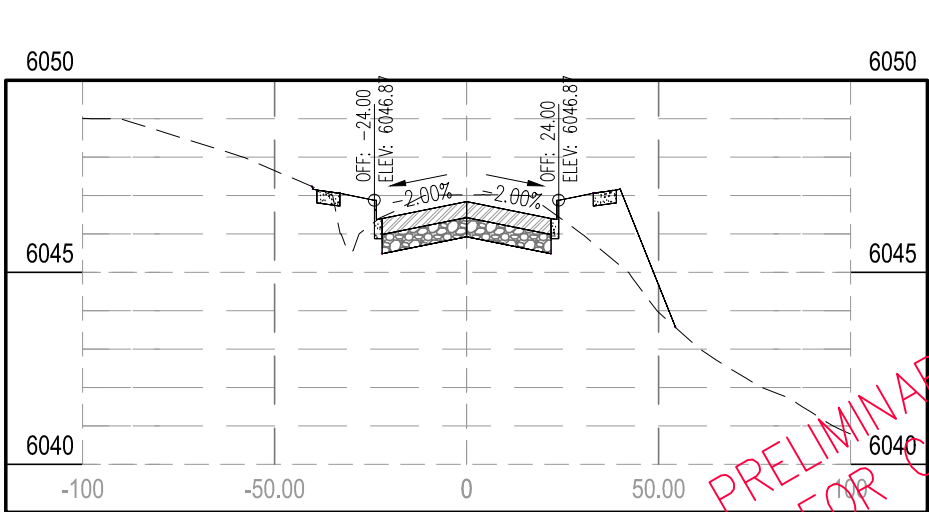

STA 40+00.00

PRELIMINARY PLANS  
NOT FOR CONSTRUCTION

| NO. | REVISION | DATE |
|-----|----------|------|
|     |          |      |
|     |          |      |
|     |          |      |
|     |          |      |

PREPARED FOR:  
MPO  
2101 ONEIL AVE.  
RM 205  
CHEYENNE, WY. 82001







PROJECT: FOX FARM ROAD STREET IMPROVEMENTS  
DRAWING TITLE: FOX FARM ROAD STREET IMPROVEMENTS

avi p.c.  
engineering  
planning  
surveying  
PHONE (307) 637-6017  
1103 OLD TOWN LANE, SUITE 101  
CHEYENNE, WY 82009  
AVI@AVIIPC.COM

DATE: 6-20-13  
DRAWN BY: SRL  
DESIGNED BY: TC  
CHECKED BY: TC

JOB NO.: 2-3211-B

XS-07 83  
SHEET NO. OF

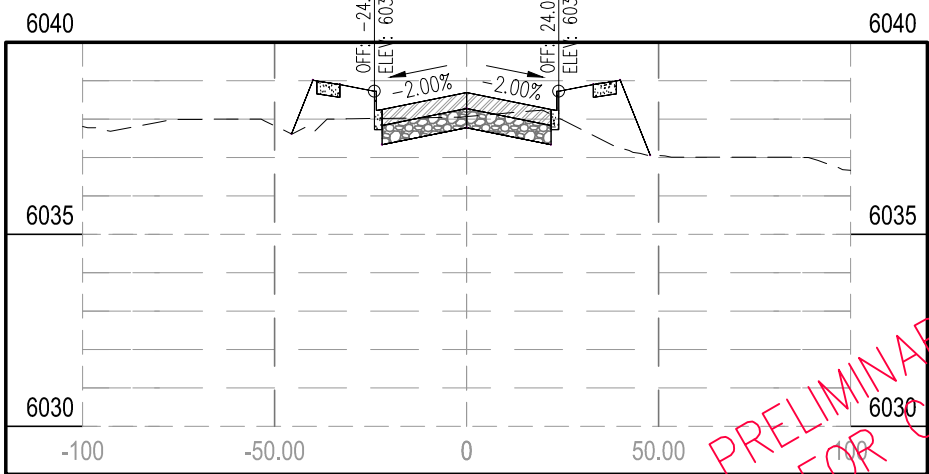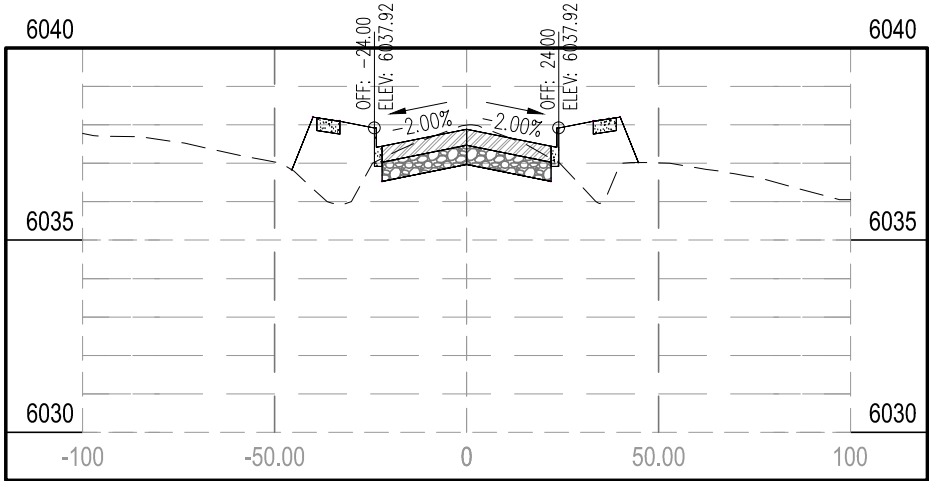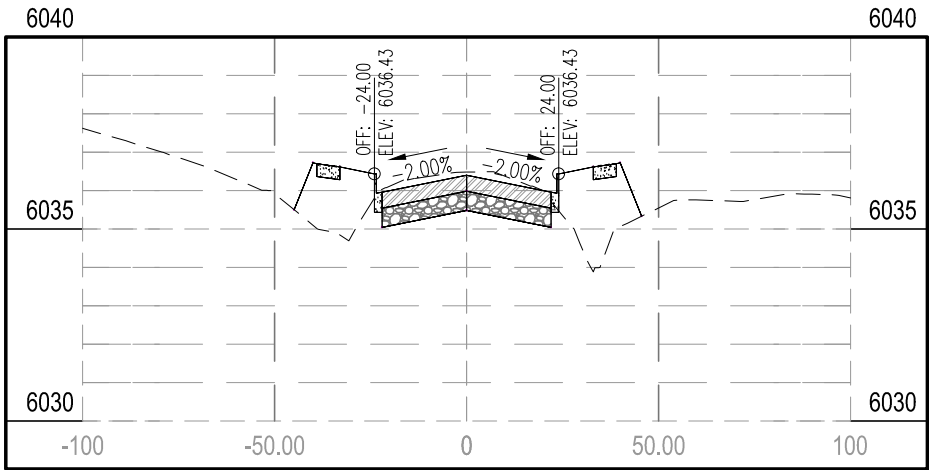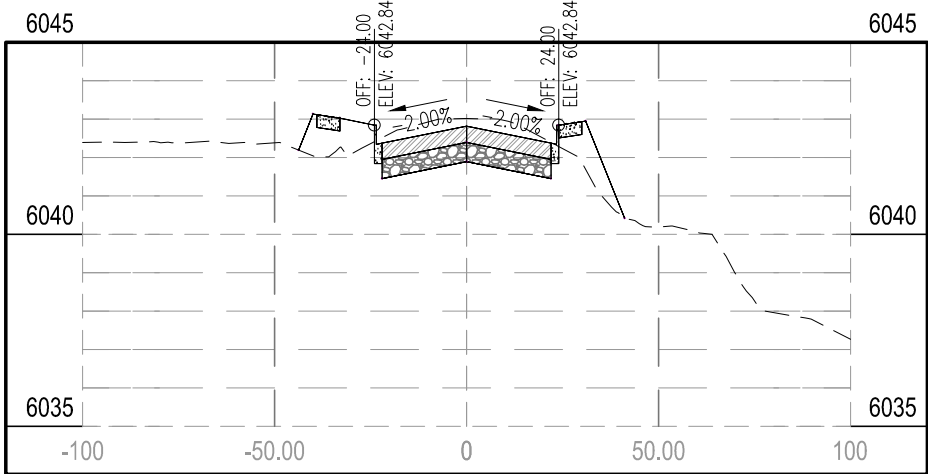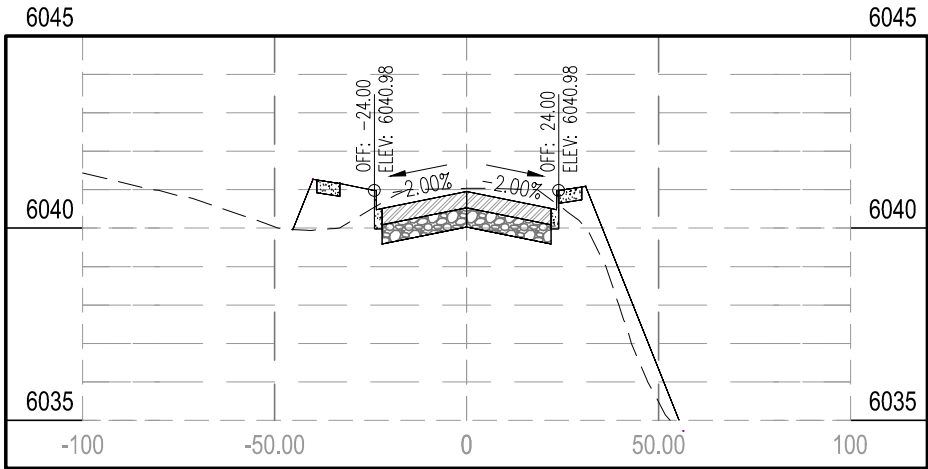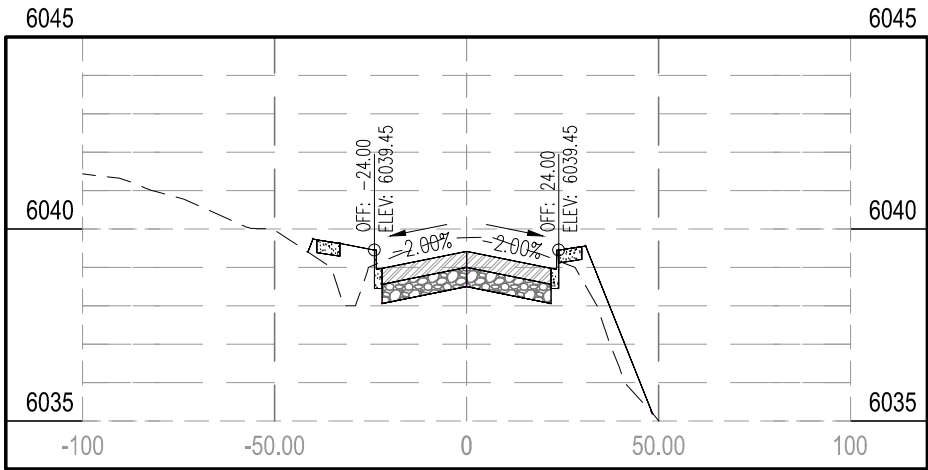

PRELIMINARY PLANS  
NOT FOR CONSTRUCTION

| NO. | REVISION | DATE |
|-----|----------|------|
|     |          |      |
|     |          |      |
|     |          |      |
|     |          |      |


PROJECT: FOX FARM ROAD STREET IMPROVEMENTS  
DRAWING TITLE: FOX FARM RD. CROSS SECTIONS STA. 43+00 - 48+00  
PREPARED FOR: MPO 2101 ONEIL AVE. RM 205 CHEYENNE, WY. 82001

DATE: 6-20-13  
DRAWN BY: SRL  
DESIGNED BY: TC  
CHECKED BY: TC


AVI p.c.  
engineering  
planning  
surveying  
PHONE (307) 637-6017  
1103 OLD TOWN LANE, SUITE 101  
CHEYENNE, WY 82009  
AVI@AVIPC.COM

JOB NO.: 2-3211-B


XS-08 83  
SHEET NO. OF

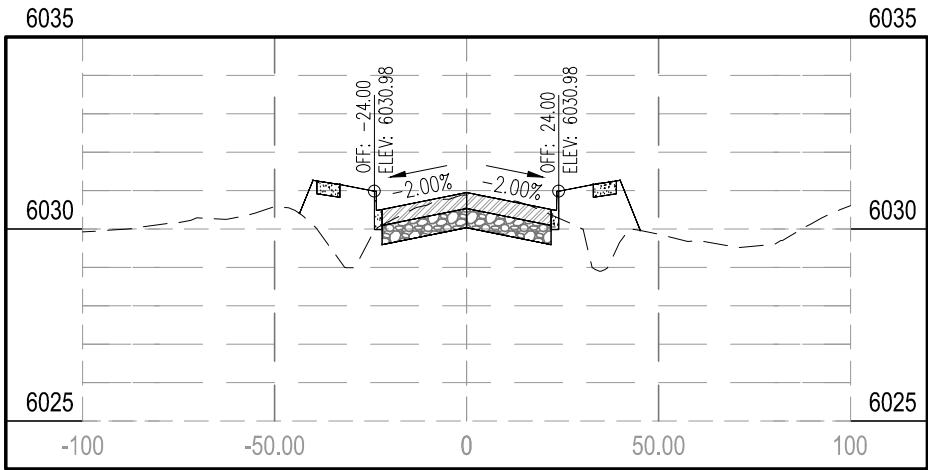


STA 51+00.00

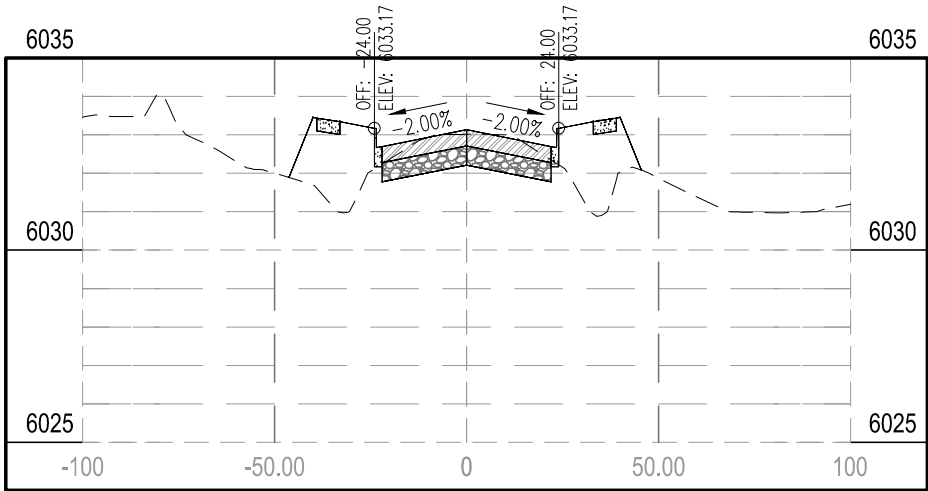


STA 50+00.00

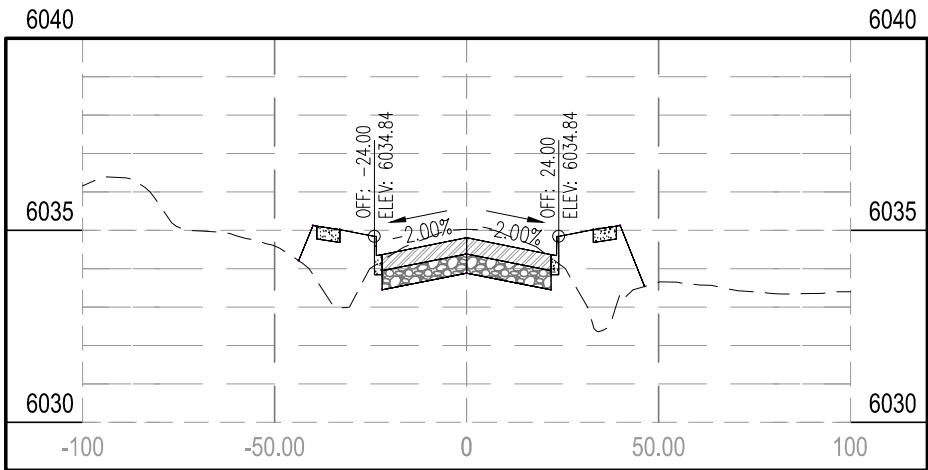


STA 49+00.00

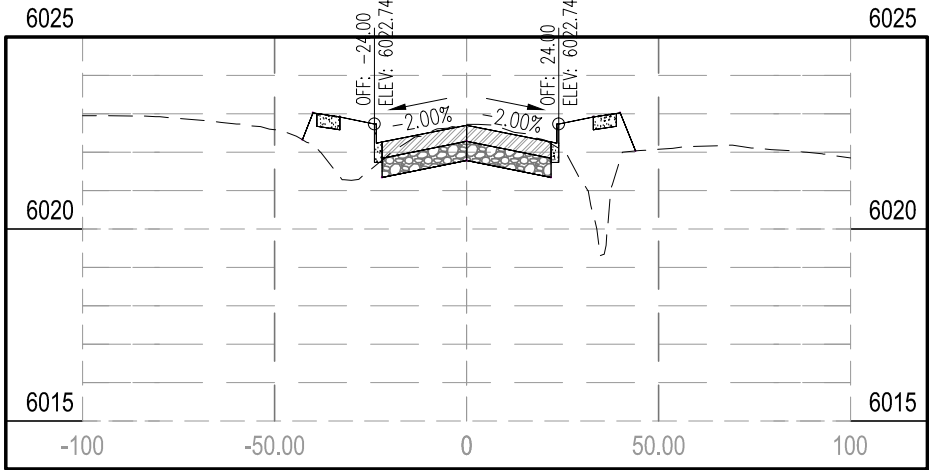

STA 54+00.00

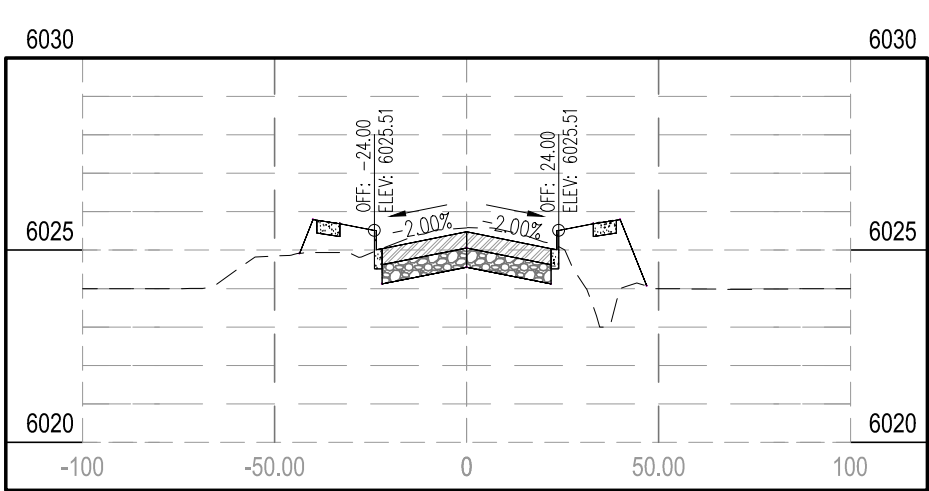

STA 53+00.00

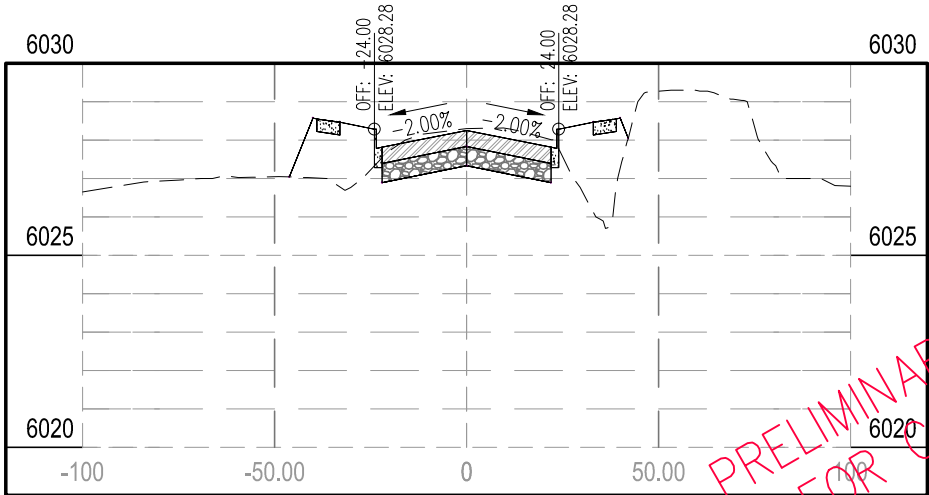

STA 52+00.00

PRELIMINARY PLANS  
NOT FOR CONSTRUCTION

| NO. |  | REVISION | DATE |
|-----|--|----------|------|
|     |  |          |      |
|     |  |          |      |
|     |  |          |      |
|     |  |          |      |

PROJECT: FOX FARM ROAD STREET IMPROVEMENTS

PREPARED FOR: MPO 2101 ONEIL AVE. RM 205 CHEYENNE, WY. 82001

DRAWING TITLE: FOX FARM RD. CROSS SECTIONS STA. 49+00 - 54+00


**avi** p.c.  
engineering  
planning  
surveying

PHONE (307) 637-6017  
1103 OLD TOWN LANE, SUITE 101  
CHEYENNE, WY 82009  
AVI@AVIPC.COM


DATE: 6-20-13  
DRAWN BY: SRL  
DESIGNED BY: TC  
CHECKED BY: TC

JOB NO.: 2-3211-B


XS-09 83  
SHEET NO. OF

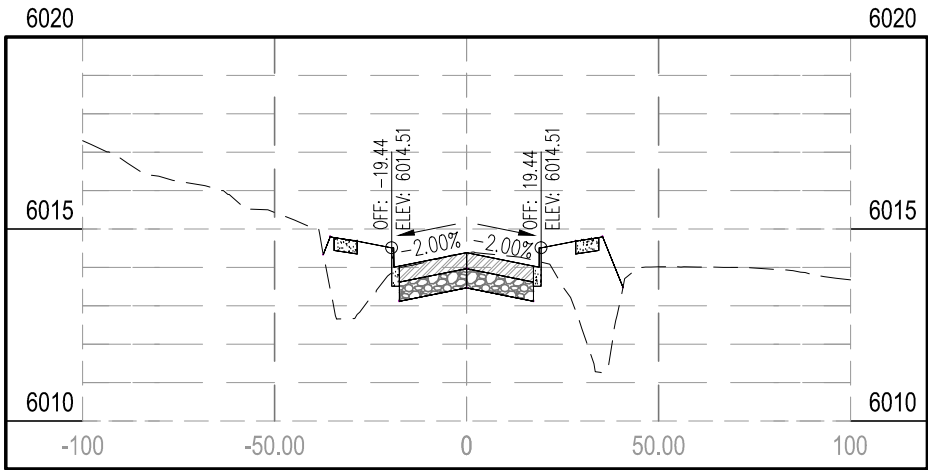


STA 57+00.00

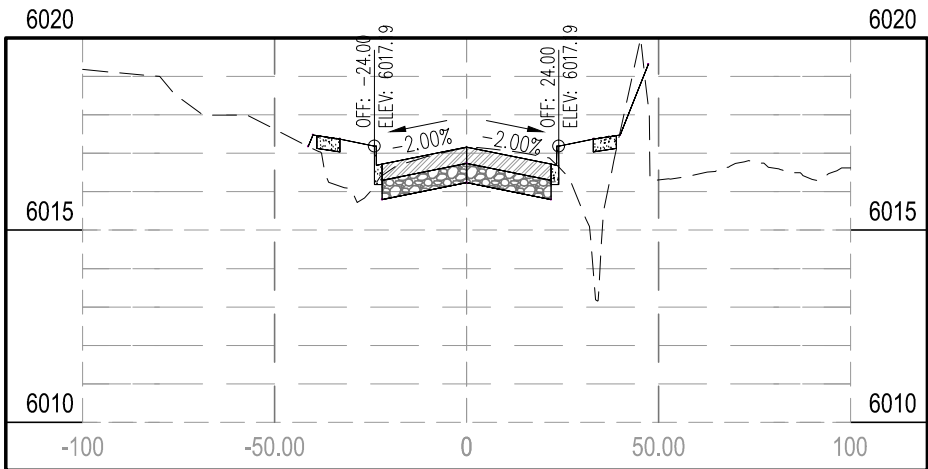


STA 56+00.00

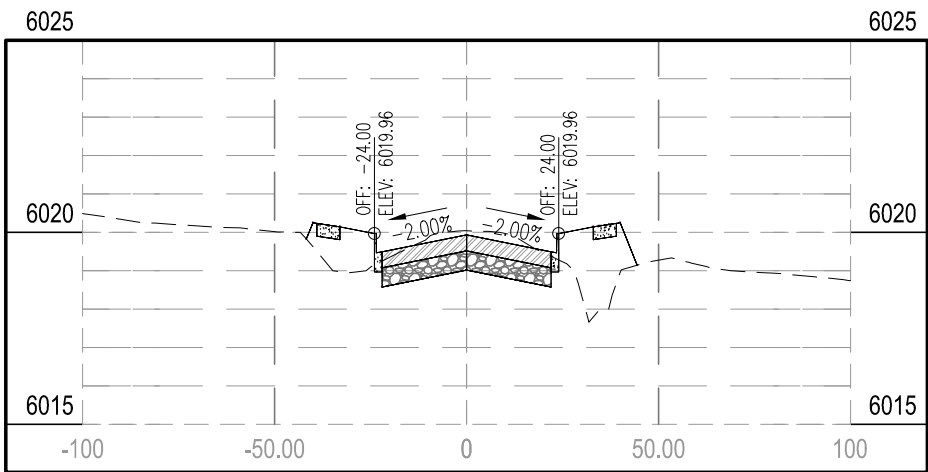


STA 55+00.00

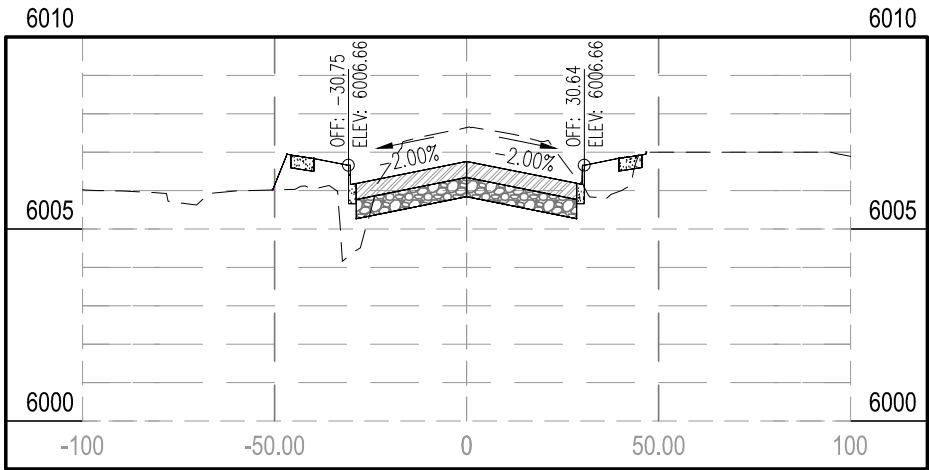

STA 60+00.00

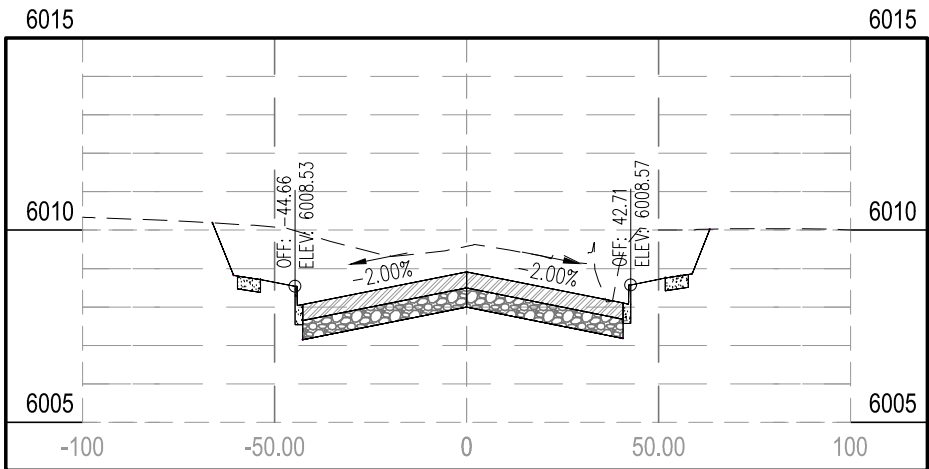

STA 59+00.00

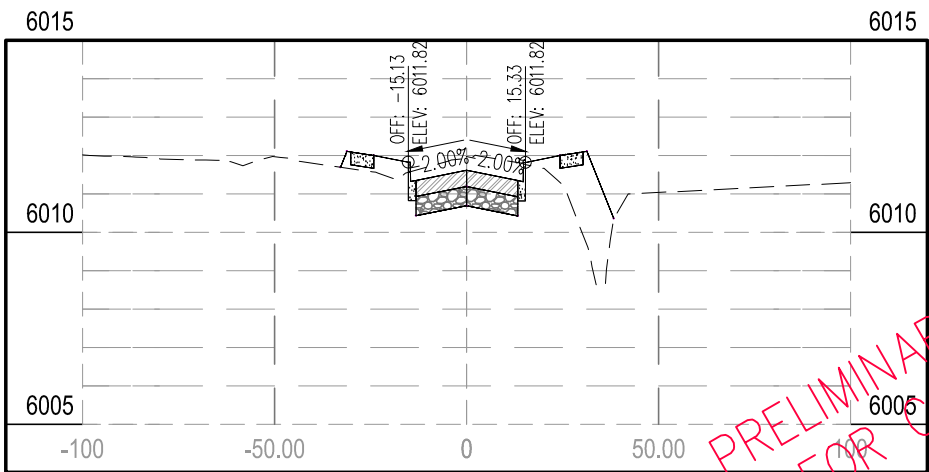

STA 58+00.00

PRELIMINARY PLANS  
NOT FOR CONSTRUCTION

| NO. | REVISION | DATE |
|-----|----------|------|
|     |          |      |
|     |          |      |
|     |          |      |
|     |          |      |

PREPARED FOR:  
MPO  
2101 ONEIL AVE.  
RM 205  
CHEYENNE, WY. 82001


PROJECT: FOX FARM ROAD STREET IMPROVEMENTS  
DRAWING TITLE: FOX FARM RD. CROSS SECTIONS STA. 55+00 - 60+00

avi p.c.  
engineering  
planning  
surveying  
PHONE (307) 637-6017  
1103 OLD TOWN LANE, SUITE 101  
CHEYENNE, WY 82009  
AVI@AVIPC.COM


DATE: 6-20-13  
DRAWN BY: SRL  
DESIGNED BY: TC  
CHECKED BY: TC

JOB NO.: 2-3211-B


XS-10 83  
SHEET NO. OF

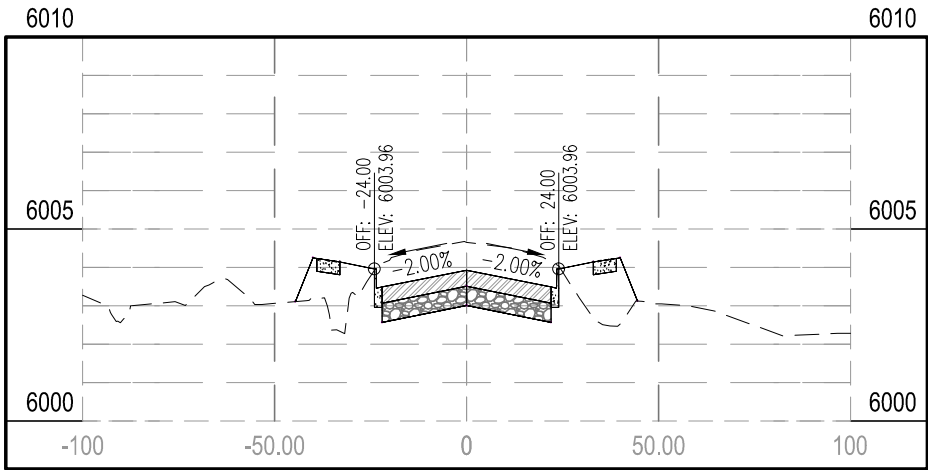


STA 63+00.00

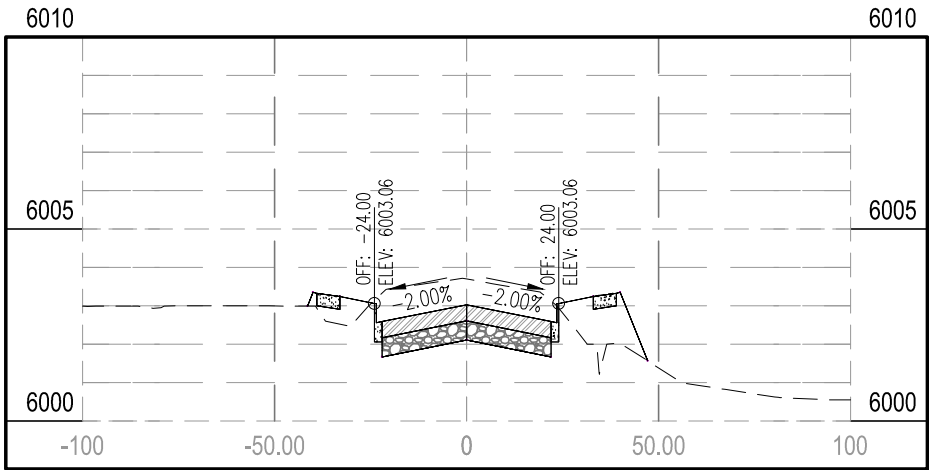


STA 66+00.00

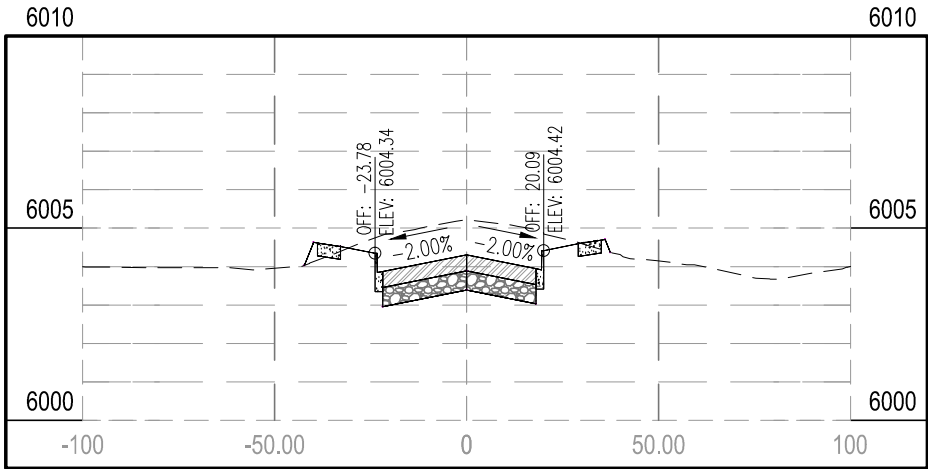


STA 62+00.00

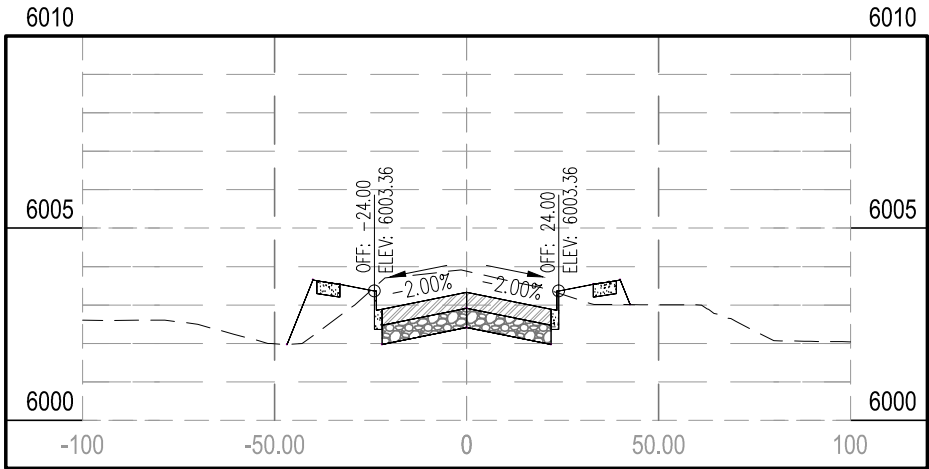

STA 65+00.00

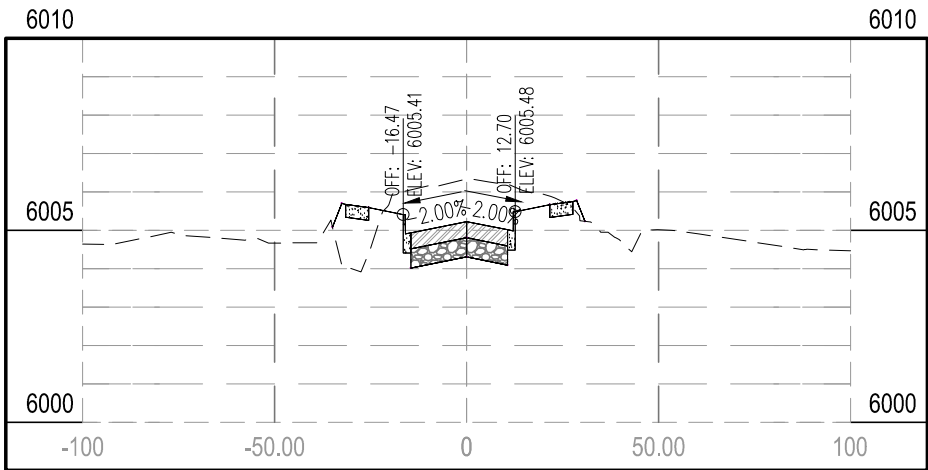

STA 61+00.00

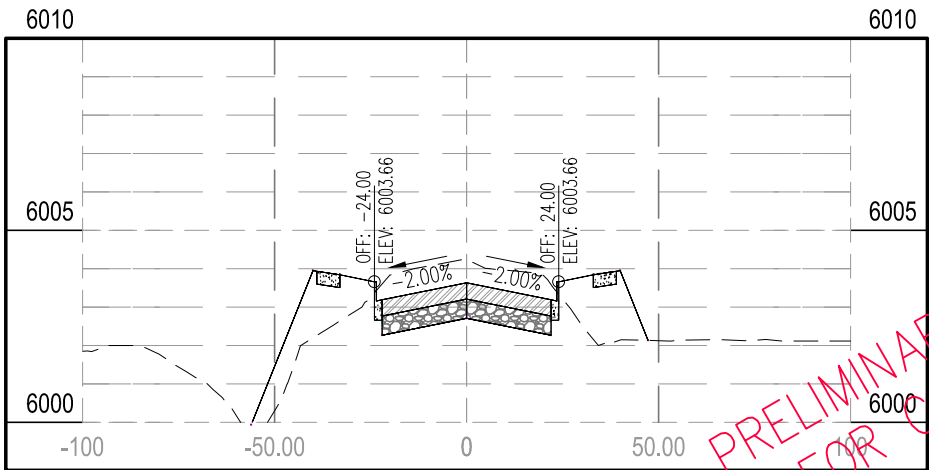

STA 64+00.00

PRELIMINARY PLANS  
NOT FOR CONSTRUCTION

| NO. | REVISION | DATE |
|-----|----------|------|
|     |          |      |
|     |          |      |
|     |          |      |
|     |          |      |

PREPARED FOR:  
MPO  
2101 ONEIL AVE.  
RM 205  
CHEYENNE, WY. 82001







PROJECT: FOX FARM ROAD STREET IMPROVEMENTS  
DRAWING TITLE: FOX FARM RD. CROSS SECTIONS STA. 61+00 - 66+00

avi p.c.  
engineering  
planning  
surveying  
PHONE (307) 637-6017  
1103 OLD TOWN LANE, SUITE 101  
CHEYENNE, WY 82009  
AVI@AVIPC.COM

DATE: 6-20-13  
DRAWN BY: SRL  
DESIGNED BY: TC  
CHECKED BY: TC

JOB NO.: 2-3211-B

XS-11 83  
SHEET NO. OF

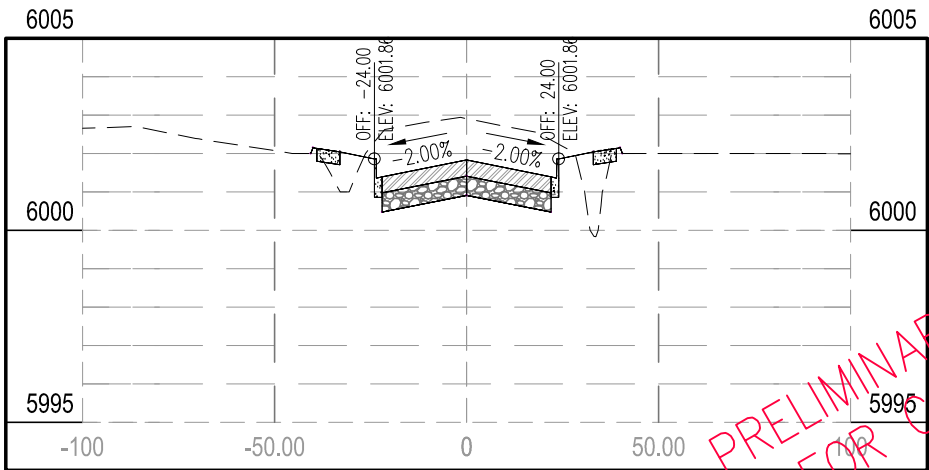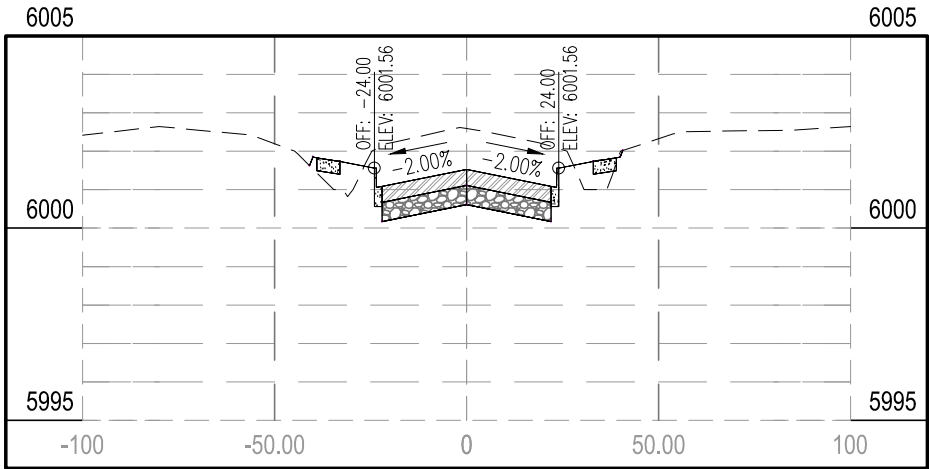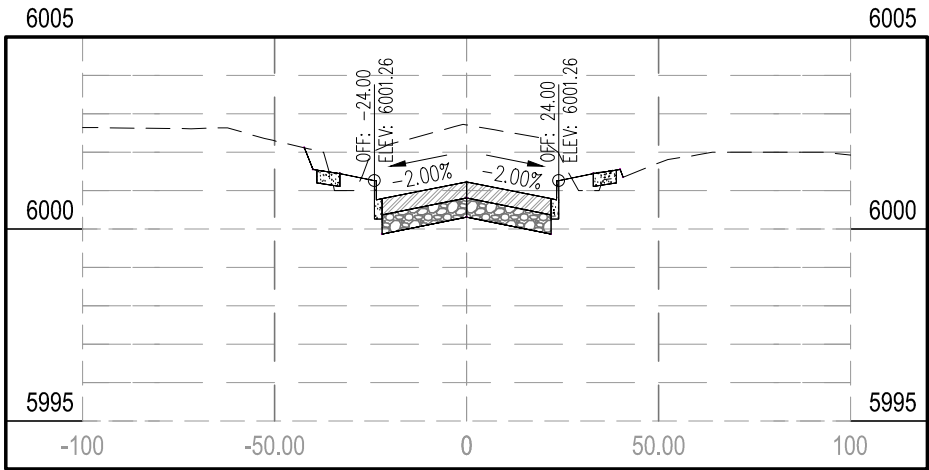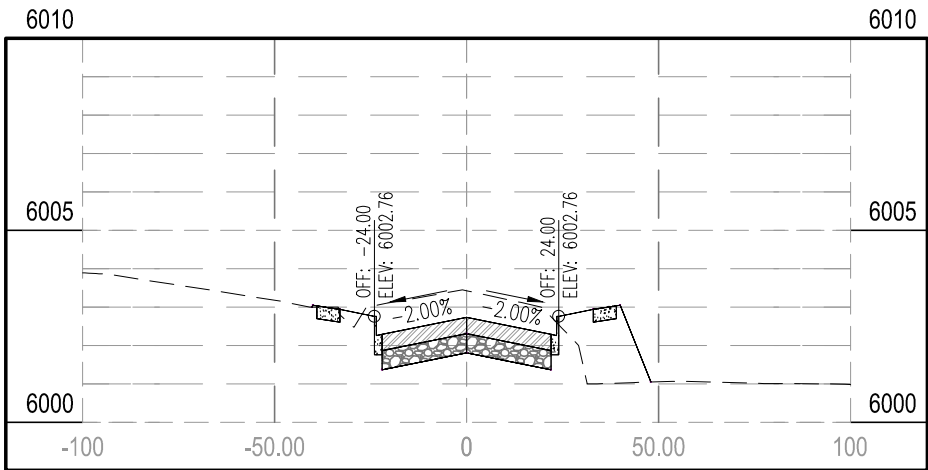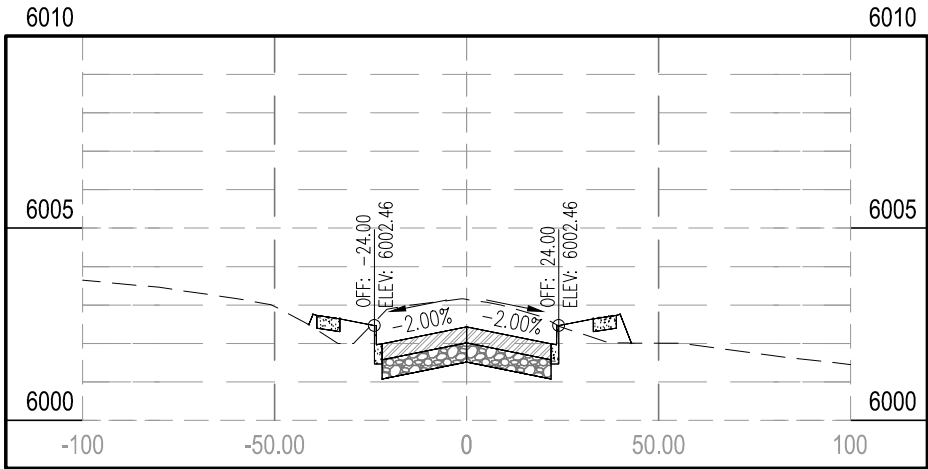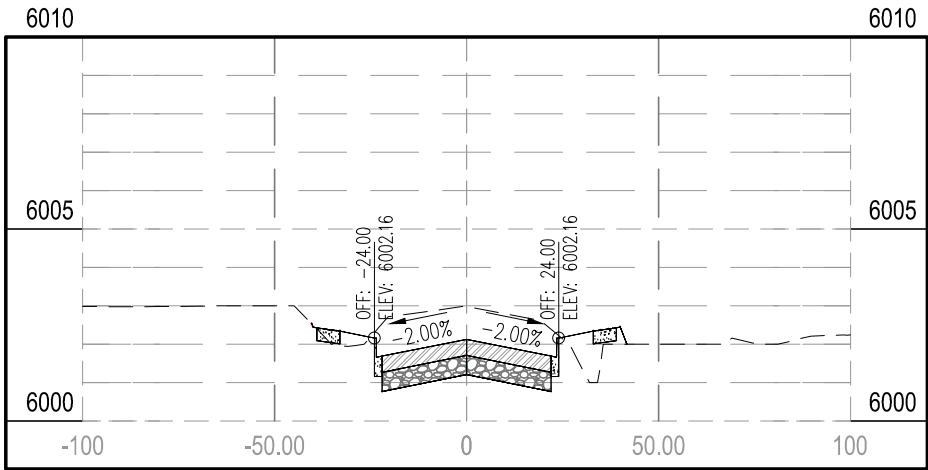

PRELIMINARY PLANS  
NOT FOR CONSTRUCTION

| NO. | REVISION | DATE |
|-----|----------|------|
|     |          |      |
|     |          |      |
|     |          |      |
|     |          |      |

PREPARED FOR:  
MPO  
2101 ONEIL AVE.  
RM 205  
CHEYENNE, WY. 82001







PROJECT: FOX FARM ROAD STREET IMPROVEMENTS  
DRAWING TITLE: FOX FARM RD. CROSS SECTIONS STA. 67+00-72+00

avi p.c.  
engineering  
planning  
surveying  
PHONE (307) 637-6017  
1103 OLD TOWN LANE, SUITE 101  
CHEYENNE, WY 82009  
AVI@AVIPC.COM

DATE: 6-20-13  
DRAWN BY: SRL  
DESIGNED BY: TC  
CHECKED BY: TC

JOB NO.: 2-3211-B

XS-12 83  
SHEET NO. OF

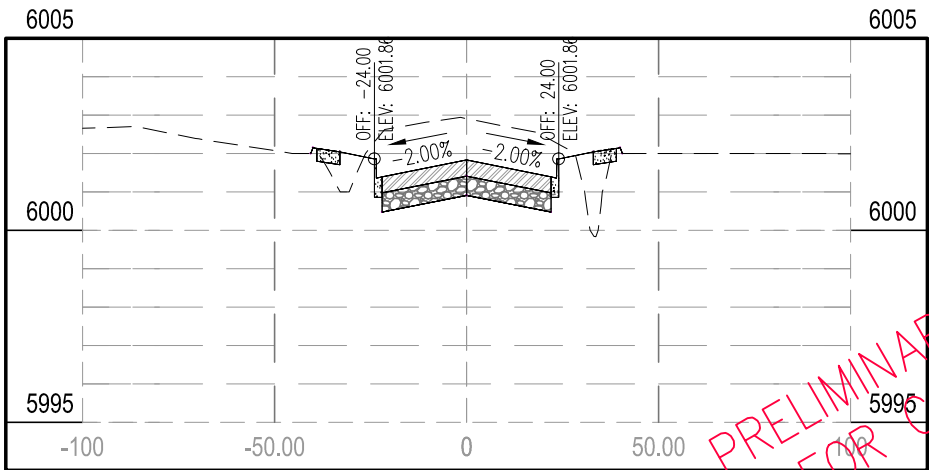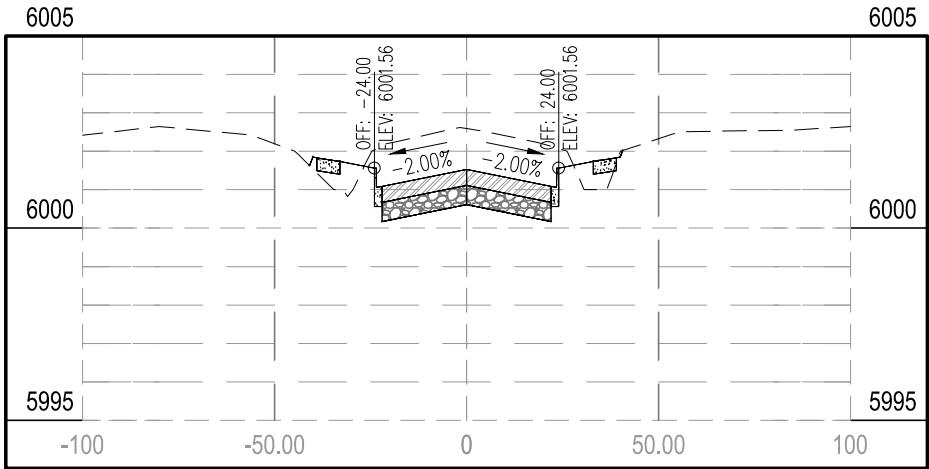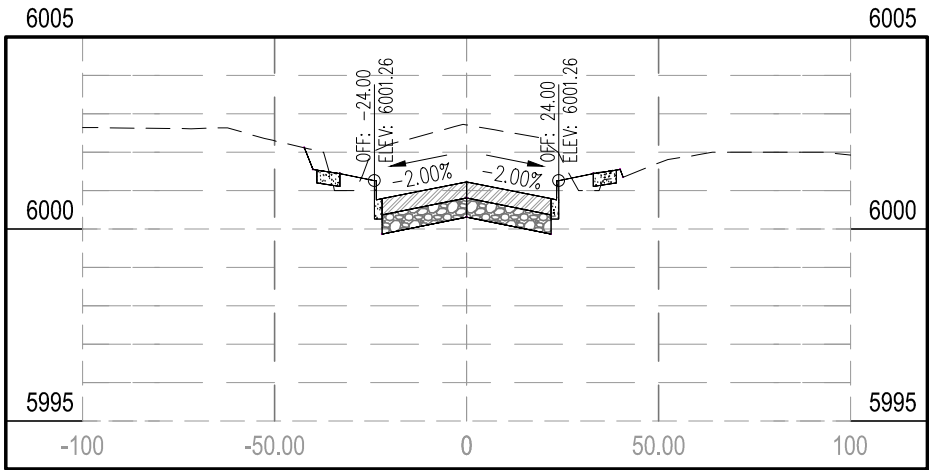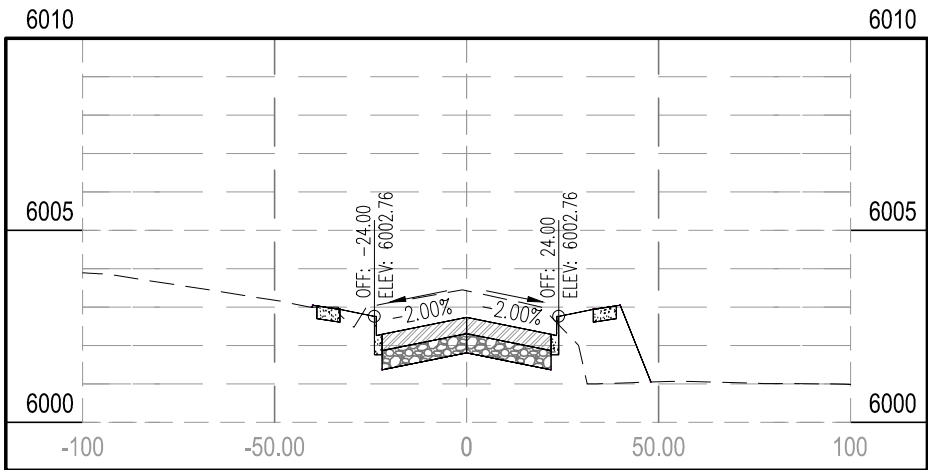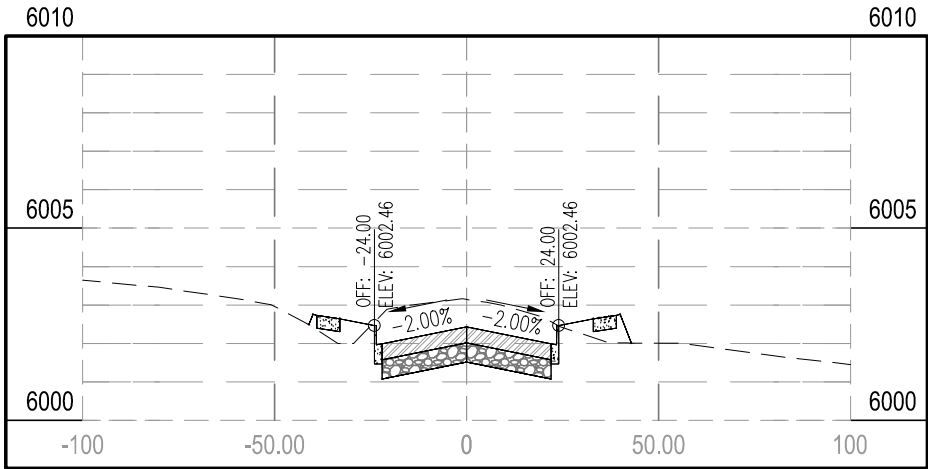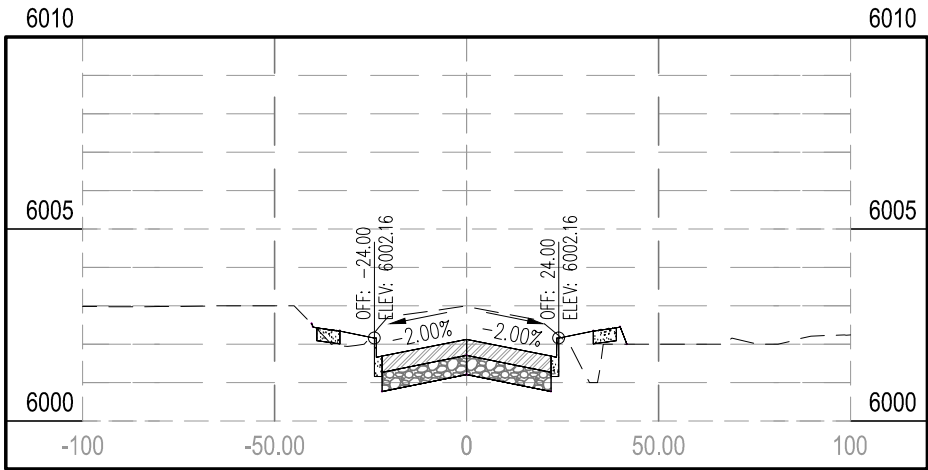

PRELIMINARY PLANS  
NOT FOR CONSTRUCTION

| NO. | REVISION | DATE |
|-----|----------|------|
|     |          |      |
|     |          |      |
|     |          |      |
|     |          |      |

PREPARED FOR:  
MPO  
2101 ONEIL AVE.  
RM 205  
CHEYENNE, WY. 82001







PROJECT: FOX FARM ROAD STREET IMPROVEMENTS  
DRAWING TITLE: FOX FARM RD. CROSS SECTIONS STA. 73+00 - 78+00

avi p.c.  
engineering  
planning  
surveying  
PHONE (307) 637-6017  
1103 OLD TOWN LANE, SUITE 101  
CHEYENNE, WY 82009  
AVI@AVIPC.COM

DATE: 6-20-13  
DRAWN BY: SRL  
DESIGNED BY: TC  
CHECKED BY: TC

JOB NO.: 2-3211-B

XS-13 83  
SHEET NO. OF

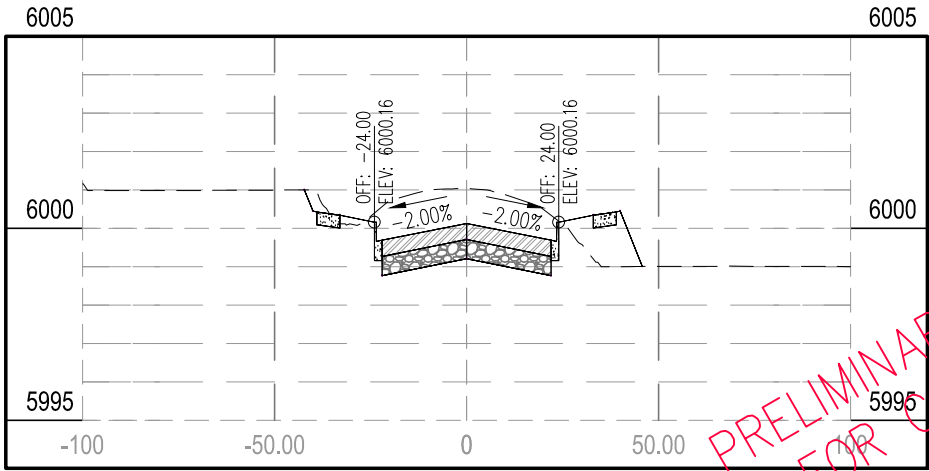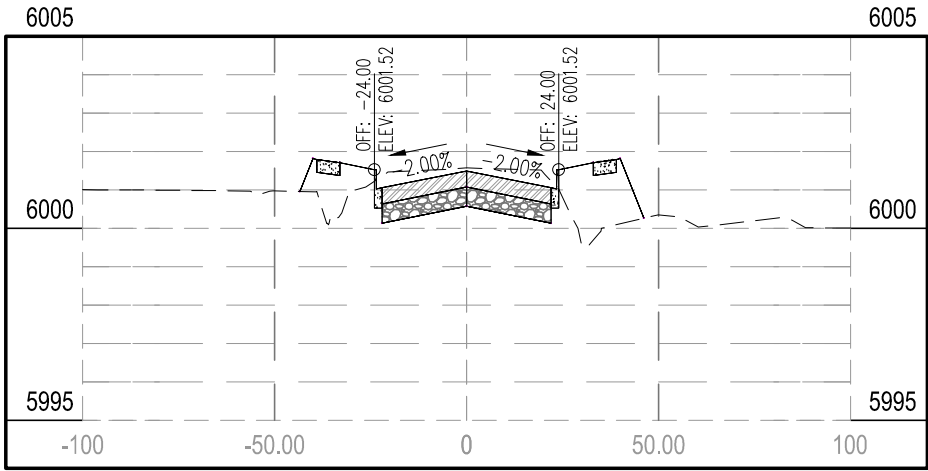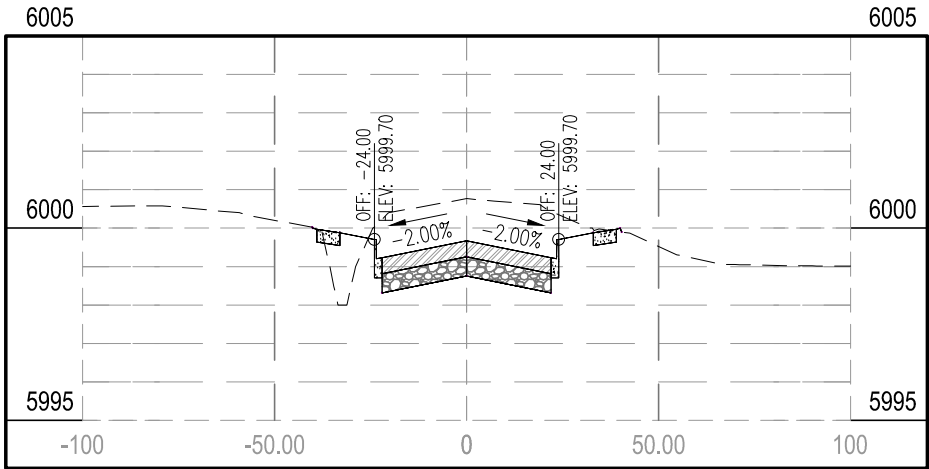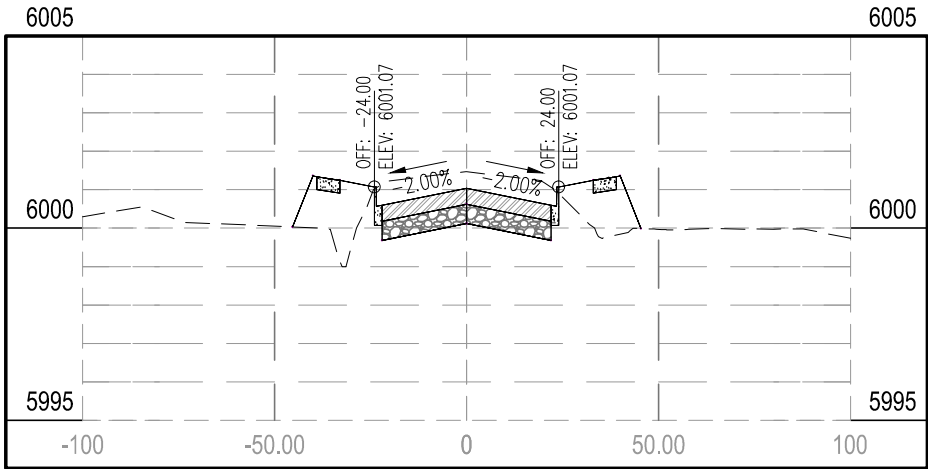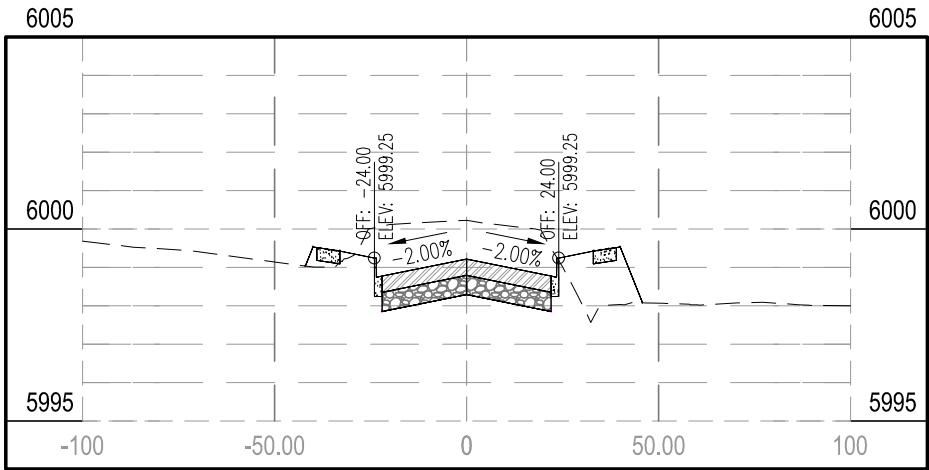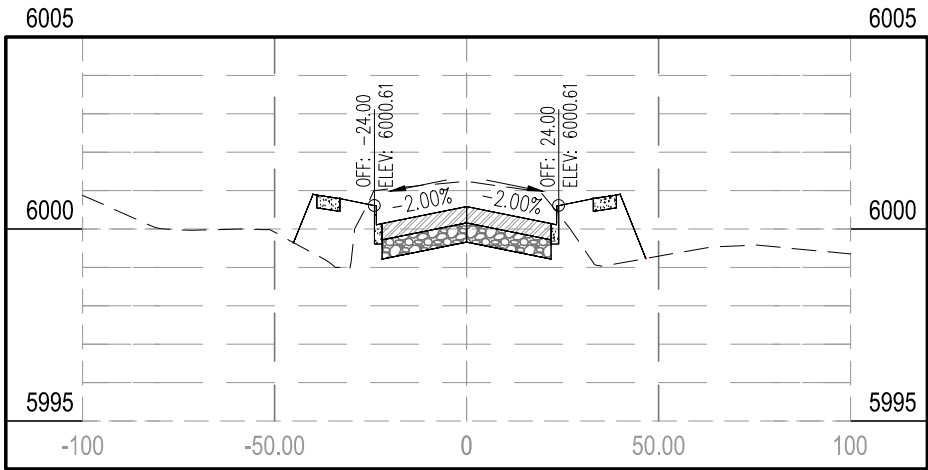

PRELIMINARY PLANS  
NOT FOR CONSTRUCTION

| NO. | REVISION | DATE |
|-----|----------|------|
|     |          |      |
|     |          |      |
|     |          |      |
|     |          |      |

PREPARED FOR:  
MPO  
2101 ONEIL AVE.  
RM 205  
CHEYENNE, WY. 82001







PROJECT: FOX FARM ROAD STREET IMPROVEMENTS  
DRAWING TITLE: FOX FARM RD. CROSS SECTIONS STA. 79+00 - 84+00

avi p.c.  
engineering  
planning  
surveying  
PHONE (307) 637-6017  
1103 OLD TOWN LANE, SUITE 101  
CHEYENNE, WY 82009  
AVI@AVIIPC.COM

DATE: 6-20-13  
DRAWN BY: SRL  
DESIGNED BY: TC  
CHECKED BY: TC

JOB NO.: 2-3211-B

XS-14 83  
SHEET NO. OF

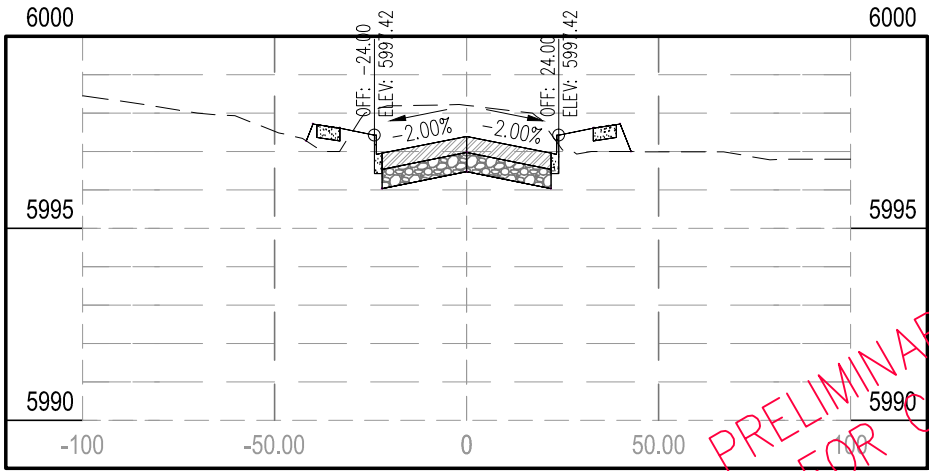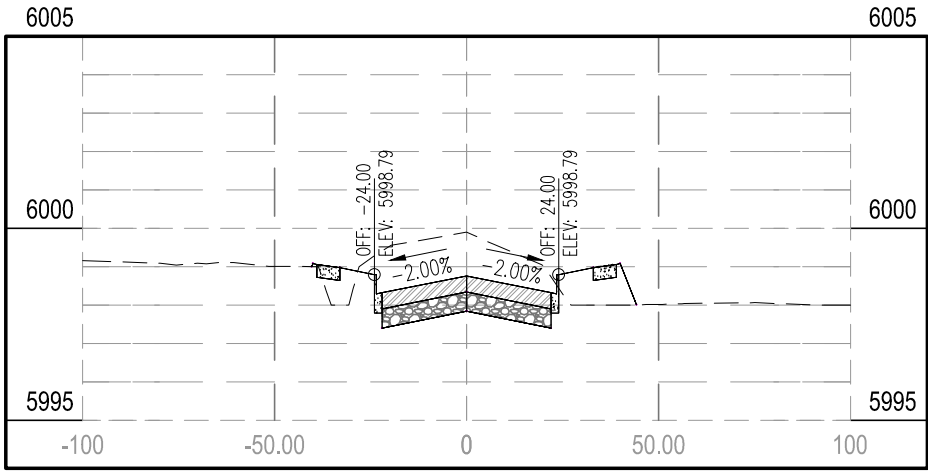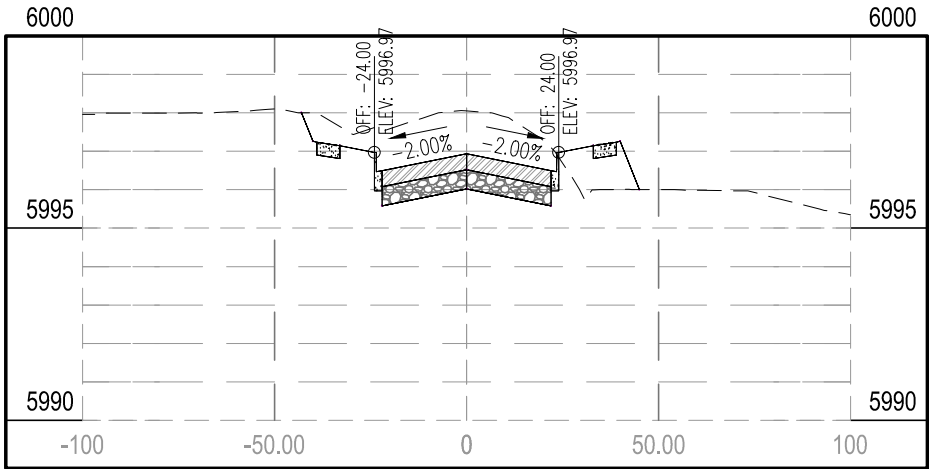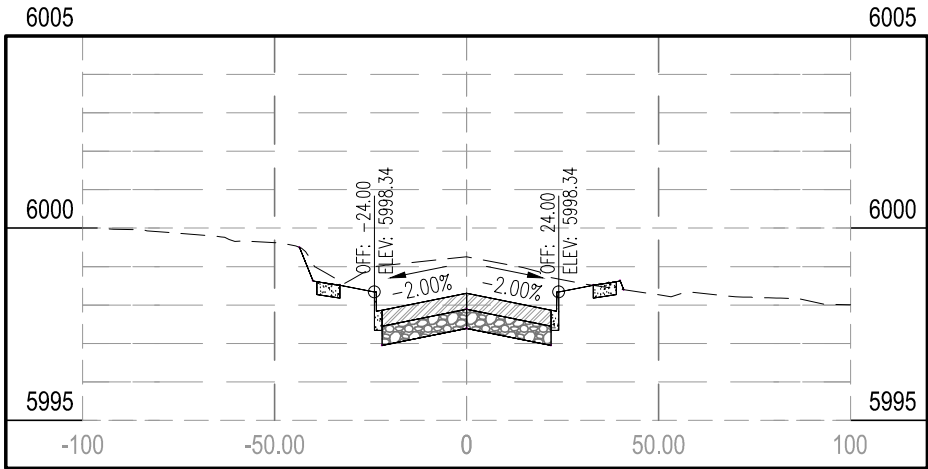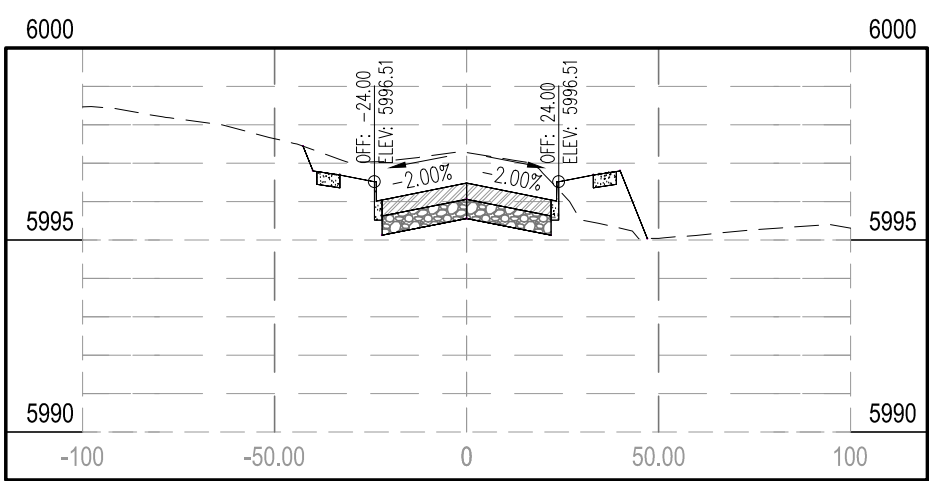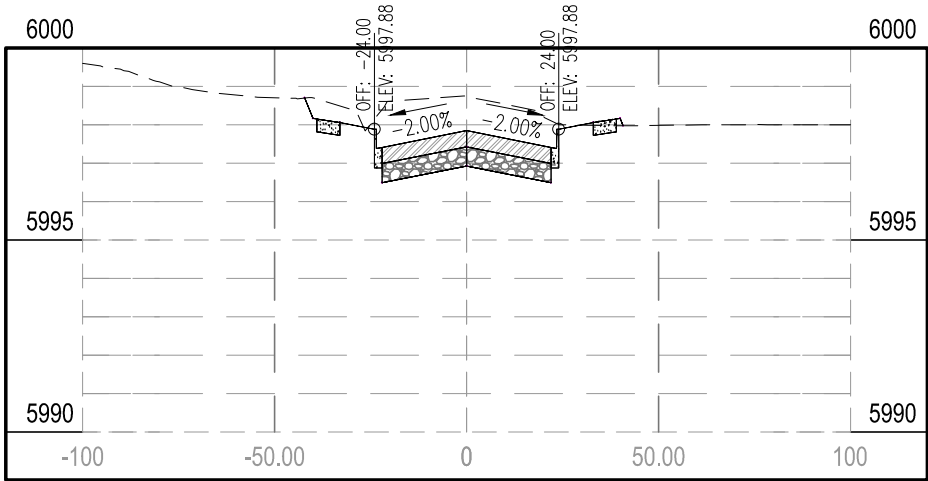

PRELIMINARY PLANS  
NOT FOR CONSTRUCTION

| NO. | REVISION | DATE |
|-----|----------|------|
|     |          |      |
|     |          |      |
|     |          |      |
|     |          |      |

PREPARED FOR:  
MPO  
2101 ONEIL AVE.  
RM 205  
CHEYENNE, WY. 82001


PROJECT: FOX FARM ROAD STREET IMPROVEMENTS  
DRAWING TITLE: FOX FARM RD. CROSS SECTIONS STA. 85+00 - 90+00

avi p.c.  
engineering  
planning  
surveying  
PHONE (307) 637-6017  
1103 OLD TOWN LANE, SUITE 101  
CHEYENNE, WY 82009  
AVI@AVIPC.COM


DATE: 6-20-13  
DRAWN BY: SRL  
DESIGNED BY: TC  
CHECKED BY: TC

JOB NO.: 2-3211-B


XS-15 83  
SHEET NO. OF

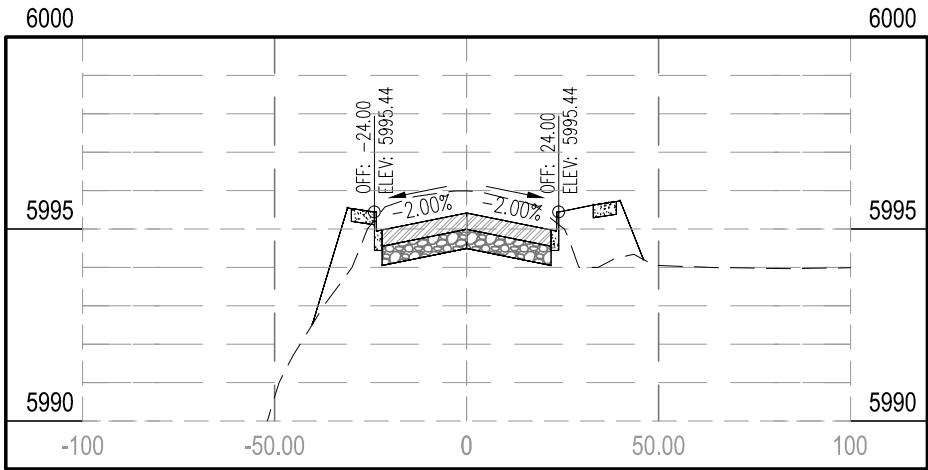


STA 93+00.00

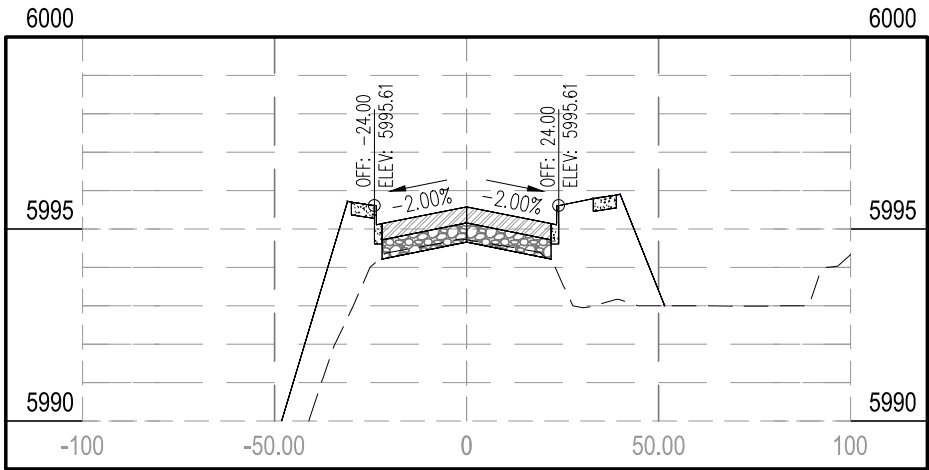


STA 96+00.00

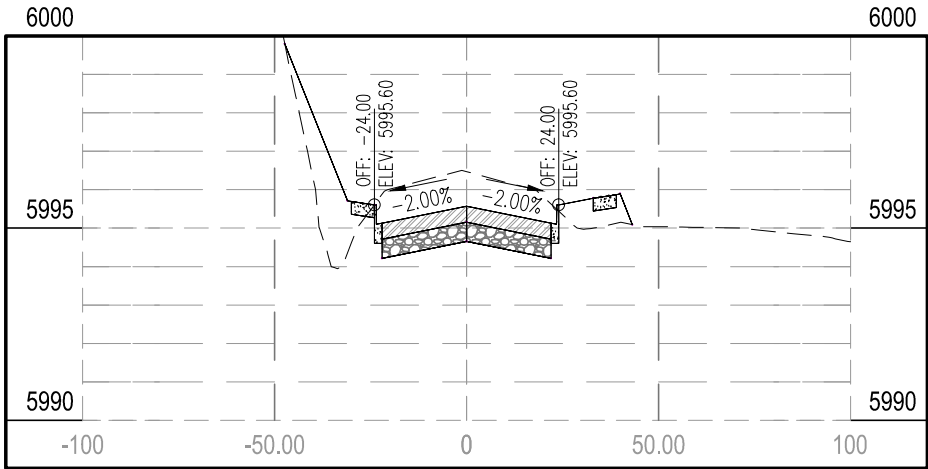


STA 92+00.00

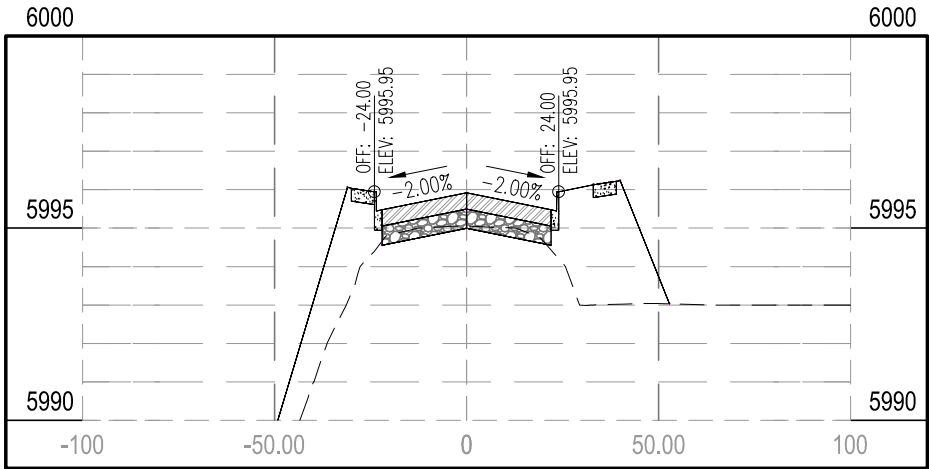

STA 95+00.00

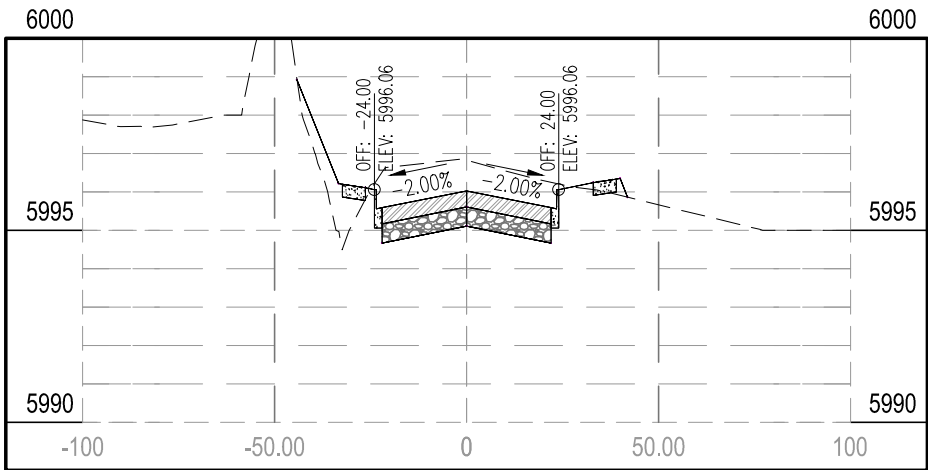

STA 91+00.00

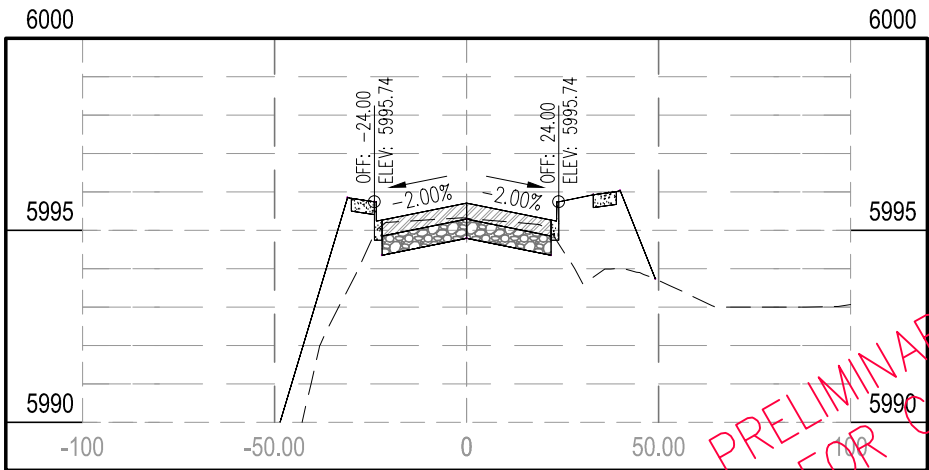

STA 94+00.00

PRELIMINARY PLANS  
NOT FOR CONSTRUCTION

| NO. | REVISION | DATE |
|-----|----------|------|
|     |          |      |
|     |          |      |
|     |          |      |
|     |          |      |

PREPARED FOR:  
MPO  
2101 ONEIL AVE.  
RM 205  
CHEYENNE, WY. 82001

PROJECT: FOX FARM ROAD STREET IMPROVEMENTS  
DRAWING TITLE: FOX FARM RD. CROSS SECTIONS STA. 91+00 - 96+00


avi p.c.  
engineering  
planning  
surveying  
PHONE (307) 637-6017  
1103 OLD TOWN LANE, SUITE 101  
CHEYENNE, WY 82009  
AVI@AVIPC.COM

DATE: 6-20-13  
DRAWN BY: SRL  
DESIGNED BY: TC  
CHECKED BY: TC


JOB NO.: 2-3211-B

XS-16 83  
SHEET NO. OF


H:\3211\design\3211B FOX FARM STREET IMP.dwg Aug 30, 2013 4:24pm jwilson

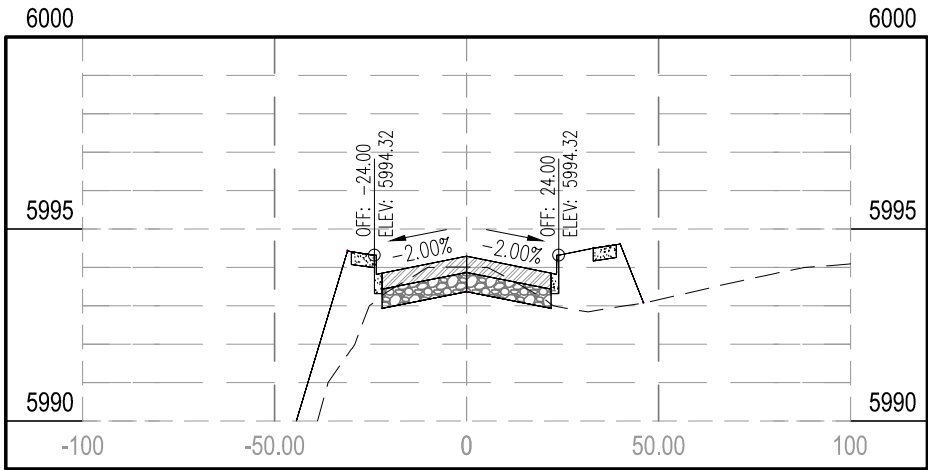


STA 99+00.00

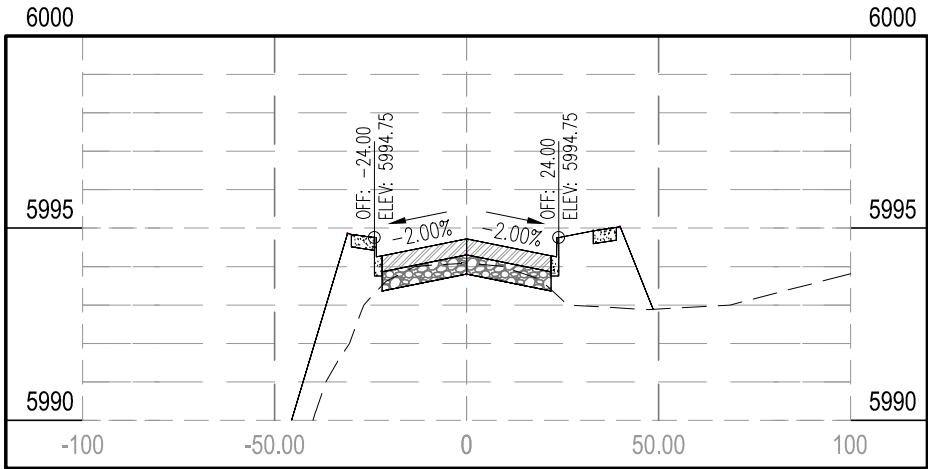

STA 98+00.00

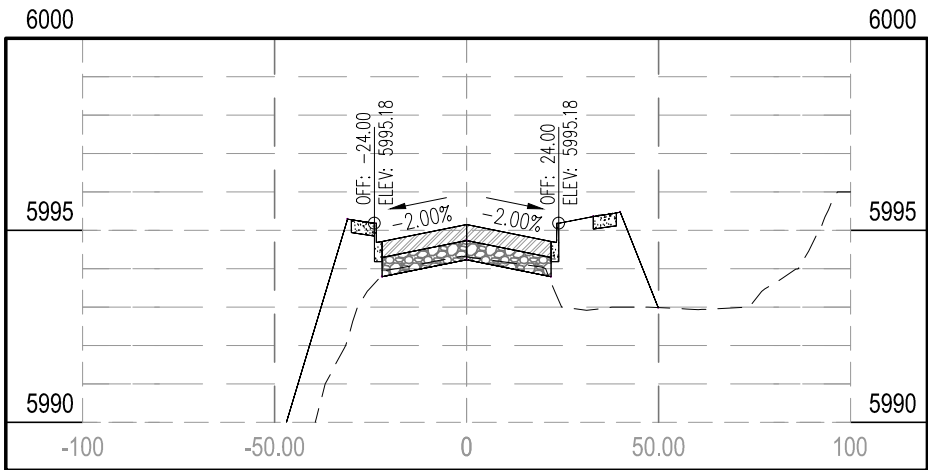


STA 97+00.00

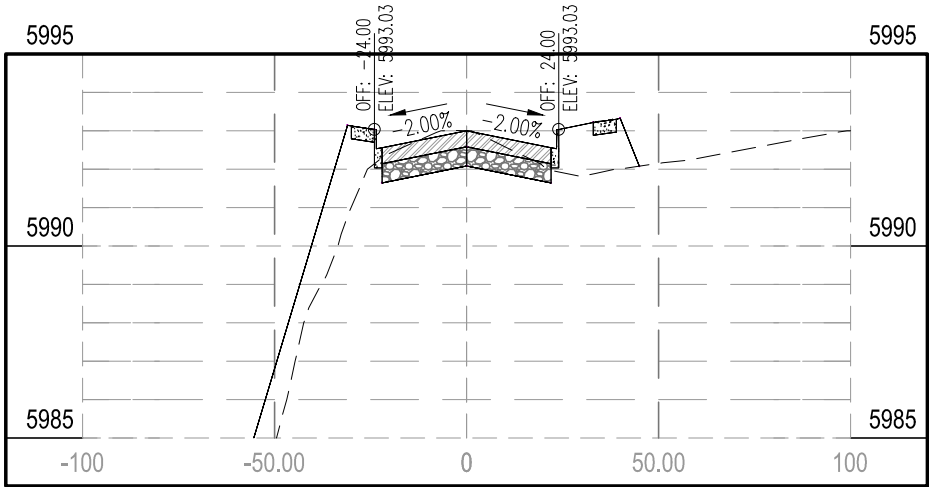

STA 102+00.00



STA 101+00.00

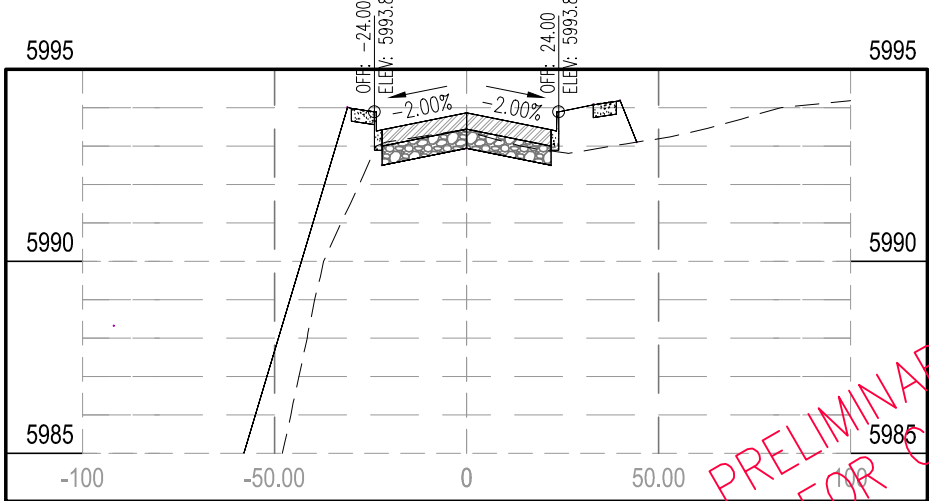

STA 100+00.00

PRELIMINARY PLANS  
NOT FOR CONSTRUCTION

| NO. | REVISION | DATE |
|-----|----------|------|
|     |          |      |
|     |          |      |
|     |          |      |
|     |          |      |

PREPARED FOR:  
MPO  
2101 ONEIL AVE.  
RM 205  
CHEYENNE, WY. 82001

PROJECT: FOX FARM ROAD STREET IMPROVEMENTS  
DRAWING TITLE: FOX FARM RD. CROSS SECTIONS STA. 97+00 - 102+00







avi p.c.  
engineering  
planning  
surveying  
PHONE (307) 637-6017  
1103 OLD TOWN LANE, SUITE 101  
CHEYENNE, WY 82009  
AVI@AVIFPC.COM

DATE: 6-20-13  
DRAWN BY: SRL  
DESIGNED BY: TC  
CHECKED BY: TC

JOB NO.: 2-3211-B

XS-17 83  
SHEET NO. OF

H:\3211\design\3211B FOX FARM STREET IMP.dwg Aug 30, 2013 4:25pm jwilson

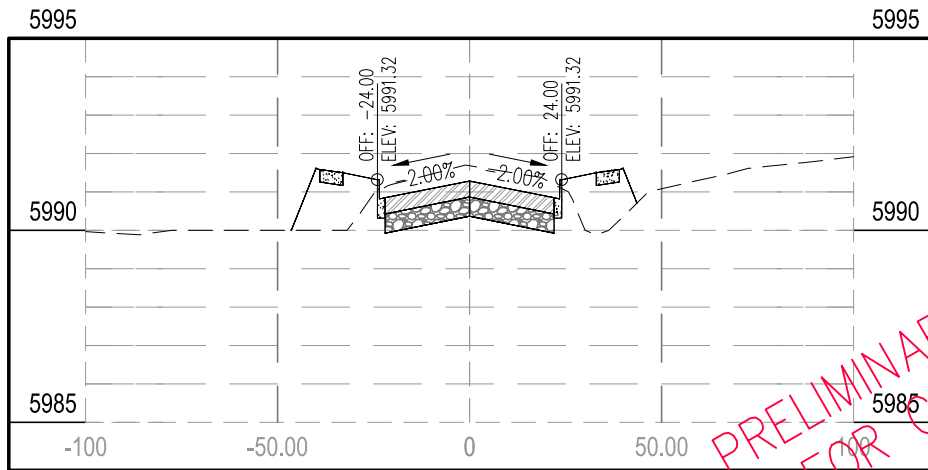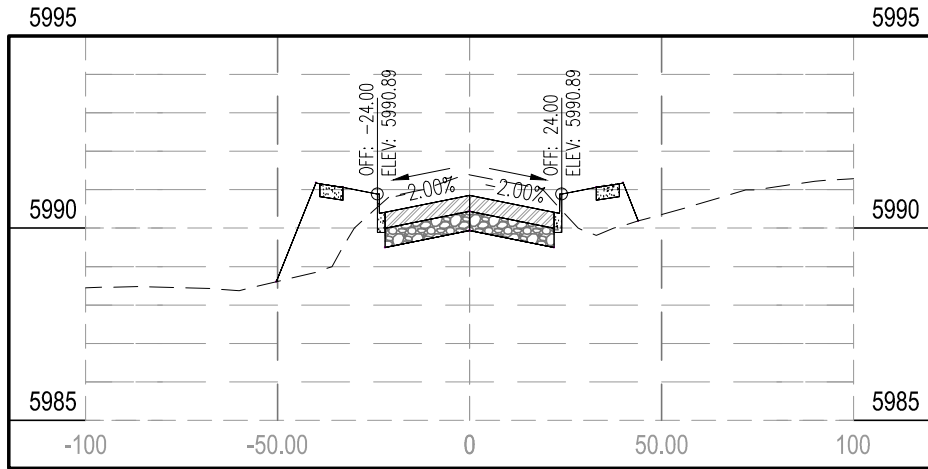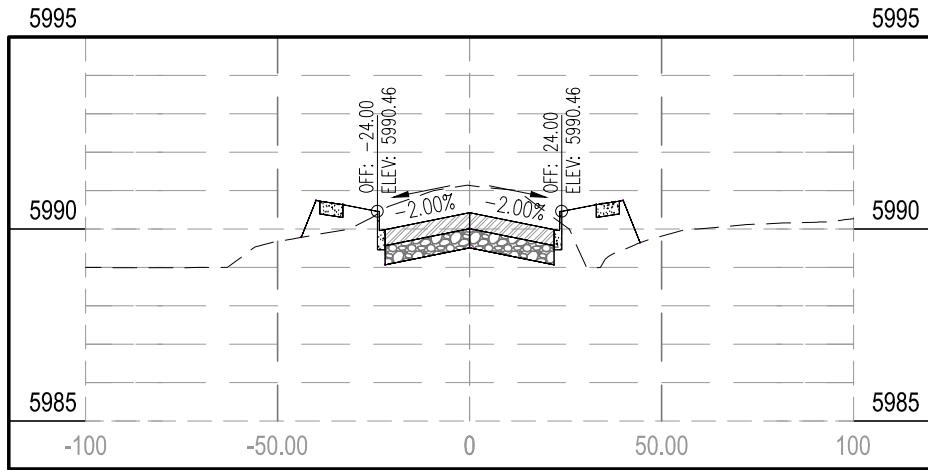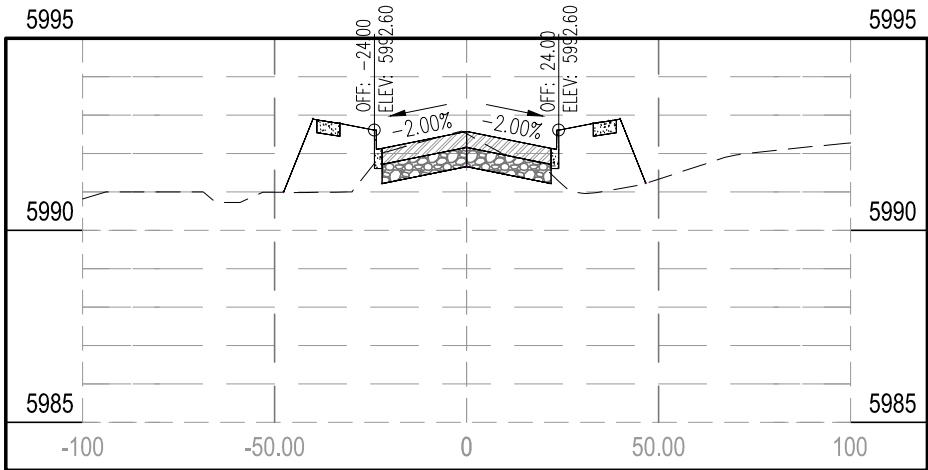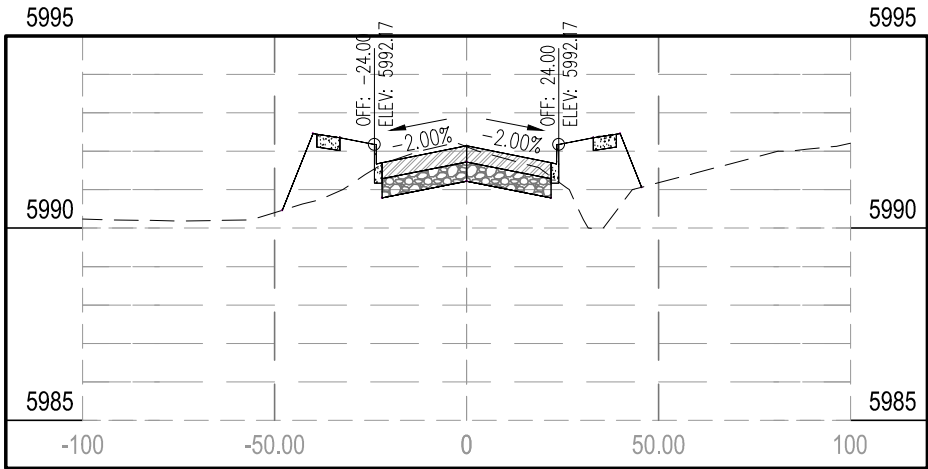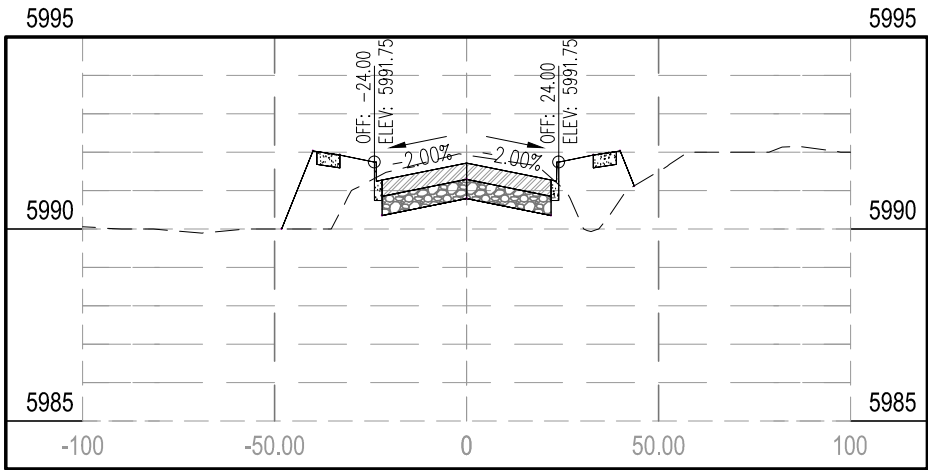

PRELIMINARY PLANS  
NOT FOR CONSTRUCTION

| NO. | REVISION | DATE |
|-----|----------|------|
|     |          |      |
|     |          |      |
|     |          |      |
|     |          |      |

PREPARED FOR:  
MPO  
2101 ONEIL AVE.  
RM 205  
CHEYENNE, WY. 82001


PROJECT: FOX FARM ROAD STREET IMPROVEMENTS  
DRAWING TITLE: FOX FARM RD. CROSS SECTIONS STA. 103+00 - 108+00

avi p.c.  
engineering  
planning  
surveying  
PHONE (307) 637-6017  
1103 OLD TOWN LANE, SUITE 101  
CHEYENNE, WY 82009  
AVI@AVIPC.COM


DATE: 6-20-13  
DRAWN BY: SRL  
DESIGNED BY: TC  
CHECKED BY: TC

JOB NO.: 2-3211-B


XS-18 83  
SHEET NO. OF

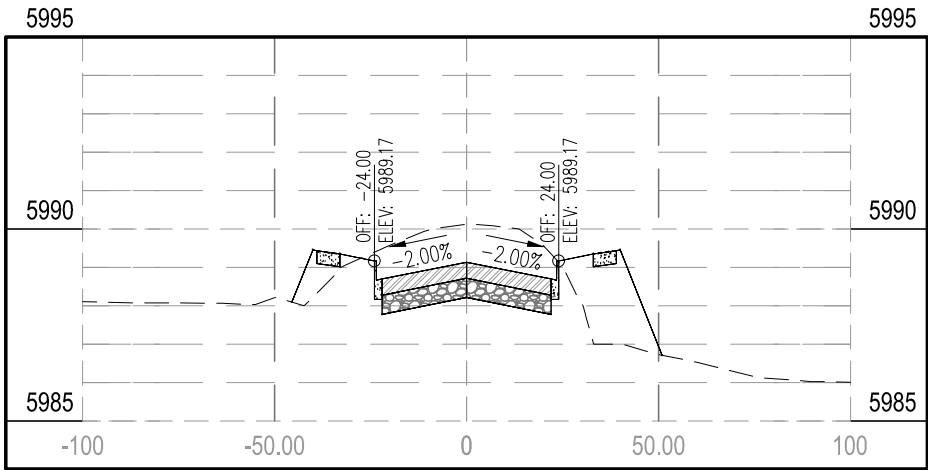


STA 111+00.00

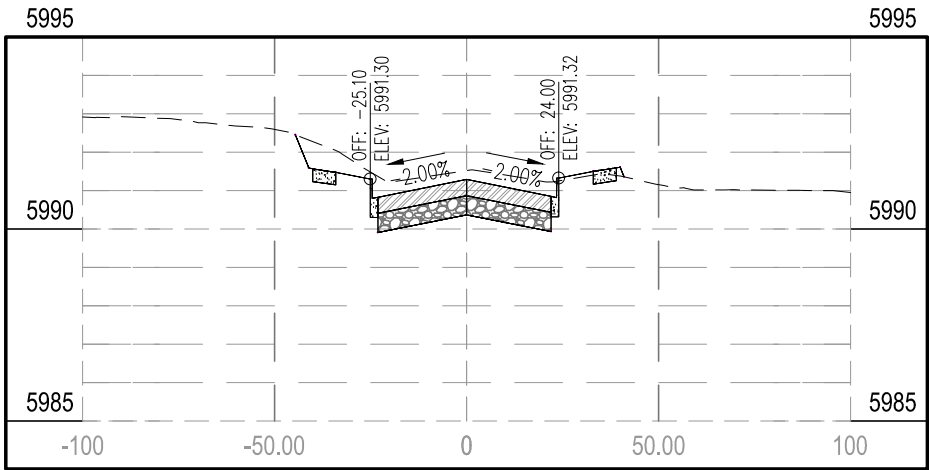


STA 114+00.00

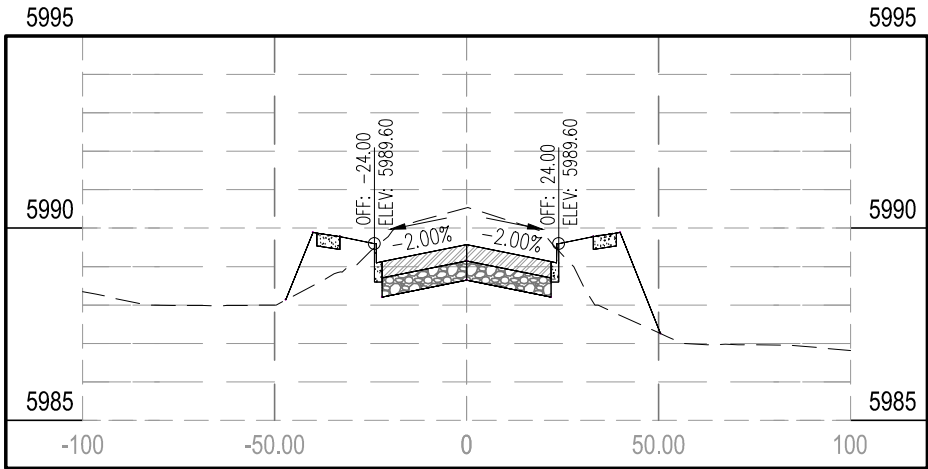


STA 110+00.00

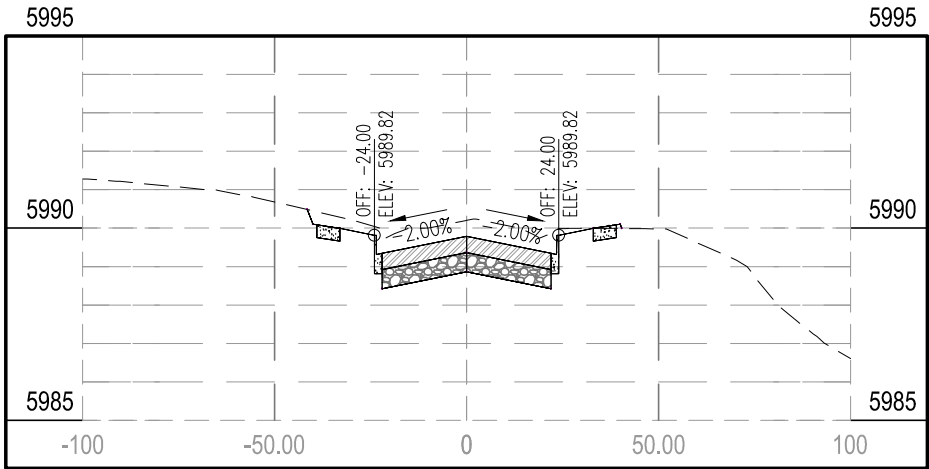

STA 113+00.00

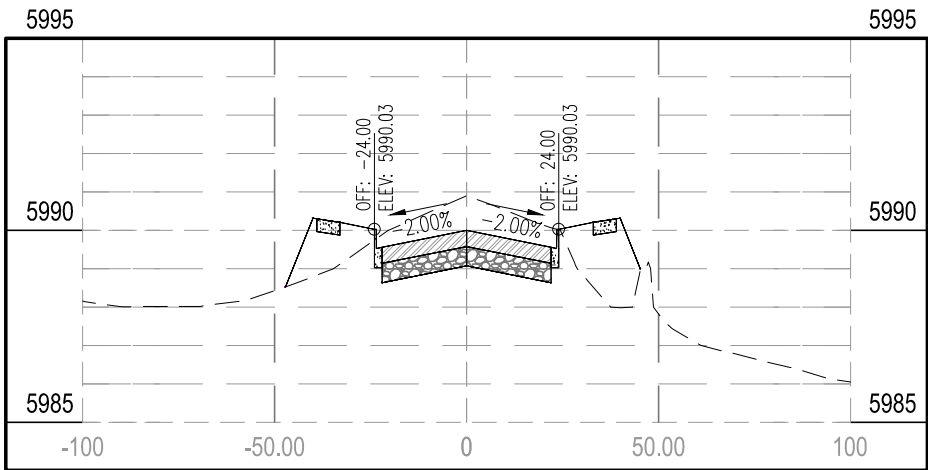

STA 109+00.00

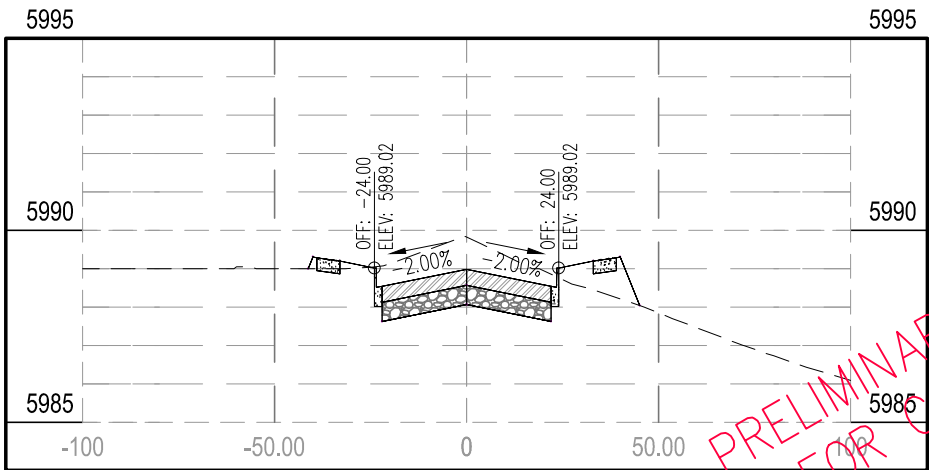

STA 112+00.00

PRELIMINARY PLANS  
NOT FOR CONSTRUCTION

| NO. | REVISION | DATE |
|-----|----------|------|
|     |          |      |
|     |          |      |
|     |          |      |
|     |          |      |

PREPARED FOR:  
MPO  
2101 ONEIL AVE.  
RM 205  
CHEYENNE, WY. 82001


PROJECT: FOX FARM ROAD STREET IMPROVEMENTS  
DRAWING TITLE: FOX FARM RD. CROSS SECTIONS  
STA. 109+00 - 114+00

avi p.c.  
engineering  
planning  
surveying  
PHONE (307) 637-6017  
1103 OLD TOWN LANE, SUITE 101  
CHEYENNE, WY 82009  
AVI@AVIFPC.COM


DATE: 6-20-13  
DRAWN BY: SRL  
DESIGNED BY: TC  
CHECKED BY: TC

JOB NO.: 2-3211-B


XS-19 83  
SHEET NO. OF

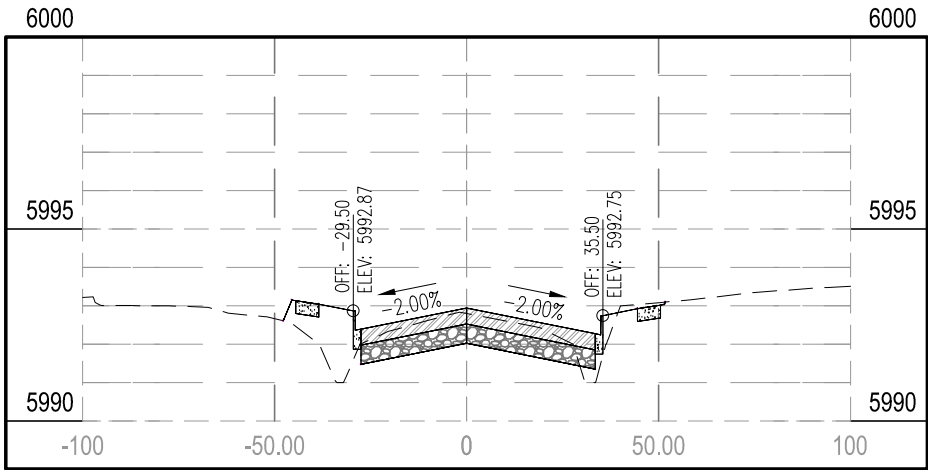


STA 117+00.00

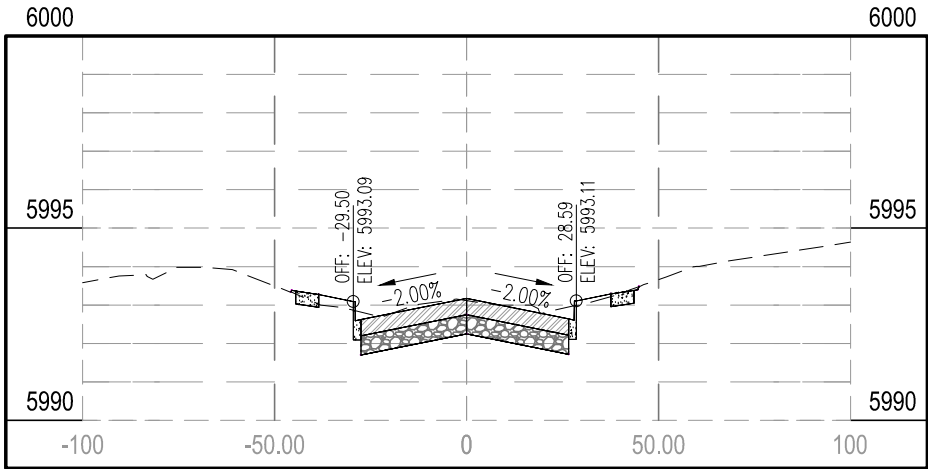


STA 116+00.00

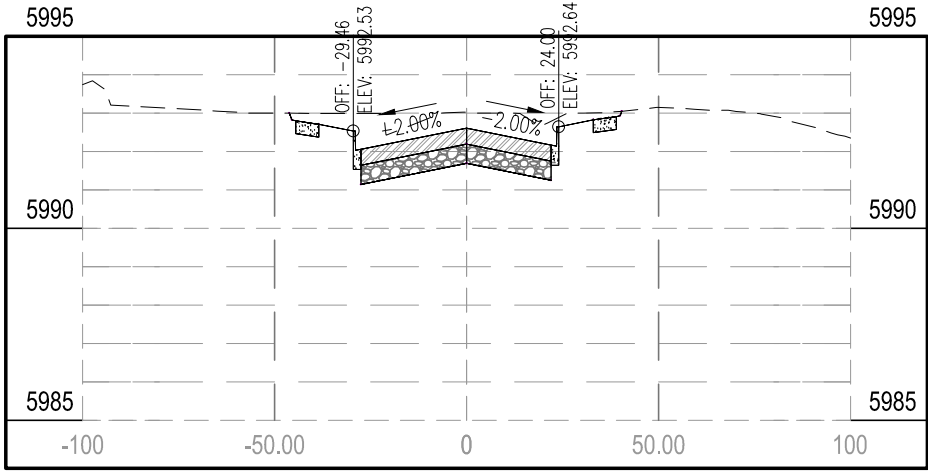


STA 115+00.00

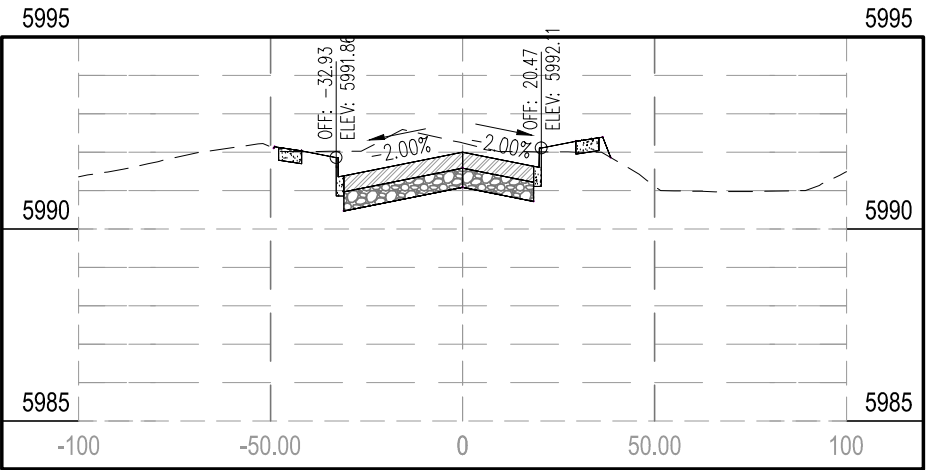

STA 120+00.00

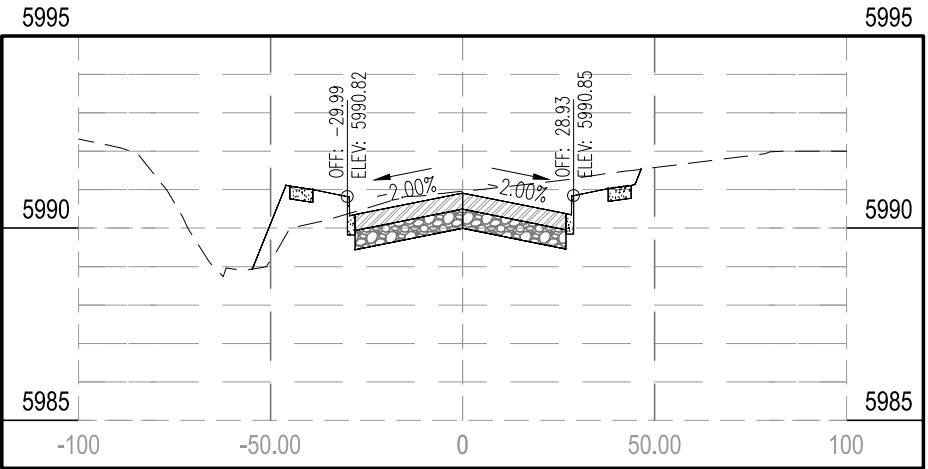

STA 119+00.00

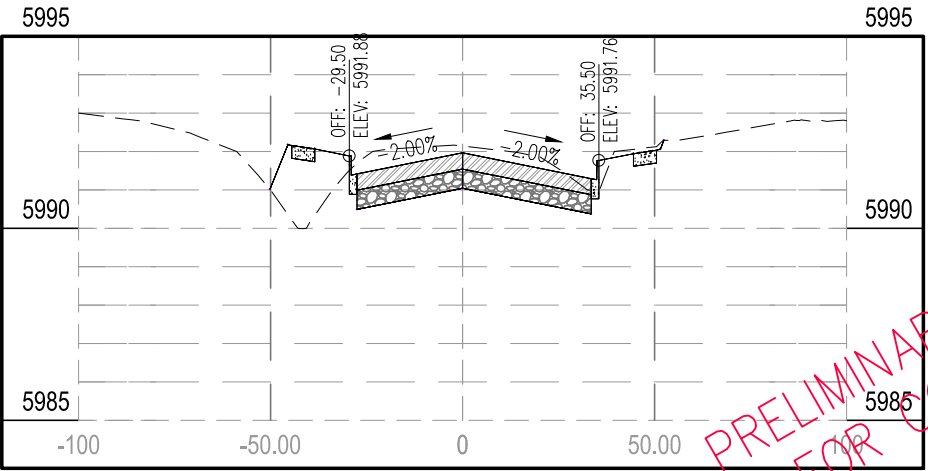

STA 118+00.00

PRELIMINARY PLANS  
NOT FOR CONSTRUCTION

| NO. | REVISION | DATE |
|-----|----------|------|
|     |          |      |
|     |          |      |
|     |          |      |
|     |          |      |

PREPARED FOR:  
MPO  
2101 O'NEIL AVE.  
RM 205  
CHEYENNE, WY. 82001


PROJECT: FOX FARM ROAD STREET IMPROVEMENTS  
DRAWING TITLE: FOX FARM RD. CROSS SECTIONS STA. 115+00 - 120+00

avi p.c.  
engineering  
planning  
surveying  
PHONE (307) 637-6017  
1103 OLD TOWN LANE, SUITE 101  
CHEYENNE, WY 82009  
AVI@AVIPC.COM


DATE: 6-20-13  
DRAWN BY: SRL  
DESIGNED BY: TC  
CHECKED BY: TC

JOB NO.: 2-3211-B


XS-20 83  
SHEET NO. OF

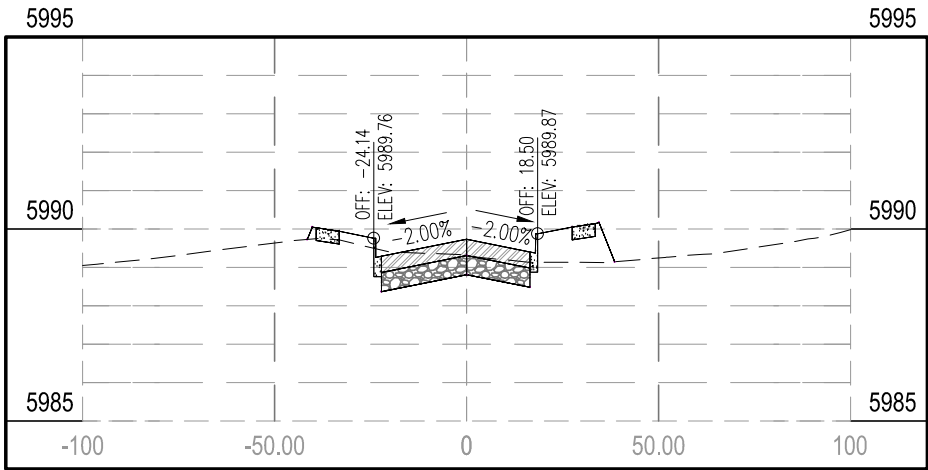


STA 123+00.00

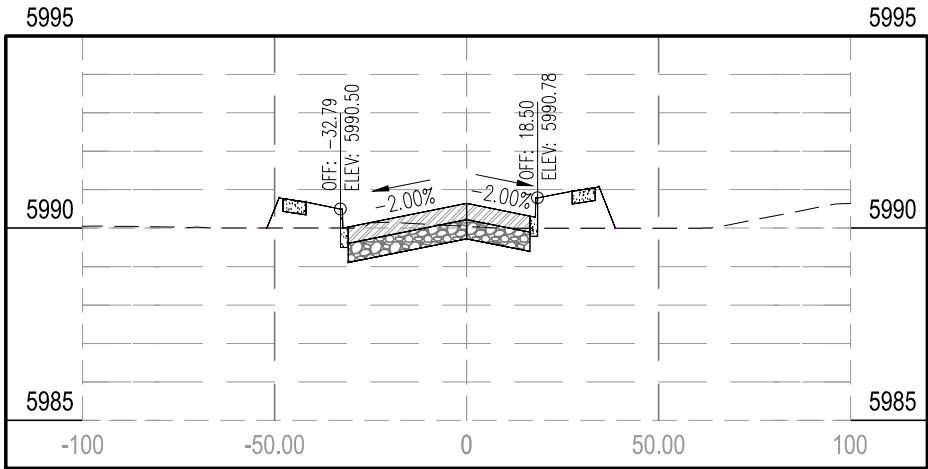


STA 122+00.00

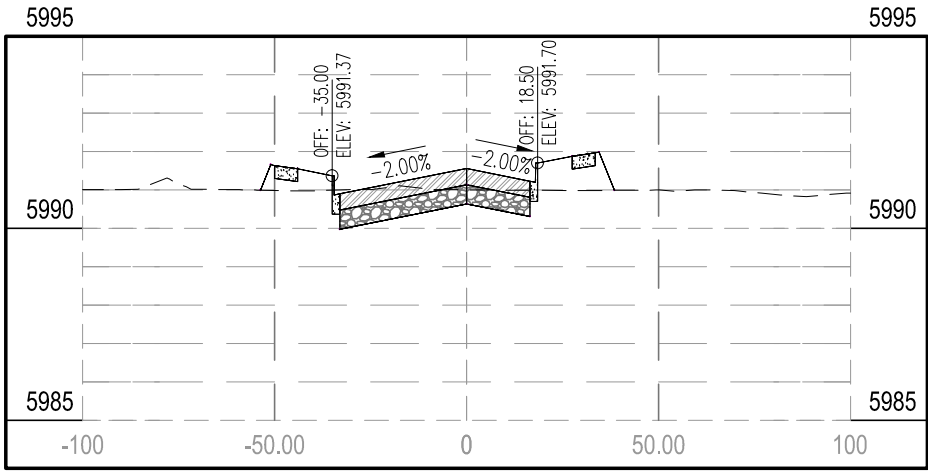

STA 121+00.00

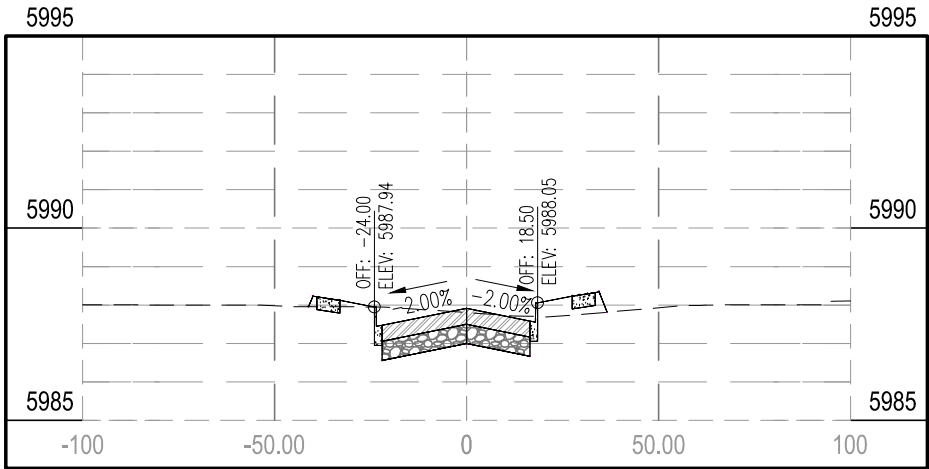

STA 125+00.00

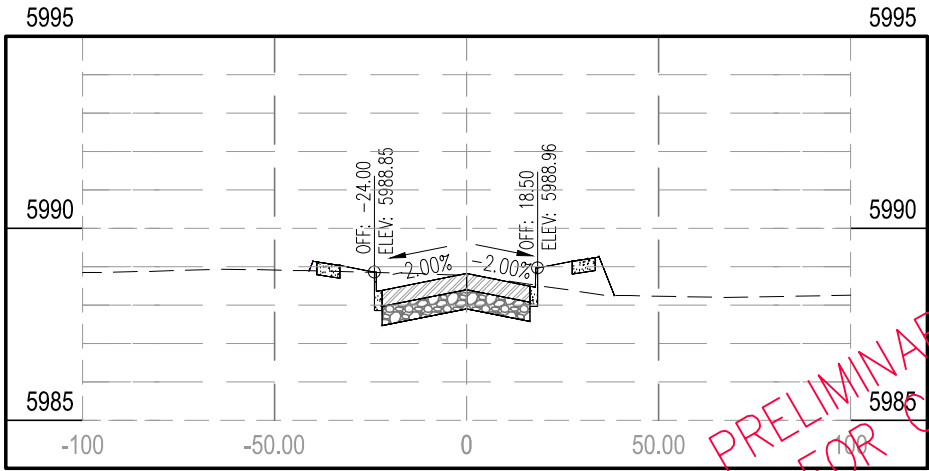

STA 124+00.00

PRELIMINARY PLANS  
NOT FOR CONSTRUCTION

| NO. | REVISION | DATE |
|-----|----------|------|
|     |          |      |
|     |          |      |
|     |          |      |
|     |          |      |

PREPARED FOR:  
MPO  
2101 ONEIL AVE.  
RM 205  
CHEYENNE, WY. 82001


PROJECT: FOX FARM ROAD STREET IMPROVEMENTS  
DRAWING TITLE: FOX FARM RD. CROSS SECTIONS STA. 121+00 - 125+00

avi p.c.  
engineering  
planning  
surveying  
PHONE (307) 637-6017  
1103 OLD TOWN LANE, SUITE 101  
CHEYENNE, WY 82009  
AVI@AVIPC.COM


DATE: 6-20-13  
DRAWN BY: SRL  
DESIGNED BY: TC  
CHECKED BY: TC

JOB NO.: 2-3211-B


XS-21 83  
SHEET NO. OF

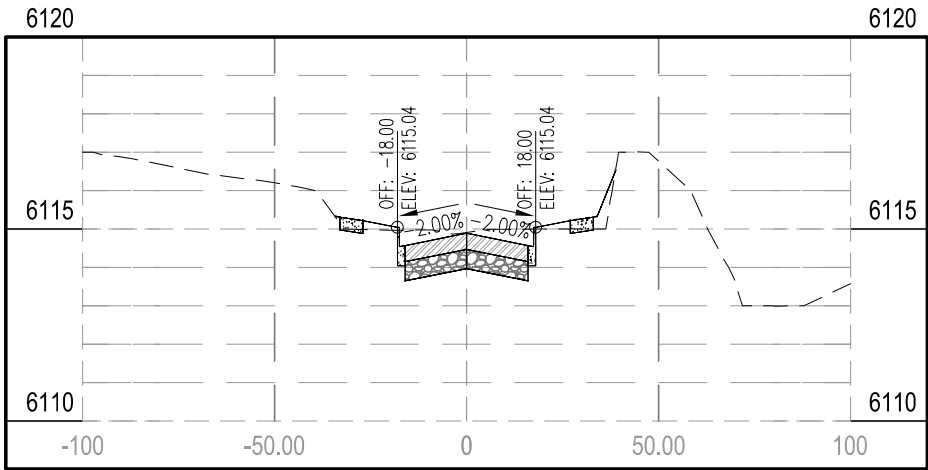


STA 2+00.00

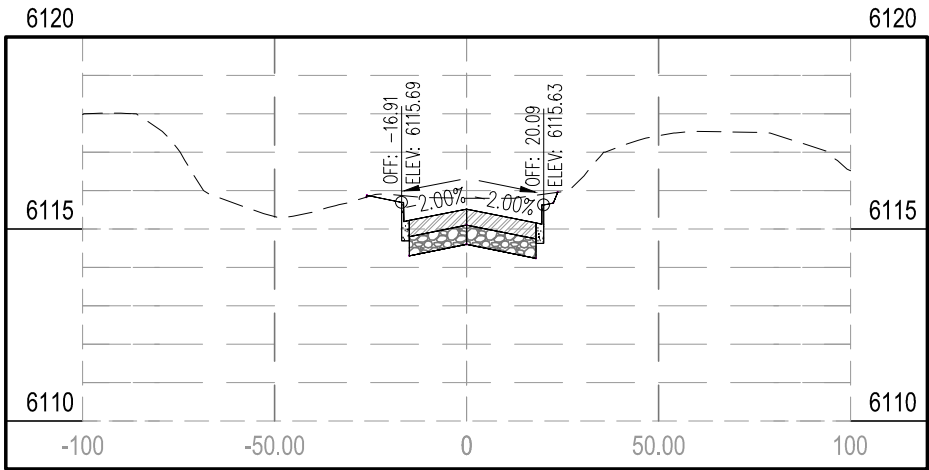


STA 3+50.00

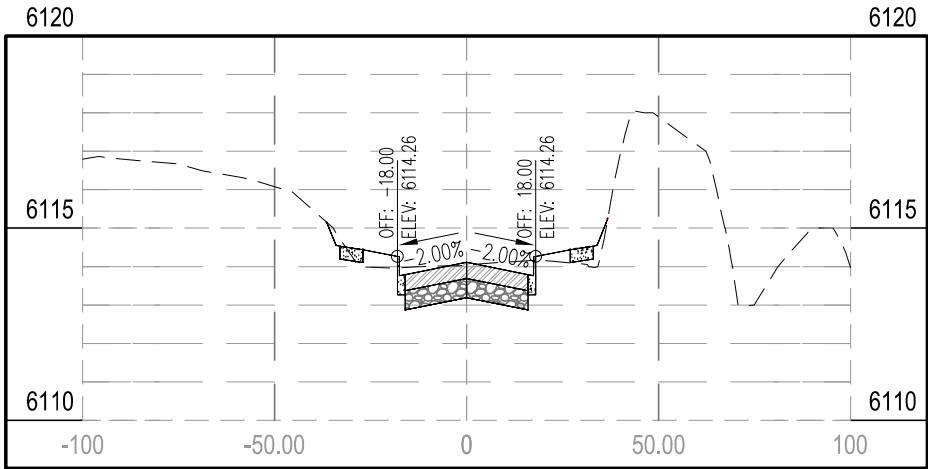


STA 1+50.00

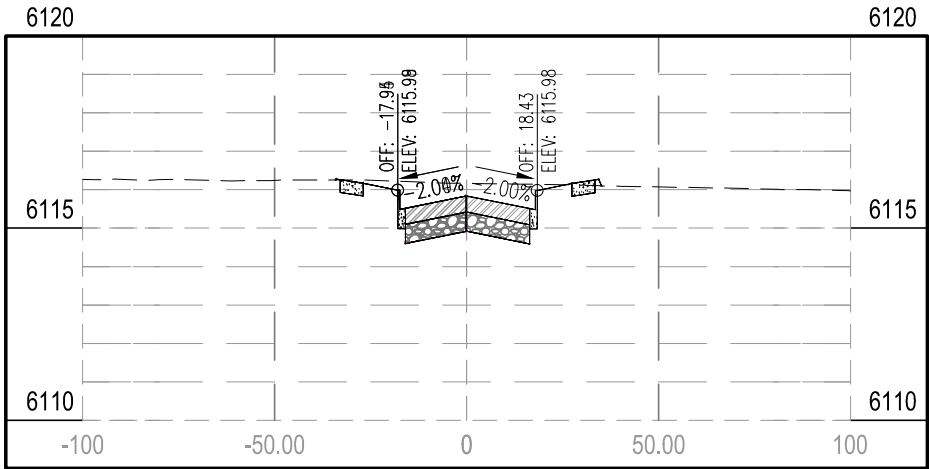

STA 3+00.00

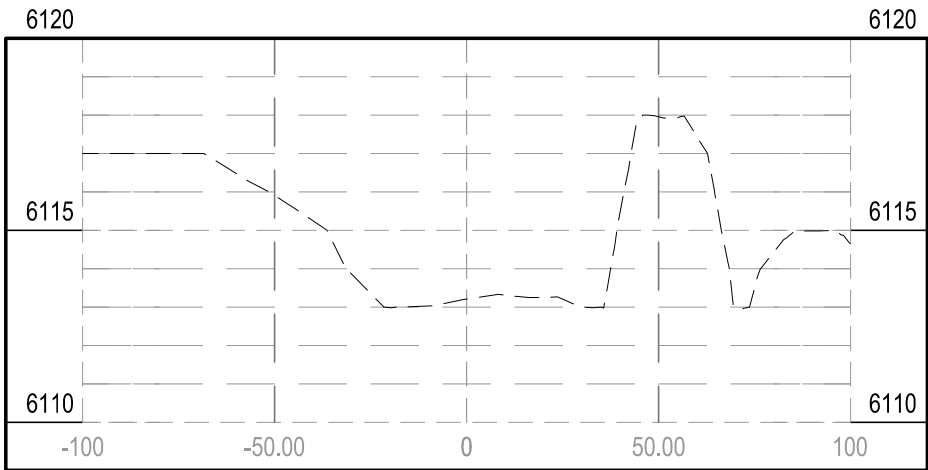

STA 1+00.00

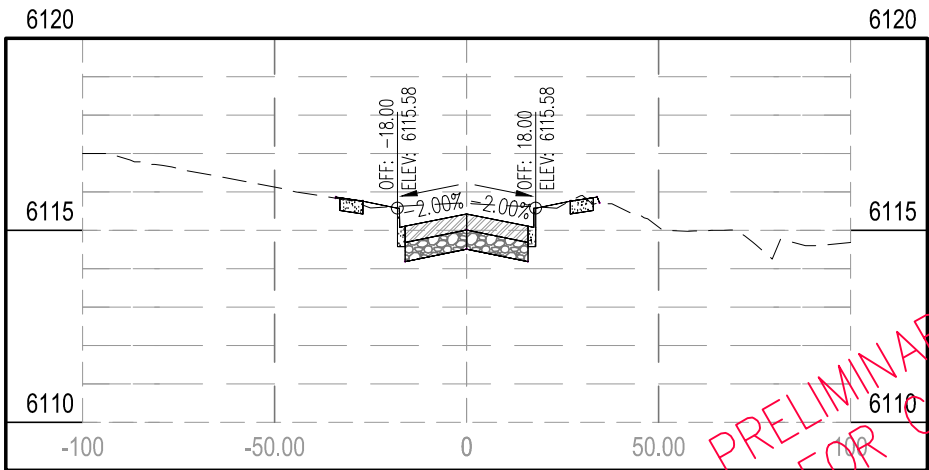

STA 2+50.00

PRELIMINARY PLANS  
NOT FOR CONSTRUCTION

| NO. | REVISION | DATE |
|-----|----------|------|
|     |          |      |
|     |          |      |
|     |          |      |
|     |          |      |

PREPARED FOR:  
MPO  
2101 ONEIL AVE.  
RM 205  
CHEYENNE, WY. 82001


PROJECT: FOX FARM ROAD STREET IMPROVEMENTS  
DRAWING TITLE: WALTERSCHIED BLVD. CROSS SECTIONS STA. 1+00 - 3+50

avi p.c.  
engineering  
planning  
surveying  
PHONE (307) 637-6017  
1103 OLD TOWN LANE, SUITE 101  
CHEYENNE, WY 82009  
AVI@AVIFPC.COM


DATE: 6-20-13  
DRAWN BY: SRL  
DESIGNED BY: TC  
CHECKED BY: TC

JOB NO.: 2-3211-B


XS-22 83  
SHEET NO. OF

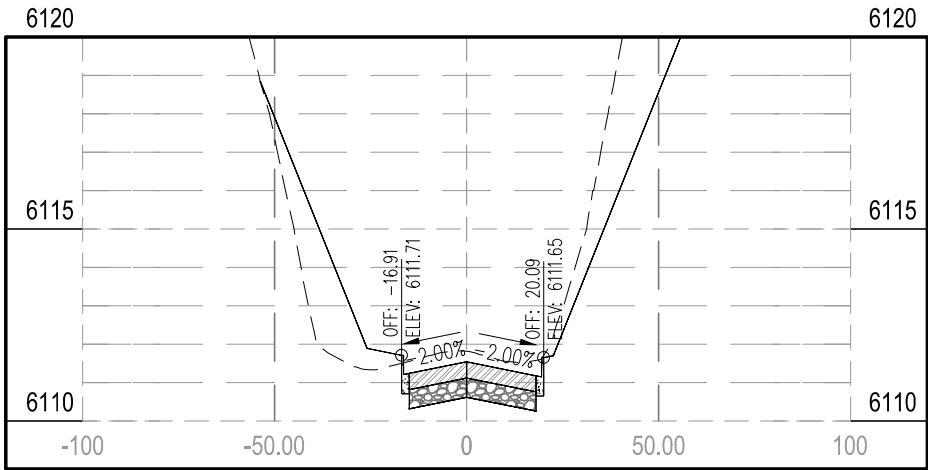


STA 5+00.00

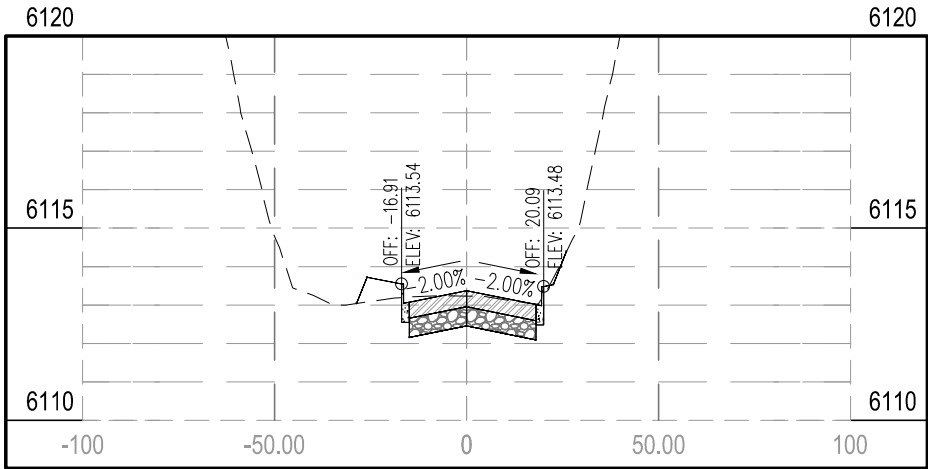

STA 4+50.00

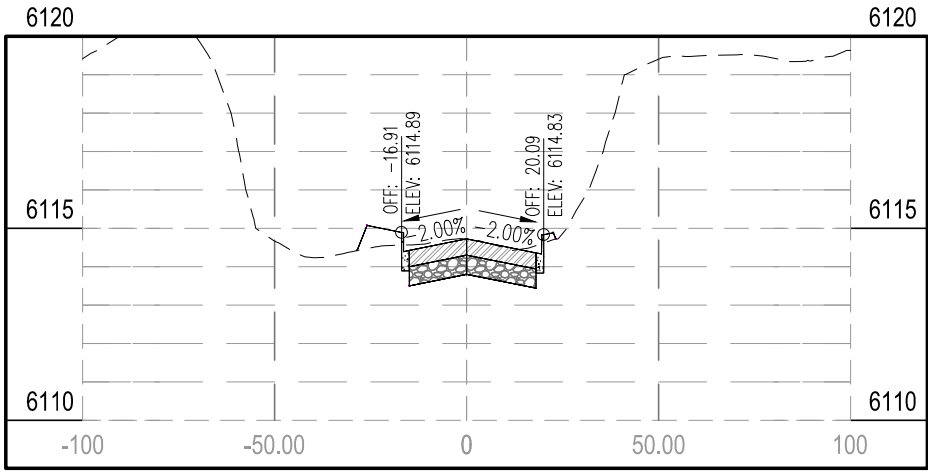

STA 4+00.00

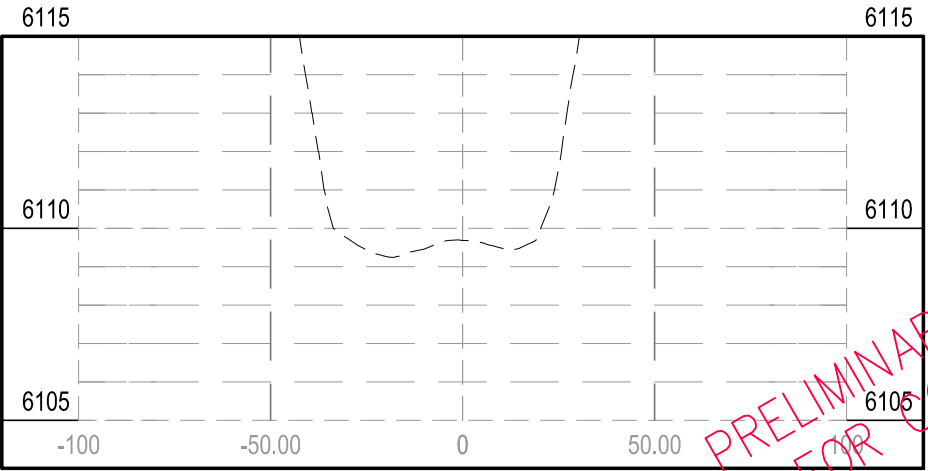

STA 5+50.00

PRELIMINARY PLANS  
NOT FOR CONSTRUCTION

| NO. | REVISION | DATE |
|-----|----------|------|
|     |          |      |
|     |          |      |
|     |          |      |
|     |          |      |
|     |          |      |

PREPARED FOR:  
MPO  
2101 O'NEIL AVE.  
RM 205  
CHEYENNE, WY. 82001


PROJECT: FOX FARM ROAD STREET IMPROVEMENTS  
DRAWING TITLE: WALTERSCHIED BLVD. CROSS SECTIONS STA. 4+00 - 5+50

avi p.c.  
engineering  
planning  
surveying  
PHONE (307) 637-6017  
1103 OLD TOWN LANE, SUITE 101  
CHEYENNE, WY 82009  
AVI@AVIFPC.COM


DATE: 6-20-13  
DRAWN BY: SRL  
DESIGNED BY: TC  
CHECKED BY: TC

JOB NO.: 2-3211-B


XS-23 83  
SHEET NO. OF

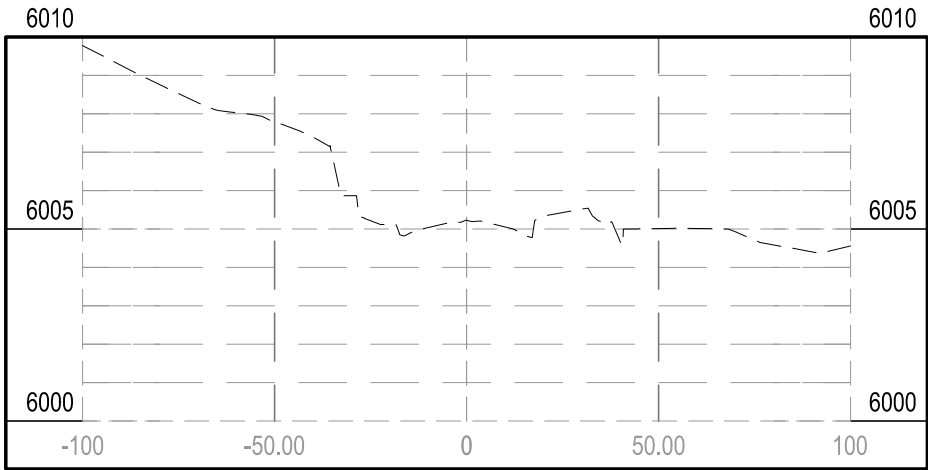


STA 1+00.00

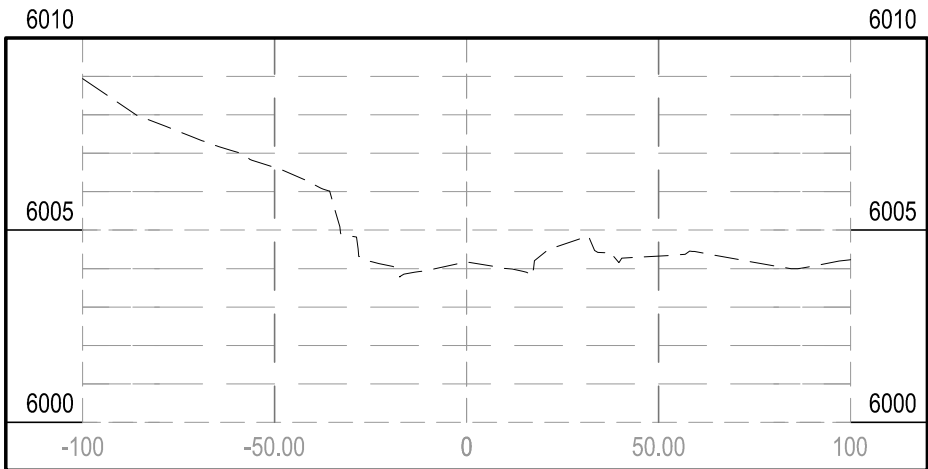


STA 0+50.00

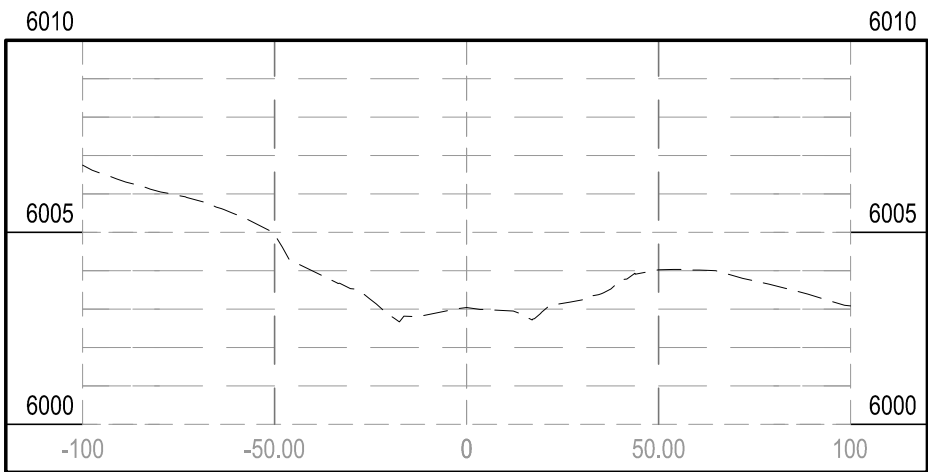


STA 0+00.00

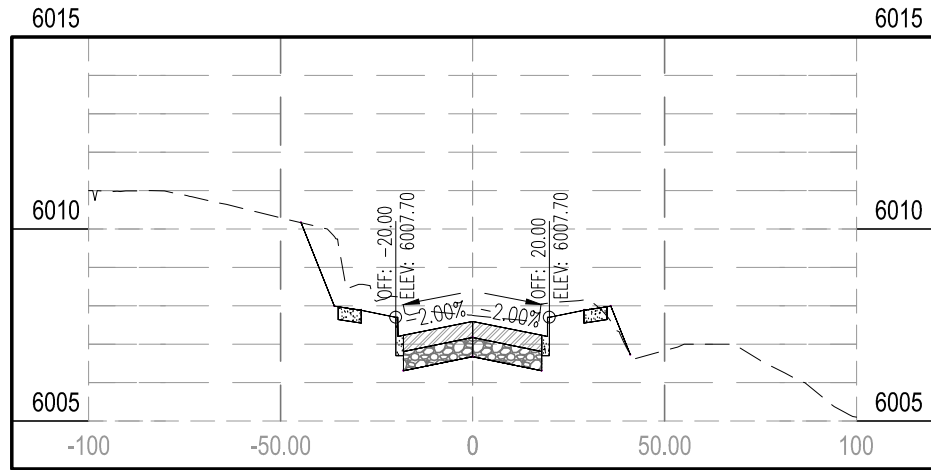

STA 2+50.00

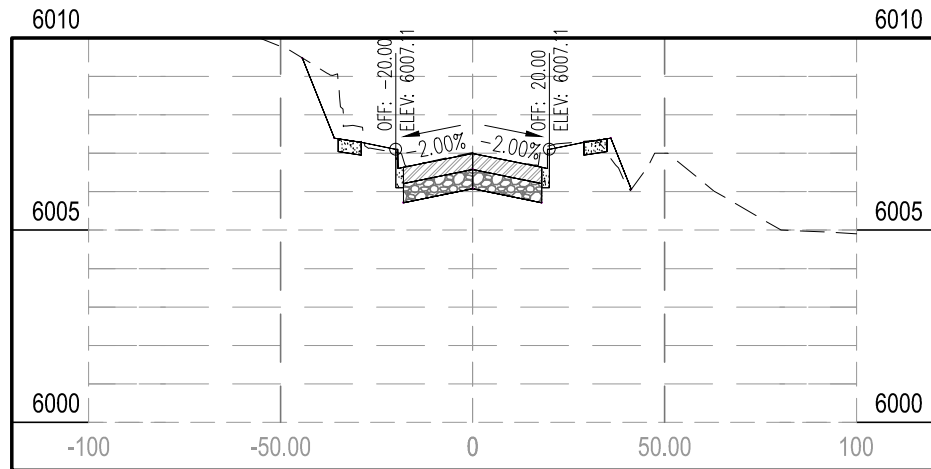

STA 2+00.00

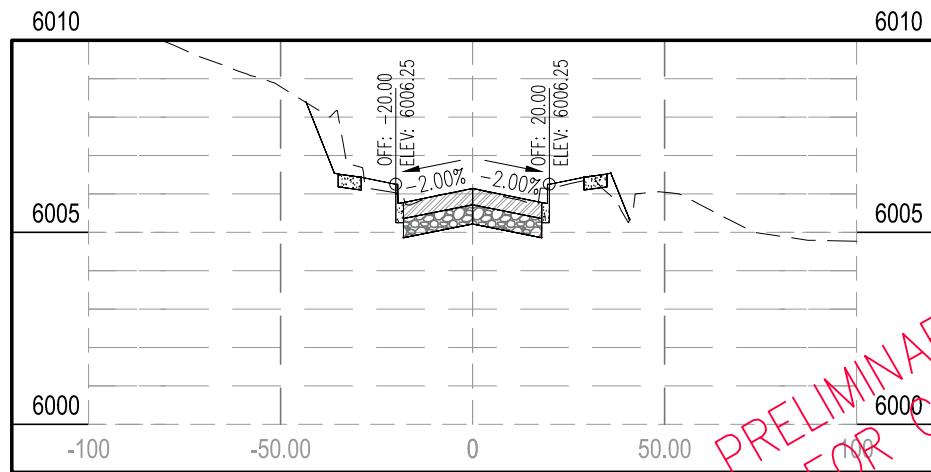

STA 1+50.00

PRELIMINARY PLANS  
NOT FOR CONSTRUCTION

| NO. | REVISION | DATE |
|-----|----------|------|
|     |          |      |
|     |          |      |
|     |          |      |
|     |          |      |

PREPARED FOR:  
MPO  
2101 ONEIL AVE.  
RM 205  
CHEYENNE, WY. 82001


PROJECT: FOX FARM ROAD STREET IMPROVEMENTS  
DRAWING TITLE: AVENUE C CROSS SECTIONS STA. 0+00 - 2+50

avi p.c.  
engineering  
planning  
surveying  
PHONE (307) 637-6017  
1103 OLD TOWN LANE, SUITE 101  
CHEYENNE, WY 82009  
AVI@AVIPC.COM


DATE: 6-20-13  
DRAWN BY: SRL  
DESIGNED BY: TC  
CHECKED BY: TC

JOB NO.: 2-3211-B


XS-24 83  
SHEET NO. OF

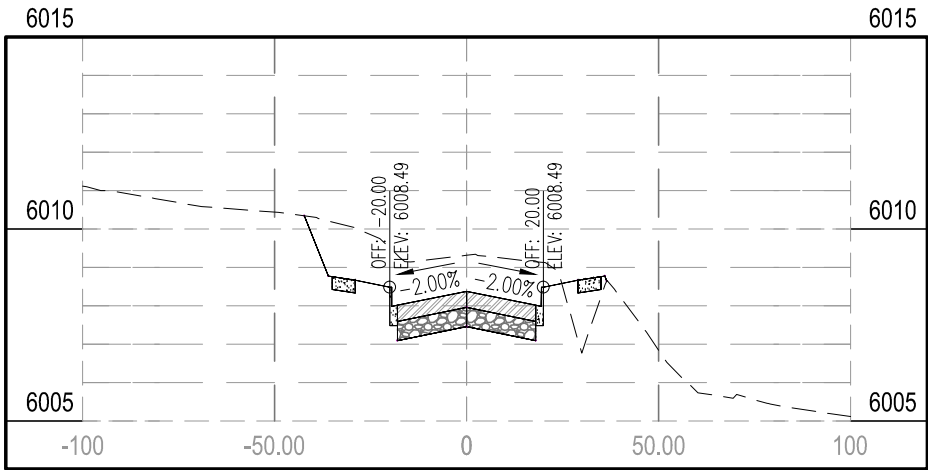


STA 4+00.00

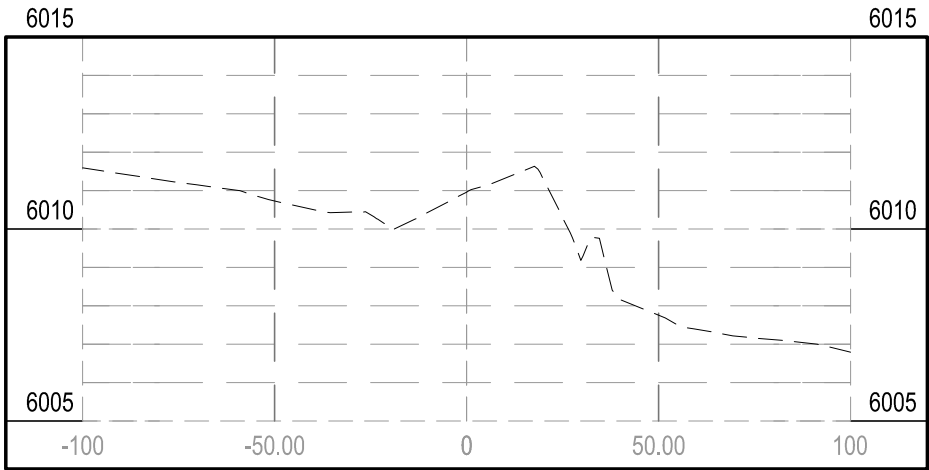


STA 5+00.00

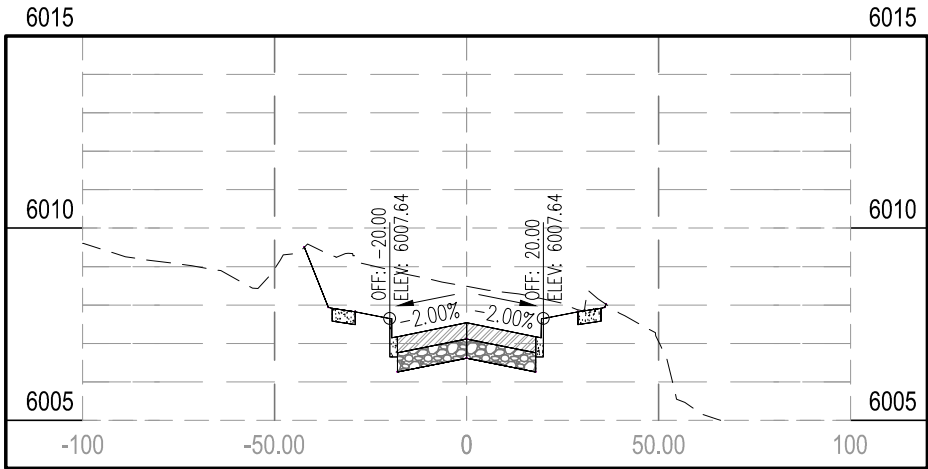


STA 3+50.00

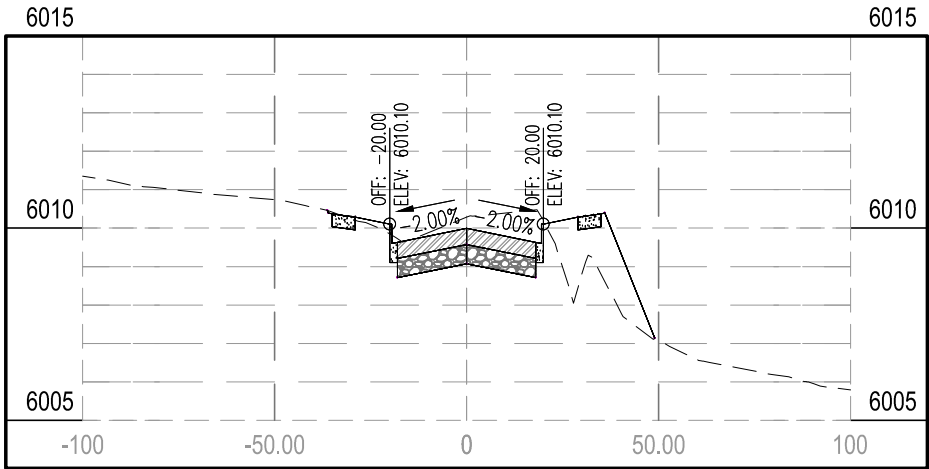

STA 4+51.50

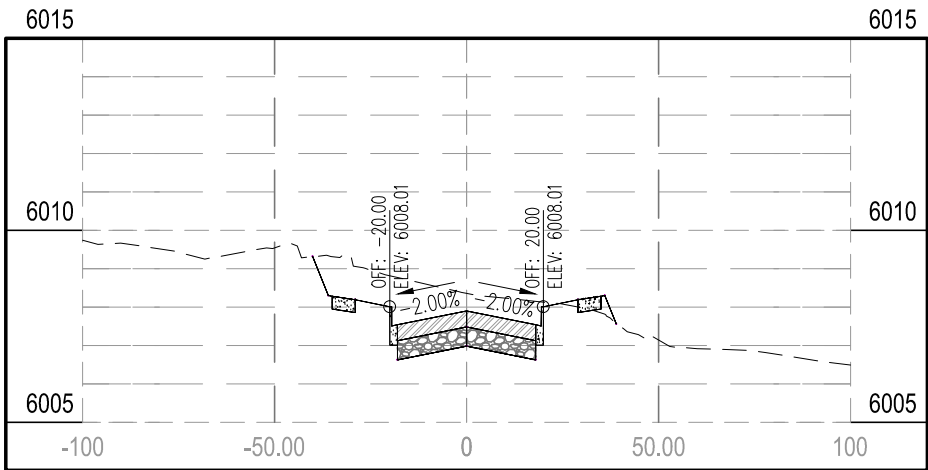

STA 3+00.00

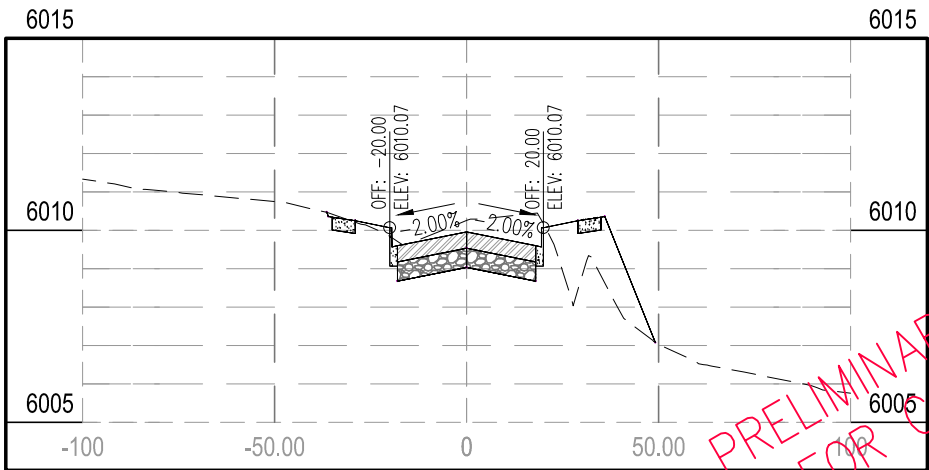

STA 4+50.00

PRELIMINARY PLANS  
NOT FOR CONSTRUCTION

| NO. | REVISION | DATE |
|-----|----------|------|
|     |          |      |
|     |          |      |
|     |          |      |
|     |          |      |

PREPARED FOR:  
MPO  
2101 ONEIL AVE.  
RM 205  
CHEYENNE, WY. 82001

PROJECT: FOX FARM ROAD STREET IMPROVEMENTS  
DRAWING TITLE: AVENUE C CROSS SECTIONS STA. 3+00 - 5+00


avi p.c.  
engineering  
planning  
surveying  
PHONE (307) 637-6017  
1103 OLD TOWN LANE, SUITE 101  
CHEYENNE, WY 82009  
AVI@AVIFPC.COM

DATE: 6-20-13  
DRAWN BY: SRL  
DESIGNED BY: TC  
CHECKED BY: TC


JOB NO.: 2-3211-B

XS-25 83  
SHEET NO. OF


H:\3211\design\3211B FOX FARM STREET IMP.dwg Aug 30, 2013 4:27pm jwilson

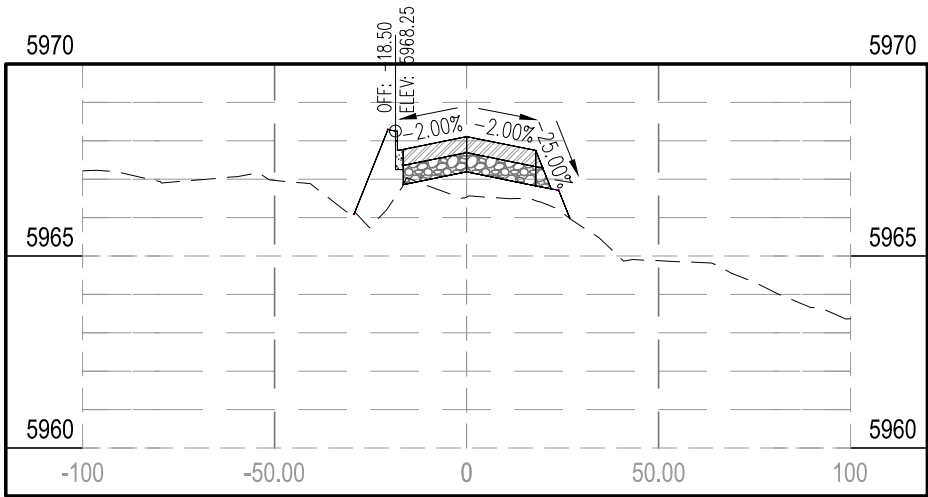


STA 1+16.50

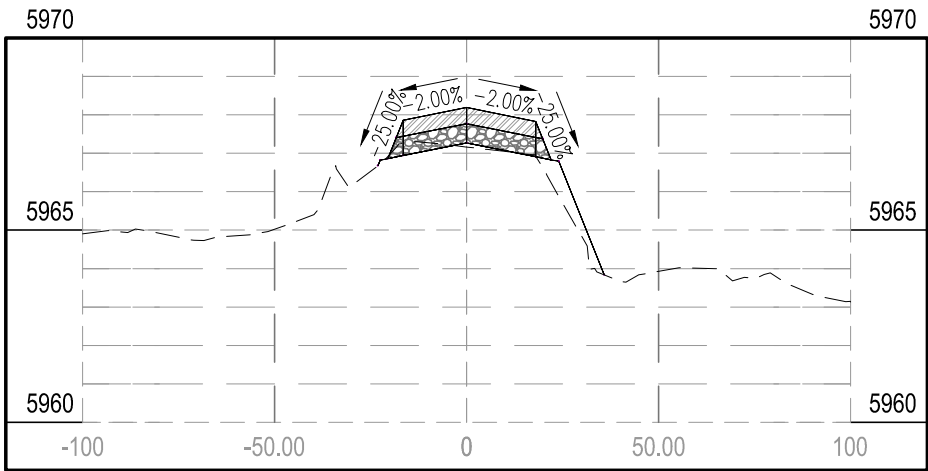


STA 1+00.00

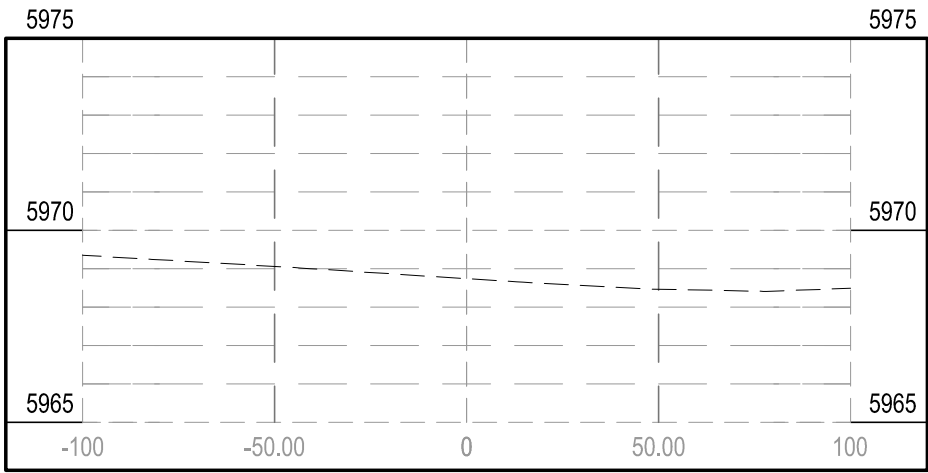


STA 0+50.00

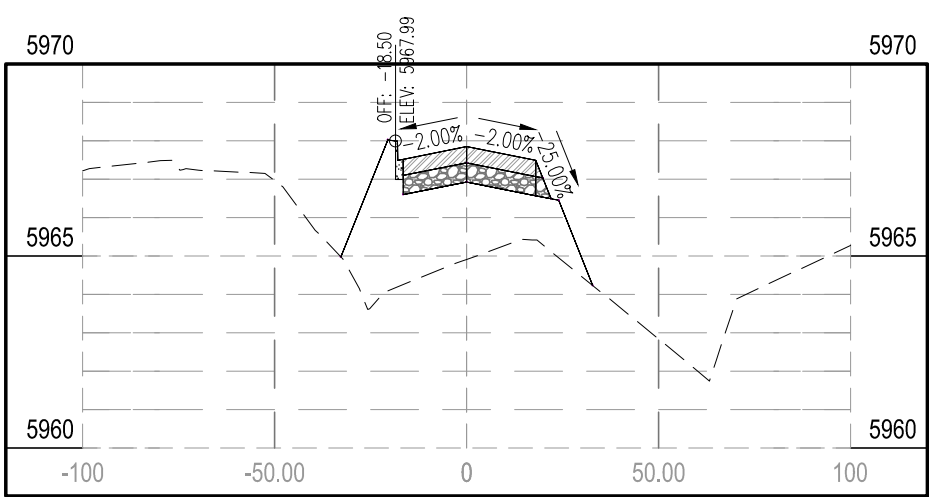

STA 1+68.51

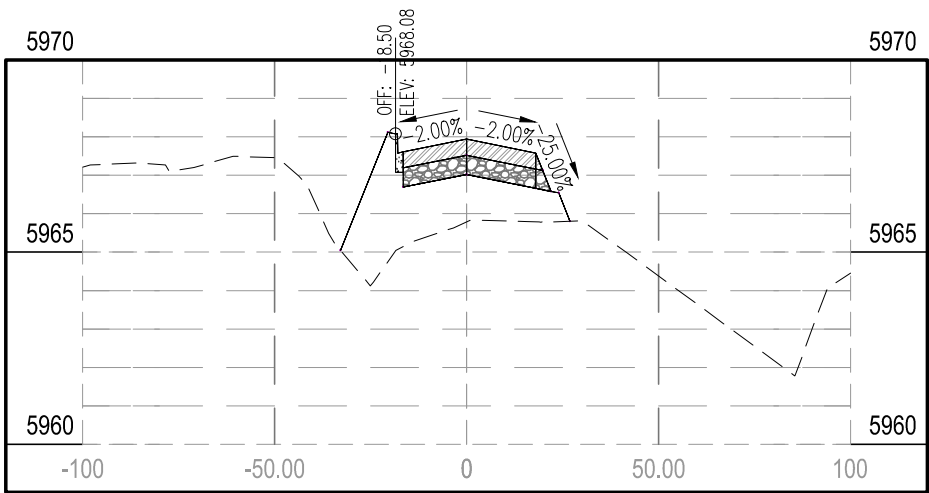

STA 1+50.00

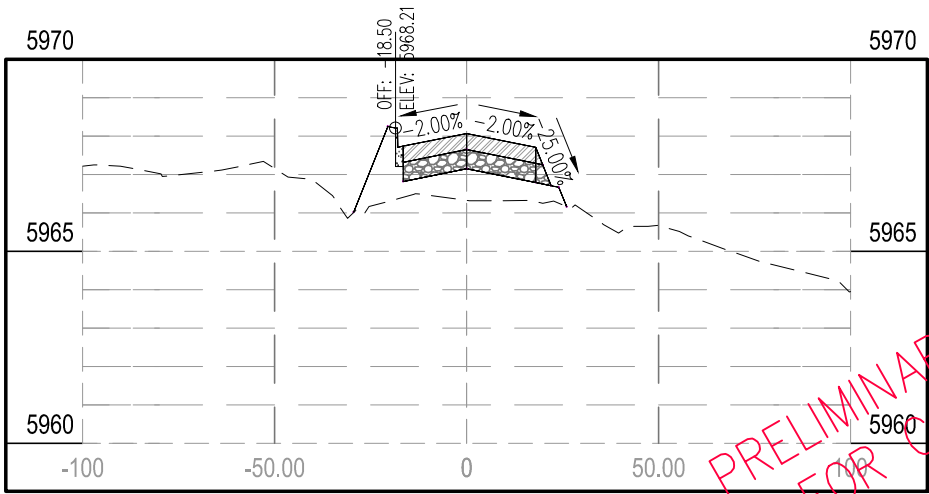

STA 1+25.00

PRELIMINARY PLANS  
NOT FOR CONSTRUCTION

| NO. | REVISION | DATE |
|-----|----------|------|
|     |          |      |
|     |          |      |
|     |          |      |
|     |          |      |

PREPARED FOR:  
MPO  
2101 ONEIL AVE.  
RM 205  
CHEYENNE, WY. 82001


PROJECT: FOX FARM ROAD STREET IMPROVEMENTS  
DRAWING TITLE: BURLINGTON TRAILS RD. CROSS SECTIONS STA. 0+50 -1+68.51

avi p.c.  
engineering  
planning  
surveying  
PHONE (307) 637-6017  
1103 OLD TOWN LANE, SUITE 101  
CHEYENNE, WY 82009  
AVI@AVIFC.COM


DATE: 6-20-13  
DRAWN BY: SRL  
DESIGNED BY: TC  
CHECKED BY: TC

JOB NO.: 2-3211-B


XS-26 83  
SHEET NO. OF

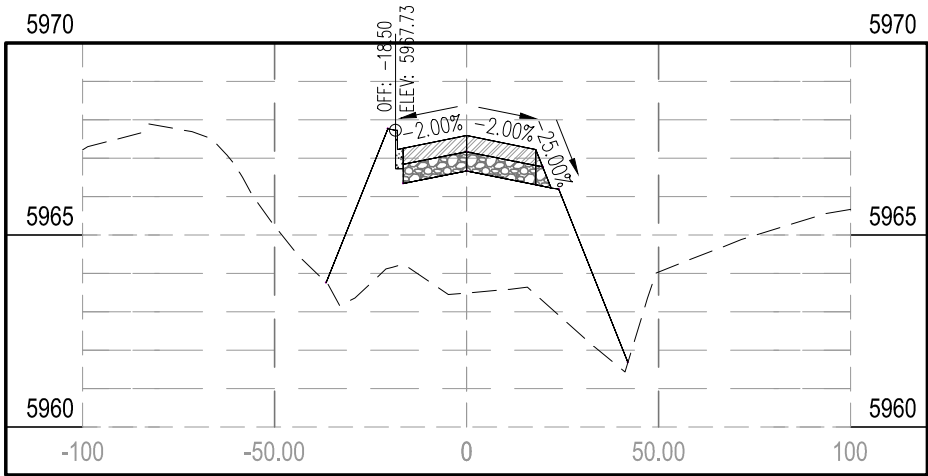


STA 2+20.52

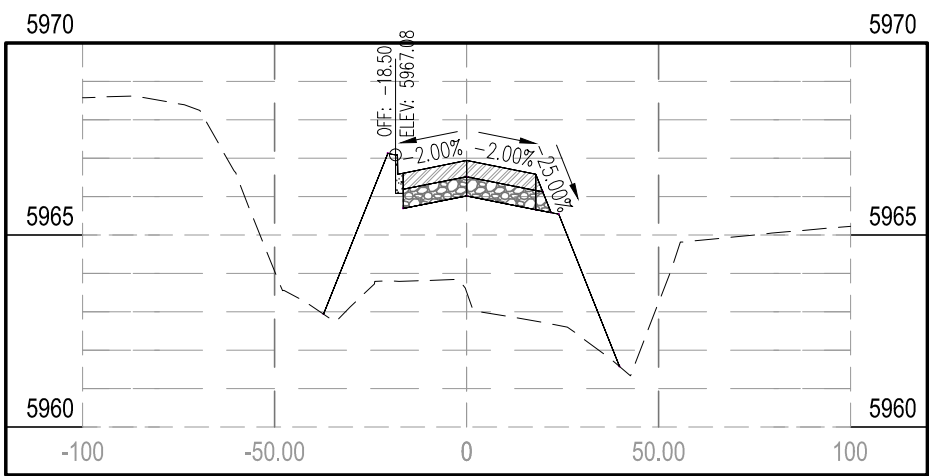


STA 3+50.00

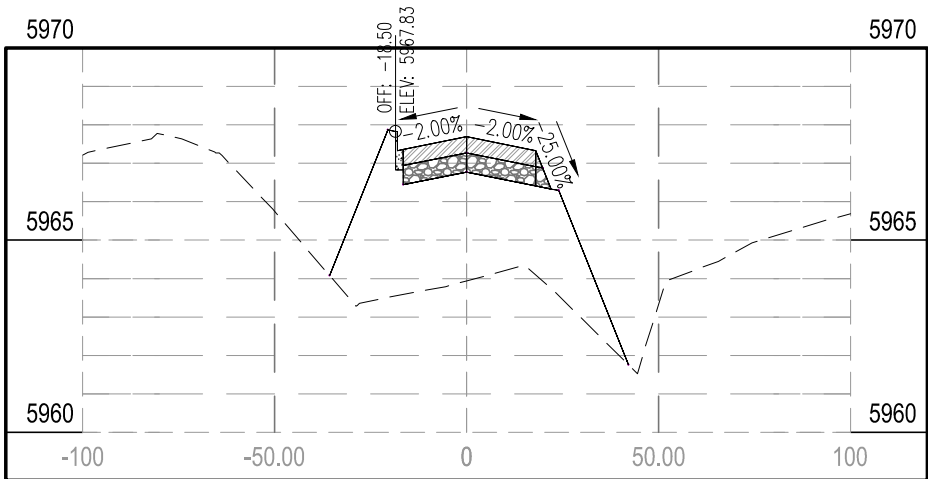


STA 2+00.00

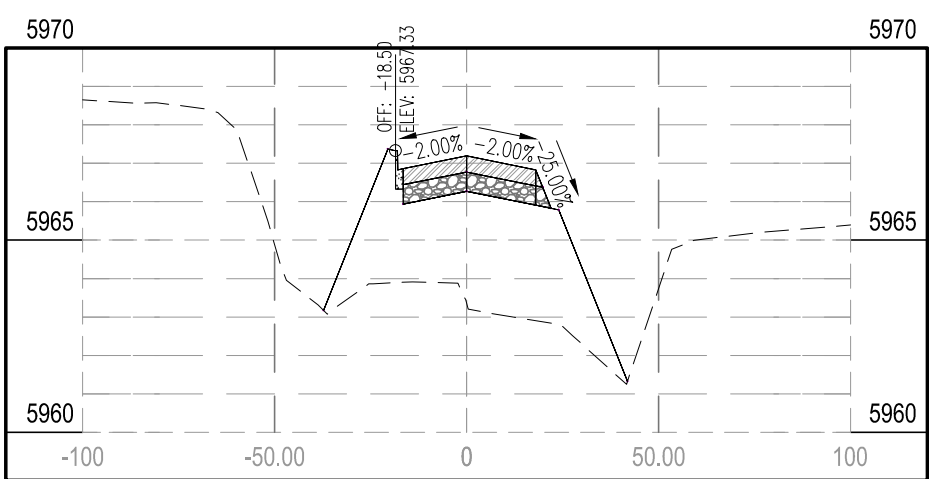

STA 3+00.00

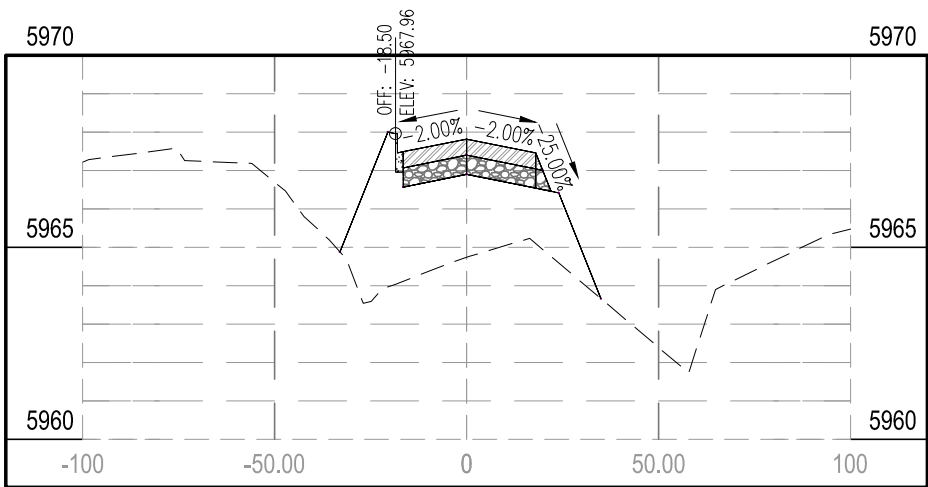

STA 1+75.00

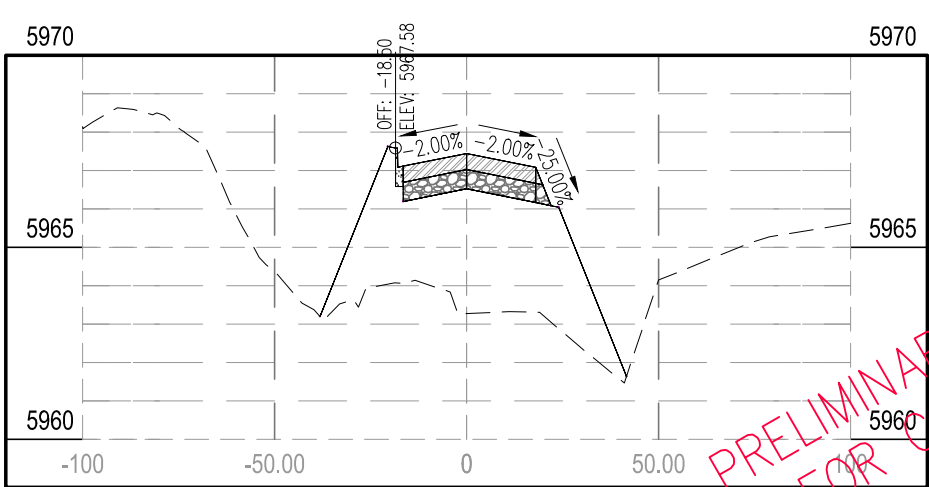

STA 2+50.00

PRELIMINARY PLANS  
NOT FOR CONSTRUCTION

| NO. | REVISION | DATE |
|-----|----------|------|
|     |          |      |
|     |          |      |
|     |          |      |
|     |          |      |

PREPARED FOR:  
MPO  
2101 O'NEIL AVE.  
RM 205  
CHEYENNE, WY. 82001

PROJECT: FOX FARM ROAD STREET  
IMPROVEMENTS  
DRAWING TITLE:  
BURLINGTON TRAILS RD. CROSS  
SECTIONS STA. 1+75 - 3+50


avi p.c.  
engineering  
planning  
surveying  
PHONE (307) 637-6017  
1103 OLD TOWN LANE, SUITE 101  
CHEYENNE, WY 82009  
AVI@AVIPC.COM

DATE:  
6-20-13  
DRAWN BY:  
SRL  
DESIGNED BY:  
TC  
CHECKED BY:  
TC


JOB NO.:  
2-3211-B

XS-27 83  
SHEET NO. OF


H:\3211\design\3211B FOX FARM STREET IMP.dwg Aug 30, 2013 4:27pm jwilson

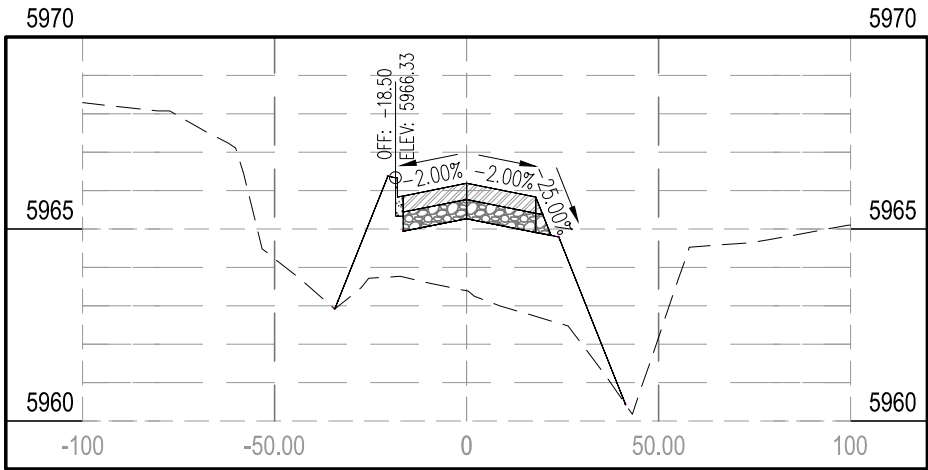


STA 5+00.00

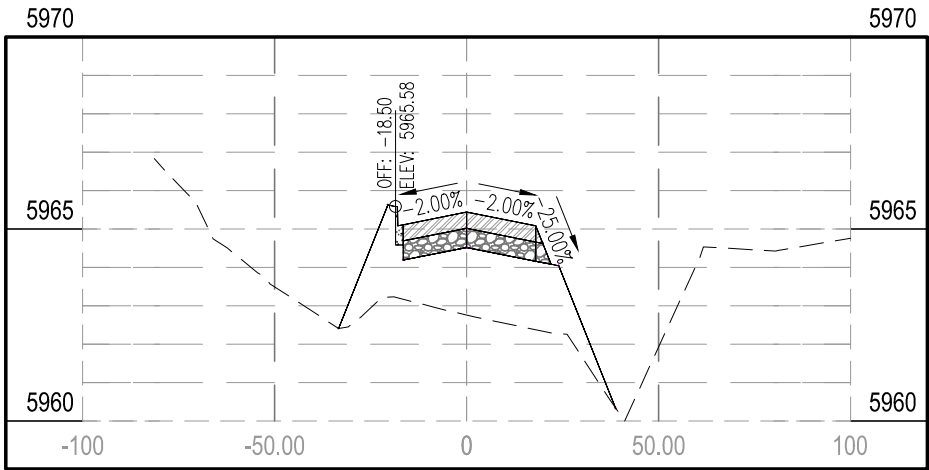


STA 6+50.00

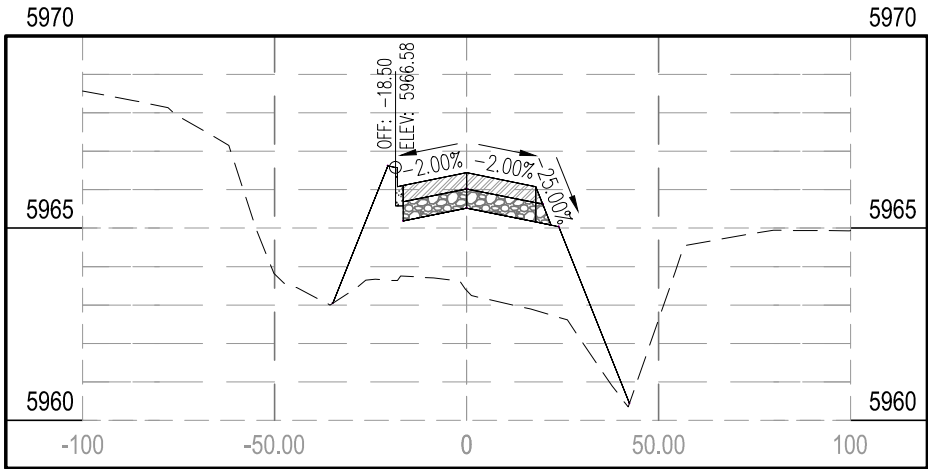


STA 4+50.00

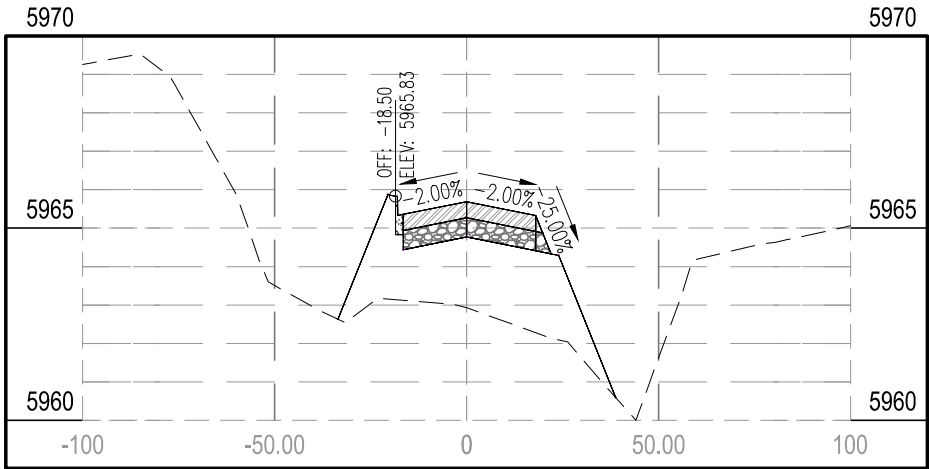

STA 6+00.00

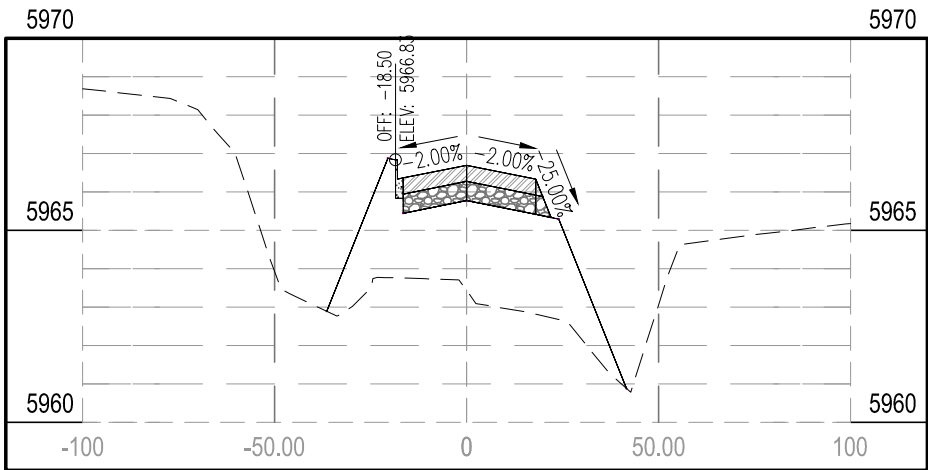

STA 4+00.00

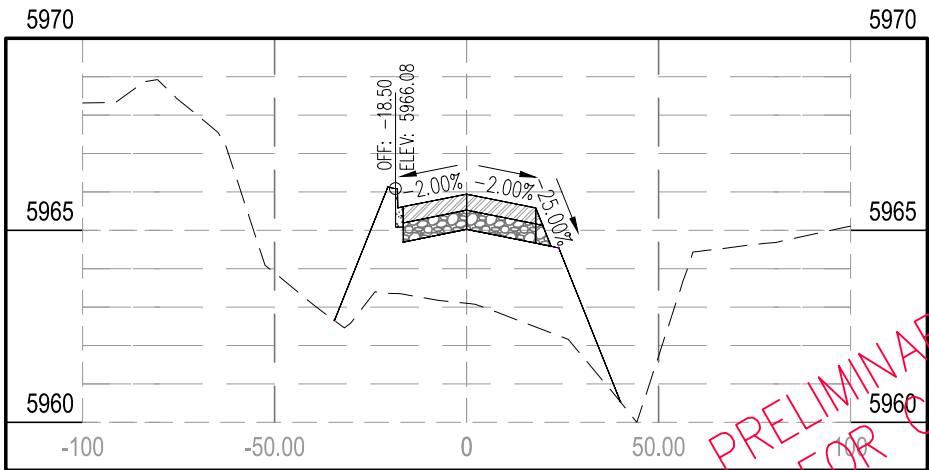

STA 5+50.00

PRELIMINARY PLANS  
NOT FOR CONSTRUCTION

| NO. | REVISION | DATE |
|-----|----------|------|
|     |          |      |
|     |          |      |
|     |          |      |
|     |          |      |

PREPARED FOR:  
MPO  
2101 ONEIL AVE.  
RM 205  
CHEYENNE, WY. 82001


PROJECT: FOX FARM ROAD STREET  
IMPROVEMENTS  
DRAWING TITLE:  
BURLINGTON TRAILS RD. CROSS  
SECTIONS STA. 4+00 - 6+50

avi p.c.  
engineering  
planning  
surveying  
PHONE (307) 637-6017  
1103 OLD TOWN LANE, SUITE 101  
CHEYENNE, WY 82009  
AVI@AVIPC.COM


DATE:  
6-20-13  
DRAWN BY:  
SRL  
DESIGNED BY:  
TC  
CHECKED BY:  
TC

JOB NO.:  
2-3211-B


XS-28 83  
SHEET NO. OF

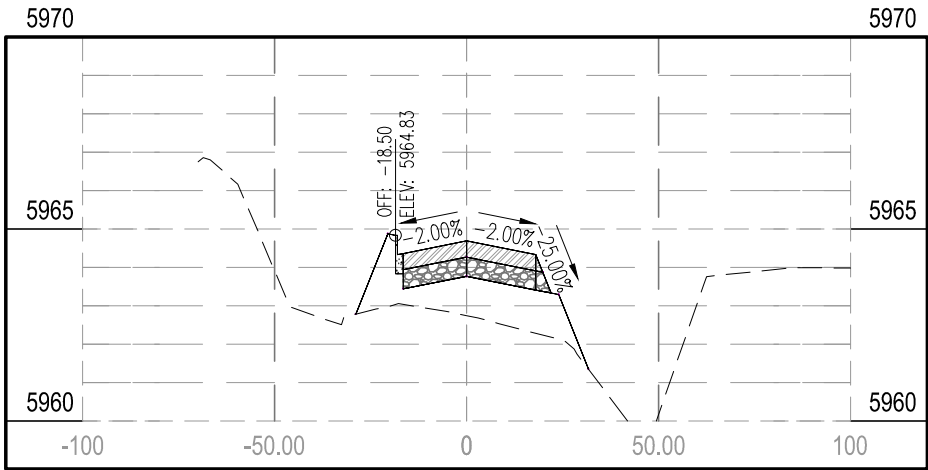


STA 8+00.00

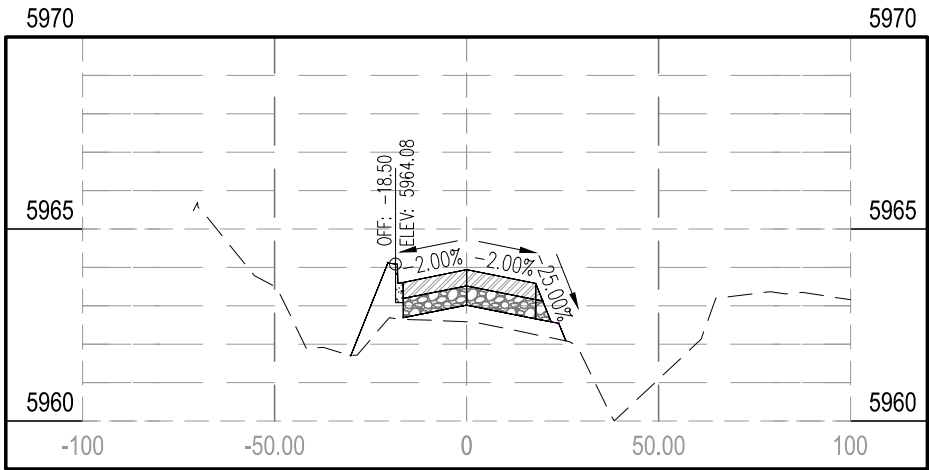


STA 9+50.00

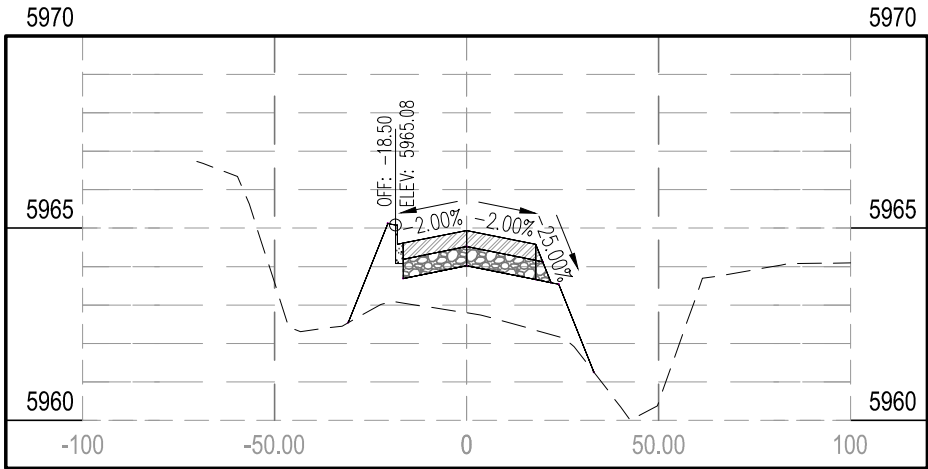


STA 7+50.00

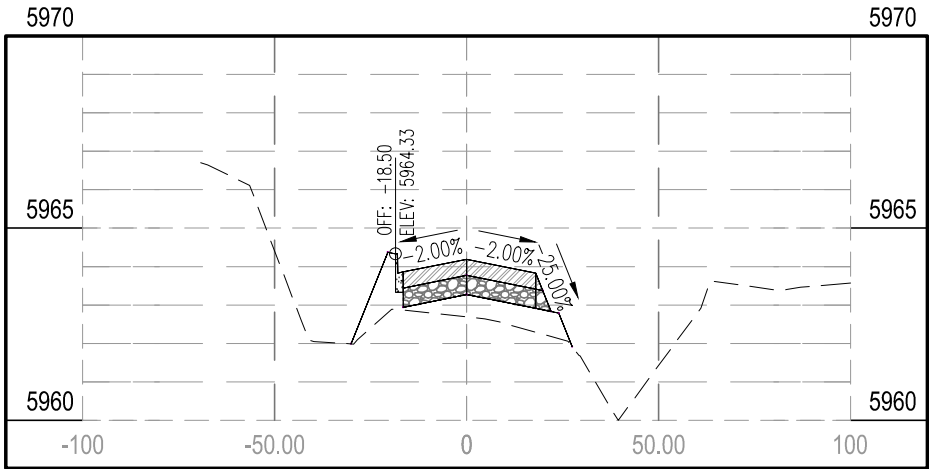

STA 9+00.00

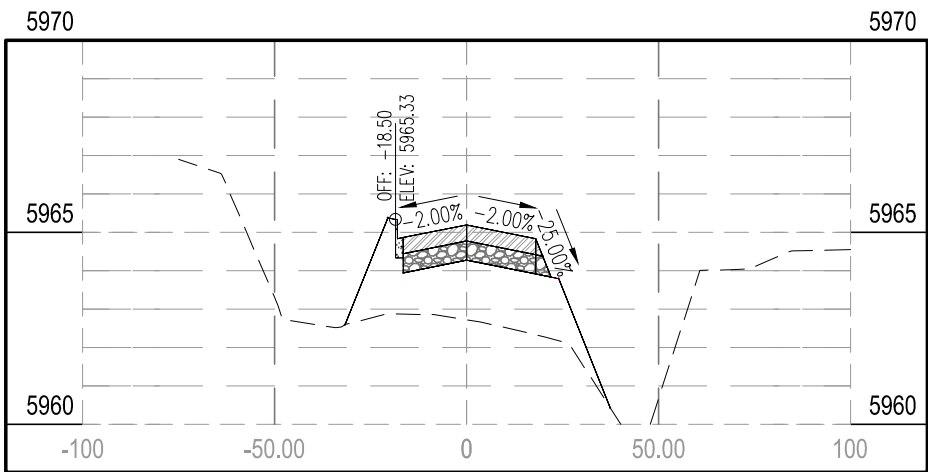

STA 7+00.00

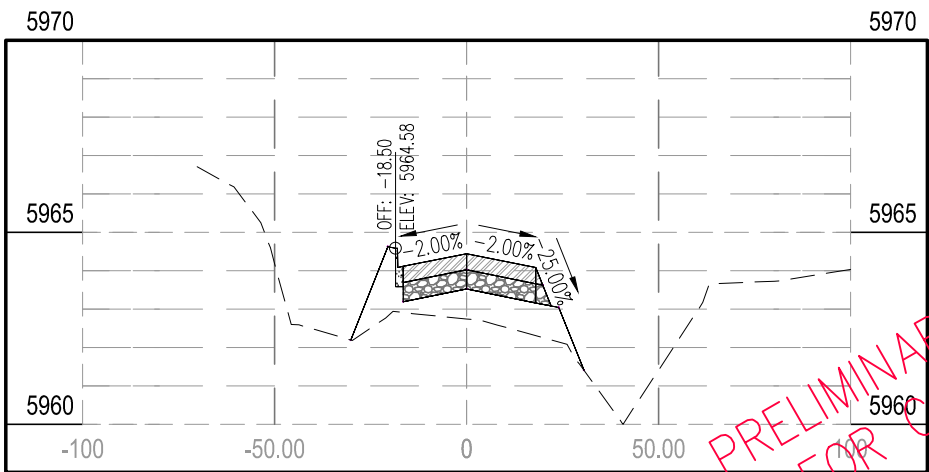

STA 8+50.00

PRELIMINARY PLANS  
NOT FOR CONSTRUCTION

| NO. | REVISION | DATE |
|-----|----------|------|
|     |          |      |
|     |          |      |
|     |          |      |
|     |          |      |

PREPARED FOR:  
MPO  
2101 ONEIL AVE.  
RM 205  
CHEYENNE, WY. 82001


PROJECT: FOX FARM ROAD STREET IMPROVEMENTS  
DRAWING TITLE: BURLINGTON TRAILS RD. CROSS SECTIONS STA. 7+00 - 9+50

avi p.c.  
engineering  
planning  
surveying  
PHONE (307) 637-6017  
1103 OLD TOWN LANE, SUITE 101  
CHEYENNE, WY 82009  
AVI@AVIPC.COM


DATE: 6-20-13  
DRAWN BY: SRL  
DESIGNED BY: TC  
CHECKED BY: TC

JOB NO.: 2-3211-B


XS-29 83  
SHEET NO. OF

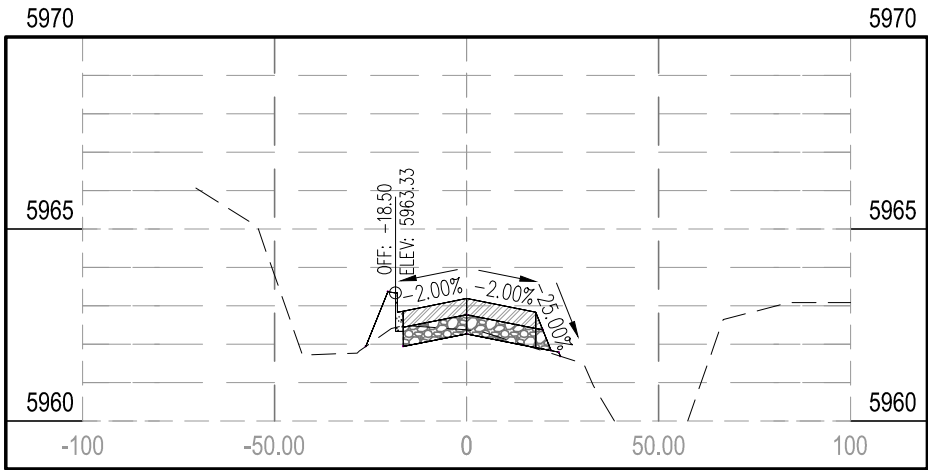


STA 11+00.00

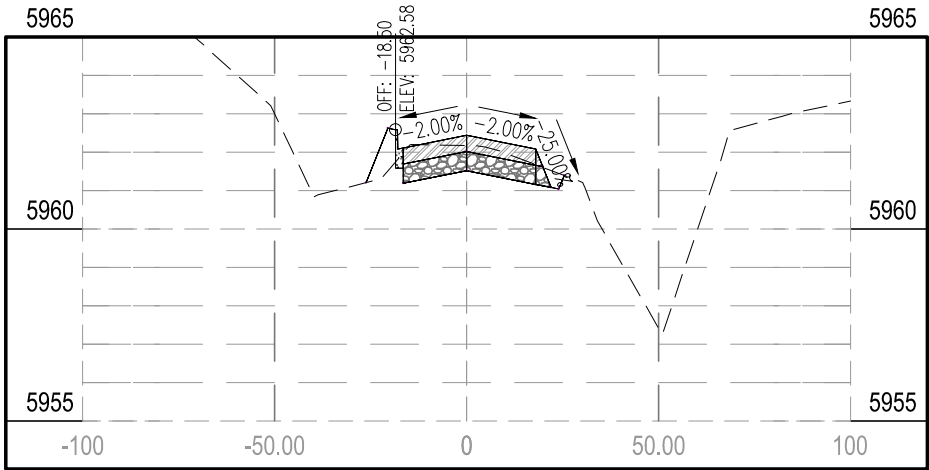


STA 12+50.00

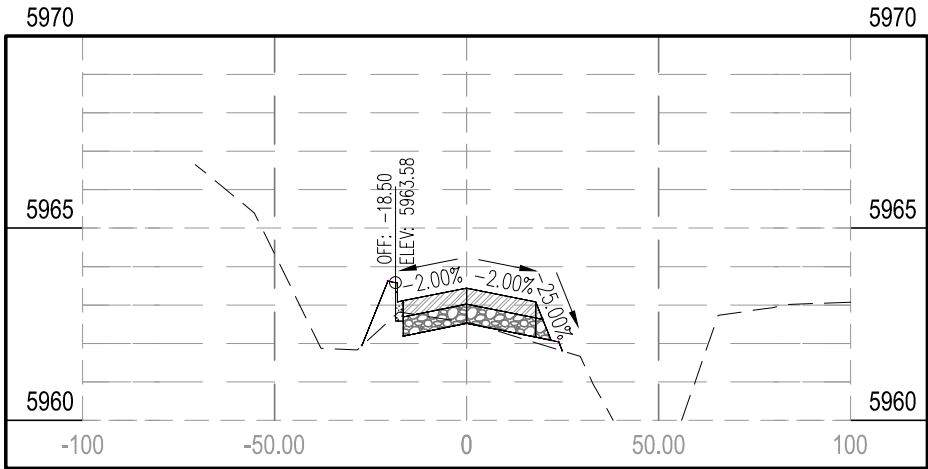


STA 10+50.00

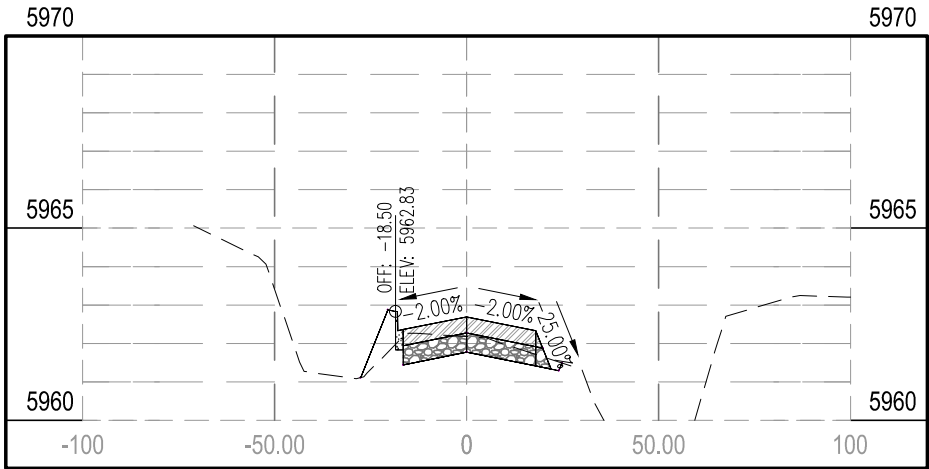

STA 12+00.00

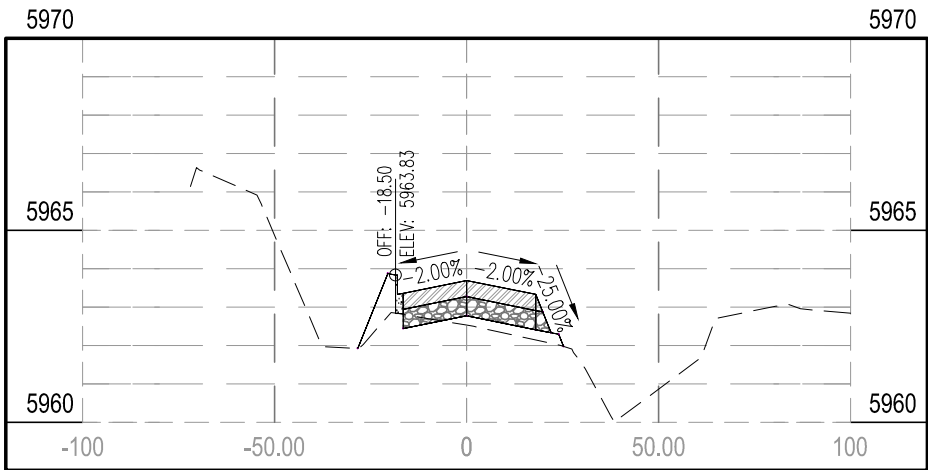

STA 10+00.00

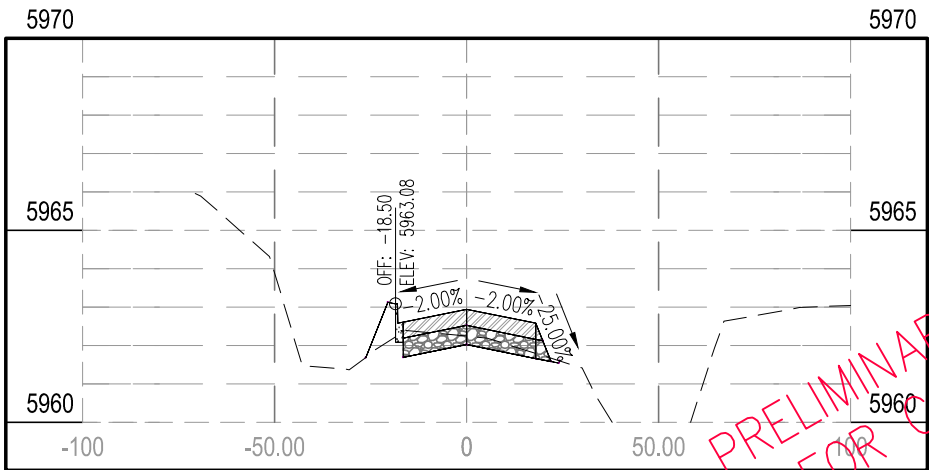

STA 11+50.00

PRELIMINARY PLANS  
NOT FOR CONSTRUCTION

| NO. | REVISION | DATE |
|-----|----------|------|
|     |          |      |
|     |          |      |
|     |          |      |
|     |          |      |

PREPARED FOR:  
MPO  
2101 ONEIL AVE.  
RM 205  
CHEYENNE, WY. 82001

PROJECT: FOX FARM ROAD STREET IMPROVEMENTS  
DRAWING TITLE: BURLINGTON TRAILS RD. CROSS SECTIONS STA. 10+00 - 12+50


avi p.c.  
engineering  
planning  
surveying  
PHONE (307) 637-6017  
1103 OLD TOWN LANE, SUITE 101  
CHEYENNE, WY 82009  
AVI@AVIPC.COM

DATE: 6-20-13  
DRAWN BY: SRL  
DESIGNED BY: TC  
CHECKED BY: TC


JOB NO.: 2-3211-B

XS-30 83  
SHEET NO. OF


H:\3211\design\3211B FOX FARM STREET IMP.dwg Aug 30, 2013 4:28pm jwilson

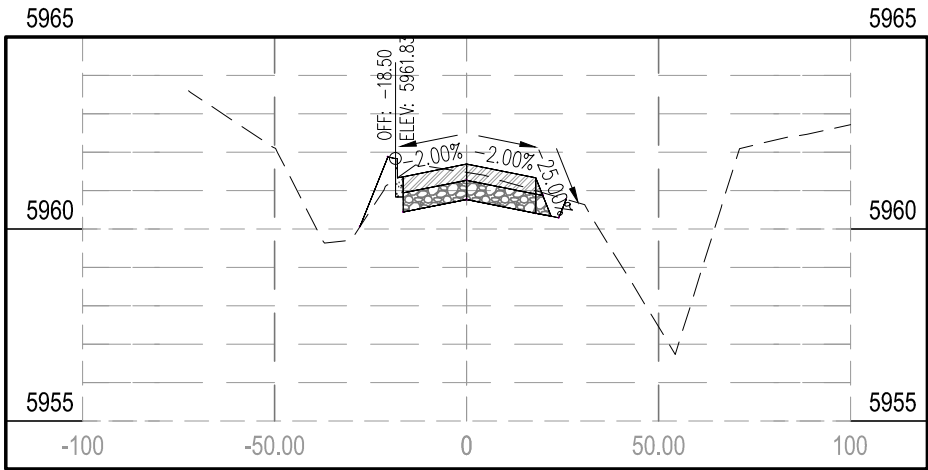


STA 14+00.00

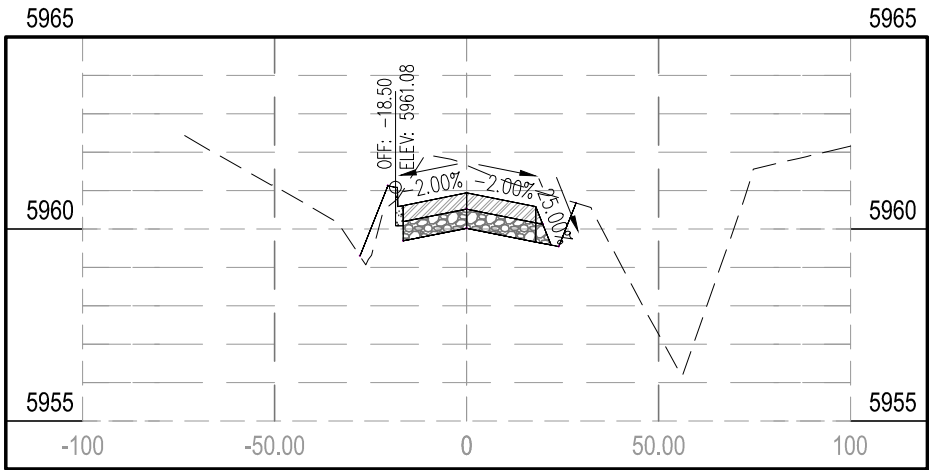


STA 15+50.00

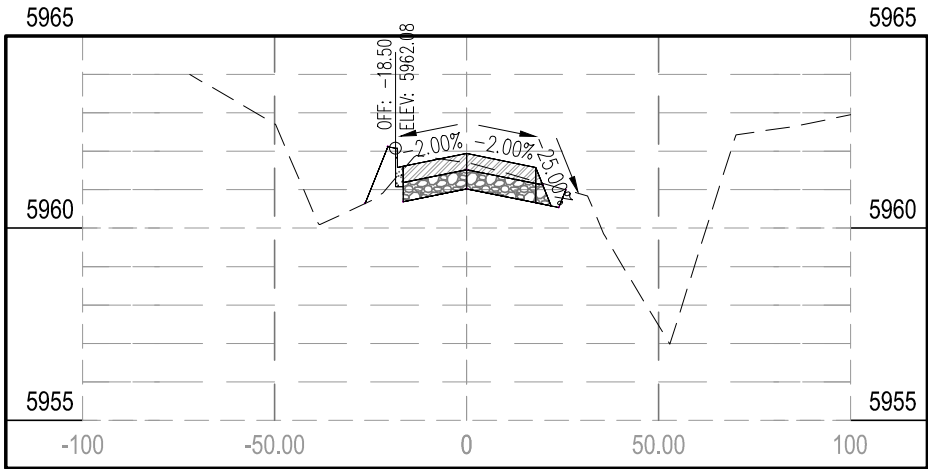


STA 13+50.00

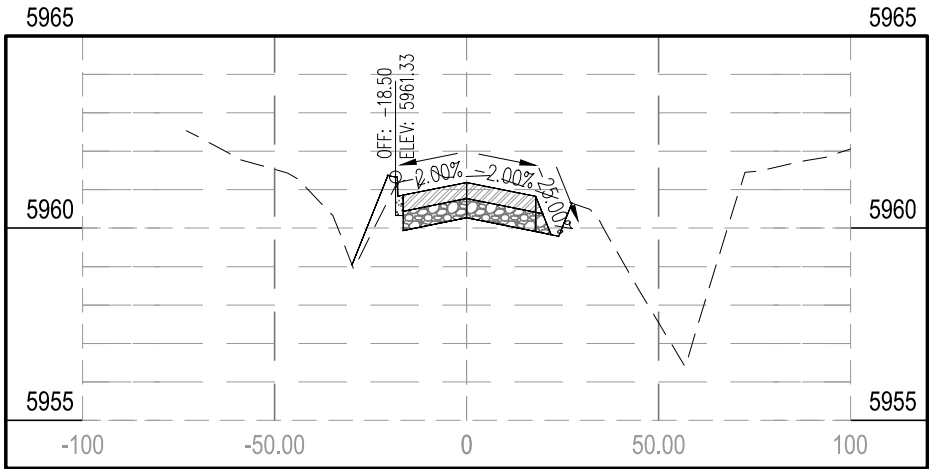

STA 15+00.00

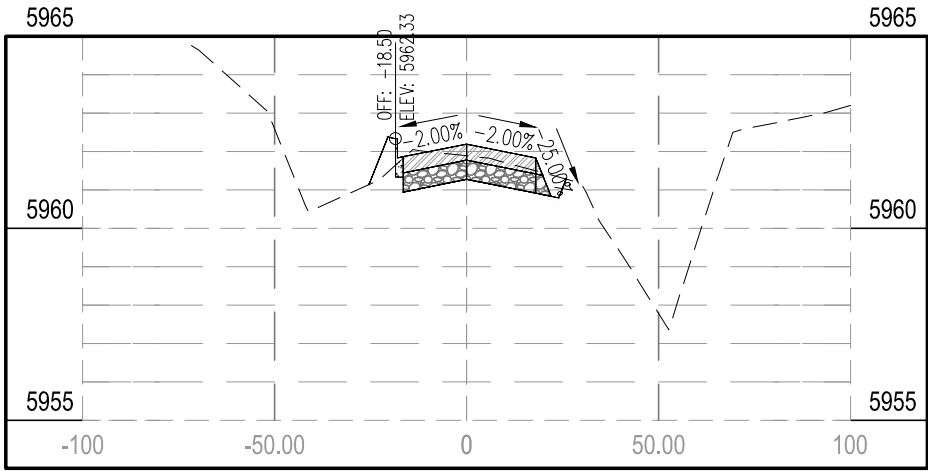

STA 13+00.00

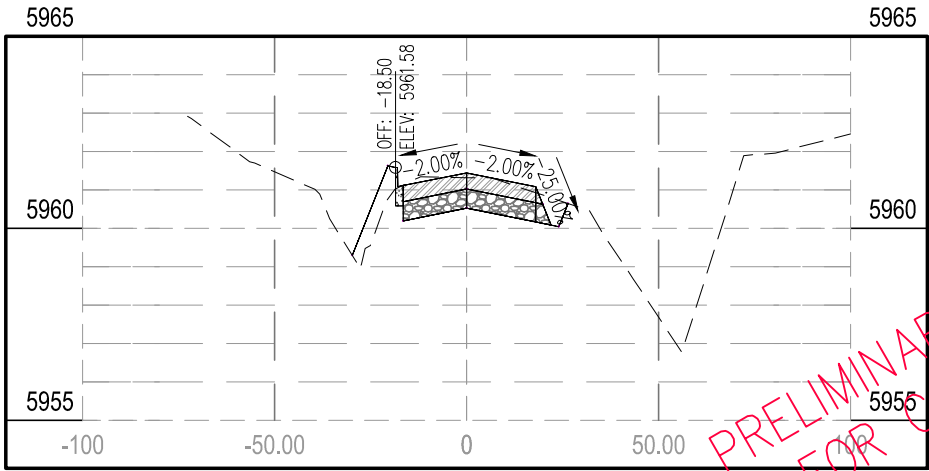

STA 14+50.00

PRELIMINARY PLANS  
NOT FOR CONSTRUCTION

| NO. | REVISION | DATE |
|-----|----------|------|
|     |          |      |
|     |          |      |
|     |          |      |
|     |          |      |

PREPARED FOR:  
MPO  
2101 ONEIL AVE.  
RM 205  
CHEYENNE, WY. 82001


PROJECT: FOX FARM ROAD STREET IMPROVEMENTS  
DRAWING TITLE: BURLINGTON TRAILS RD. CROSS SECTIONS STA. 13+00 - 15+50

avi p.c.  
engineering  
planning  
surveying  
PHONE (307) 637-6017  
1103 OLD TOWN LANE, SUITE 101  
CHEYENNE, WY 82009  
AVI@AVIFC.COM


DATE: 6-20-13  
DRAWN BY: SRL  
DESIGNED BY: TC  
CHECKED BY: TC

JOB NO.: 2-3211-B


XS-31 83  
SHEET NO. OF

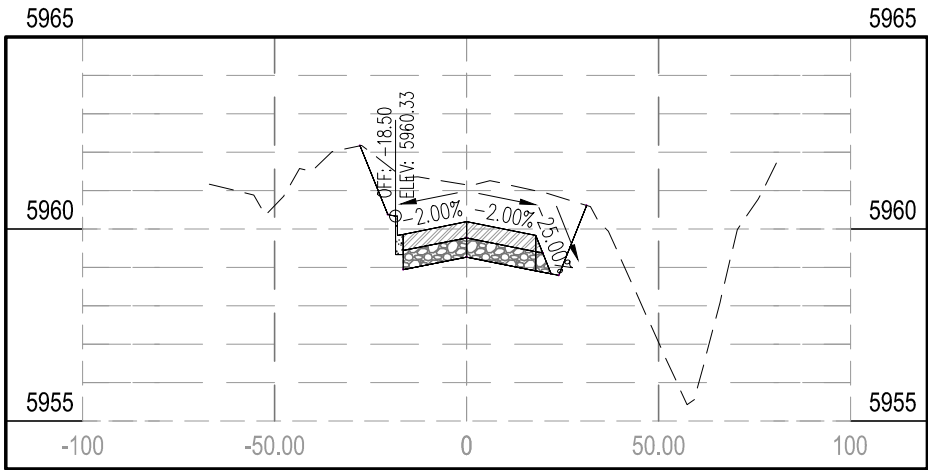


STA 17+00.00

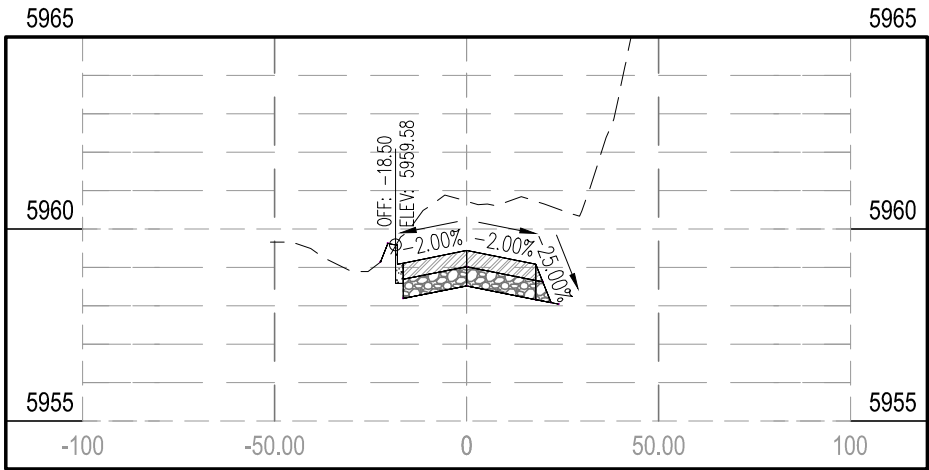


STA 18+50.00

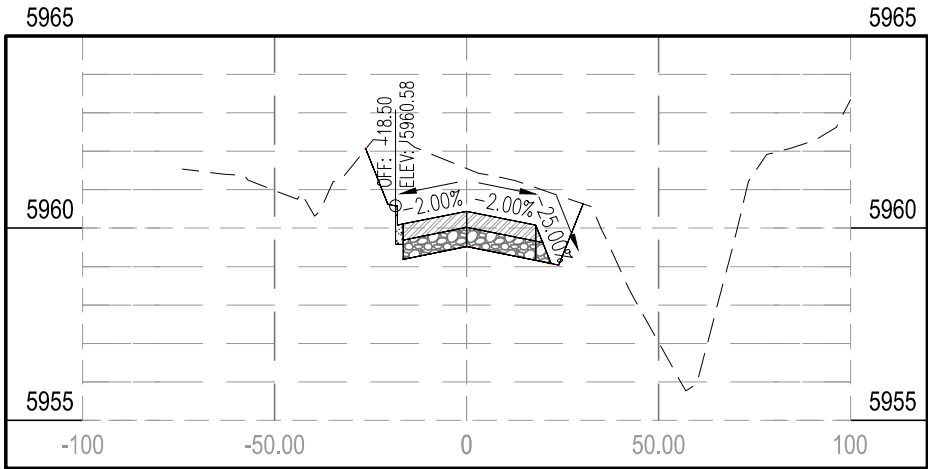


STA 16+50.00

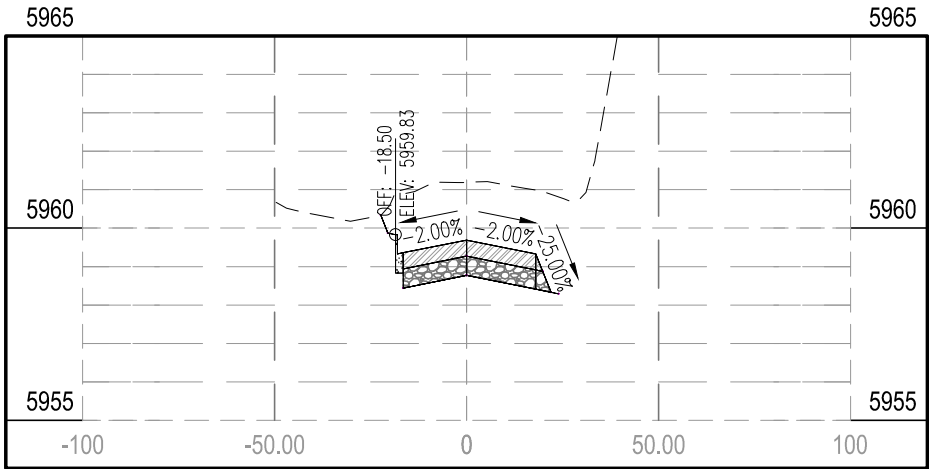

STA 18+00.00

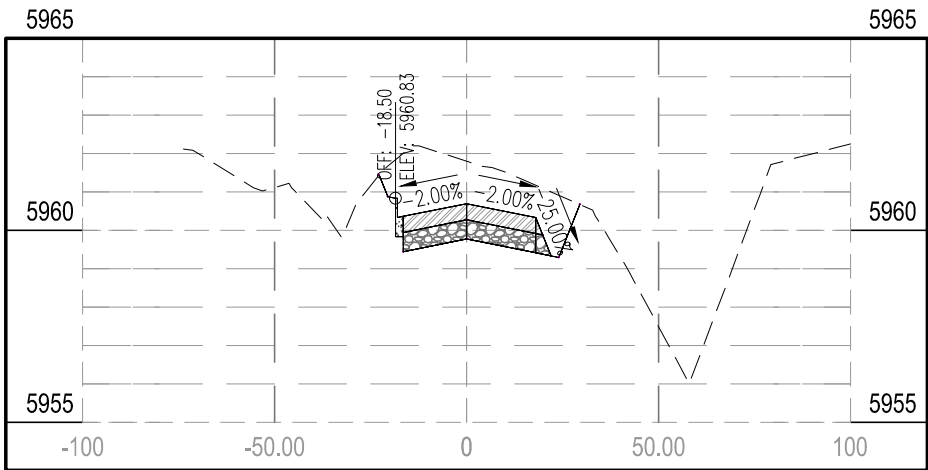

STA 16+00.00

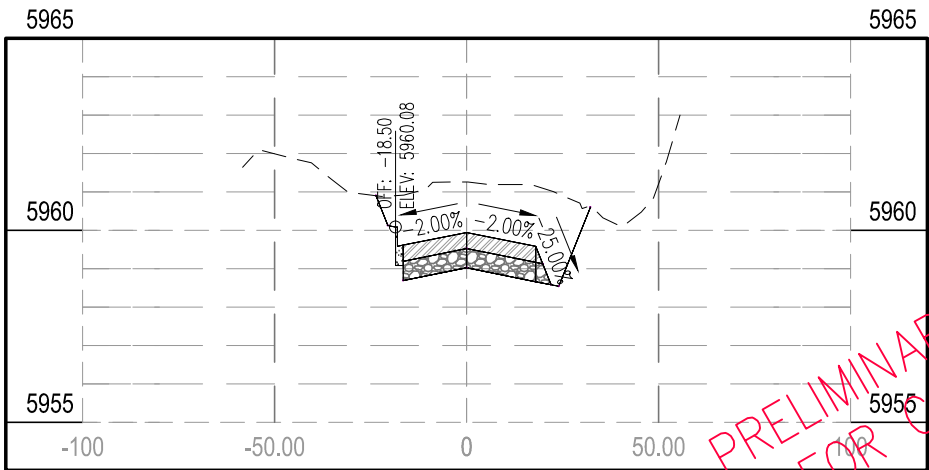

STA 17+50.00

PRELIMINARY PLANS  
NOT FOR CONSTRUCTION

| NO. | REVISION | DATE |
|-----|----------|------|
|     |          |      |
|     |          |      |
|     |          |      |
|     |          |      |
|     |          |      |

PREPARED FOR:  
MPO  
2101 ONEIL AVE.  
RM 205  
CHEYENNE, WY. 82001


PROJECT: FOX FARM ROAD STREET  
IMPROVEMENTS  
DRAWING TITLE:  
BURLINGTON TRAILS RD. CROSS  
SECTIONS STA. 16+00 - 18+50

avi p.c.  
engineering  
planning  
surveying  
PHONE (307) 637-6017  
1103 OLD TOWN LANE, SUITE 101  
CHEYENNE, WY 82009  
AVI@AVIPC.COM


DATE:  
6-20-13  
DRAWN BY:  
SRL  
DESIGNED BY:  
TC  
CHECKED BY:  
TC

JOB NO.:  
2-3211-B


XS-32 83  
SHEET NO. OF

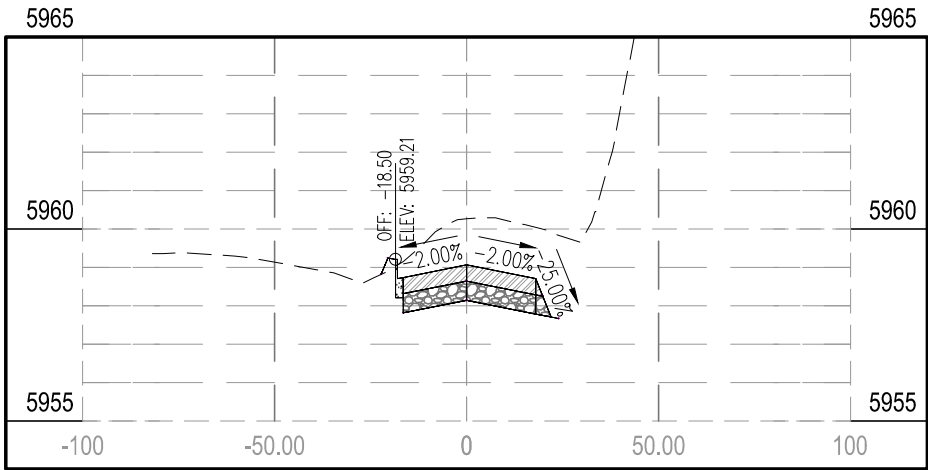


STA 19+25.00

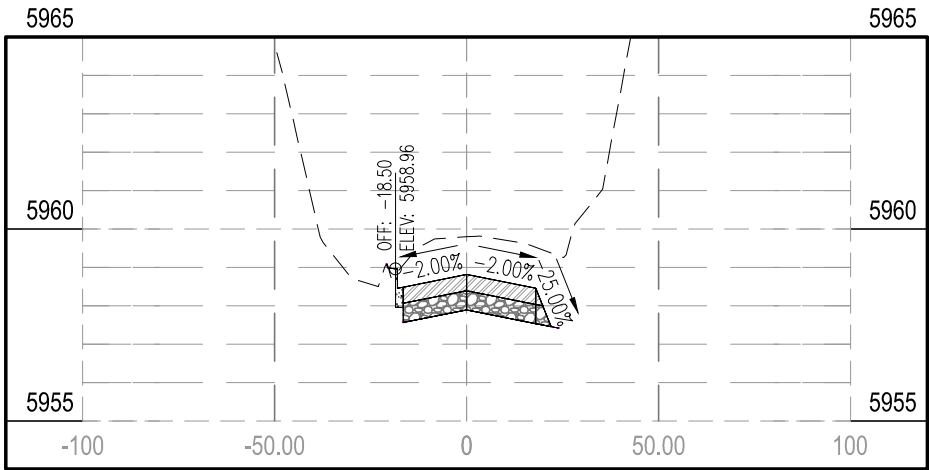


STA 19+75.00

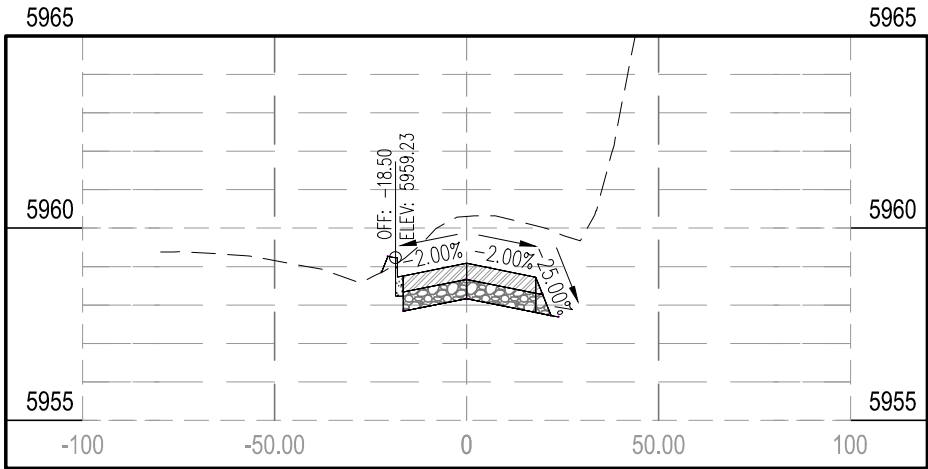


STA 19+21.35

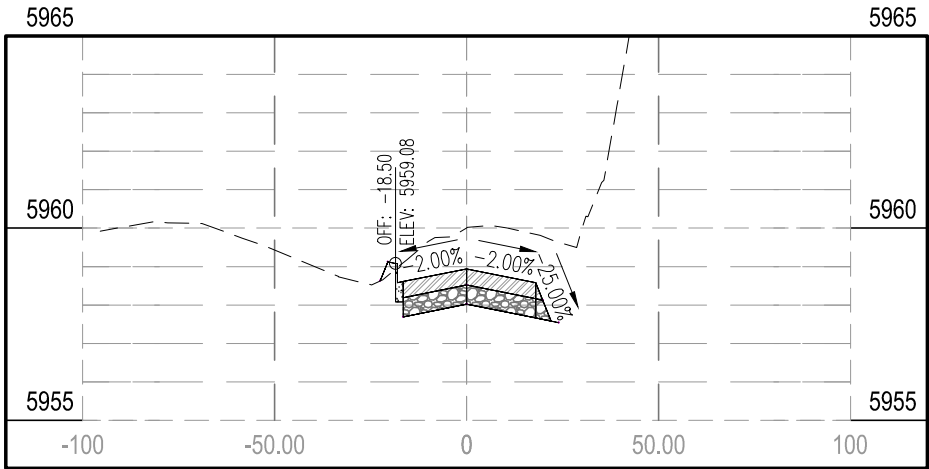

STA 19+50.04

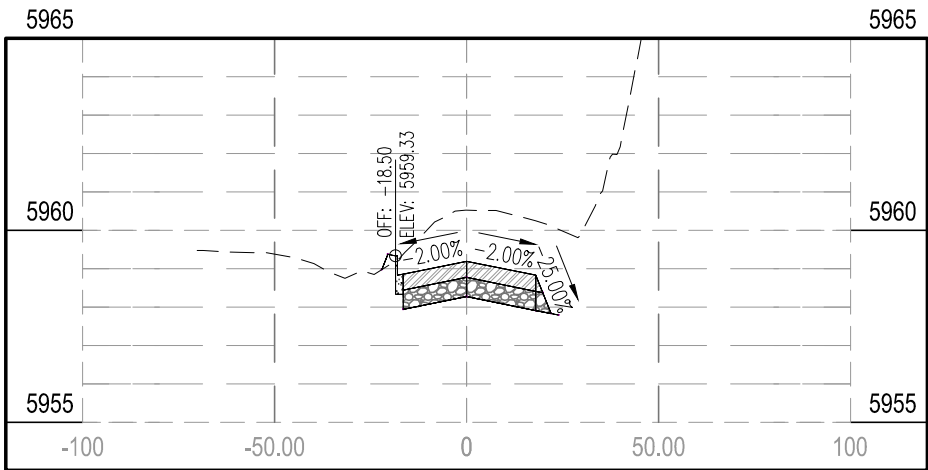

STA 19+00.00

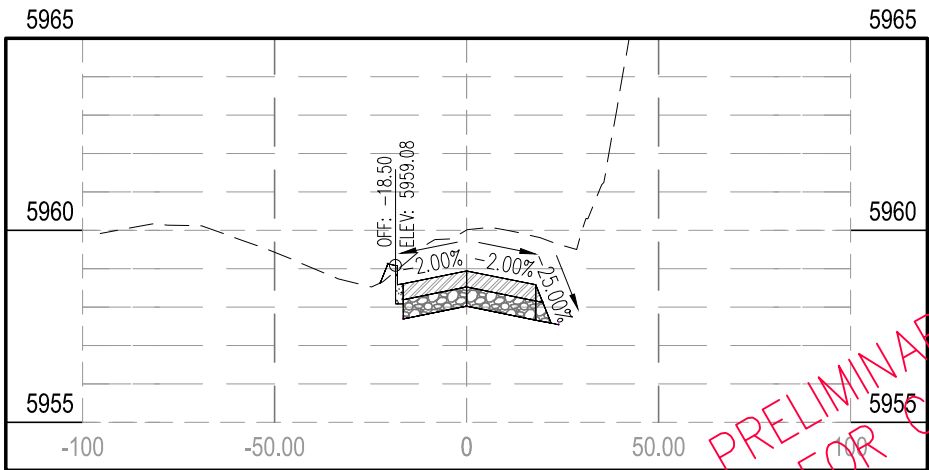

STA 19+50.00

PRELIMINARY PLANS  
NOT FOR CONSTRUCTION

| NO. | REVISION | DATE |
|-----|----------|------|
|     |          |      |
|     |          |      |
|     |          |      |
|     |          |      |

PREPARED FOR:  
MPO  
2101 ONEIL AVE.  
RM 205  
CHEYENNE, WY. 82001


PROJECT: FOX FARM ROAD STREET IMPROVEMENTS  
DRAWING TITLE: BURLINGTON TRAILS RD. CROSS SECTIONS STA. 19+00 - 19+75

avi p.c.  
engineering  
planning  
surveying  
PHONE (307) 637-6017  
1103 OLD TOWN LANE, SUITE 101  
CHEYENNE, WY 82009  
AVI@AVIPC.COM


DATE: 6-20-13  
DRAWN BY: SRL  
DESIGNED BY: TC  
CHECKED BY: TC

JOB NO.: 2-3211-B


XS-33 83  
SHEET NO. OF

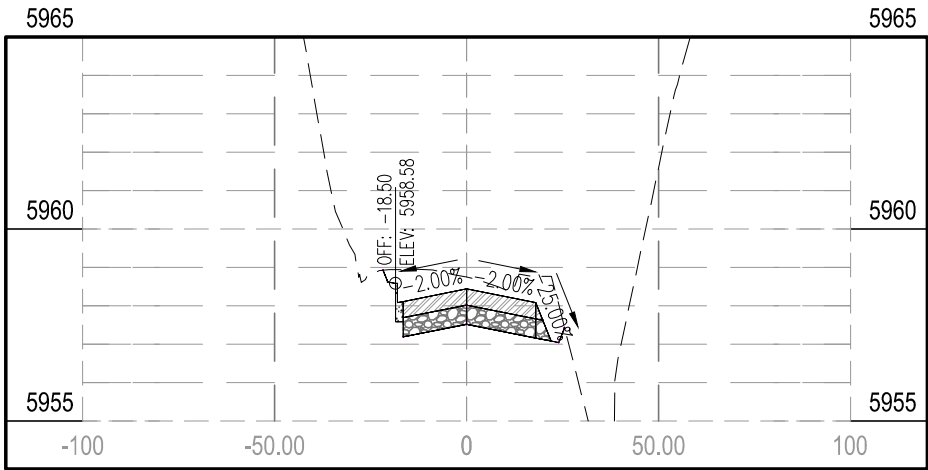


STA 20+50.00

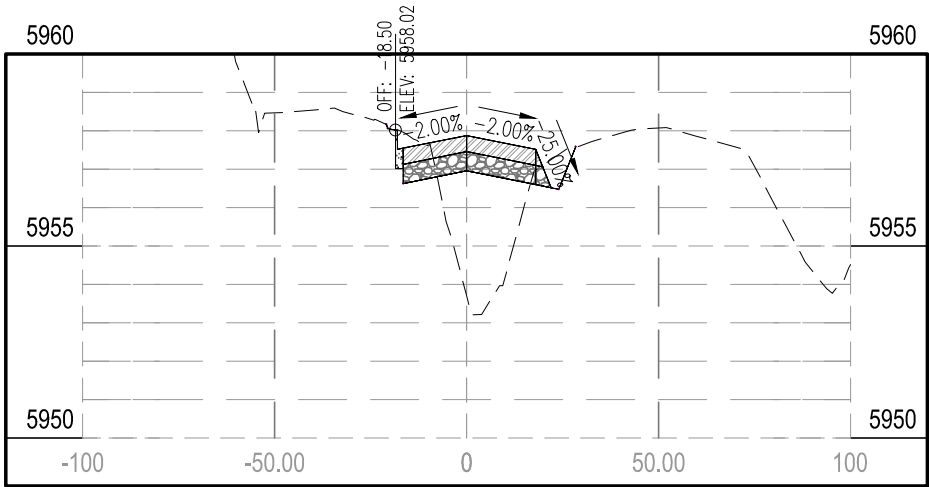


STA 22+00.00

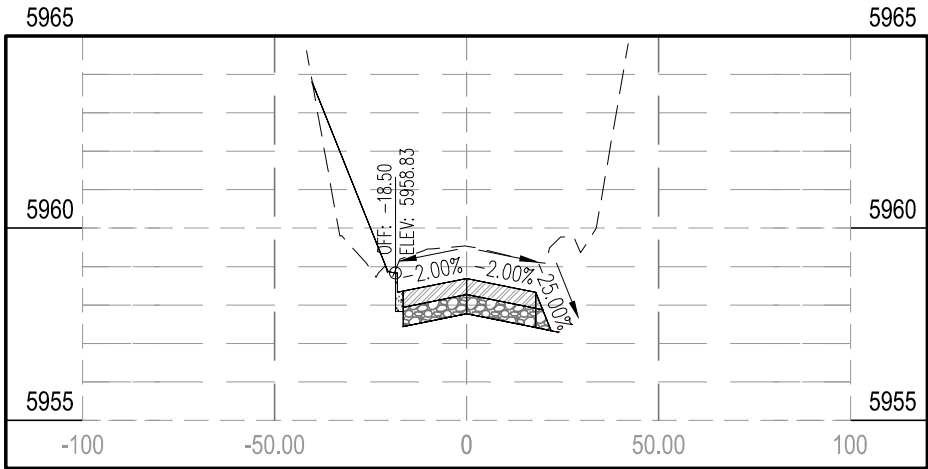


STA 20+00.00

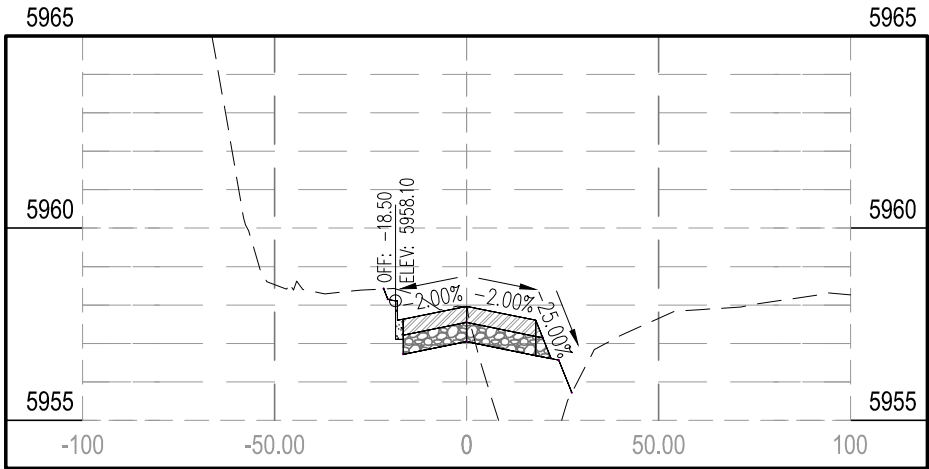

STA 21+50.00

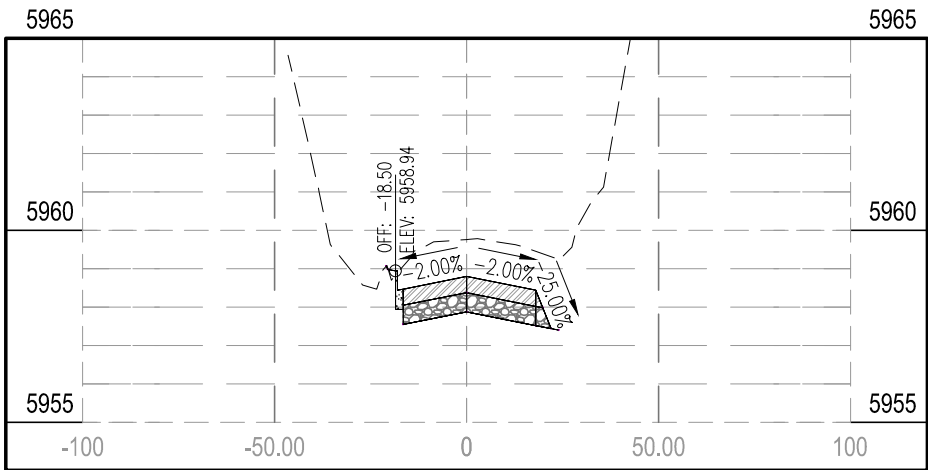

STA 19+78.74

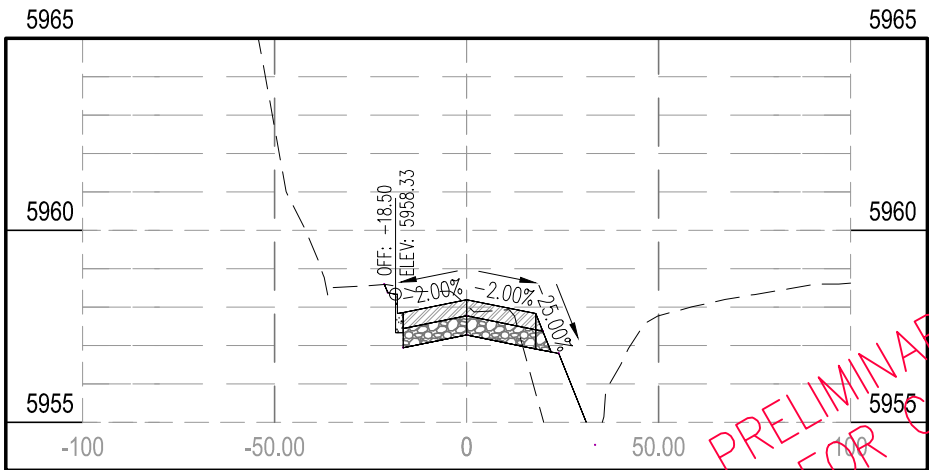

STA 21+00.00

PRELIMINARY PLANS  
NOT FOR CONSTRUCTION

| NO. | REVISION | DATE |
|-----|----------|------|
|     |          |      |
|     |          |      |
|     |          |      |
|     |          |      |

PREPARED FOR:  
MPO  
2101 ONEIL AVE.  
RM 205  
CHEYENNE, WY. 82001

PROJECT: FOX FARM ROAD STREET IMPROVEMENTS


DRAWING TITLE: BURLINGTON TRAILS RD. CROSS SECTIONS STA. 19+78.74 - 22+00

**avi** p.c.  
engineering  
planning  
surveying  
PHONE (307) 637-6017  
1103 OLD TOWN LANE, SUITE 101  
CHEYENNE, WY 82009  
AVI@AVIPC.COM


DATE: 6-20-13  
DRAWN BY: SRL  
DESIGNED BY: TC  
CHECKED BY: TC

JOB NO.: 2-3211-B


XS-34 83  
SHEET NO. OF

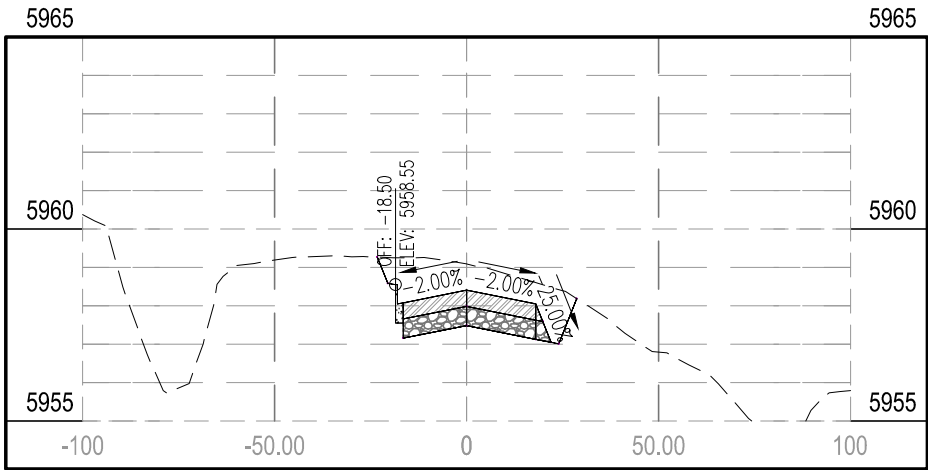


STA 23+50.00

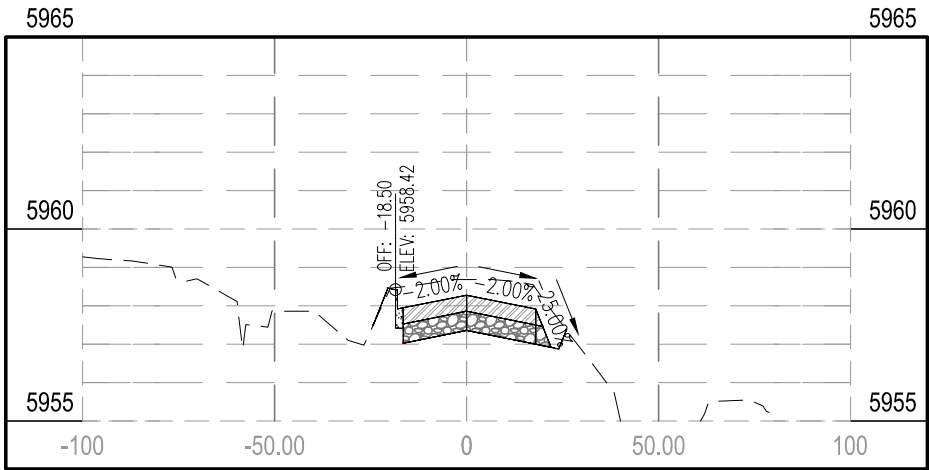


STA 24+25.00

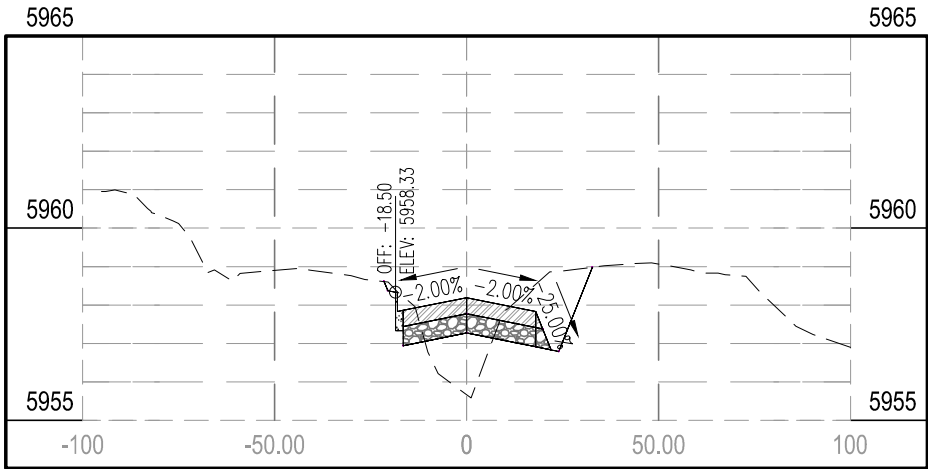


STA 23+00.00

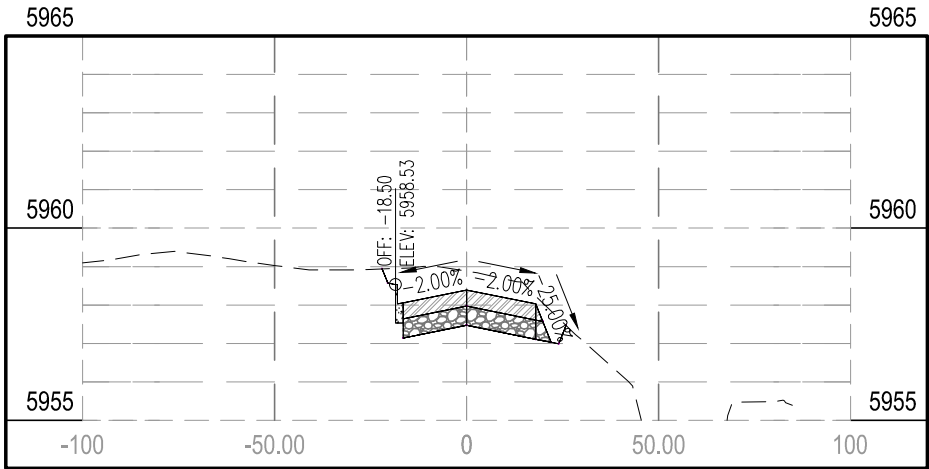

STA 24+00.00

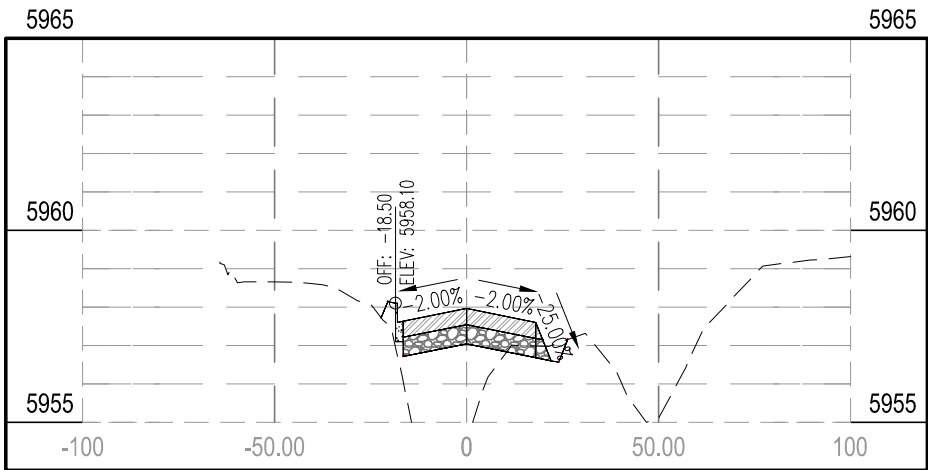

STA 22+50.00

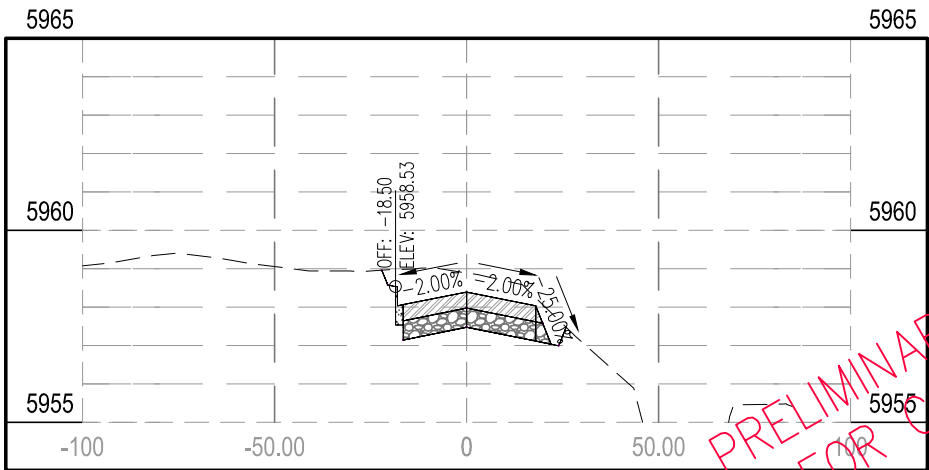

STA 23+98.76

PRELIMINARY PLANS  
NOT FOR CONSTRUCTION

| NO. | REVISION | DATE |
|-----|----------|------|
|     |          |      |
|     |          |      |
|     |          |      |
|     |          |      |

PREPARED FOR:  
MPO  
2101 ONEIL AVE.  
RM 205  
CHEYENNE, WY. 82001


PROJECT: FOX FARM ROAD STREET IMPROVEMENTS  
DRAWING TITLE: BURLINGTON TRAILS RD. CROSS SECTIONS STA. 22+50 - 24+25

avi p.c.  
engineering  
planning  
surveying  
PHONE (307) 637-6017  
1103 OLD TOWN LANE, SUITE 101  
CHEYENNE, WY 82009  
AVI@AVIPC.COM


DATE: 6-20-13  
DRAWN BY: SRL  
DESIGNED BY: TC  
CHECKED BY: TC

JOB NO.: 2-3211-B


XS-35 83  
SHEET NO. OF

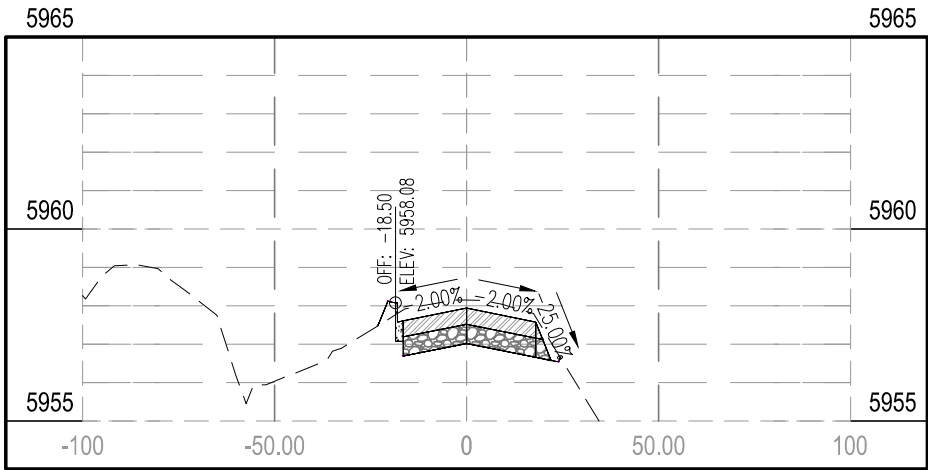


STA 24+67.10

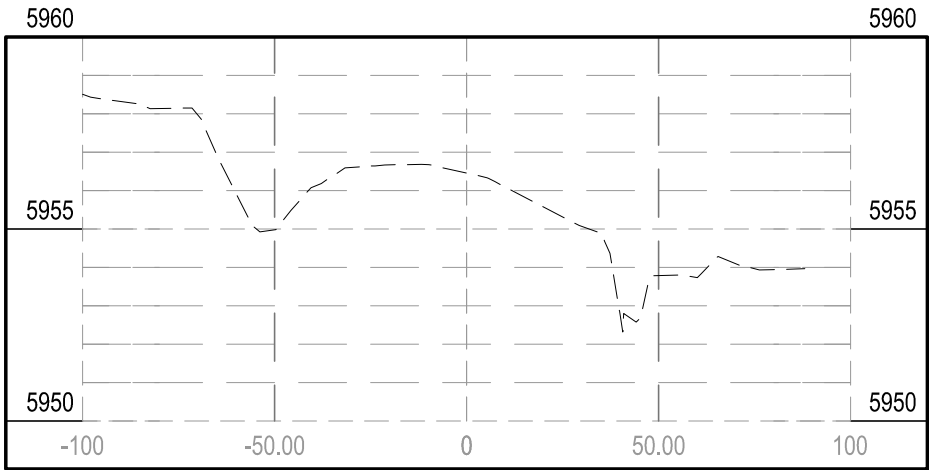


STA 26+00.00

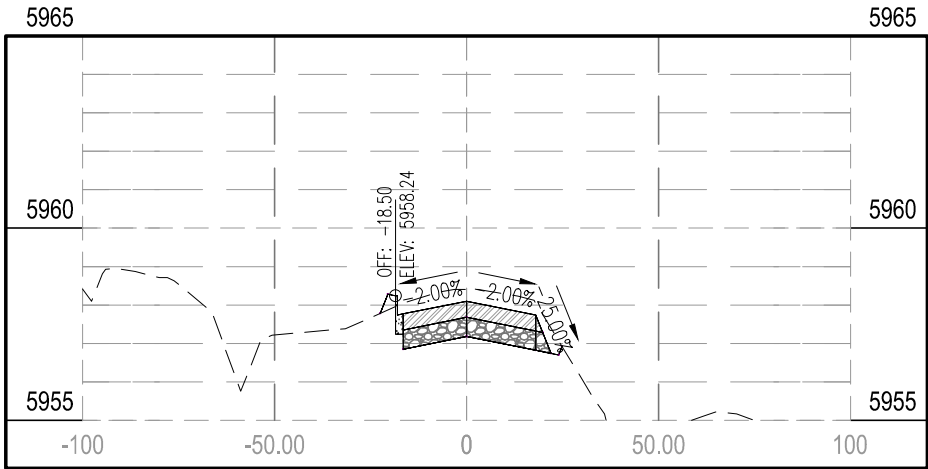


STA 24+50.00

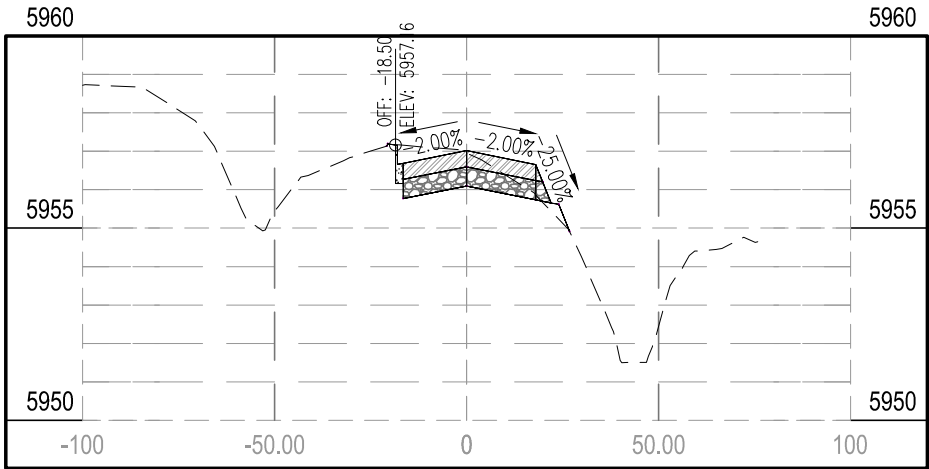

STA 25+50.00

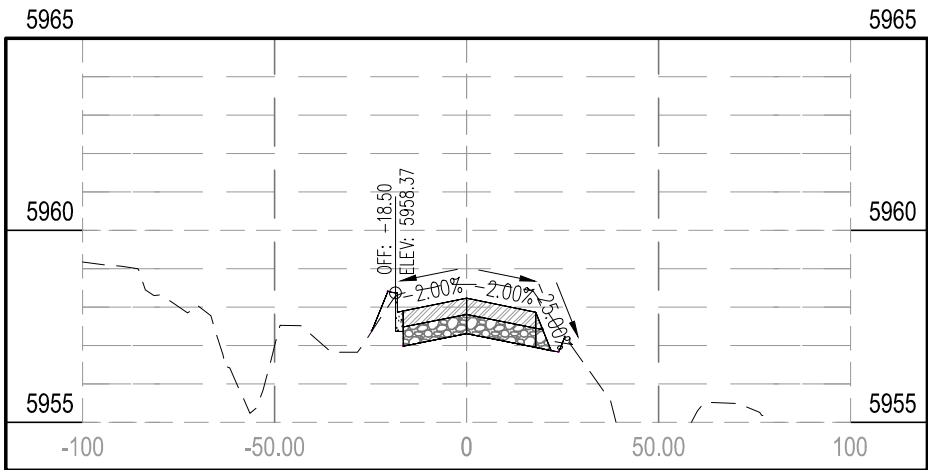

STA 24+32.93

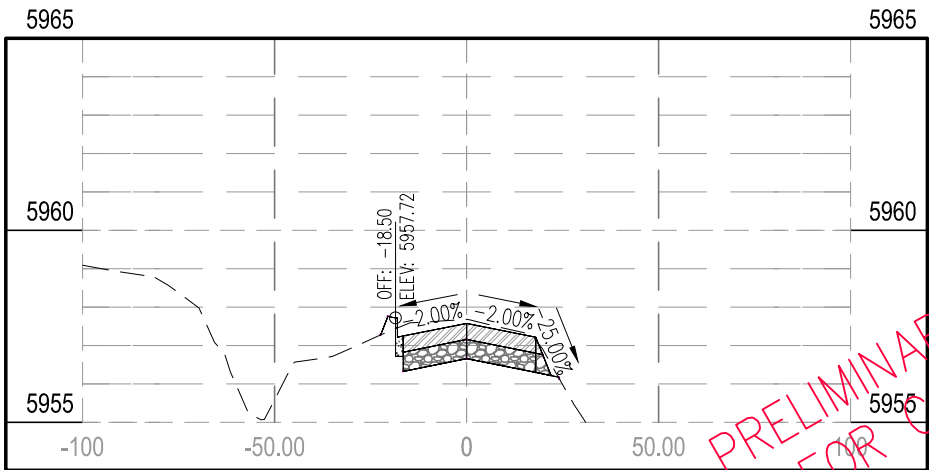

STA 25+00.00

PRELIMINARY PLANS  
NOT FOR CONSTRUCTION

| NO. | REVISION | DATE |
|-----|----------|------|
|     |          |      |
|     |          |      |
|     |          |      |
|     |          |      |
|     |          |      |

PREPARED FOR:  
MPO  
2101 O'NEIL AVE.  
RM 205  
CHEYENNE, WY. 82001

PROJECT: FOX FARM ROAD STREET IMPROVEMENTS  
DRAWING TITLE: BURLINGTON TRAILS RD. CROSS SECTIONS STA. 24+32.93 - 26+00


avi p.c.  
engineering  
planning  
surveying  
PHONE (307) 637-6017  
1103 OLD TOWN LANE, SUITE 101  
CHEYENNE, WY 82009  
AVI@AVIPC.COM

DATE: 6-20-13  
DRAWN BY: SRL  
DESIGNED BY: TC  
CHECKED BY: TC


JOB NO.: 2-3211-B

SHEET NO. XS-37 OF 83


H:\3211\design\3211B FOX FARM STREET IMP.dwg Aug 30, 2013 4:29pm jwilson

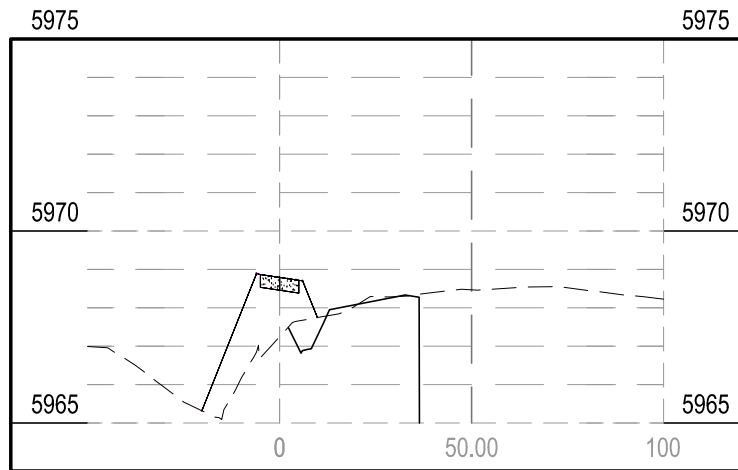


STA 0+50.00

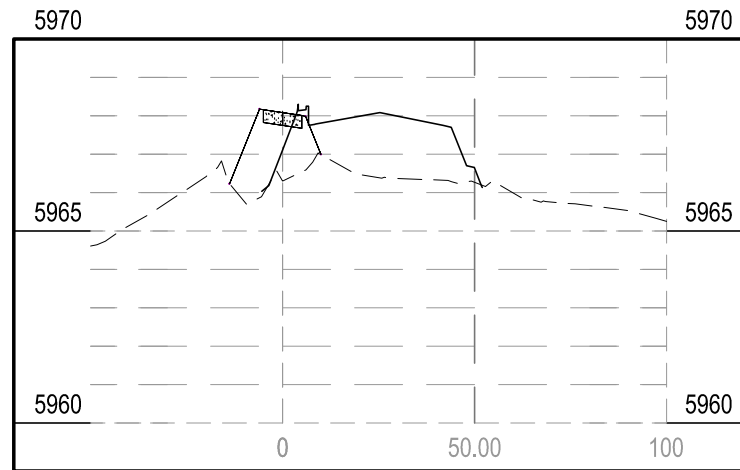


STA 0+75.00

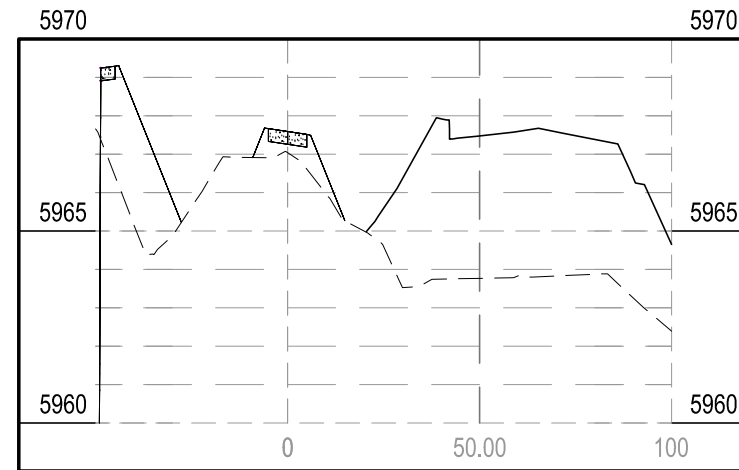


STA 1+00.00

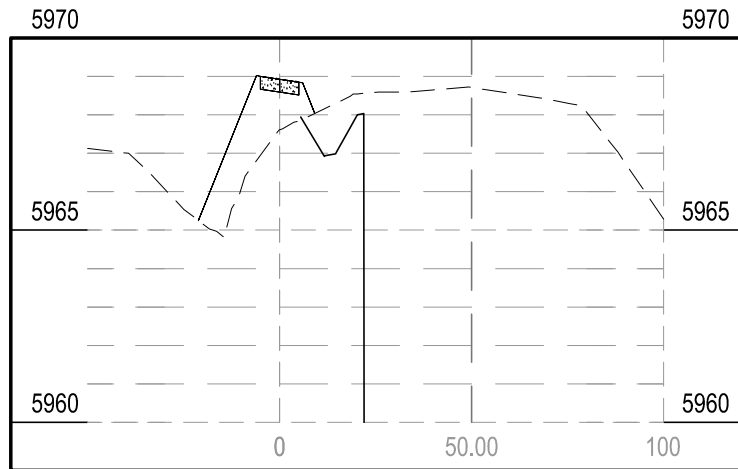


STA 0+44.65

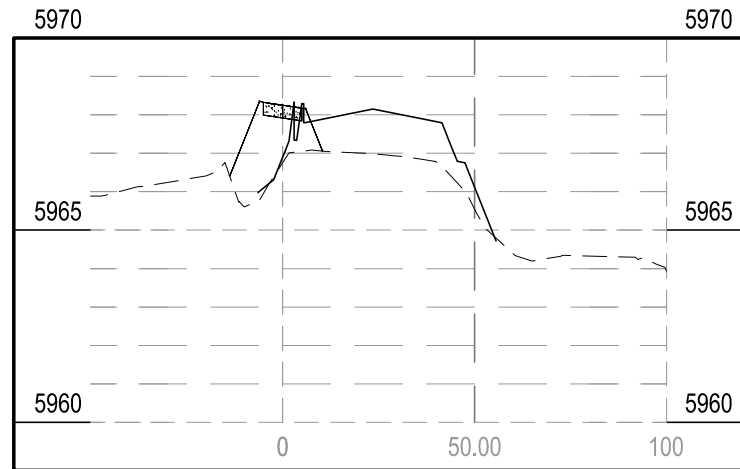


STA 0+68.92

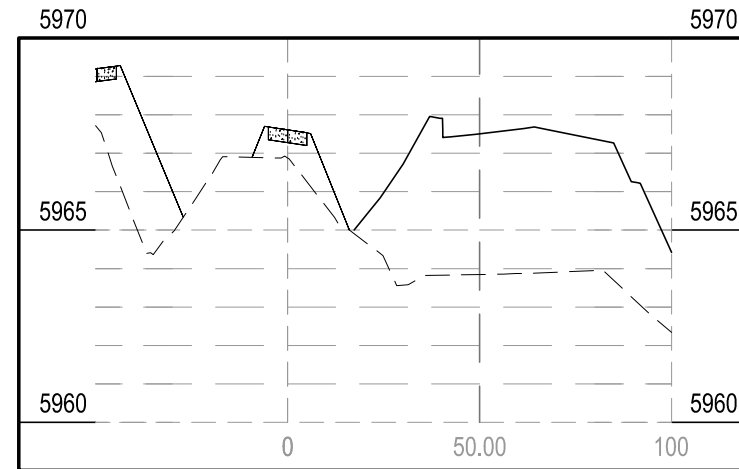


STA 0+98.13

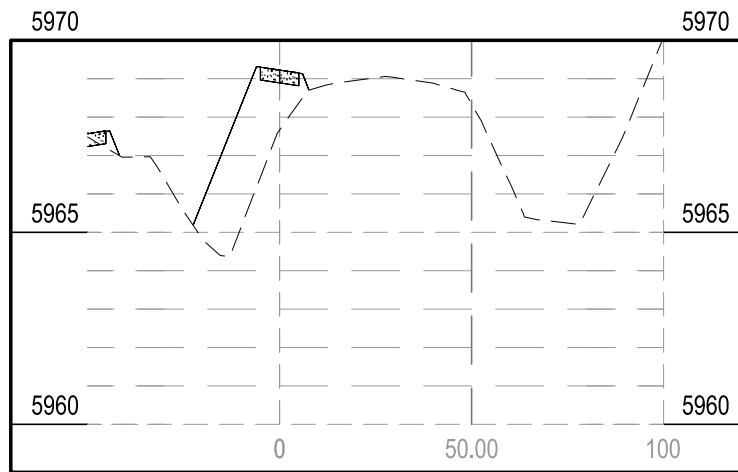

STA 0+25.00

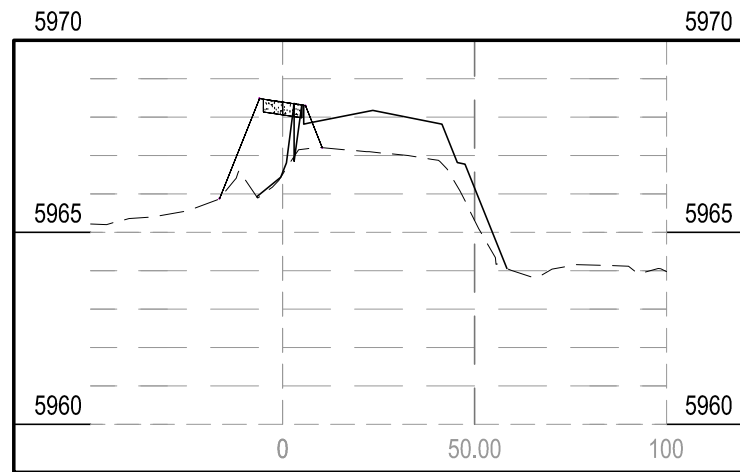

STA 0+64.29

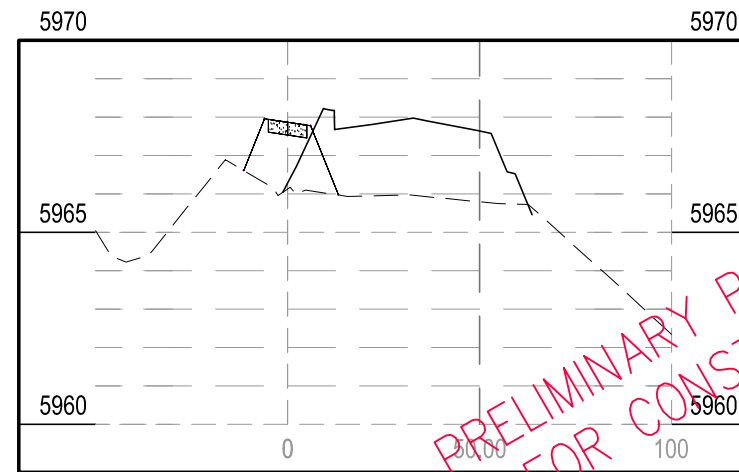

STA 0+83.52

PRELIMINARY PLANS  
NOT FOR CONSTRUCTION

| NO. | REVISION | DATE |
|-----|----------|------|
|     |          |      |
|     |          |      |
|     |          |      |
|     |          |      |

PREPARED FOR:  
MPO  
2101 ONEIL AVE.  
RM 205  
CHEYENNE, WY. 82001

PROJECT: FOX FARM ROAD STREET  
IMPROVEMENTS  
DRAWING TITLE:  
BURLINGTON TRAILS SIDEWALK  
CROSS SECTIONS STA. 0+25 - 1+00


avi p.c.  
engineering  
planning  
surveying  
PHONE (307) 637-6017  
1103 OLD TOWN LANE, SUITE 101  
CHEYENNE, WY 82009  
AVI@AVIPC.COM

DATE:  
6-20-13  
DRAWN BY:  
SRL  
DESIGNED BY:  
TC  
CHECKED BY:  
TC


JOB NO.:  
2-3211-B

XS-38 83  
SHEET NO. OF


H:\3211\design\3211B FOX FARM STREET IMP.dwg Aug 30, 2013 4:30pm jwilson

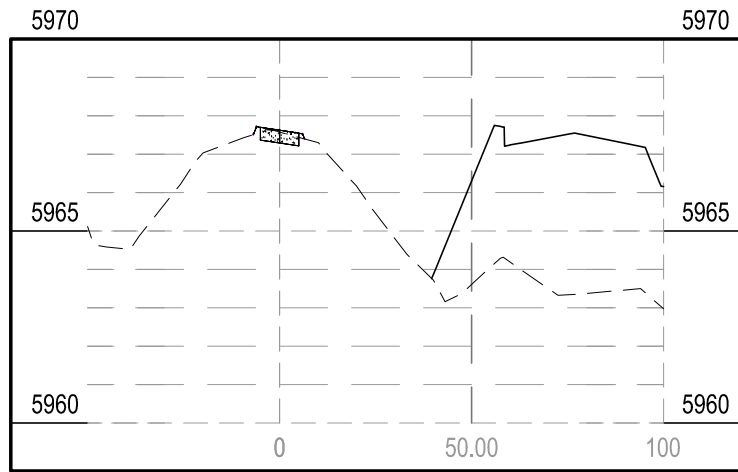


STA 1+38.09

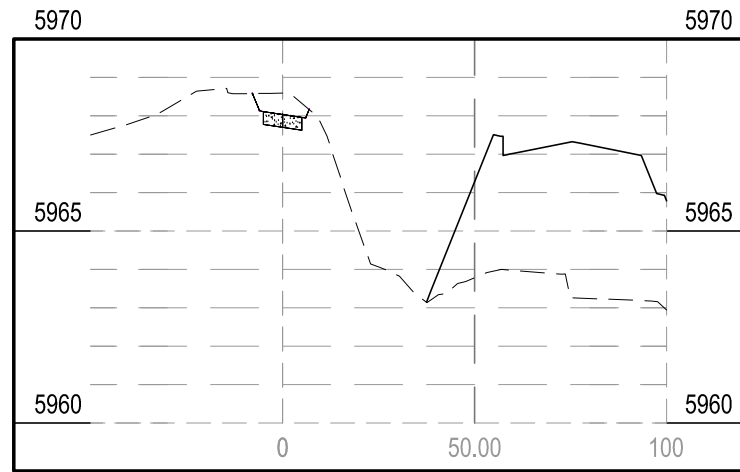


STA 2+00.00

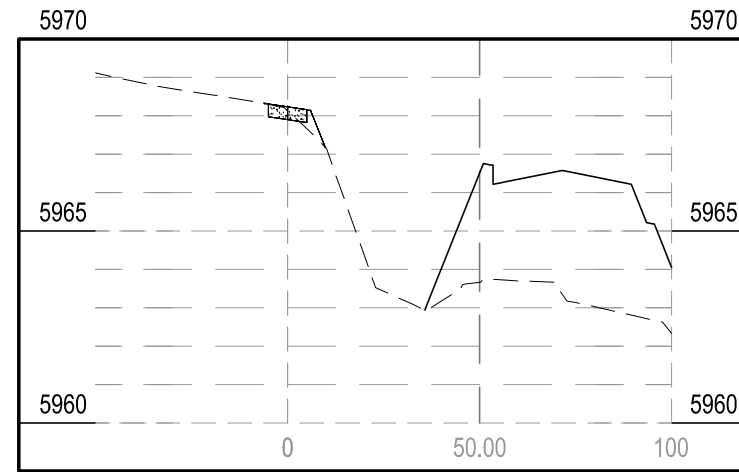


STA 3+50.00

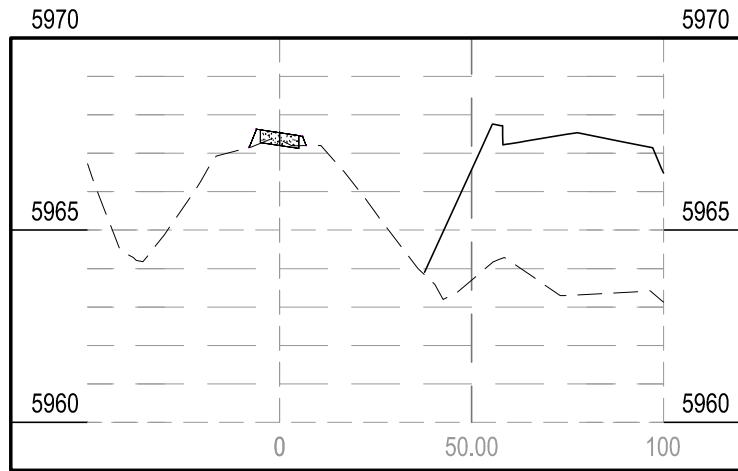


STA 1+25.00

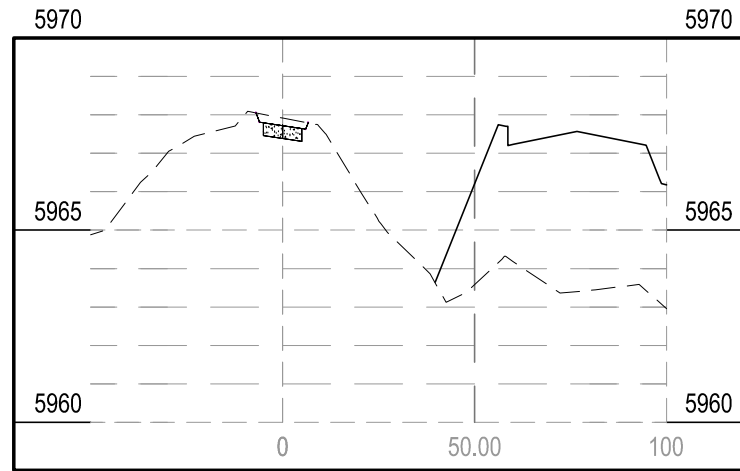


STA 1+52.59

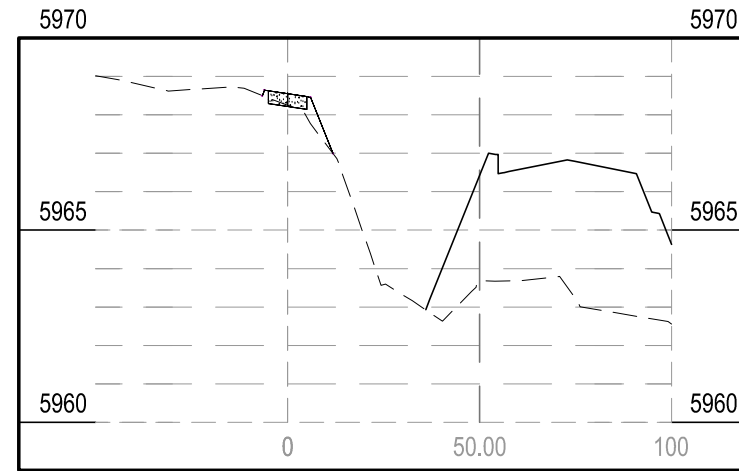


STA 3+00.00

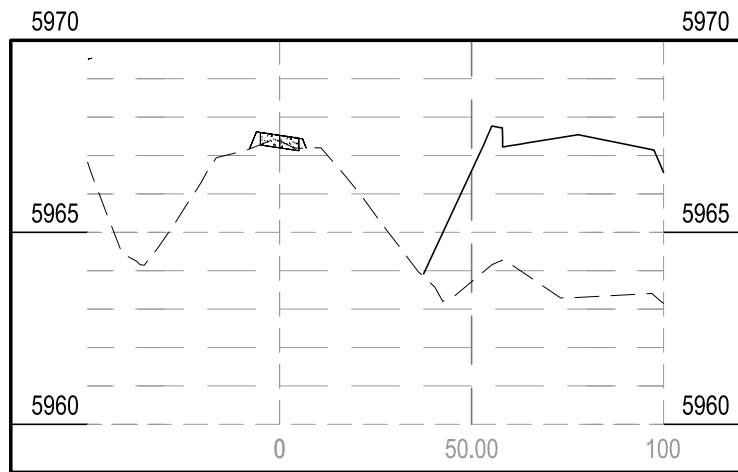

STA 1+23.59

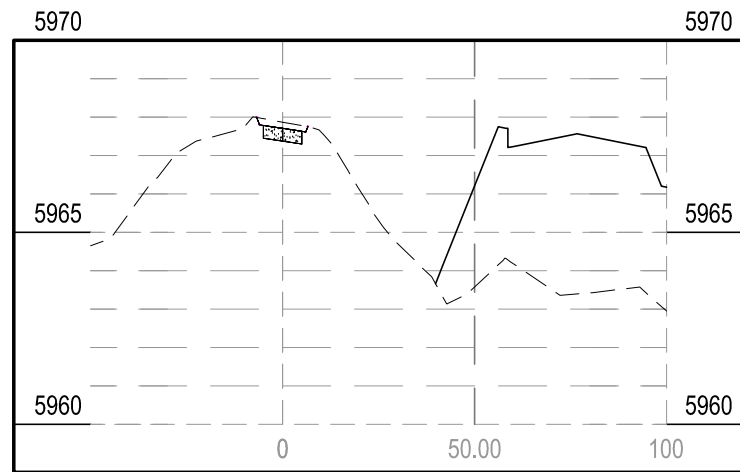

STA 1+50.00

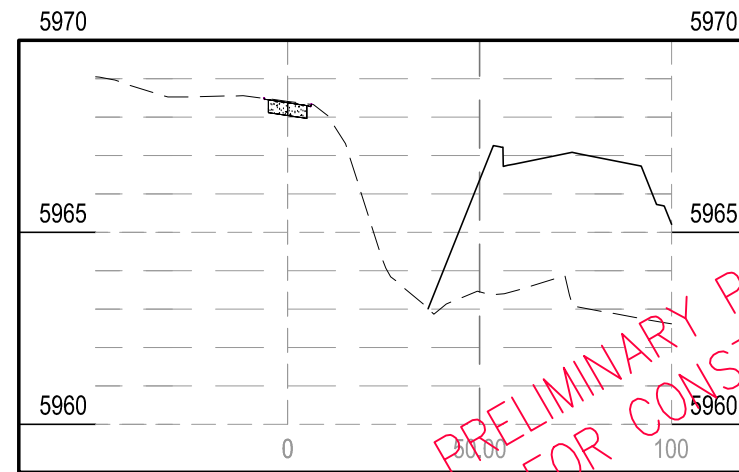

STA 2+50.00

PRELIMINARY PLANS  
NOT FOR CONSTRUCTION

| NO. | REVISION | DATE |
|-----|----------|------|
|     |          |      |
|     |          |      |
|     |          |      |
|     |          |      |
|     |          |      |

PREPARED FOR:  
MPO  
2101 ONEIL AVE.  
RM 205  
CHEYENNE, WY. 82001

PROJECT: FOX FARM ROAD STREET IMPROVEMENTS  
DRAWING TITLE: BURLINGTON TRAILS SIDEWALK CROSS SECTIONS STA. 1+23.59 - 3+50


avi p.c.  
engineering  
planning  
surveying  
PHONE (307) 637-6017  
1103 OLD TOWN LANE, SUITE 101  
CHEYENNE, WY 82009  
AVI@AVIPC.COM

DATE: 6-20-13  
DRAWN BY: SRL  
DESIGNED BY: TC  
CHECKED BY: TC


JOB NO.: 2-3211-B

XS-39 83  
SHEET NO. OF


H:\3211\design\3211B FOX FARM STREET IMP.dwg Aug 30, 2013 4:30pm jwilson

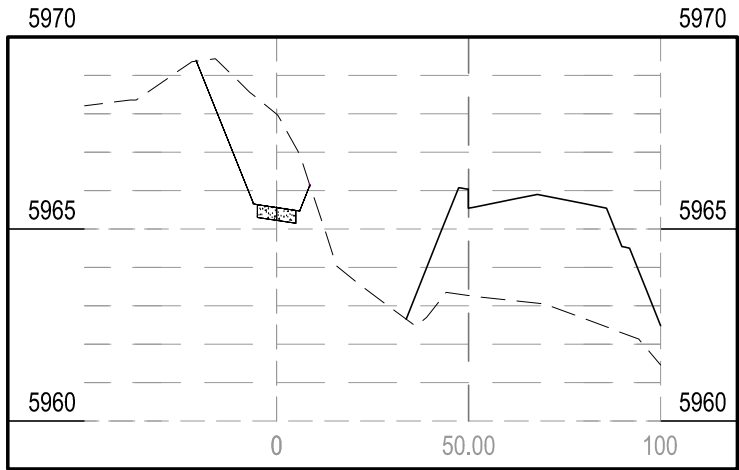


STA 4+85.65

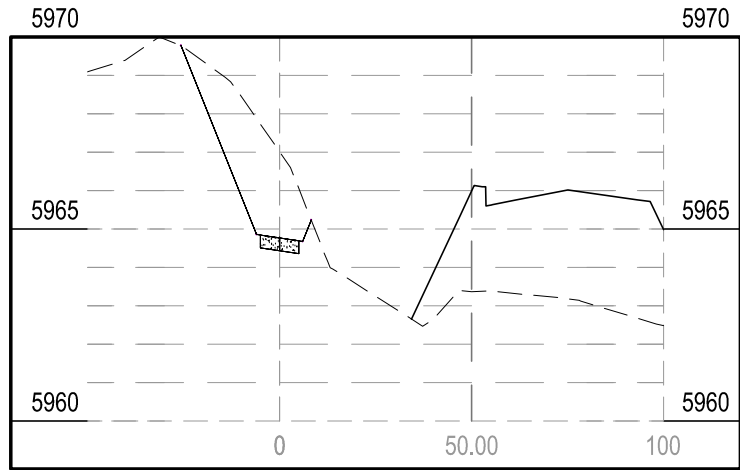


STA 5+02.00

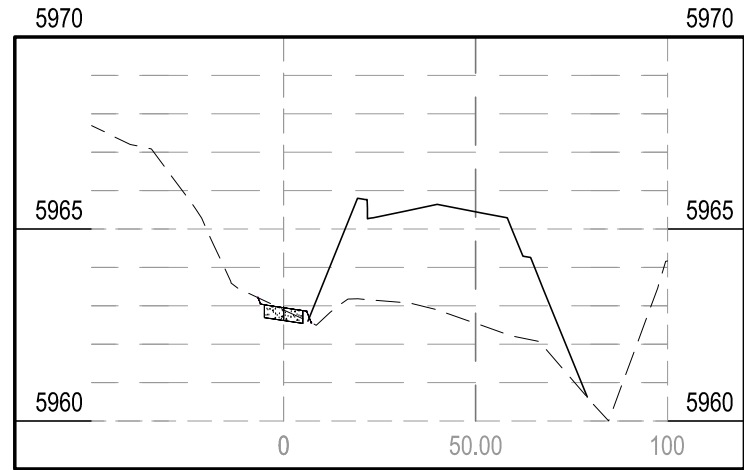


STA 5+50.00

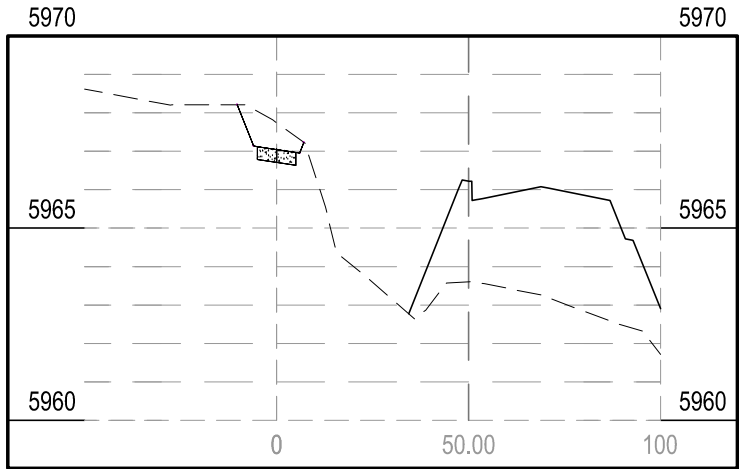


STA 4+50.00

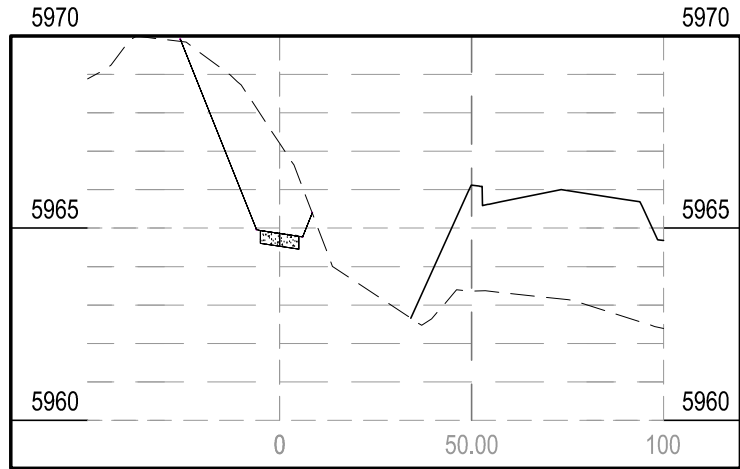


STA 5+00.00

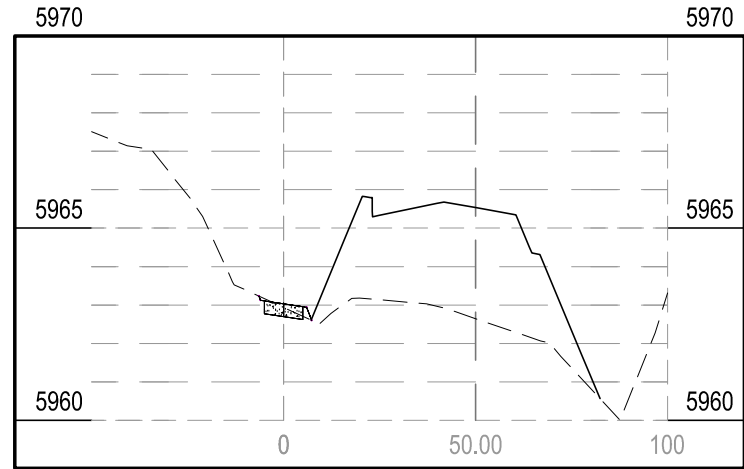


STA 5+46.58

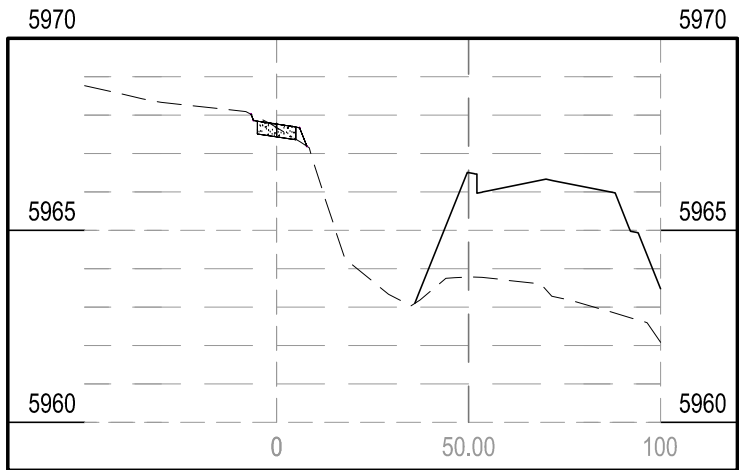

STA 4+00.00

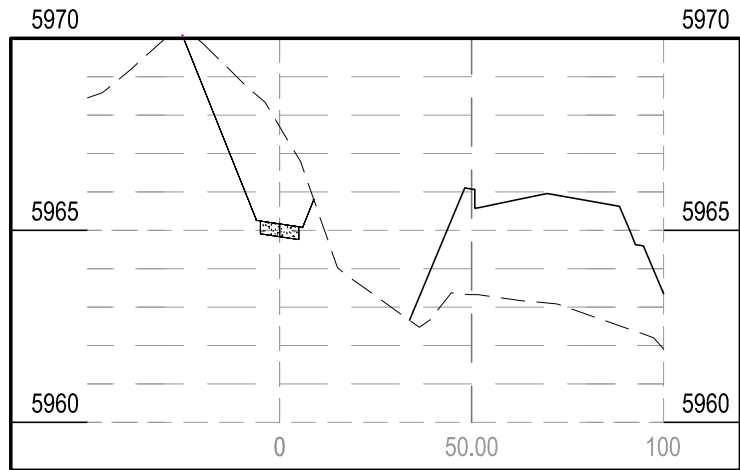

STA 4+93.83

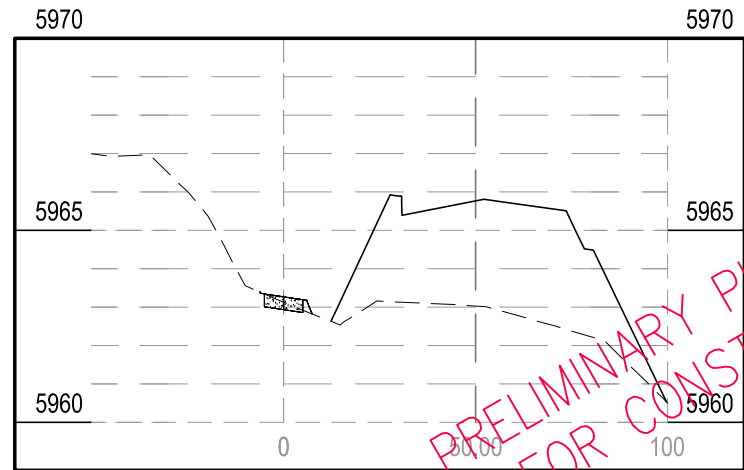

STA 5+37.66

PRELIMINARY PLANS  
NOT FOR CONSTRUCTION

| NO. | REVISION | DATE |
|-----|----------|------|
|     |          |      |
|     |          |      |
|     |          |      |
|     |          |      |

PREPARED FOR:  
MPO  
2101 ONEIL AVE.  
RM 205  
CHEYENNE, WY. 82001

PROJECT: FOX FARM ROAD STREET IMPROVEMENTS  
DRAWING TITLE: BURLINGTON TRAILS SIDEWALK CROSS SECTIONS STA. 4+00 - 5+50


avi p.c.  
engineering  
planning  
surveying  
PHONE (307) 637-6017  
1103 OLD TOWN LANE, SUITE 101  
CHEYENNE, WY 82009  
AVI@AVIPC.COM

DATE: 6-20-13  
DRAWN BY: SRL  
DESIGNED BY: TC  
CHECKED BY: TC


JOB NO.: 2-3211-B

XS-40 83  
SHEET NO. OF


H:\3211\design\3211B FOX FARM STREET IMP.dwg Aug 30, 2013 4:30pm jwilson

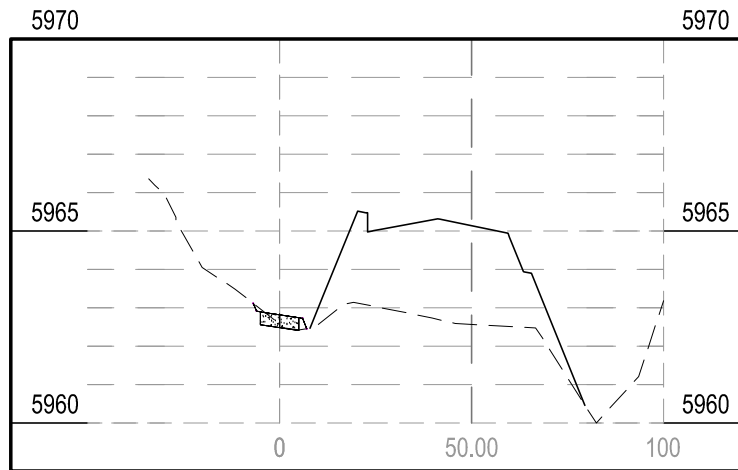


STA 6+00.00

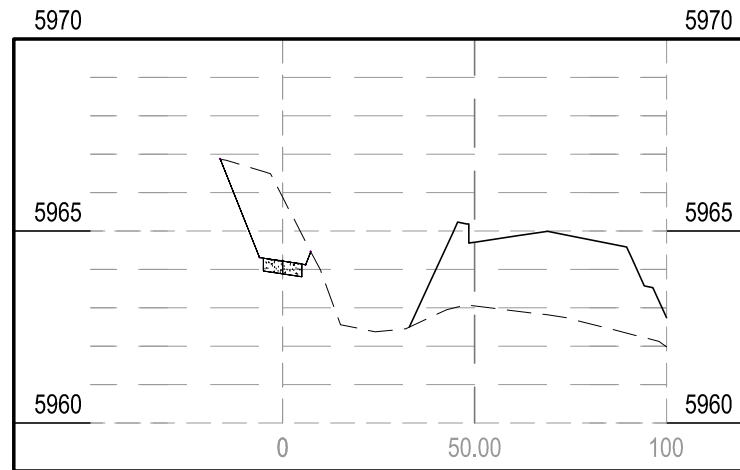


STA 6+44.28

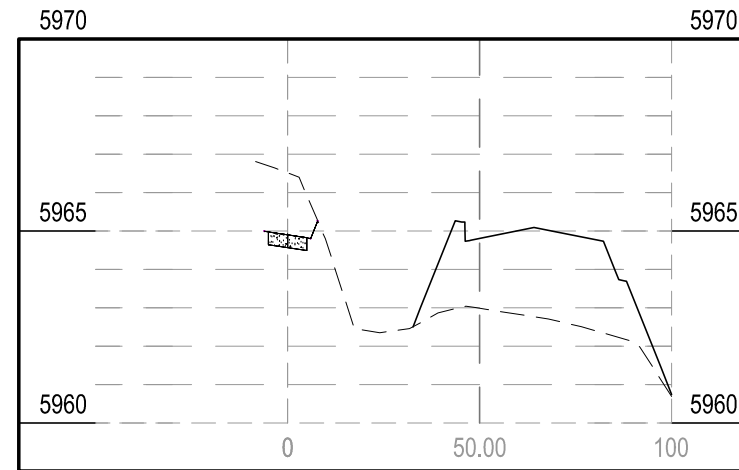


STA 6+60.06

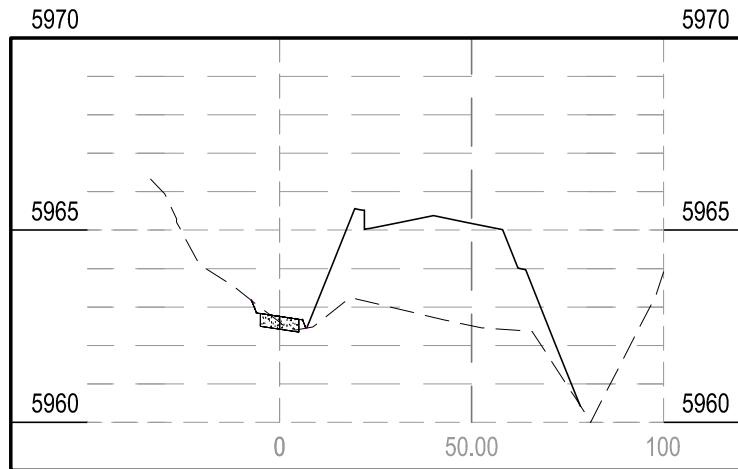


STA 5+95.35

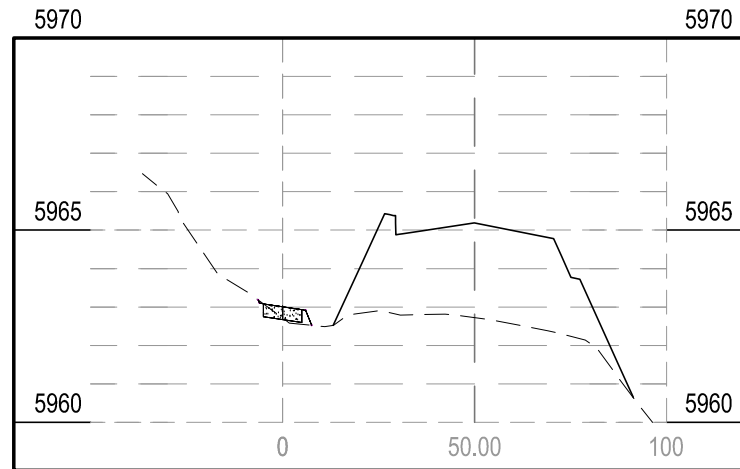


STA 6+09.75

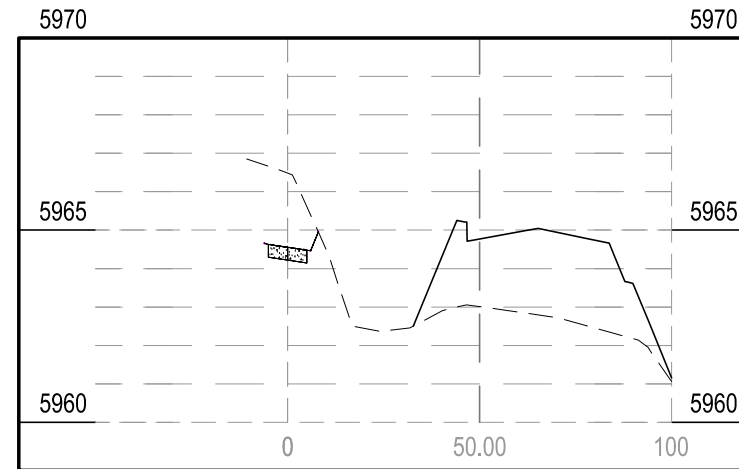


STA 6+52.17

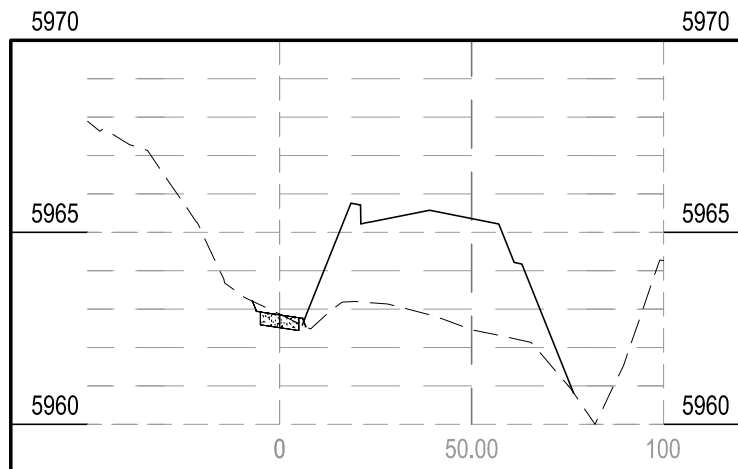

STA 5+55.51

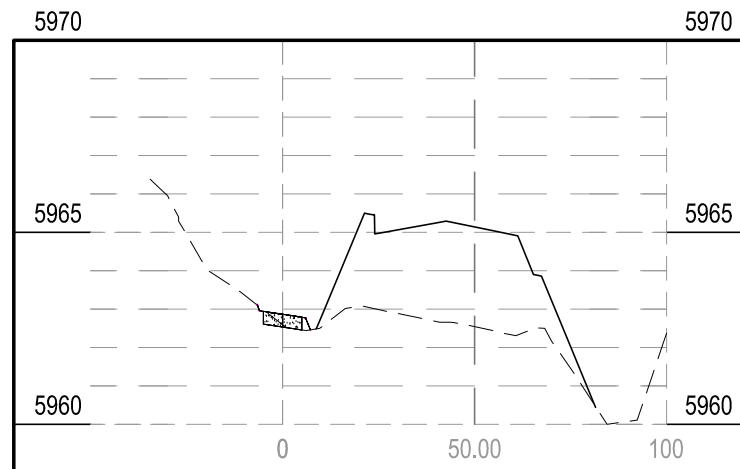

STA 6+02.55

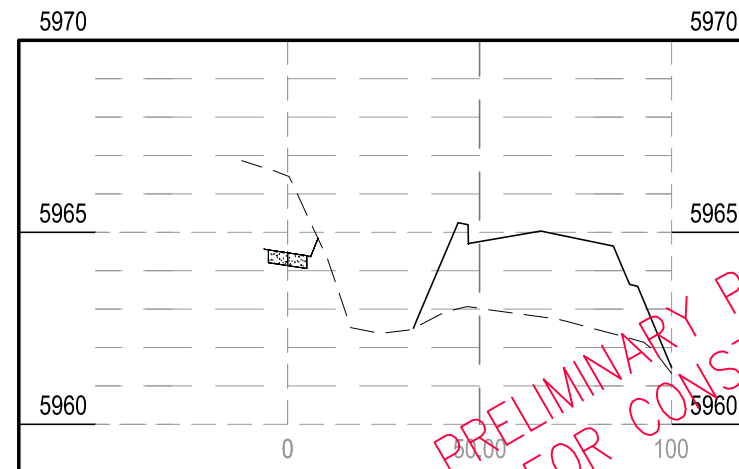

STA 6+50.00

PRELIMINARY PLANS  
NOT FOR CONSTRUCTION

| NO. | REVISION | DATE |
|-----|----------|------|
|     |          |      |
|     |          |      |
|     |          |      |
|     |          |      |

PREPARED FOR:  
MPO  
2101 ONEIL AVE.  
RM 205  
CHEYENNE, WY. 82001

PROJECT: FOX FARM ROAD STREET IMPROVEMENTS  
DRAWING TITLE: BURLINGTON TRAILS SIDEWALK CROSS SECTIONS STA. 5+55.51 - 6+60.06


avi p.c.  
engineering  
planning  
surveying  
PHONE (307) 637-6017  
1103 OLD TOWN LANE, SUITE 101  
CHEYENNE, WY 82009  
AVI@AVIPC.COM

DATE: 6-20-13  
DRAWN BY: SRL  
DESIGNED BY: TC  
CHECKED BY: TC


JOB NO.: 2-3211-B

XS-41 83  
SHEET NO. OF


H:\3211\design\3211B FOX FARM STREET IMP.dwg Aug 30, 2013 4:30pm jwilson

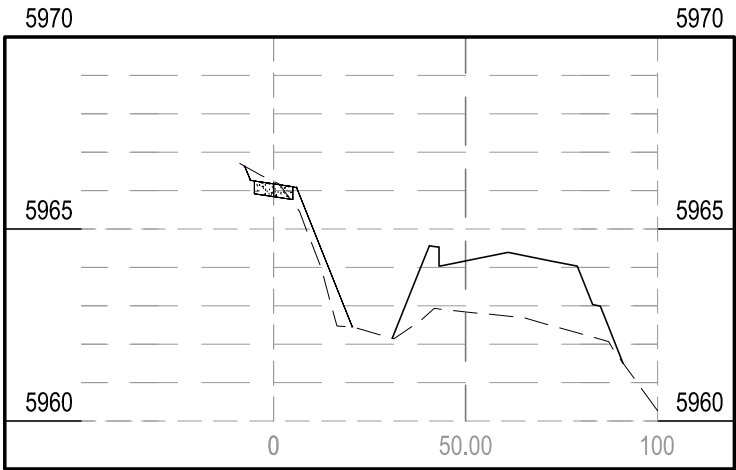


STA 8+00.00

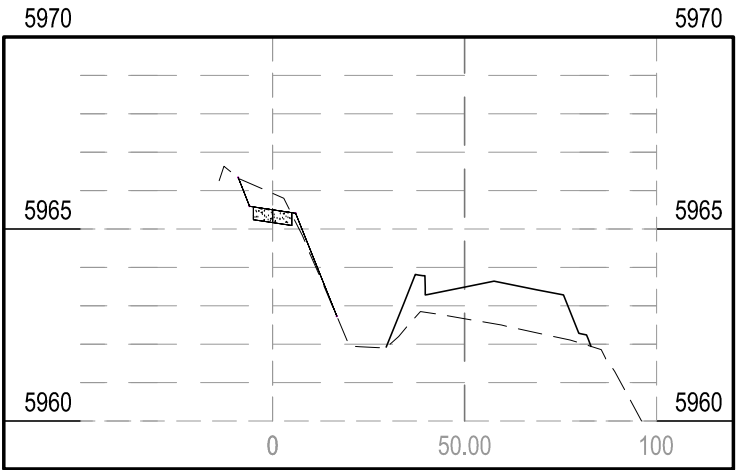


STA 9+50.00

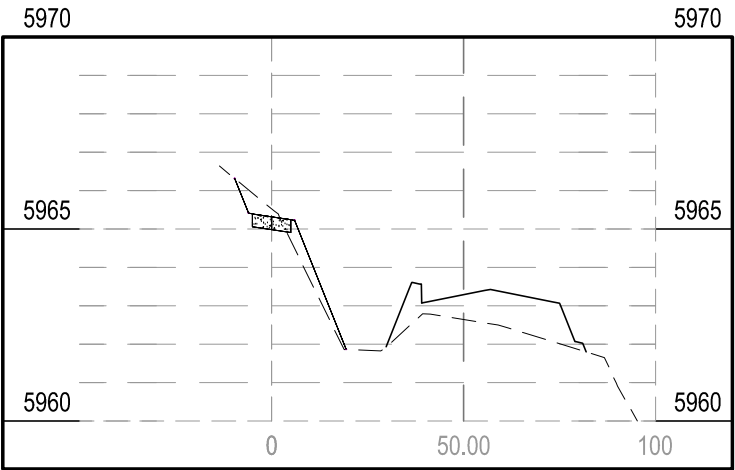


STA 9+90.76

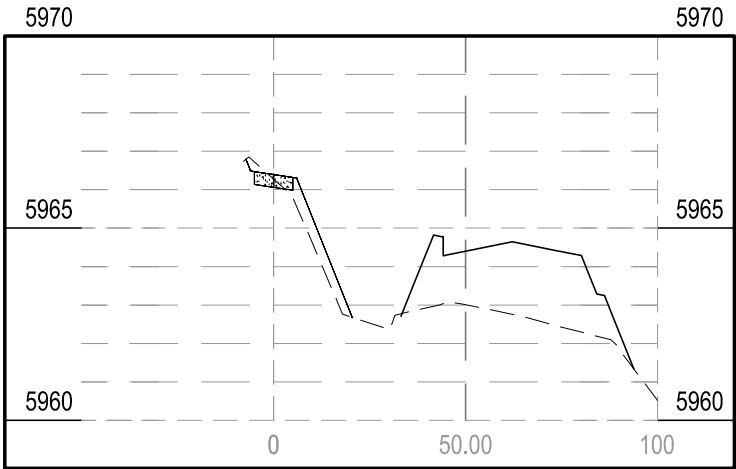


STA 7+50.00

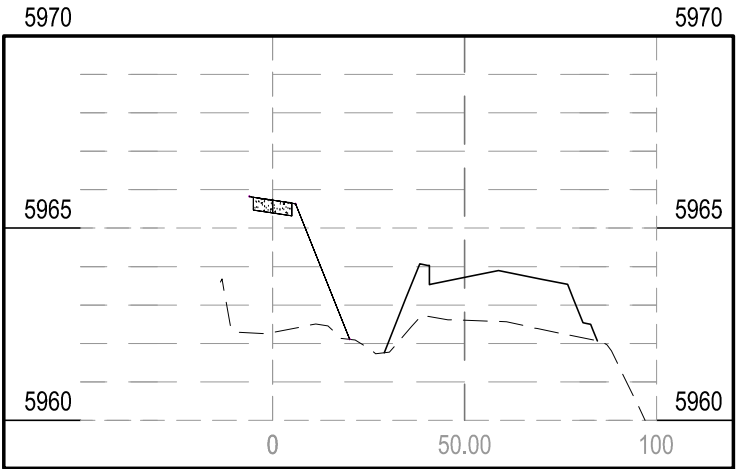


STA 9+00.00

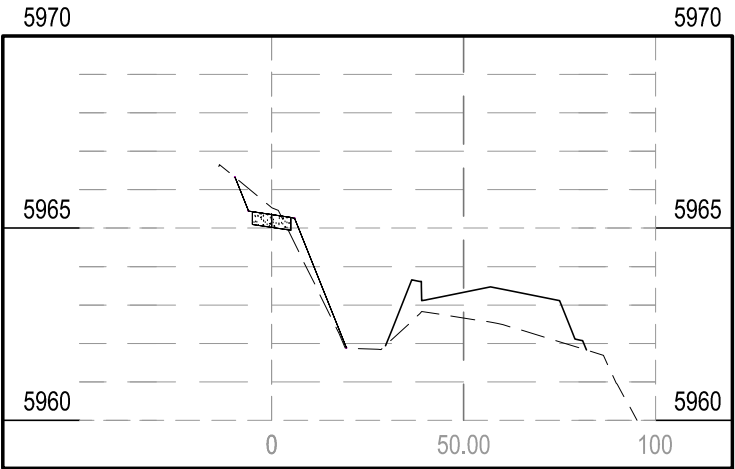


STA 9+83.46

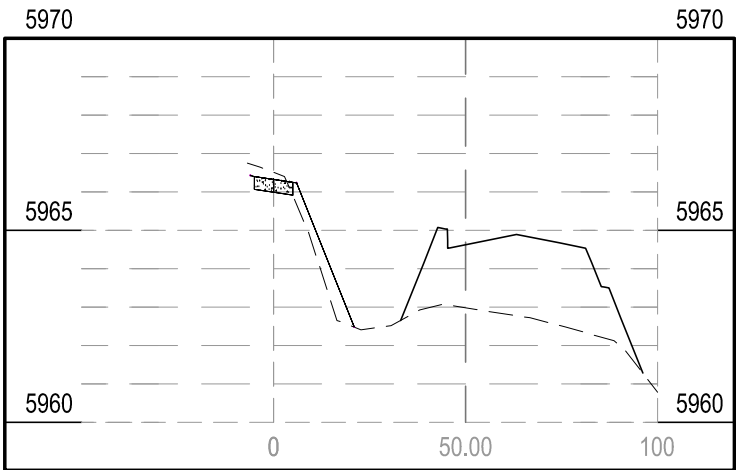

STA 7+00.00

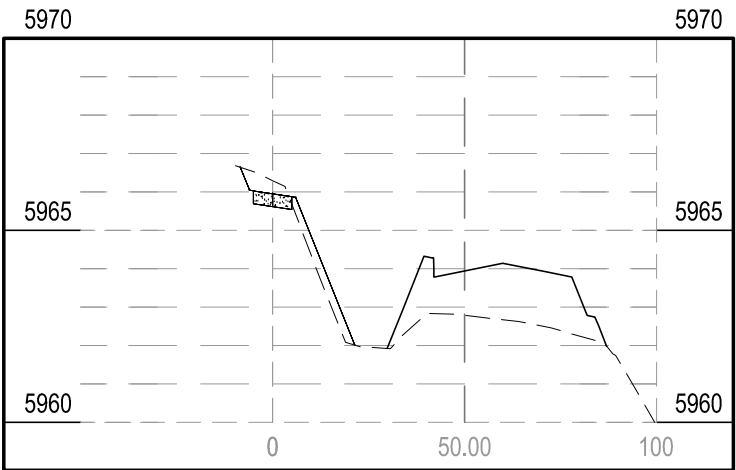

STA 8+50.00

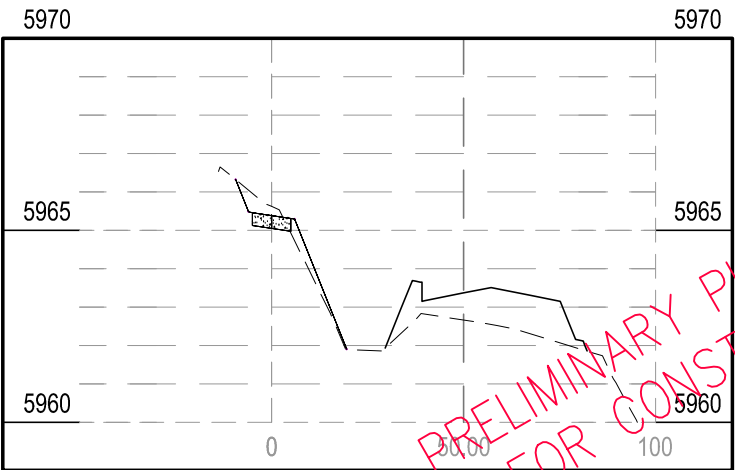

STA 9+76.16

PRELIMINARY PLANS  
NOT FOR CONSTRUCTION

| NO. | REVISION | DATE |
|-----|----------|------|
|     |          |      |
|     |          |      |
|     |          |      |
|     |          |      |

PREPARED FOR:  
MPO  
2101 ONEIL AVE.  
RM 205  
CHEYENNE, WY. 82001

PROJECT: FOX FARM ROAD STREET IMPROVEMENTS  
DRAWING TITLE: BURLINGTON TRAILS SIDEWALK CROSS SECTIONS STA. 7+00 - 9+90.76


avi p.c.  
engineering  
planning  
surveying  
PHONE (307) 637-6017  
1103 OLD TOWN LANE, SUITE 101  
CHEYENNE, WY 82009  
AVI@AVIPC.COM

DATE: 6-20-13  
DRAWN BY: SRL  
DESIGNED BY: TC  
CHECKED BY: TC


JOB NO.: 2-3211-B

XS-42 83  
SHEET NO. OF


H:\3211\design\3211B FOX FARM STREET IMP.dwg Aug 30, 2013 4:31pm jwilson

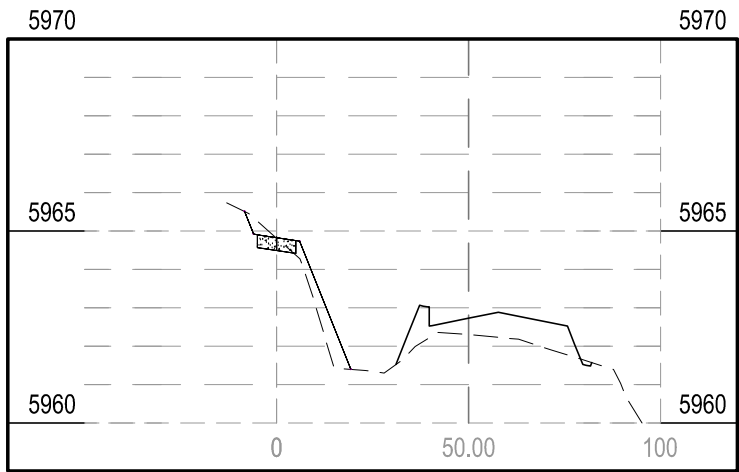


STA 11+00.00

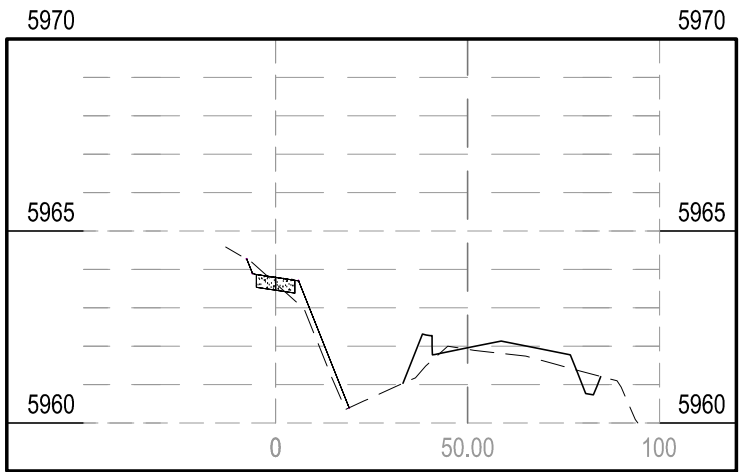


STA 12+50.00

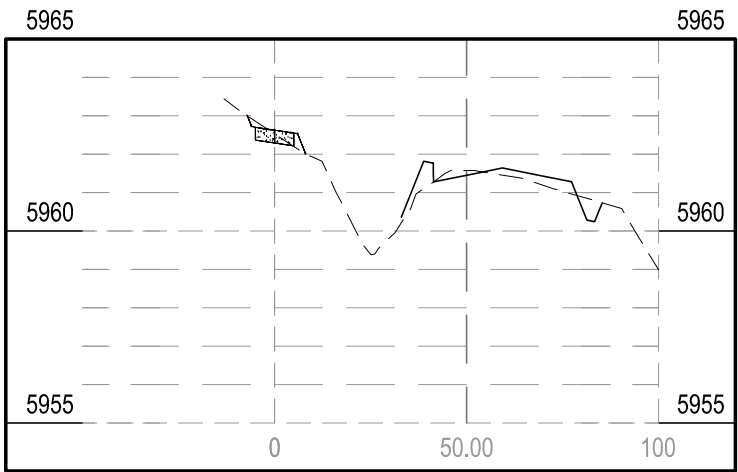


STA 13+50.00

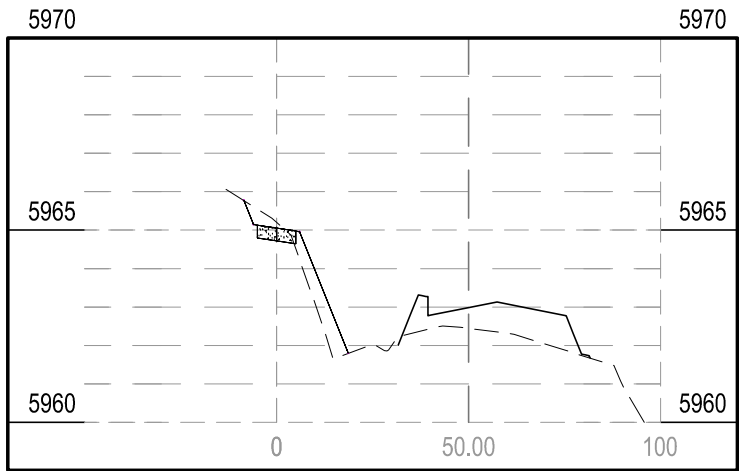


STA 10+50.00

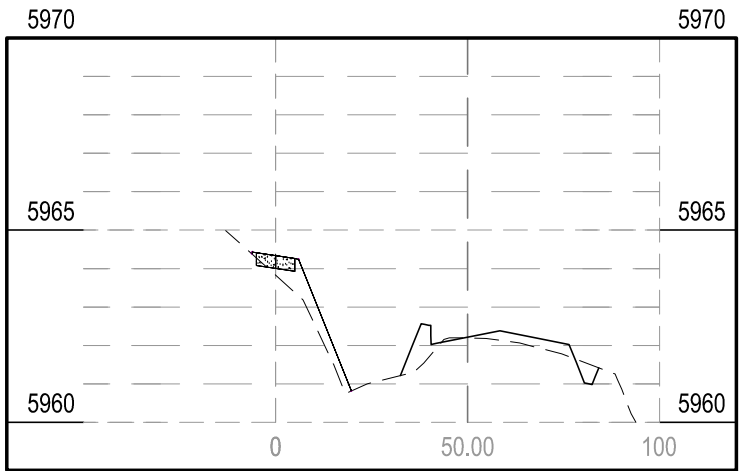


STA 12+00.00

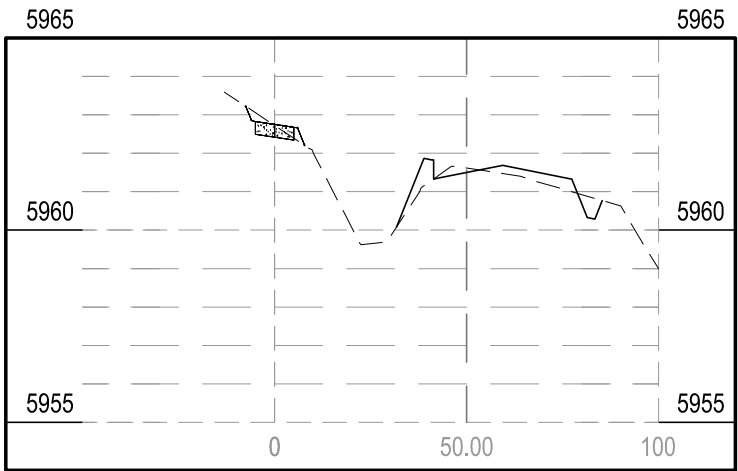


STA 13+39.01

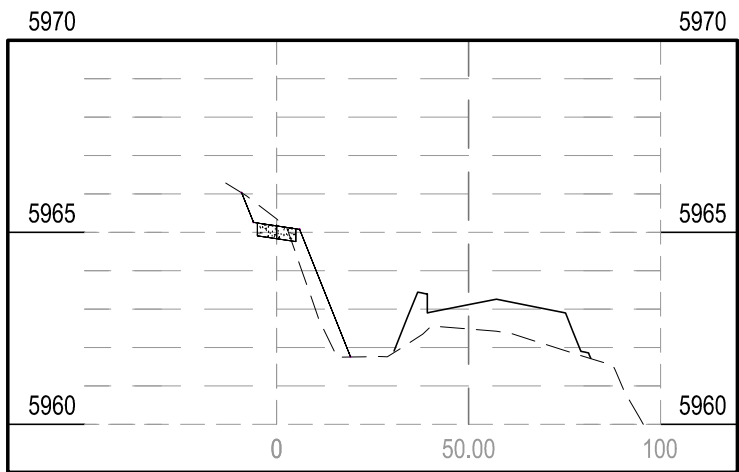

STA 10+25.00

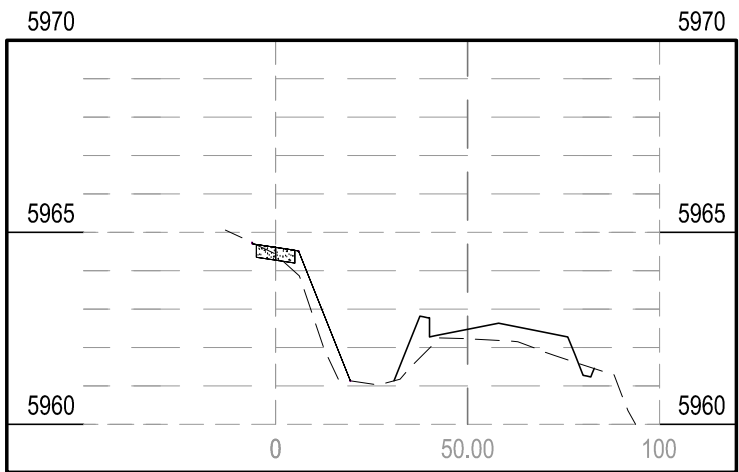

STA 11+50.00

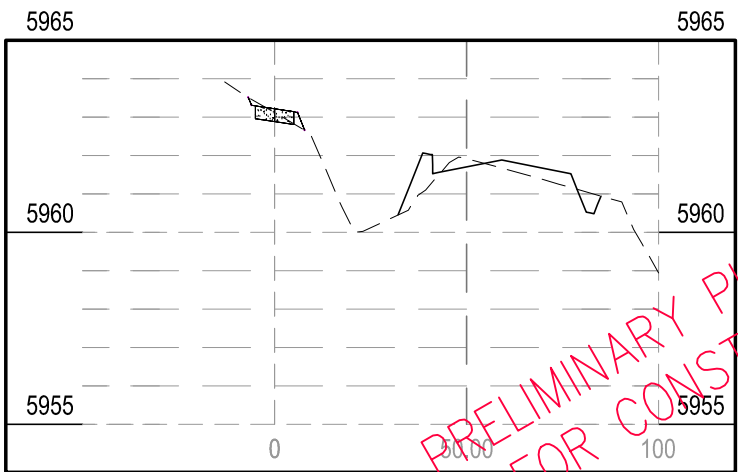

STA 13+00.00

PRELIMINARY PLANS  
NOT FOR CONSTRUCTION

| NO. | REVISION | DATE |
|-----|----------|------|
|     |          |      |
|     |          |      |
|     |          |      |
|     |          |      |
|     |          |      |

PREPARED FOR:  
MPO  
2101 ONEIL AVE.  
RM 205  
CHEYENNE, WY. 82001

PROJECT: FOX FARM ROAD STREET IMPROVEMENTS  
DRAWING TITLE: BURLINGTON TRAILS SIDEWALK CROSS SECTIONS STA. 10+25 - 13+50


avi p.c.  
engineering  
planning  
surveying  
PHONE (307) 637-6017  
1103 OLD TOWN LANE, SUITE 101  
CHEYENNE, WY 82009  
AVI@AVIPC.COM

DATE: 6-20-13  
DRAWN BY: SRL  
DESIGNED BY: TC  
CHECKED BY: TC


JOB NO.: 2-3211-B

XS-43 83  
SHEET NO. OF


H:\3211\design\3211B FOX FARM STREET IMP.dwg Aug 30, 2013 4:31pm jwilson

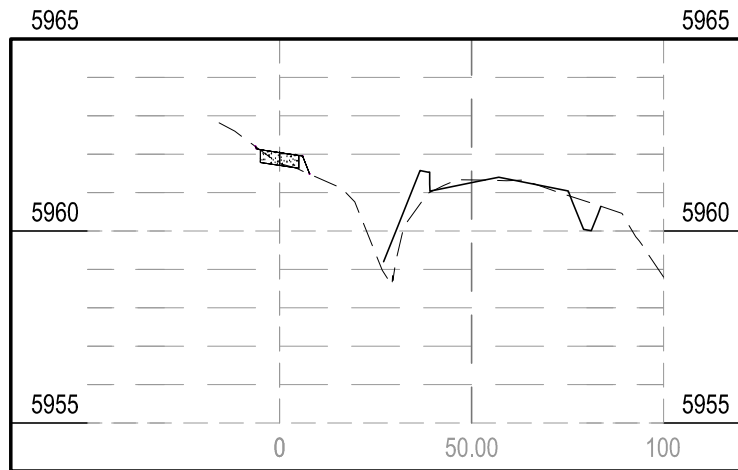


STA 14+00.00

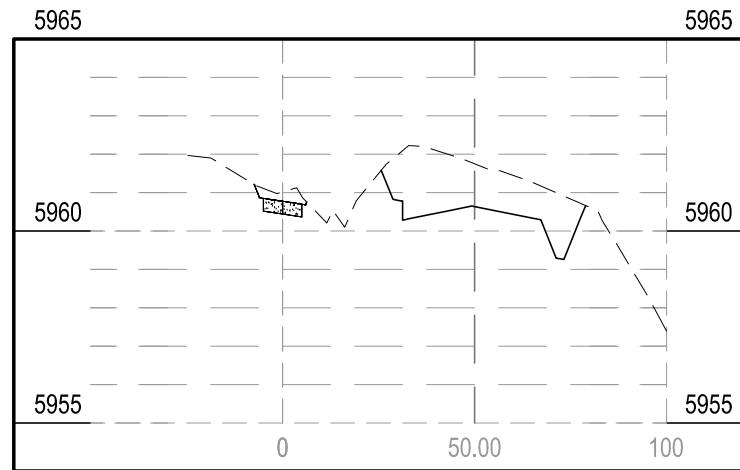


STA 15+50.00

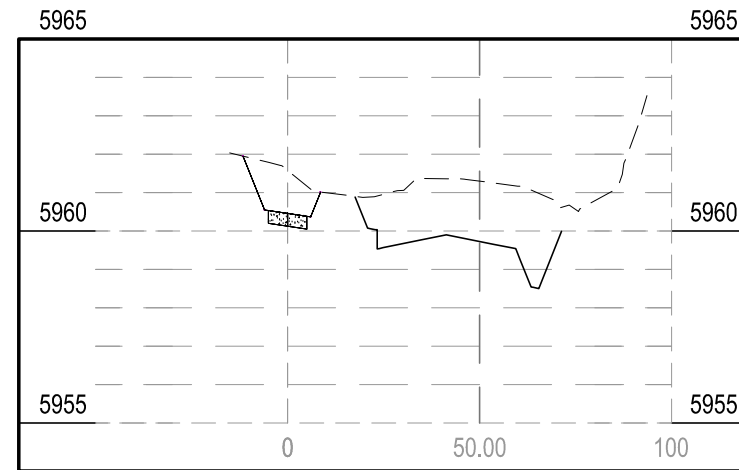


STA 17+00.00

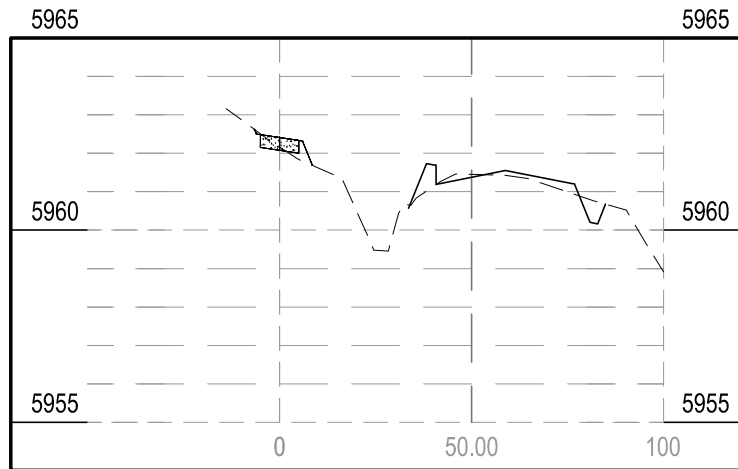


STA 13+68.72

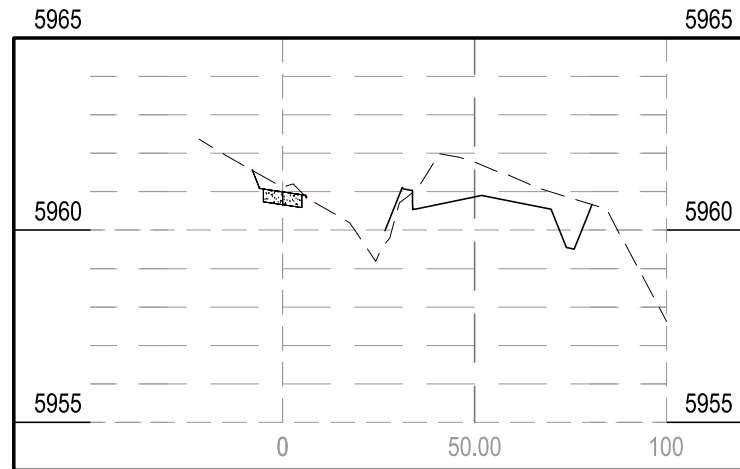


STA 15+00.00

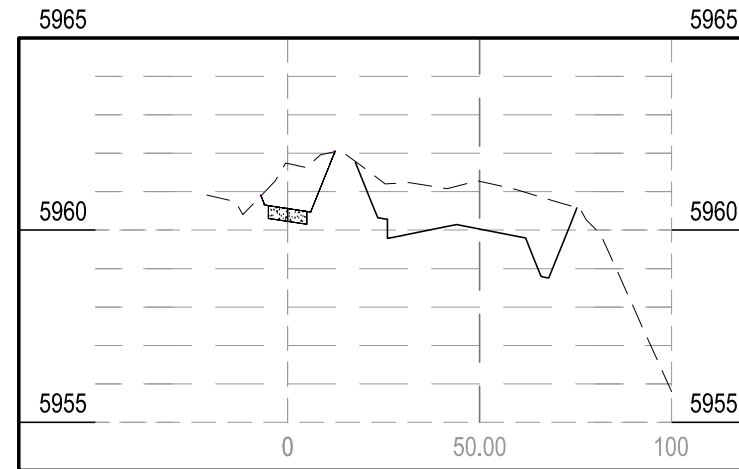


STA 16+50.00

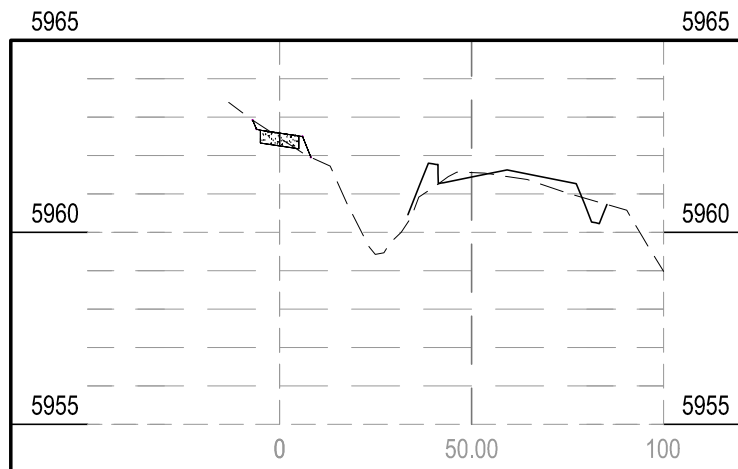

STA 13+53.86

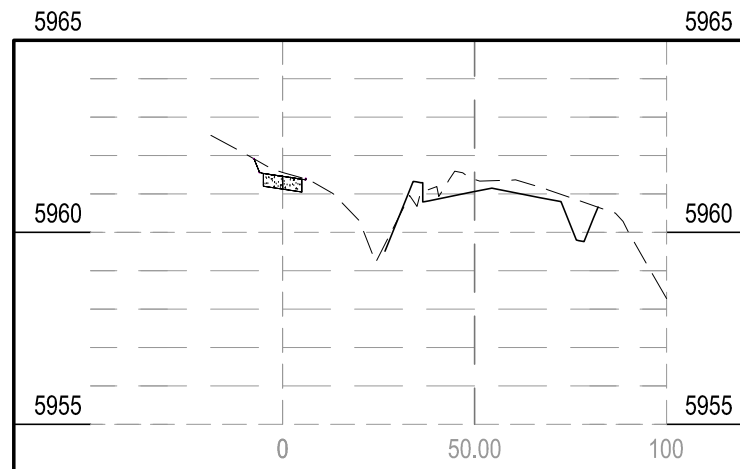

STA 14+50.00

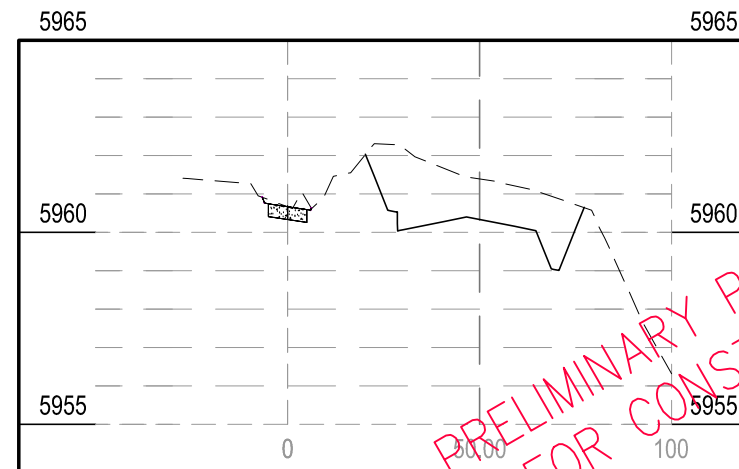

STA 16+00.00

PRELIMINARY PLANS  
NOT FOR CONSTRUCTION

| NO. | REVISION | DATE |
|-----|----------|------|
|     |          |      |
|     |          |      |
|     |          |      |
|     |          |      |
|     |          |      |

PREPARED FOR:  
MPO  
2101 ONEIL AVE.  
RM 205  
CHEYENNE, WY. 82001


PROJECT: FOX FARM ROAD STREET IMPROVEMENTS  
DRAWING TITLE: BURLINGTON TRAILS SIDEWALK CROSS SECTIONS STA. 13+53.86 - 17+00

avi p.c.  
engineering  
planning  
surveying  
PHONE (307) 637-6017  
1103 OLD TOWN LANE, SUITE 101  
CHEYENNE, WY 82009  
AVI@AVIPC.COM


DATE: 6-20-13  
DRAWN BY: SRL  
DESIGNED BY: TC  
CHECKED BY: TC

JOB NO.: 2-3211-B


XS-44 83  
SHEET NO. OF

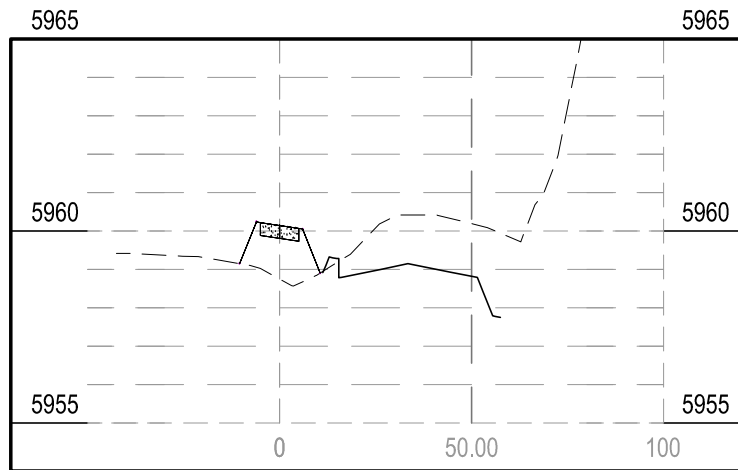


STA 18+50.00

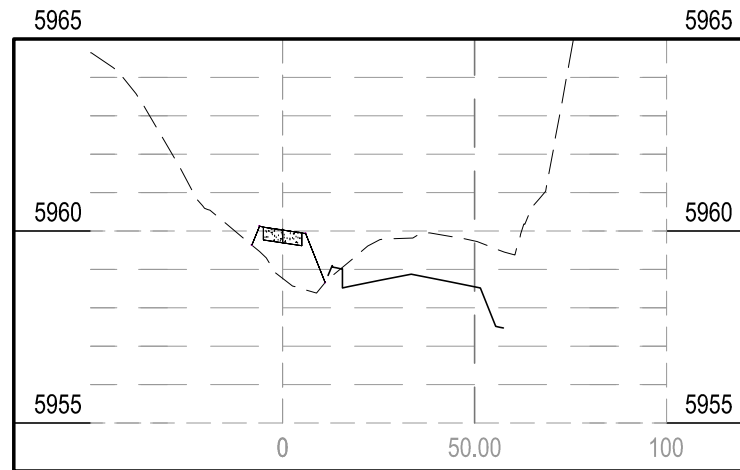


STA 19+05.84

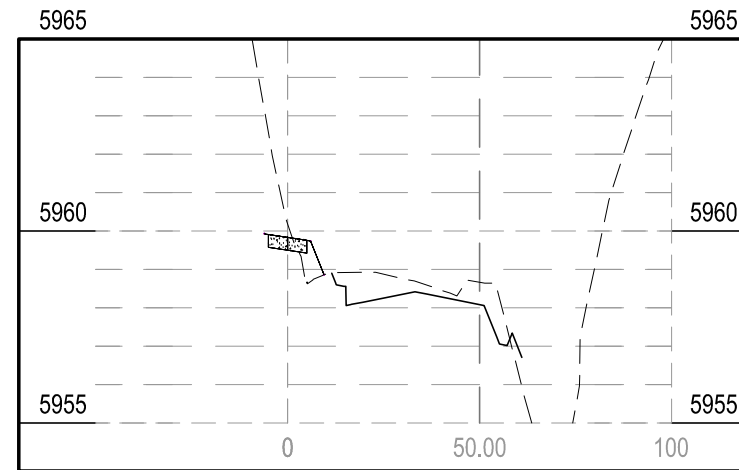


STA 20+00.00

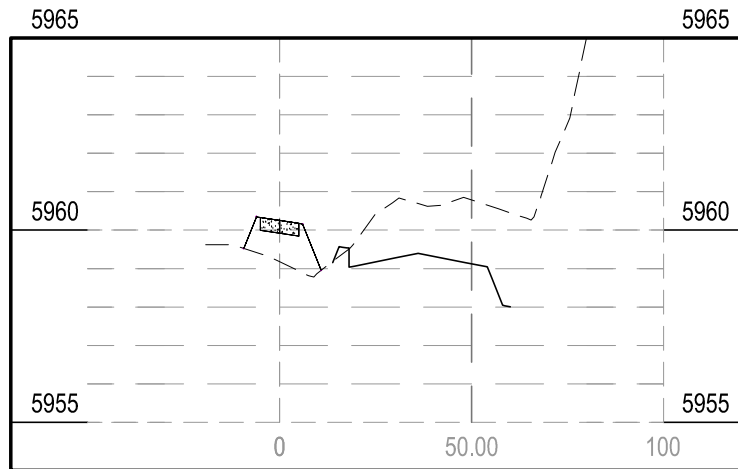


STA 18+00.00

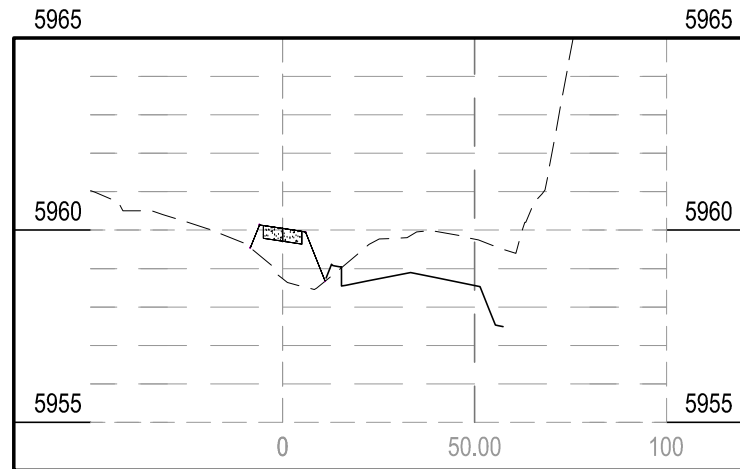


STA 19+00.00

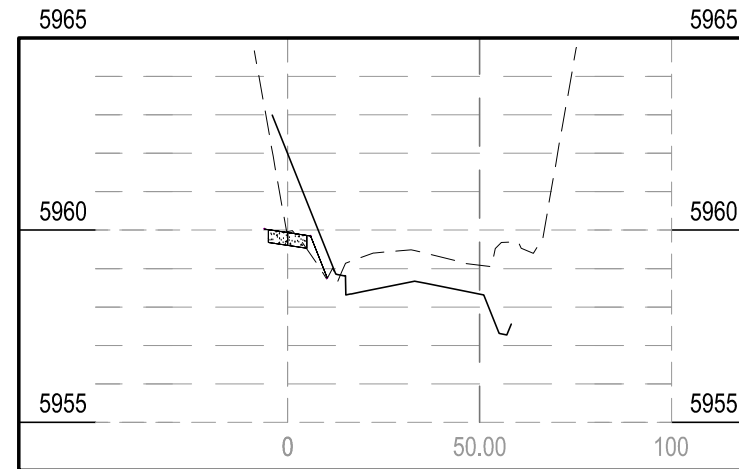


STA 19+50.00

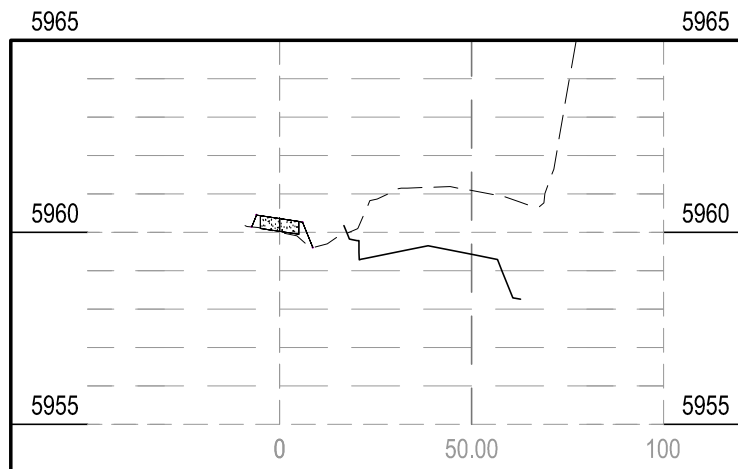

STA 17+50.00

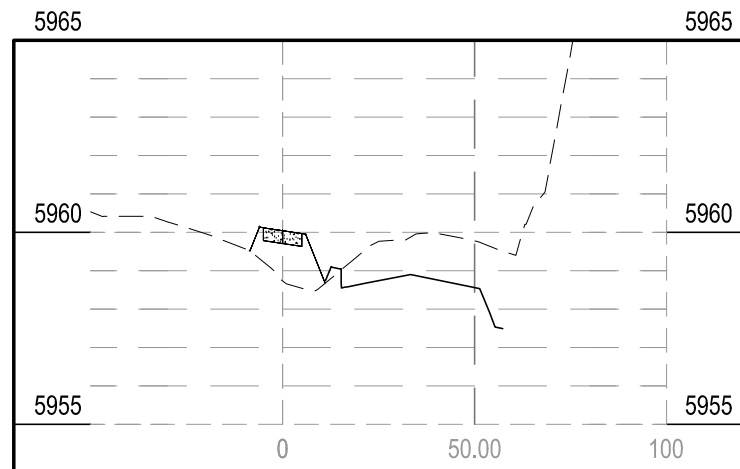

STA 18+99.01

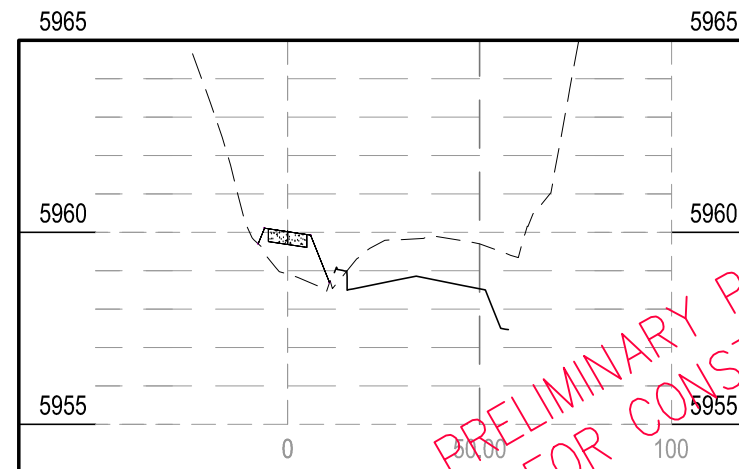

STA 19+12.67

PRELIMINARY PLANS  
NOT FOR CONSTRUCTION

| NO. | REVISION | DATE |
|-----|----------|------|
|     |          |      |
|     |          |      |
|     |          |      |
|     |          |      |
|     |          |      |

PREPARED FOR:  
MPO  
2101 ONEIL AVE.  
RM 205  
CHEYENNE, WY. 82001

PROJECT: FOX FARM ROAD STREET  
IMPROVEMENTS  
DRAWING TITLE:  
BURLINGTON TRAILS SIDEWALK  
CROSS SECTIONS STA. 17+50 - 20+00


avi p.c.  
engineering  
planning  
surveying  
PHONE (307) 637-6017  
1103 OLD TOWN LANE, SUITE 101  
CHEYENNE, WY 82009  
AVI@AVIPC.COM

DATE:  
6-20-13  
DRAWN BY:  
SRL  
DESIGNED BY:  
TC  
CHECKED BY:  
TC


JOB NO.:  
2-3211-B

XS-45 83  
SHEET NO. OF


H:\3211\design\3211B FOX FARM STREET IMP.dwg Aug 30, 2013 4:31pm jwilson

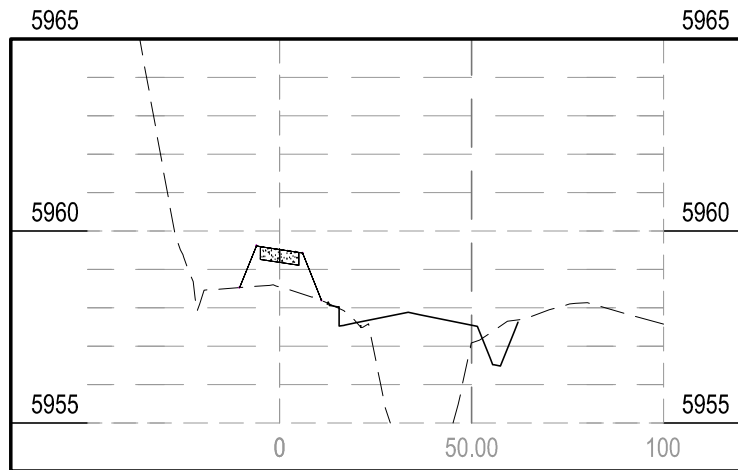


STA 21+50.00

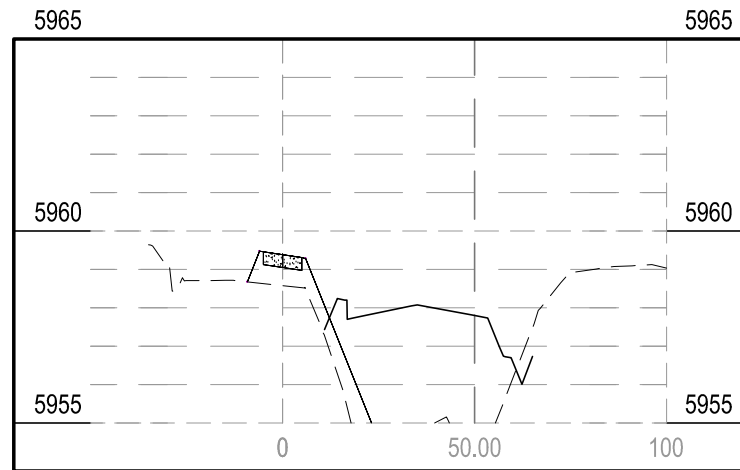


STA 22+16.93

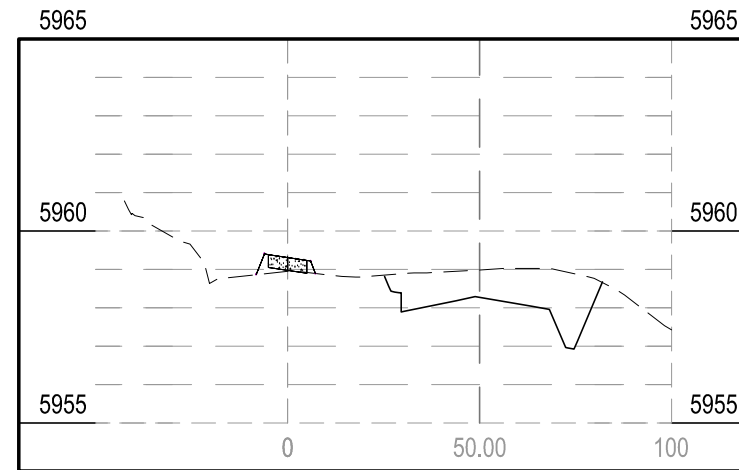


STA 22+50.00

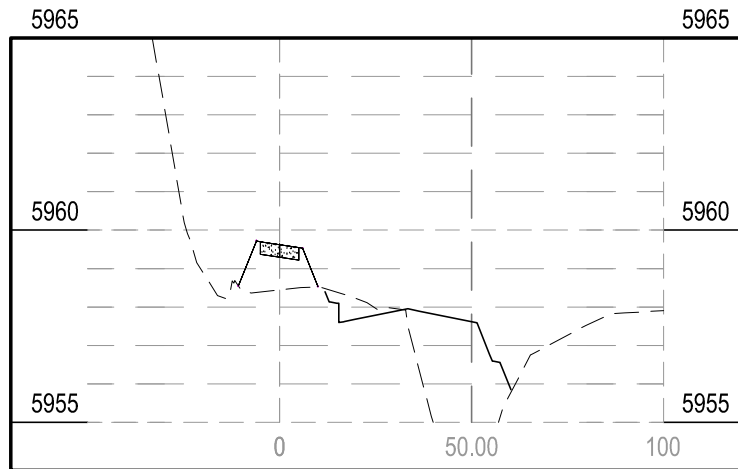


STA 21+00.00

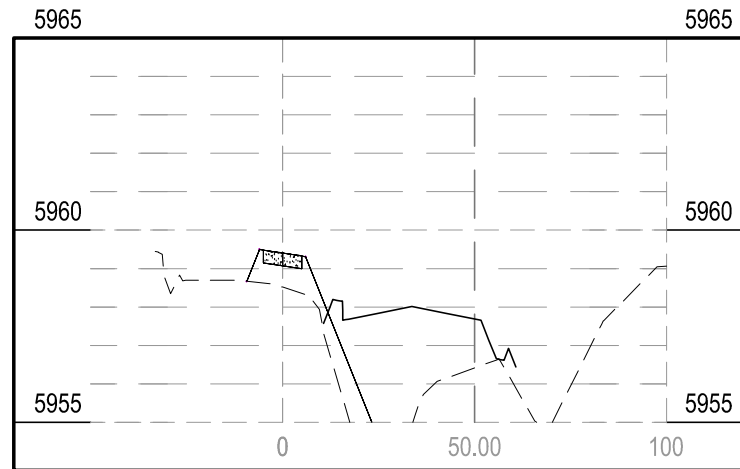


STA 22+07.78

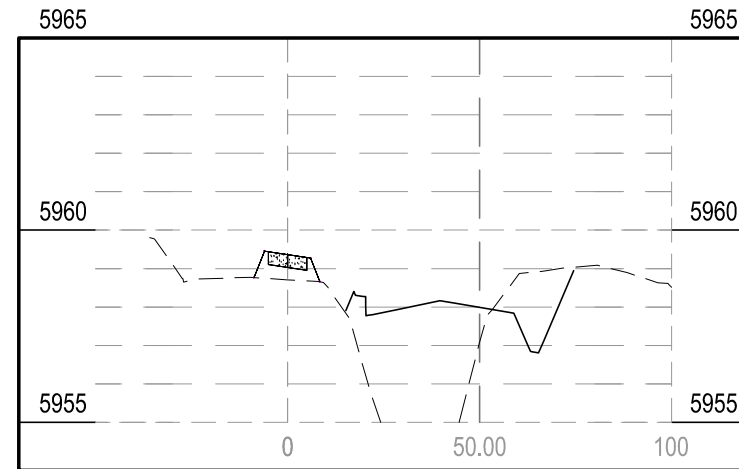


STA 22+26.08

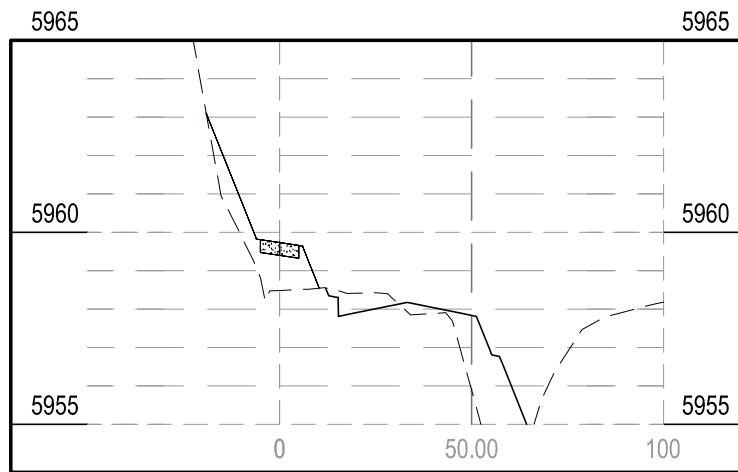

STA 20+50.00

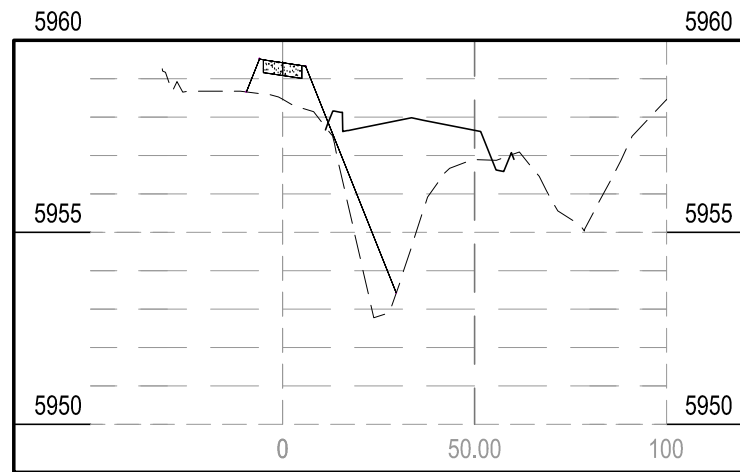

STA 22+00.00

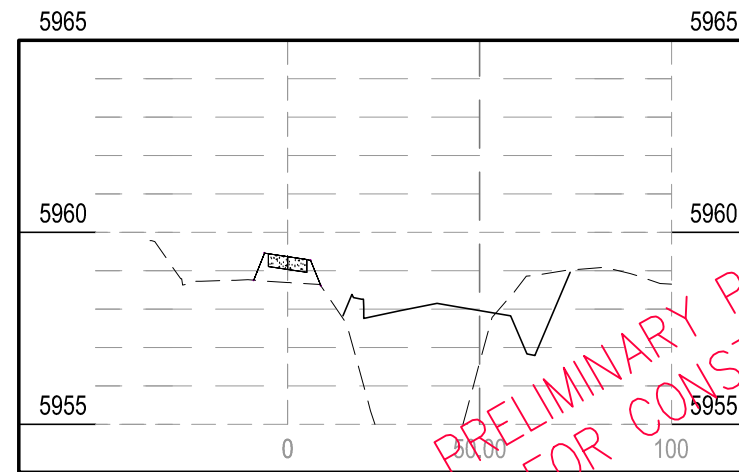

STA 22+25.00

PRELIMINARY PLANS  
NOT FOR CONSTRUCTION

| NO. | REVISION | DATE |
|-----|----------|------|
|     |          |      |
|     |          |      |
|     |          |      |
|     |          |      |

PREPARED FOR:  
MPO  
2101 ONEIL AVE.  
RM 205  
CHEYENNE, WY. 82001

PROJECT: FOX FARM ROAD STREET IMPROVEMENTS  
DRAWING TITLE: BURLINGTON TRAILS SIDEWALK CROSS SECTIONS STA. 20+50 - 22+50


avi p.c.  
engineering  
planning  
surveying  
PHONE (307) 637-6017  
1103 OLD TOWN LANE, SUITE 101  
CHEYENNE, WY 82009  
AVI@AVIPC.COM

DATE: 6-20-13  
DRAWN BY: SRL  
DESIGNED BY: TC  
CHECKED BY: TC


JOB NO.: 2-3211-B

XS-46 83  
SHEET NO. OF


H:\3211\design\3211B FOX FARM STREET IMP.dwg Aug 30, 2013 4:32pm jwilson

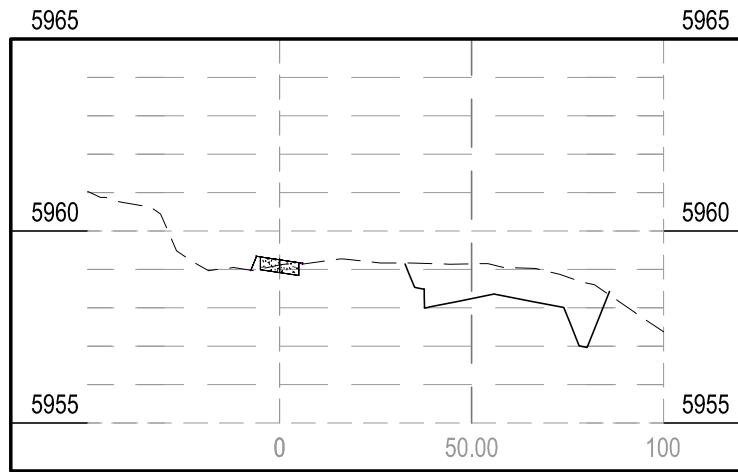


STA 22+79.40

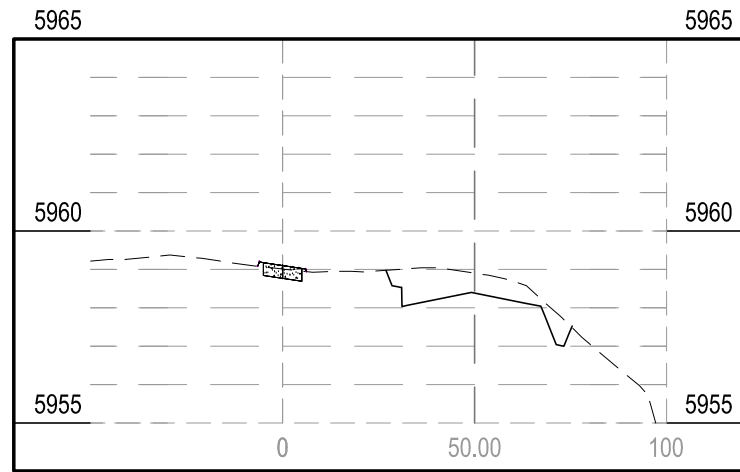


STA 23+50.00

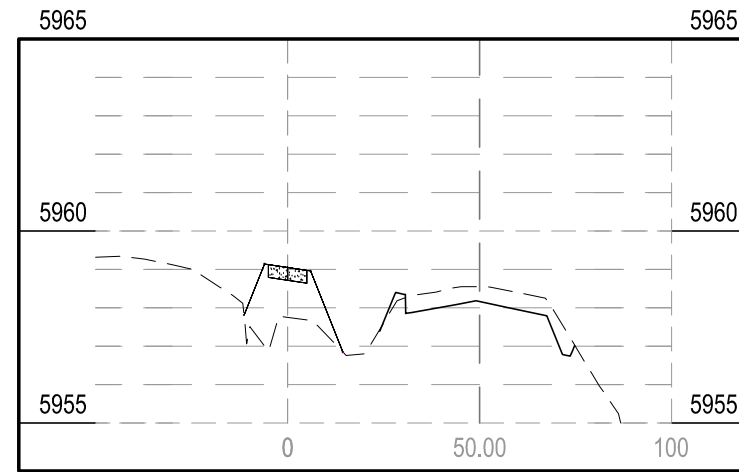


STA 23+75.00

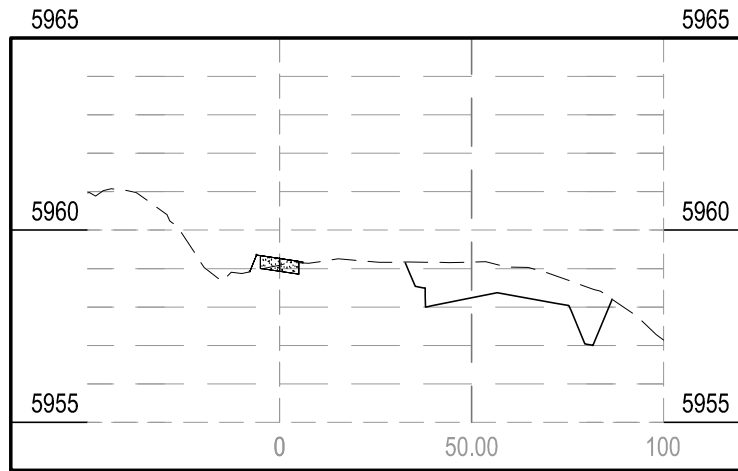


STA 22+75.00

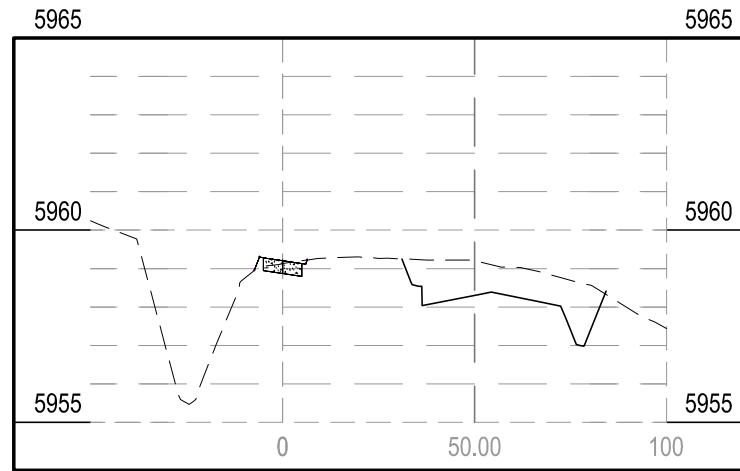


STA 23+00.00

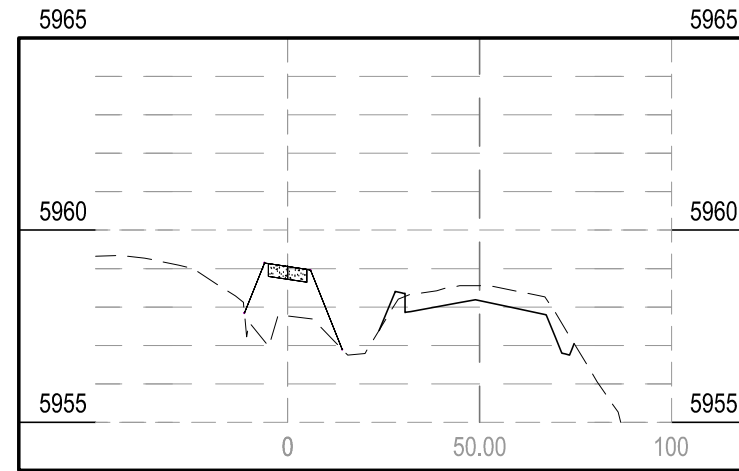


STA 23+74.75

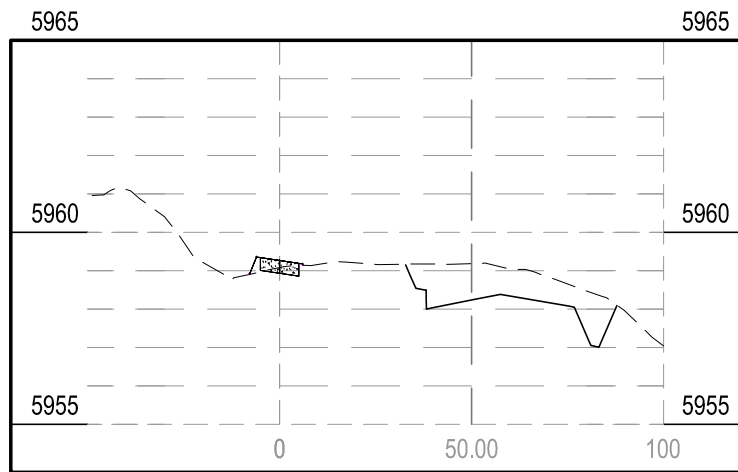

STA 22+72.32

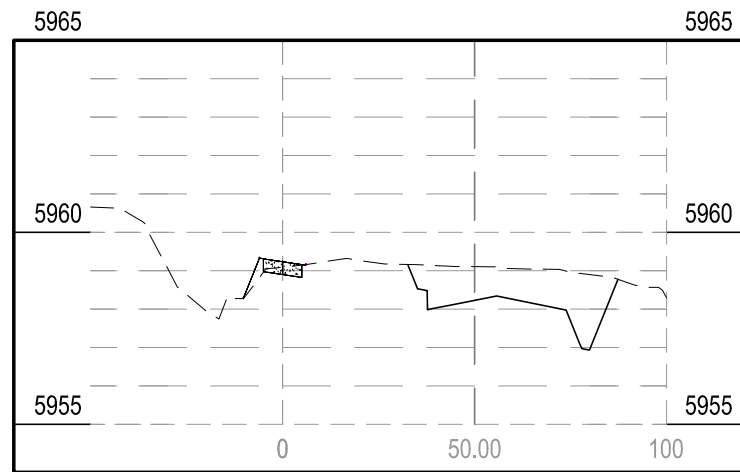

STA 22+86.49

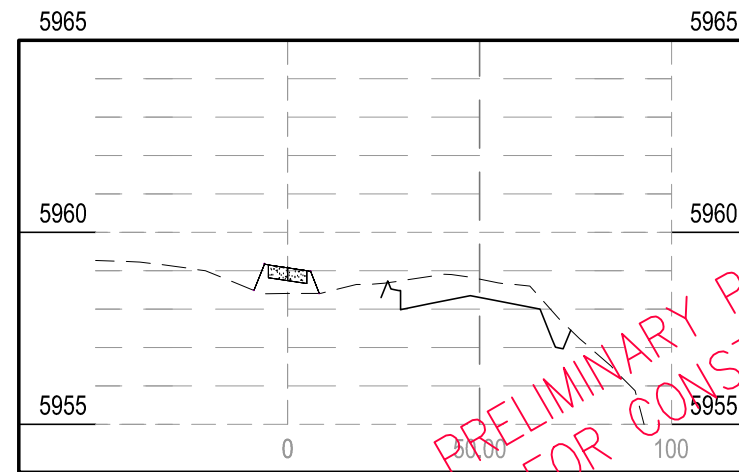

STA 23+63.01

PRELIMINARY PLANS  
NOT FOR CONSTRUCTION

| NO. | REVISION | DATE |
|-----|----------|------|
|     |          |      |
|     |          |      |
|     |          |      |
|     |          |      |
|     |          |      |

PREPARED FOR:  
MPO  
2101 ONEIL AVE.  
RM 205  
CHEYENNE, WY. 82001

PROJECT: FOX FARM ROAD STREET IMPROVEMENTS  
DRAWING TITLE: BURLINGTON TRAILS SIDEWALK CROSS SECTIONS STA. 22+72.32 - 23+75


avi p.c.  
engineering  
planning  
surveying  
PHONE (307) 637-6017  
1103 OLD TOWN LANE, SUITE 101  
CHEYENNE, WY 82009  
AVI@AVIPC.COM

DATE: 6-20-13  
DRAWN BY: SRL  
DESIGNED BY: TC  
CHECKED BY: TC


JOB NO.: 2-3211-B

XS-47 83  
SHEET NO. OF


H:\3211\design\3211B FOX FARM STREET IMP.dwg Aug 30, 2013 4:32pm jwilson

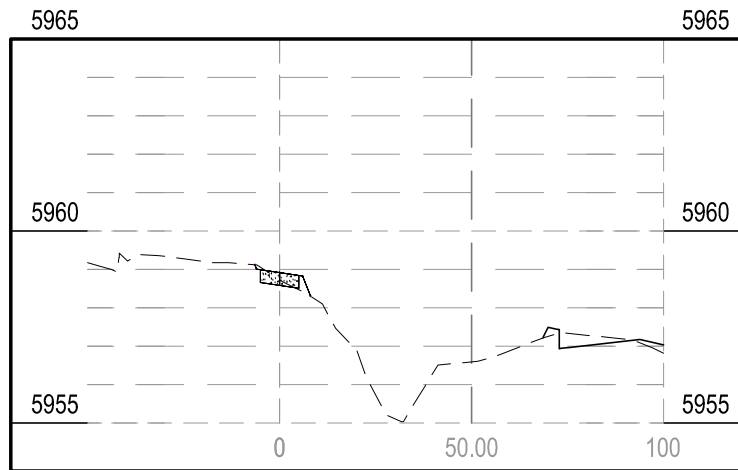


STA 24+39.20

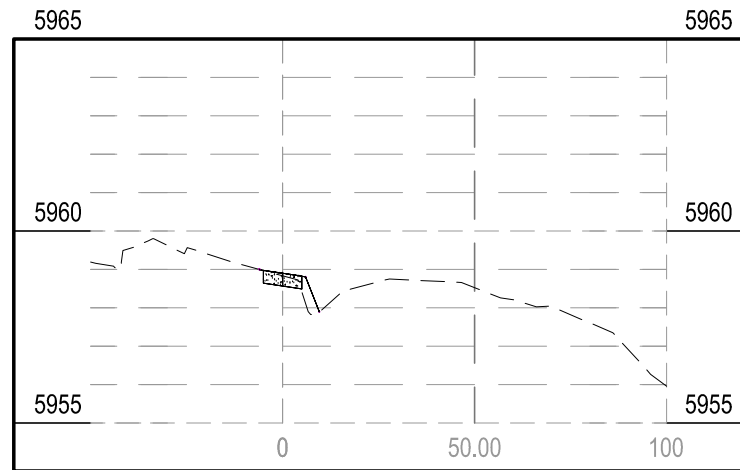


STA 24+75.00

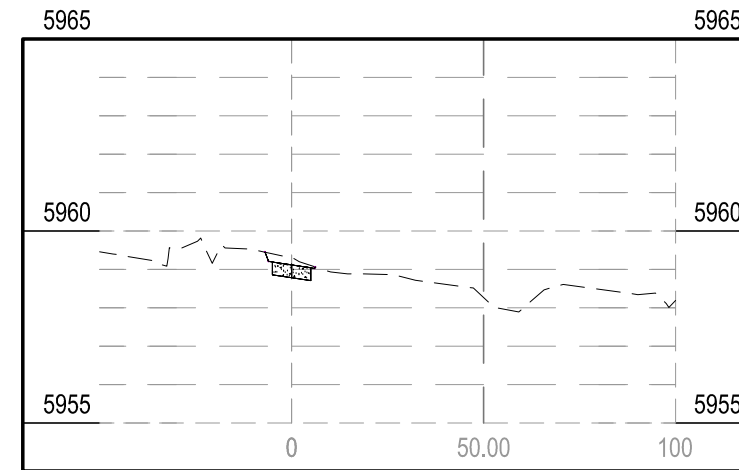


STA 25+00.00

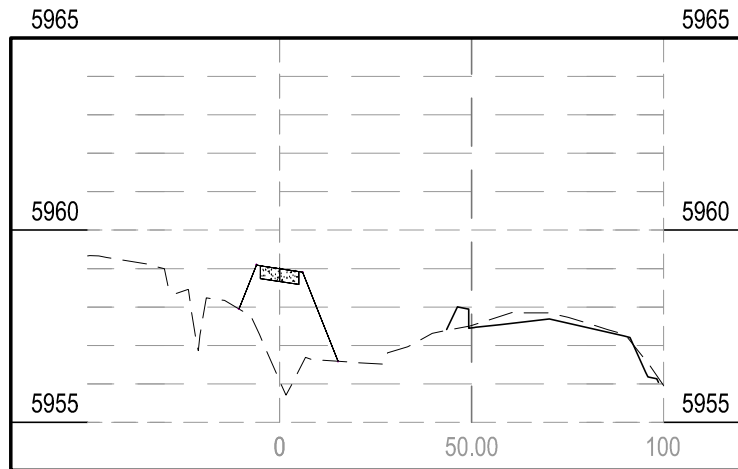


STA 24+00.00

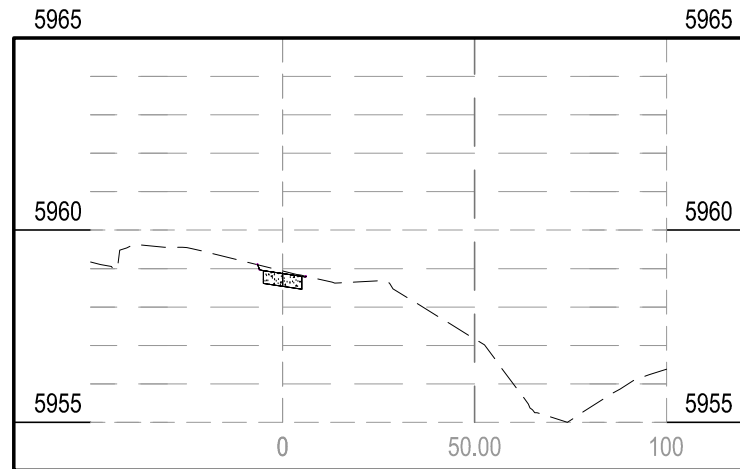


STA 24+64.02

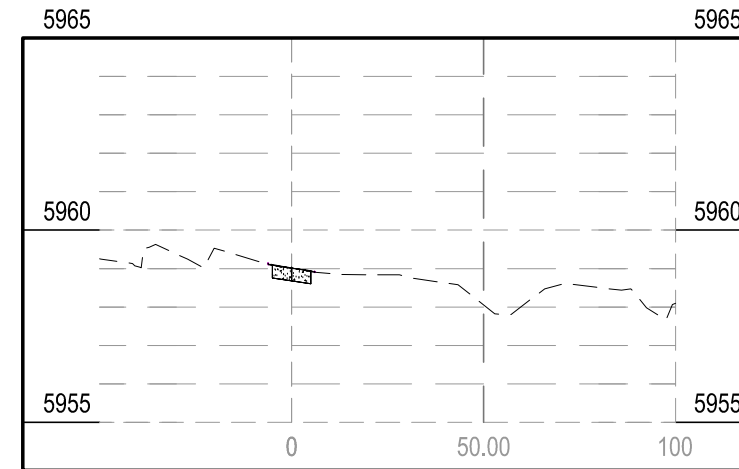


STA 24+90.51

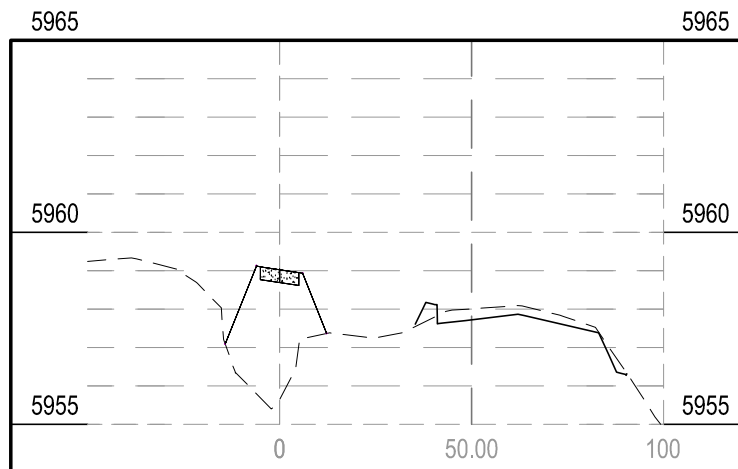

STA 23+86.49

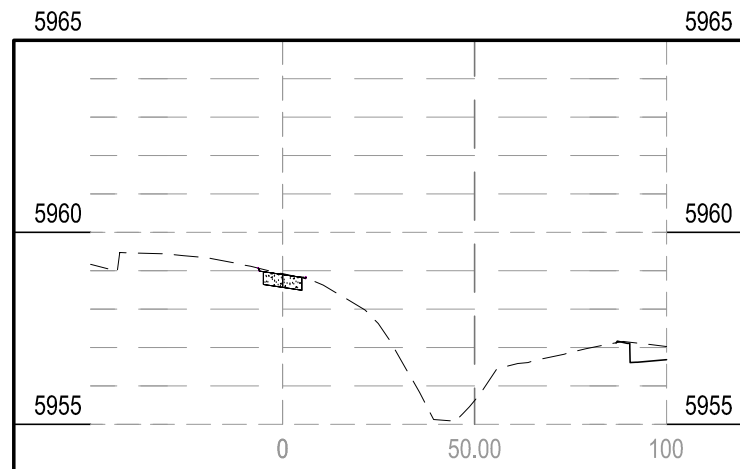

STA 24+50.00

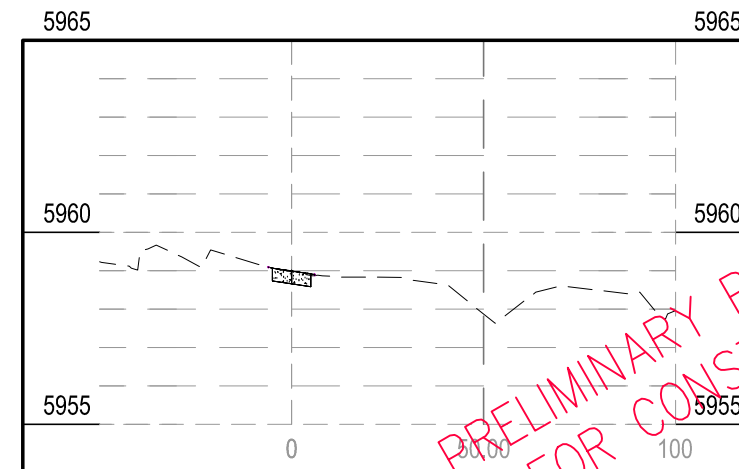

STA 24+88.84

PRELIMINARY PLANS  
NOT FOR CONSTRUCTION

| NO. | REVISION | DATE |
|-----|----------|------|
|     |          |      |
|     |          |      |
|     |          |      |
|     |          |      |

PREPARED FOR:  
MPO  
2101 ONEIL AVE.  
RM 205  
CHEYENNE, WY. 82001

PROJECT: FOX FARM ROAD STREET IMPROVEMENTS  
DRAWING TITLE: BURLINGTON TRAILS SIDEWALK CROSS SECTIONS STA. 23+86.49 - 25+00


avi p.c.  
engineering  
planning  
surveying  
PHONE (307) 637-6017  
1103 OLD TOWN LANE, SUITE 101  
CHEYENNE, WY 82009  
AVI@AVIPC.COM

DATE: 6-20-13  
DRAWN BY: SRL  
DESIGNED BY: TC  
CHECKED BY: TC


JOB NO.: 2-3211-B

XS-48 83  
SHEET NO. OF


H:\3211\design\3211B FOX FARM STREET IMP.dwg Aug 30, 2013 4:32pm jwilson

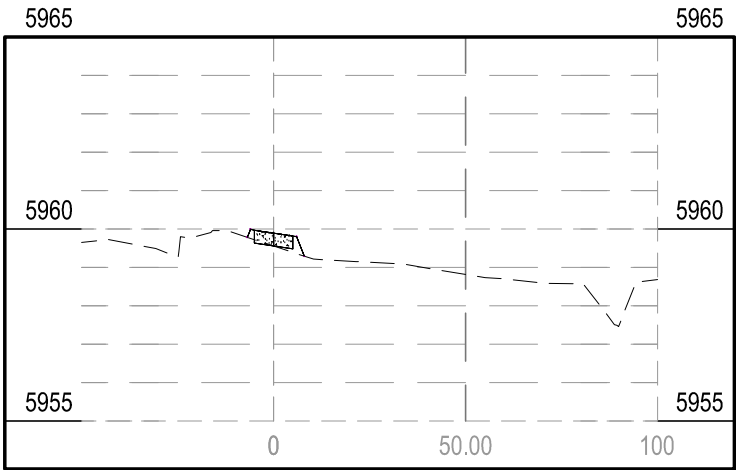


STA 25+50.00

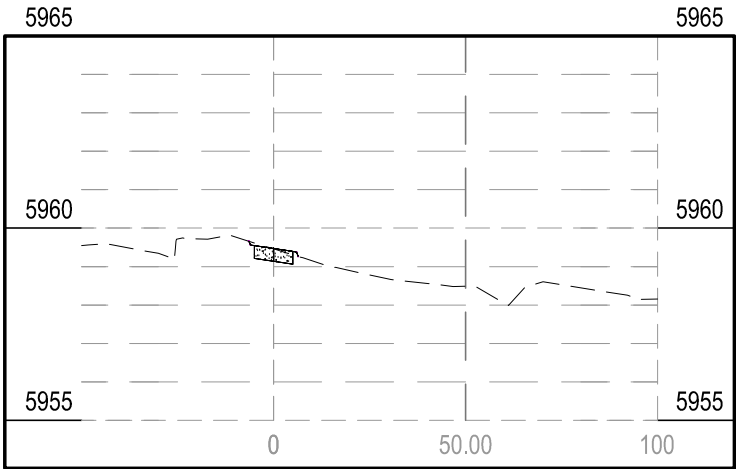

STA 25+22.87

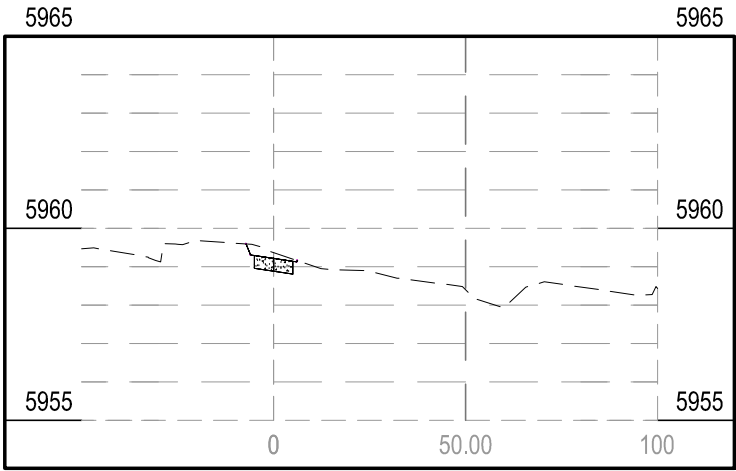

STA 25+06.69

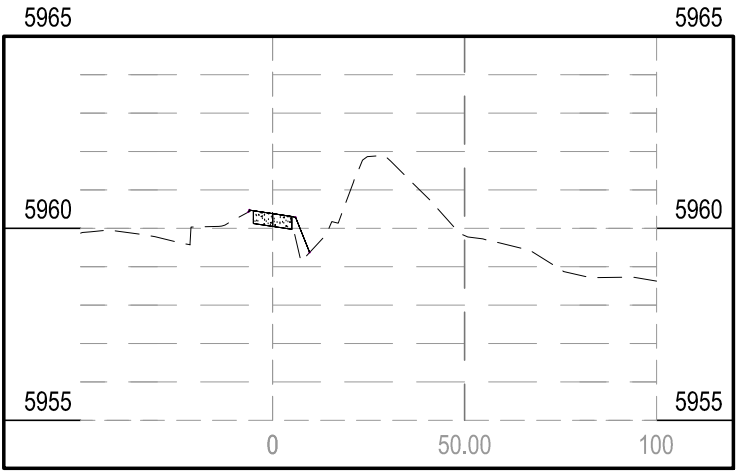

STA 26+00.00

PRELIMINARY PLANS  
NOT FOR CONSTRUCTION

| NO. | REVISION | DATE |
|-----|----------|------|
|     |          |      |
|     |          |      |
|     |          |      |
|     |          |      |
|     |          |      |

PREPARED FOR:  
MPO  
2101 O'NEIL AVE.  
RM 205  
CHEYENNE, WY. 82001

PROJECT: FOX FARM ROAD STREET IMPROVEMENTS  
DRAWING TITLE: BURLINGTON TRAILS SIDEWALK CROSS SECTIONS STA. 25+06.69 - 26+00

avi

engineering  
planning  
surveying

PHONE (307) 637-6017  
1103 OLD TOWN LANE, SUITE 101  
CHEYENNE, WY 82009  
AVI@AVIPC.COM

|              |         |
|--------------|---------|
| DATE:        | 6-20-13 |
| DRAWN BY:    | SRL     |
| DESIGNED BY: | TC      |
| CHECKED BY:  | TC      |

JOB NO.:  
2-3211-B

XS-49 83  
SHEET NO. OF