

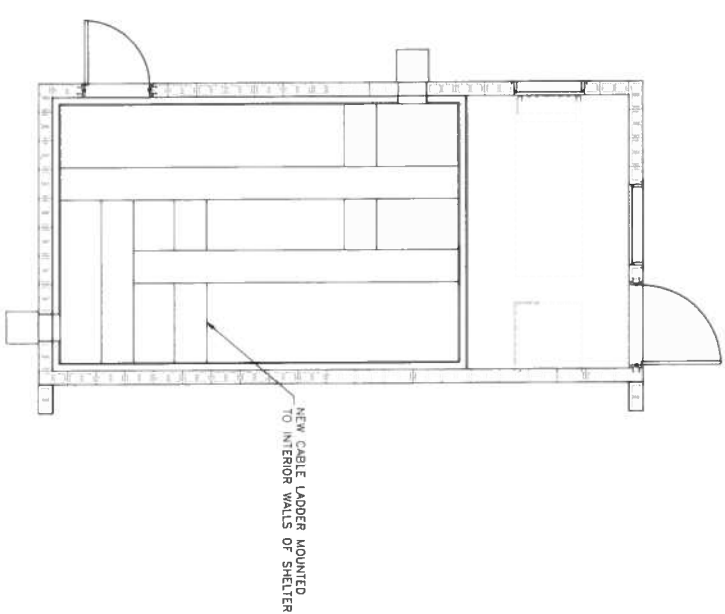
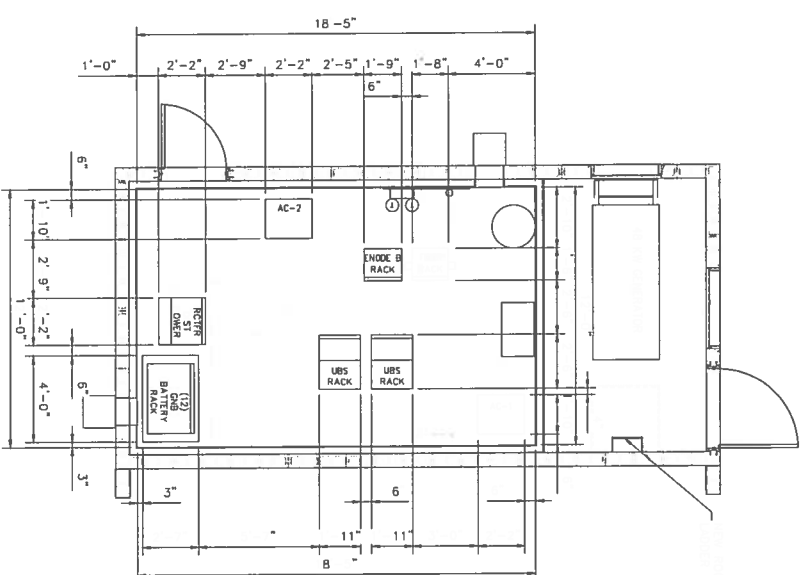


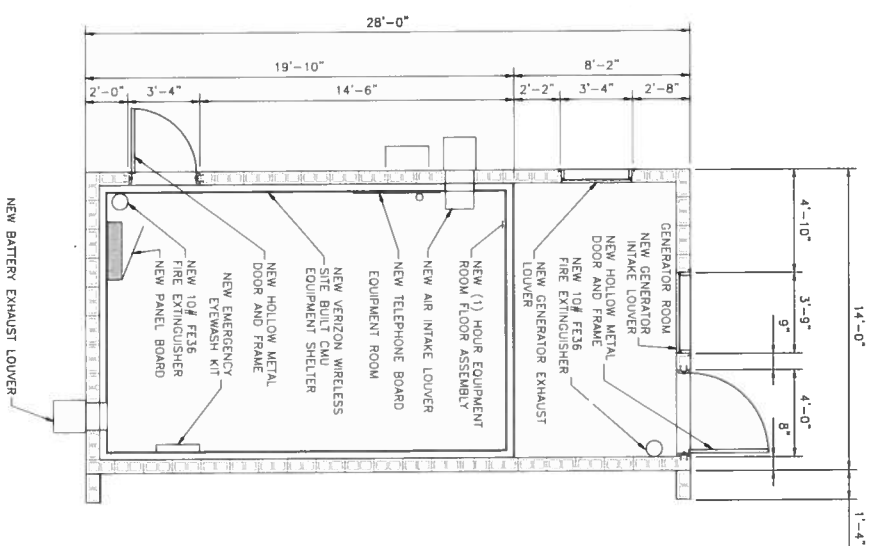


PRELIMINARY
FOR LEASING/ZONING


THESE DRAWINGS AND SURVEYS ARE COPIES OF THE ORIGINALS. THE ORIGINALS ARE THE PROPERTY OF TOWERCOM TECHNOLOGIES, LLC. NO REPRODUCTION OR USE OF THE INFORMATION CONTAINED WITHIN SAID DOCUMENTS IS PROHIBITED WITHOUT THE WRITTEN CONSENT OF TOWERCOM TECHNOLOGIES, LLC				
DESIGNED FOR: verizonwireless				
7131 SOUTH WINDHAM WAY SUITE 550 AURORA, COLORADO 80018				
DESIGNED BY: 				
ALBUQUERQUE / BOISE / EL PASO / DENVER NEW MEXICO / IDAHO / TEXAS / NEVADA / COLORADO				
PROJECT NAME: WY4 DELL (ALT.4)				
ROOF TOP CO-LOCATION				
MAINTENANCE SHOP/COMMUNICATIONS SITE				
PROJECT ADDRESS: 4500 DELL RANGE BLVD. CHEYENNE, WYOMING 82009 LARAMEE COUNTY				
SHEET TITLE: NEW EQUIPMENT SHELTER PLANS AND ELEVATIONS				
REV	DESCRIPTION	DATE	BY	CHK
A	PRELIMINARY FOR TESTING/ZONING	10/11/12	DLL	SMH
SALE DATE:		SHEET NUMBER		
10/15/2012 10:40 AM		Z3		

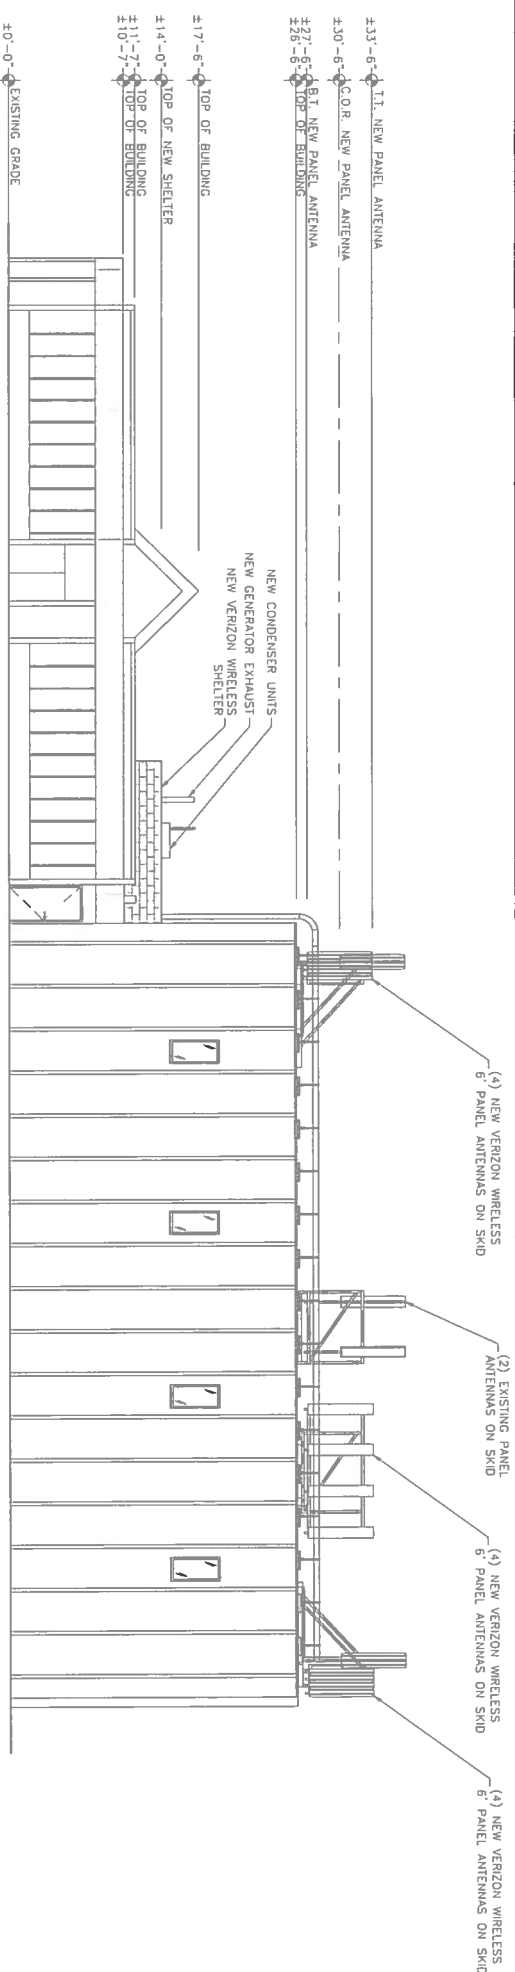

NORTH ELEVATION VIEW
SCALE N.T.S.

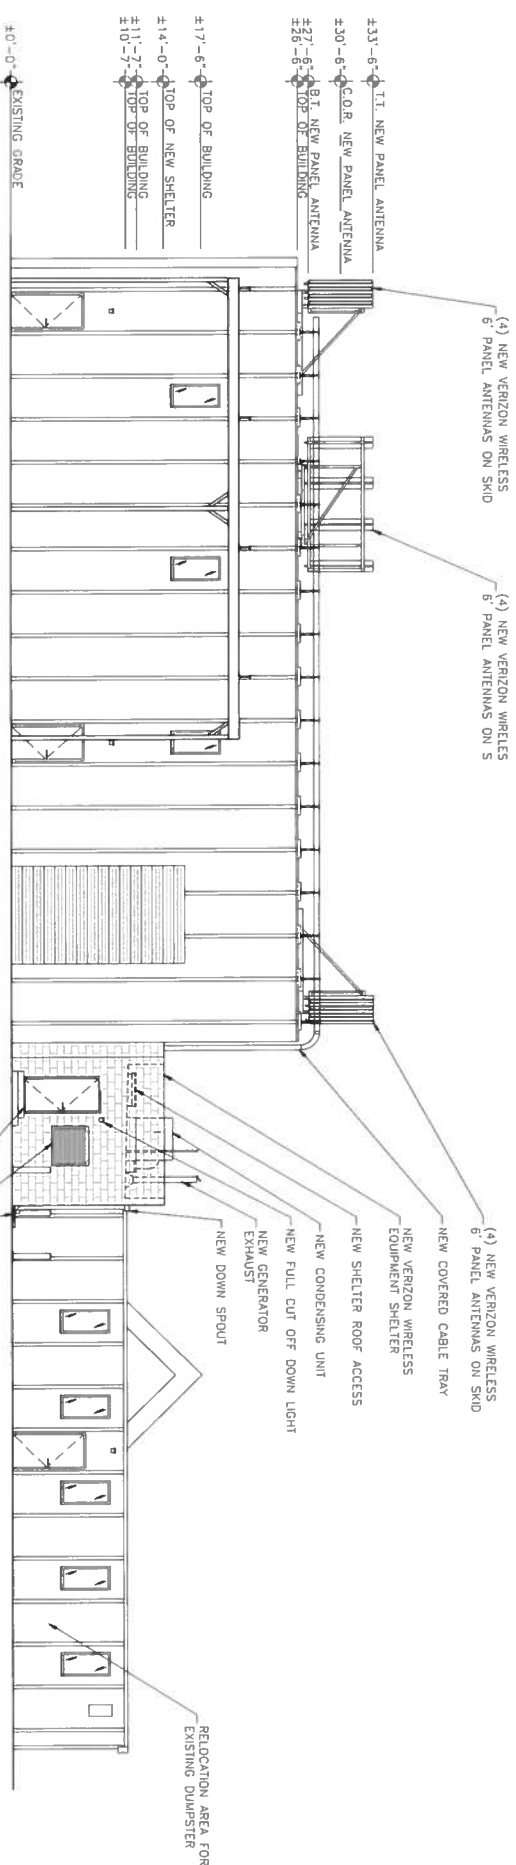

SOUTH ELEVATION VIEW
SCALE. N.T.S.

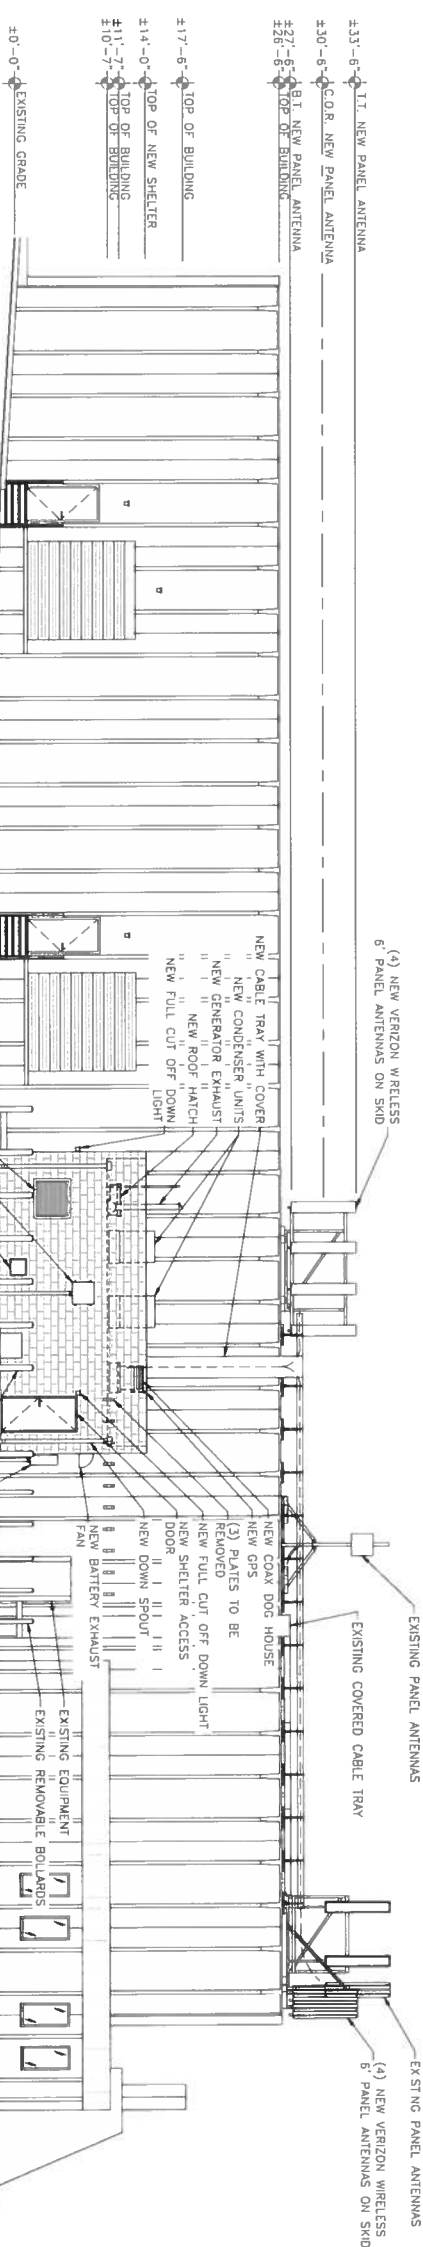

EAST ELEVATION VIEW

THESE PLANNING AND SURVEYING ARE COPYRIGHTED PROJECT PLANS AND SOLE PROPERTY OF TOWERCON TECHNOLOGIES, LLC AND PRODUCED FOR THE USE OF OUR CLIENT. ANY REPRODUCTION OR USE OF THE INFORMATION CONTAINED WITHIN SAID DOCUMENTS IS PROHIBITED WITHOUT THE WRITTEN CONSENT OF TOWERCON TECHNOLOGIES, LLC.	
DESIGNED FOR: 3131 SOUTH WINDHAM WAY, SUITE 550 AURORA, COLORADO 80018	
verizonwireless	
	
ALBUQUERQUE, / BOISE, / EL PASO, / NEVADA, / DENVER, NEW MEXICO / IDAHO / TEXAS / WYOMING / COLORADO	
PROJECT NAME: WY4 DELL (ALT.4)	
ROOF TOP CO-LOCATION	
MAINTENANCE SHOP/COMMUNICATIONS SITE	
PROJECT ADDRESS: 4500 DELL RANGE BLVD. CHEYENNE, WYOMING 82009 LARAMIE COUNTY	
SHEET TITLE: ELEVATIONS	
<table><tr><th>REV</th><th>DESCRIPTION</th><th>DATE</th><th>BY</th><th>CHK</th></tr><tr><td>A</td><td>PRELIMINARY FOR LEASING/ZONING</td><td>10/11/12</td><td>DLL</td><td>SLH</td></tr><tr><td> </td><td> </td><td> </td><td> </td><td> </td></tr><tr><td> </td><td> </td><td> </td><td> </td><td> </td></tr><tr><td> </td><td> </td><td> </td><td> </td><td> </td></tr><tr><td> </td><td> </td><td> </td><td> </td><td> </td></tr><tr><td> </td><td> </td><td> </td><td> </td><td> </td></tr><tr><td> </td><td> </td><td> </td><td> </td><td> </td></tr><tr><td> </td><td> </td><td> </td><td> </td><td> </td></tr><tr><td> </td><td> </td><td> </td><td> </td><td> </td></tr><tr><td> </td><td> </td><td> </td><td> </td><td> </td></tr></table>					REV	DESCRIPTION	DATE	BY	CHK	A	PRELIMINARY FOR LEASING/ZONING	10/11/12	DLL	SLH	
REV	DESCRIPTION	DATE	BY	CHK	
A	PRELIMINARY FOR LEASING/ZONING	10/11/12	DLL	SLH	
DATE: 10/15/2012 10:40 AM	
SHEET NUMBER: Z4	